

4

3


2

1

NOTICE

THIS DRAWING CONTAINS A PROPRIETARY DESIGN ASSIGNED TO SPIRA INTERNATIONAL, INC. ALL RIGHTS TO DUPLICATE, TRANSFER OR USE ARE EXPRESSLY RESERVED BY SPIRA INTERNATIONAL. THE BUYER IS LICENSED TO BUILD ONE ASSEMBLY FROM THESE PLANS.

REVISIONS				
ZONE	LTR	DESCRIPTION	DATE	APPROVED

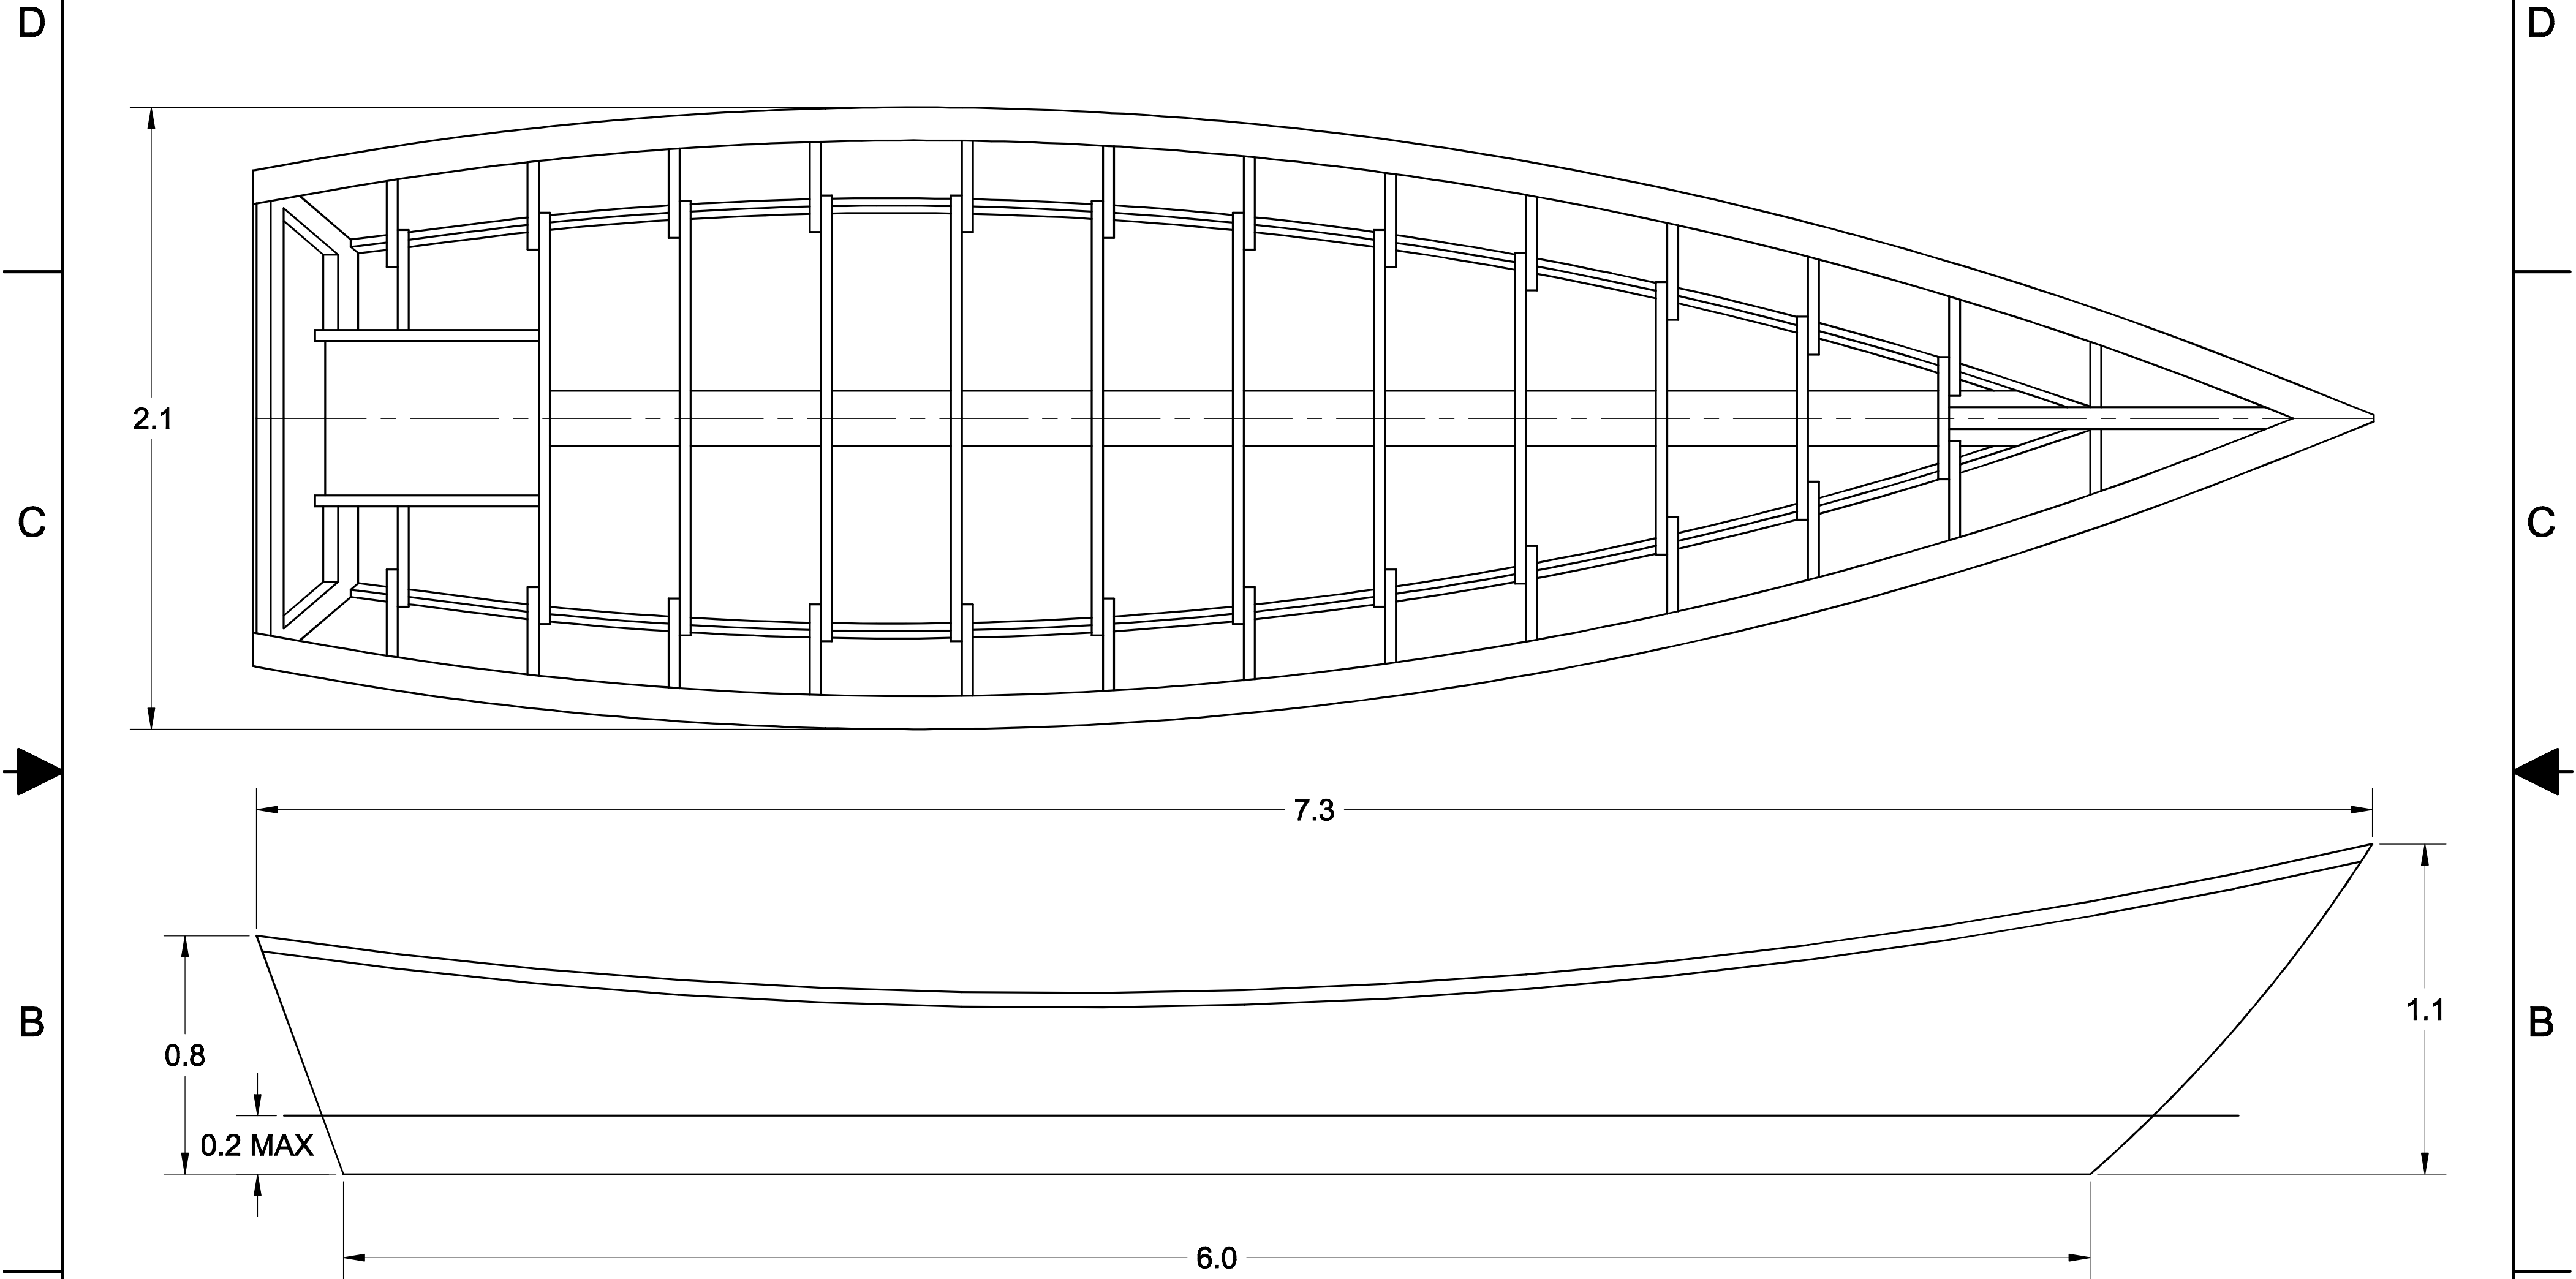

SPECIFICATIONS	
MAX. DISPLACEMENT	2444 KG
HULL WEIGHT	648 KG
CALC. MAX. HORSEPOWER	150 HP
RECOMMENDED HP	65 HP

Spira International, Inc. <i>Huntington Beach, California</i>		
KEY LARGO 7.3 M CAROLINA DORY		
DRAWN BY: J. SPIRA	DATE: 12/22/13	DRAWING NO. KEYLM01
SCALE 1 / 16	SHEET OF	

4

3


2

1

NOTICE

THIS DRAWING CONTAINS A PROPRIETARY DESIGN ASSIGNED TO SPIRA INTERNATIONAL, INC. ALL RIGHTS TO DUPLICATE, TRANSFER OR USE ARE EXPRESSLY RESERVED BY SPIRA INTERNATIONAL. THE BUYER IS LICENSED TO BUILD ONE ASSEMBLY FROM THESE PLANS.

REVISIONS				
ZONE	LTR	DESCRIPTION	DATE	APPROVED

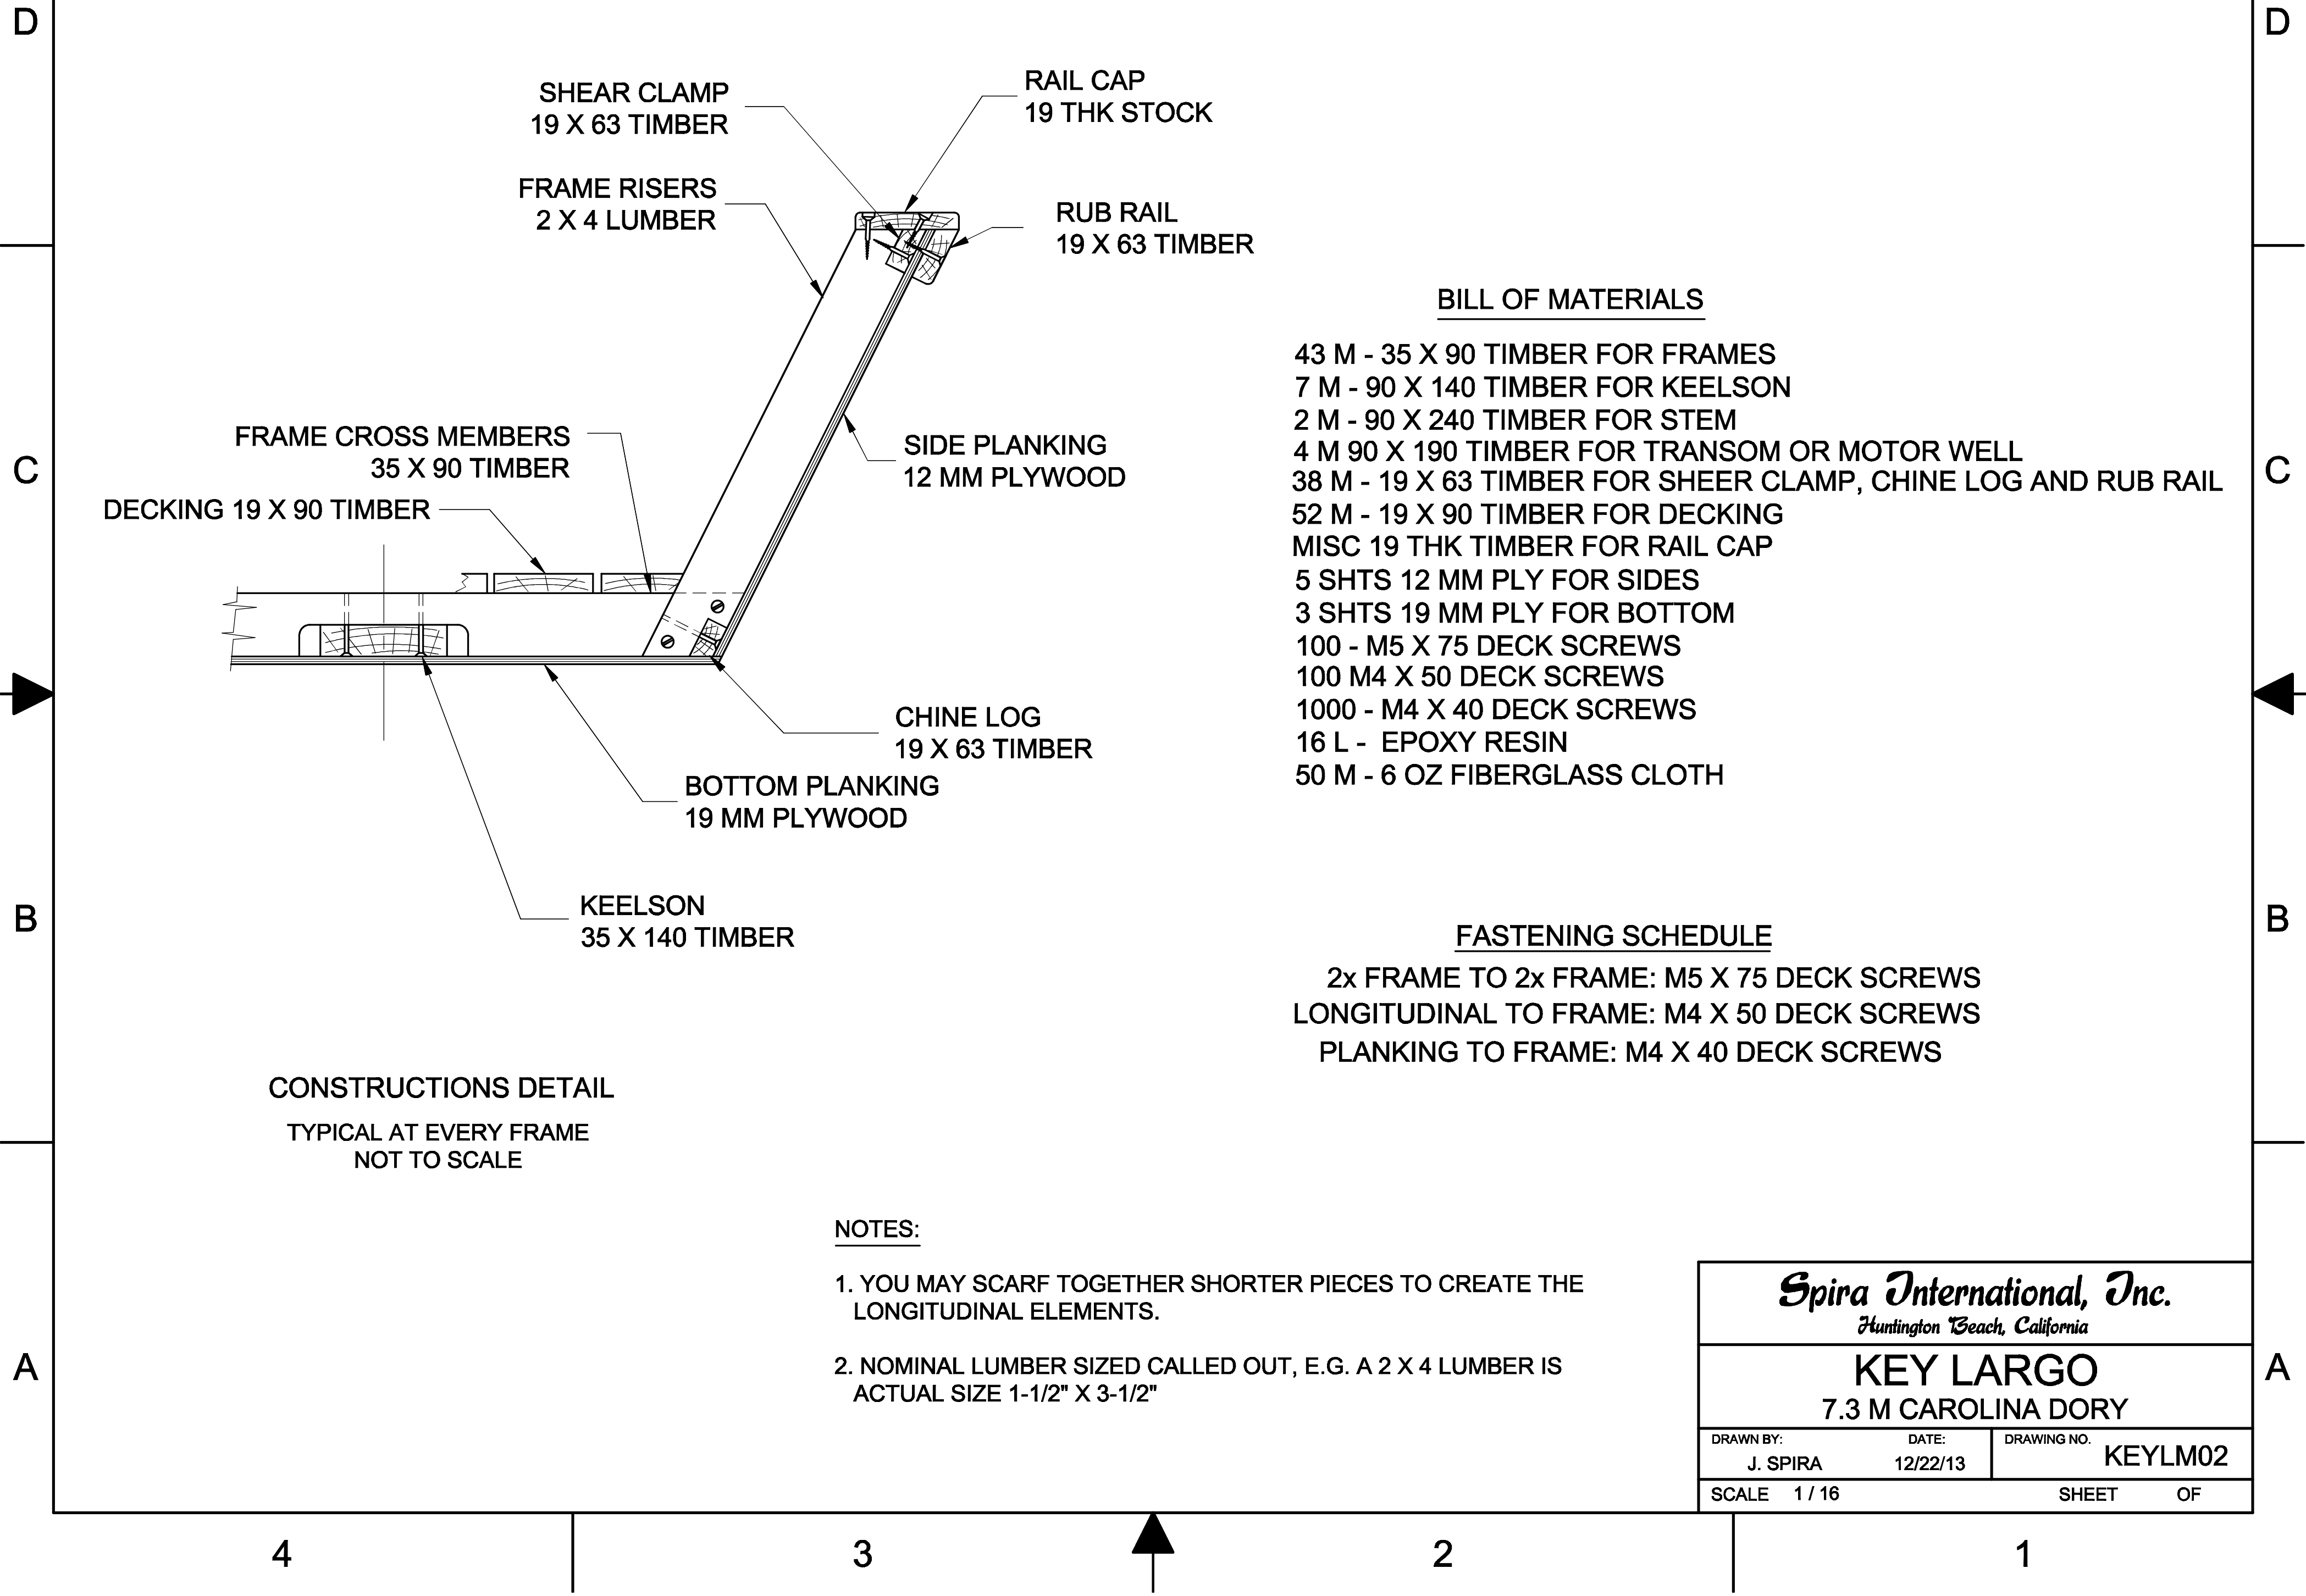

BILL OF MATERIALS

- 43 M - 35 X 90 TIMBER FOR FRAMES
- 7 M - 90 X 140 TIMBER FOR KEELSON
- 2 M - 90 X 240 TIMBER FOR STEM
- 4 M 90 X 190 TIMBER FOR TRANSOM OR MOTOR WELL
- 38 M - 19 X 63 TIMBER FOR SHEER CLAMP, CHINE LOG AND RUB RAIL
- 52 M - 19 X 90 TIMBER FOR DECKING
- MISC 19 THK TIMBER FOR RAIL CAP
- 5 SHTS 12 MM PLY FOR SIDES
- 3 SHTS 19 MM PLY FOR BOTTOM
- 100 - M5 X 75 DECK SCREWS
- 100 M4 X 50 DECK SCREWS
- 1000 - M4 X 40 DECK SCREWS
- 16 L - EPOXY RESIN
- 50 M - 6 OZ FIBERGLASS CLOTH

FASTENING SCHEDULE

- 2x FRAME TO 2x FRAME: M5 X 75 DECK SCREWS
- LONGITUDINAL TO FRAME: M4 X 50 DECK SCREWS
- PLANKING TO FRAME: M4 X 40 DECK SCREWS

NOTES:

- 1. YOU MAY SCARF TOGETHER SHORTER PIECES TO CREATE THE LONGITUDINAL ELEMENTS.
- 2. NOMINAL LUMBER SIZED CALLED OUT, E.G. A 2 X 4 LUMBER IS ACTUAL SIZE 1-1/2" X 3-1/2"

Spira International, Inc. <i>Huntington Beach, California</i>		
KEY LARGO 7.3 M CAROLINA DORY		
DRAWN BY: J. SPIRA	DATE: 12/22/13	DRAWING NO. KEYLM02
SCALE 1 / 16	SHEET OF	