

4



3

2

1

NOTICE
THIS DRAWING CONTAINS A PROPRIETARY DESIGN ASSIGNED TO SPIRA INTERNATIONAL, INC. ALL RIGHTS TO DUPLICATE, TRANSFER OR SELL THIS DESIGN ARE EXPRESSLY RESERVED. THE BUYER IS LICENSED TO BUILD ONE ASSEMBLY FROM THESE PLANS.

REVISIONS				
ZONE	LTR	DESCRIPTION	DATE	R/M/D/APP/PROVED

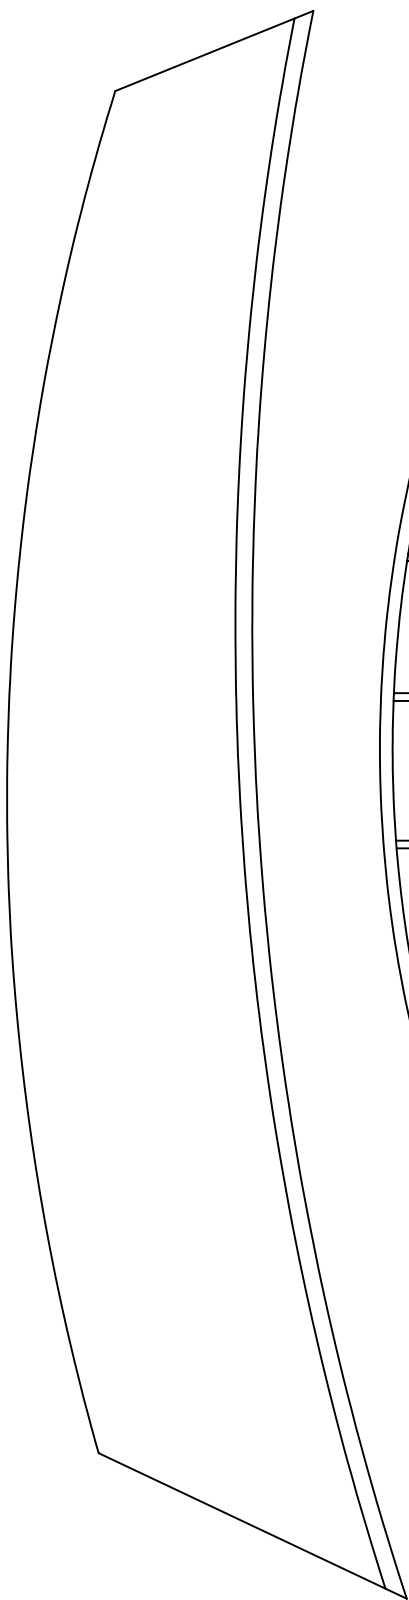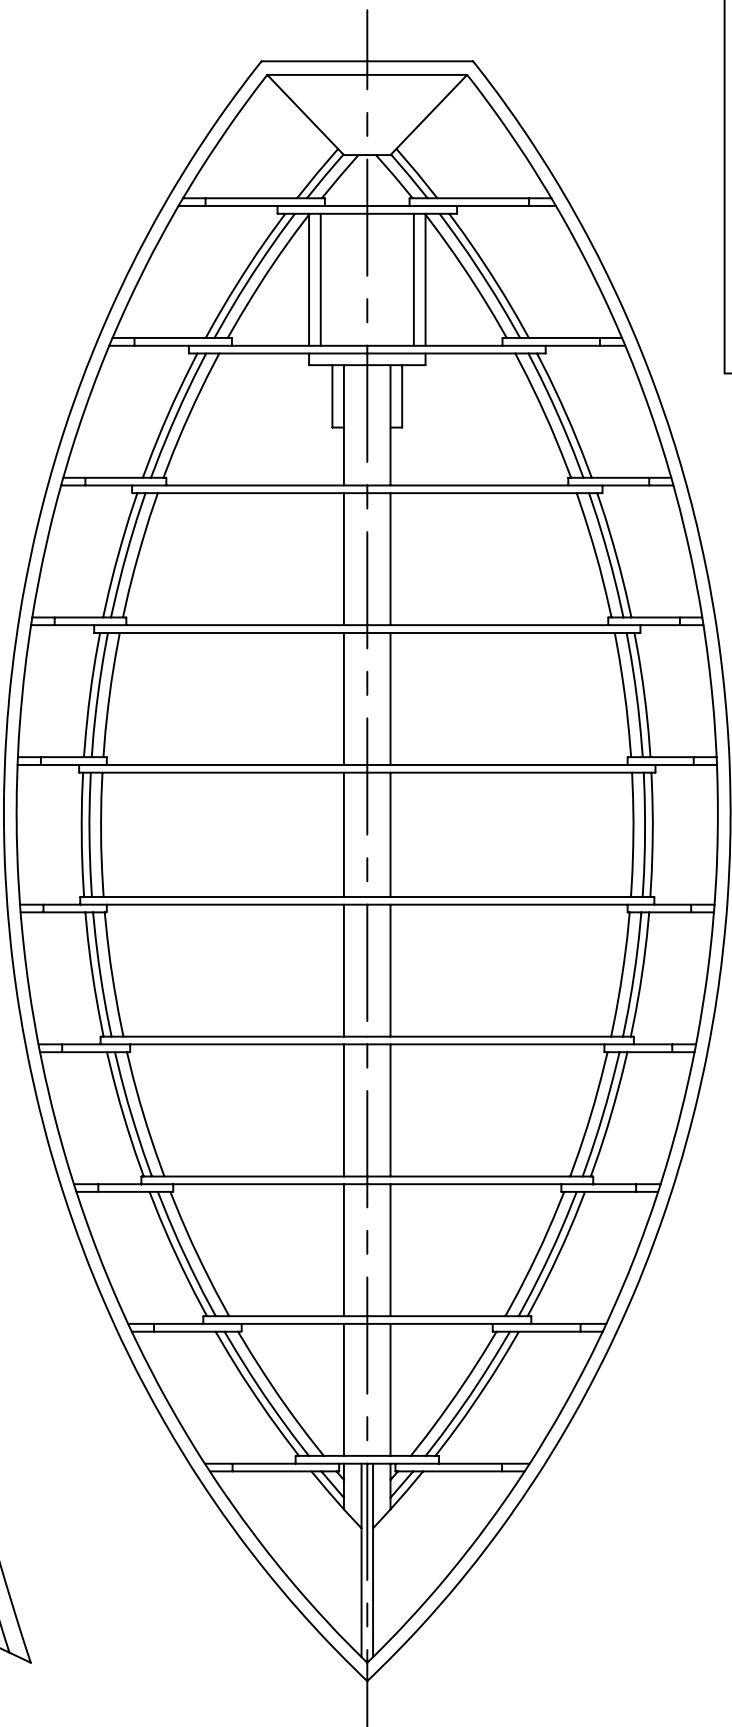

CHINDOK

LENGTH 17'
BEAM 7' 6"
FREEBOARD 30"

Spira International, Inc.
Huntington Beach, California

CHINDOK

MCKENZIE RIVER DRIFT BOAT

DRAWN BY: J. SPIRA 000318 DATE: CHINDOK

SCALE 1" = 1' SHEET OF

4



3

2

1


NOTICE
THIS DRAWING CONTAINS A PROPRIETARY DESIGN ASSIGNED TO SPIRA INTERNATIONAL, INC. ALL RIGHTS TO DUPLICATE, TRANSFER OR SELL THIS DESIGN ARE EXPRESSLY RESERVED. THE BUYER IS LICENSED TO BUILD ONE ASSEMBLY FROM THESE PLANS.

REVISIONS			
ZONE	LTR	DESCRIPTION	DATE R/M/D/DA/PPROVED

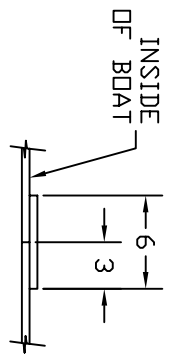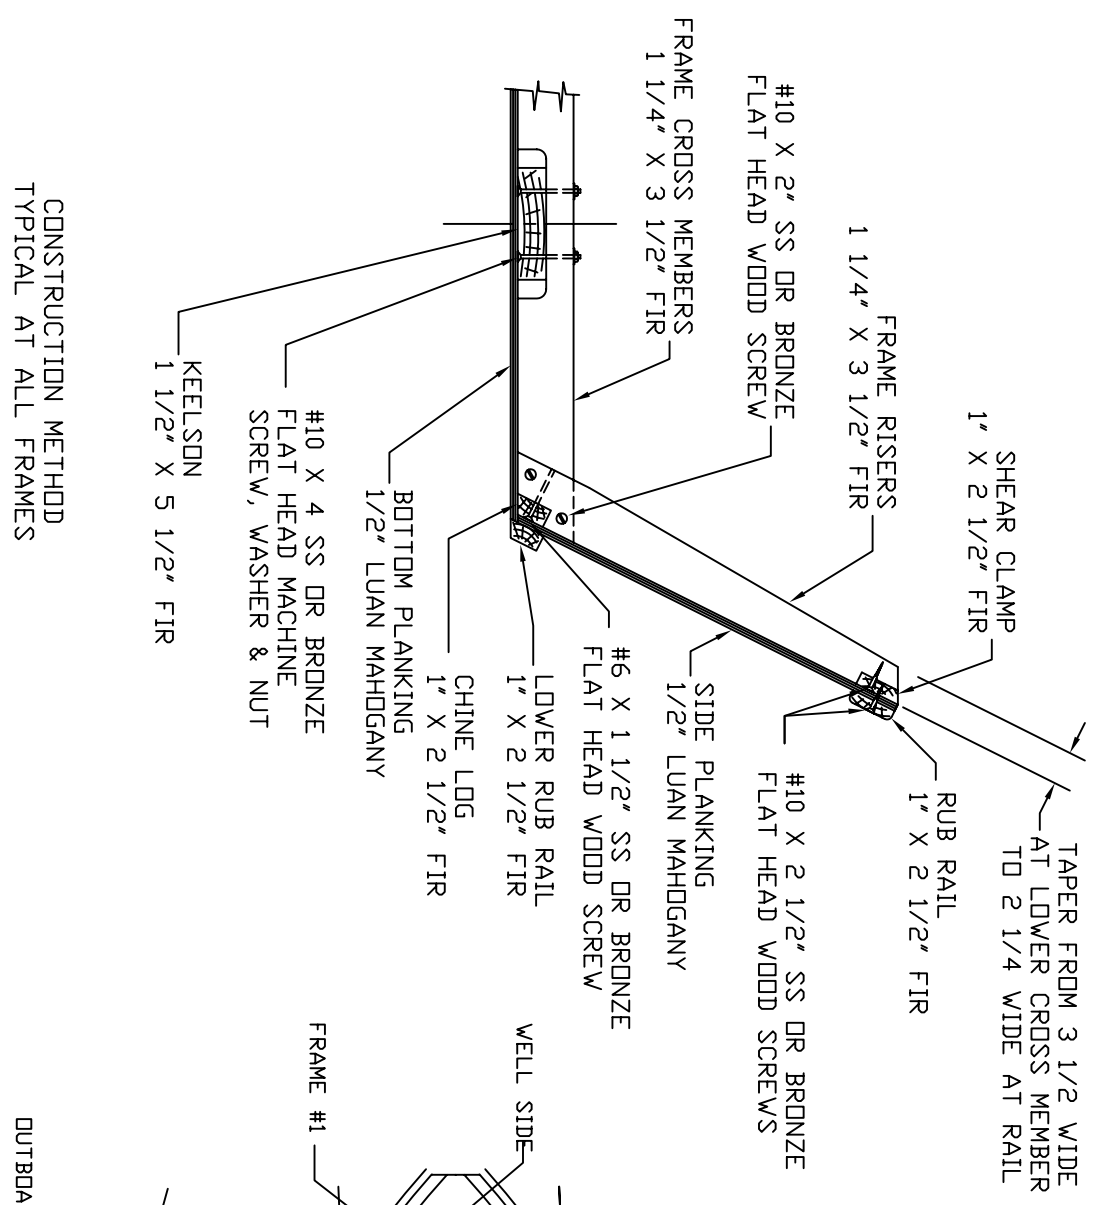

BUTT BLOCK DETAIL
FOR ALL PLYWOOD SEAMS
SCALE 2" = 1"

OUTBOARD WELL DETAILS

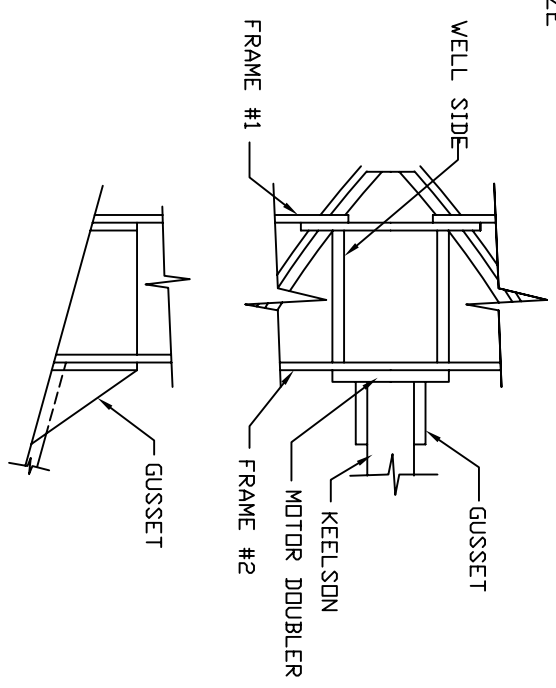

CONSTRUCTION METHOD
TYPICAL AT ALL FRAMES

Spira International, Inc.
Huntington Beach, California

CHINDOK
CONSTRUCTION DETAILS

DRAWN BY:	DATE:	DRAWING NO.
J. SPIRA	000318	CHIND04
SCALE 1" = 1' & NOTED		
SHEET OF		

Chinook Bill of Materials

10 pc. 4' x 8' sheet 1/2" thick lauan plywood (actually it's 7/16")
8 pc. 12' long 1" x 2-1/2" clear pine (or fir) molding for rub rail, chine log & sheer clamp
32 ft 1-1/4" x 3 1/2" clear fir for frames (random lengths)
1 pc. 4 ft. 1-1/4" x 11-1/2" clear fir for aft two frame bottoms
1 pc. 16 ft - 1-1/2" x 5 1/2" clear fir for keelson (one piece)
1 pc. 8' 1-1/2" x 11-1/2" clear fir for motor mount, gussets and well sides.
12 dozen #8 x 1 1/4" stainless steel wood screws
4 dozen #10 x 2" stainless steel wood screws
16 ea. #10 x 4" flat head stainless machine screws, washers & nuts
8 ea. 1/4" x 3" stainless steel lag screws
5 - gallon epoxy
A dozen or so inexpensive disposable paint brushes of various widths
Rubber gloves
Respirators (for sanding dust) & safety glasses

In addition, for the strongback and frame jig, you'll need the following materials:

1 - 16' fir 4x6s
3 - 8' 2x4 studs
3 - 3' fir 4x4s
6 - Metal Tee Brackets
1 sheet 1/2" shop ply
Some scraps of 1x2 furring strip
Handful of 16d box nails
Handful of 2d box nails
Woodworking (or white) glue