


NOTICE
THIS DRAWING CONTAINS A PROPRIETARY DESIGN ASSIGNED TO SPIRA INTERNATIONAL, INC. ALL RIGHTS TO DUPLICATE, TRANSFER OR SELL THIS DESIGN ARE EXPRESSLY RESERVED. THE BUYER IS LICENSED TO BUILD ONE ASSEMBLY FROM THESE PLANS.

REVISIONS				
ZONE	LTR	DESCRIPTION	DATE	APPROVED

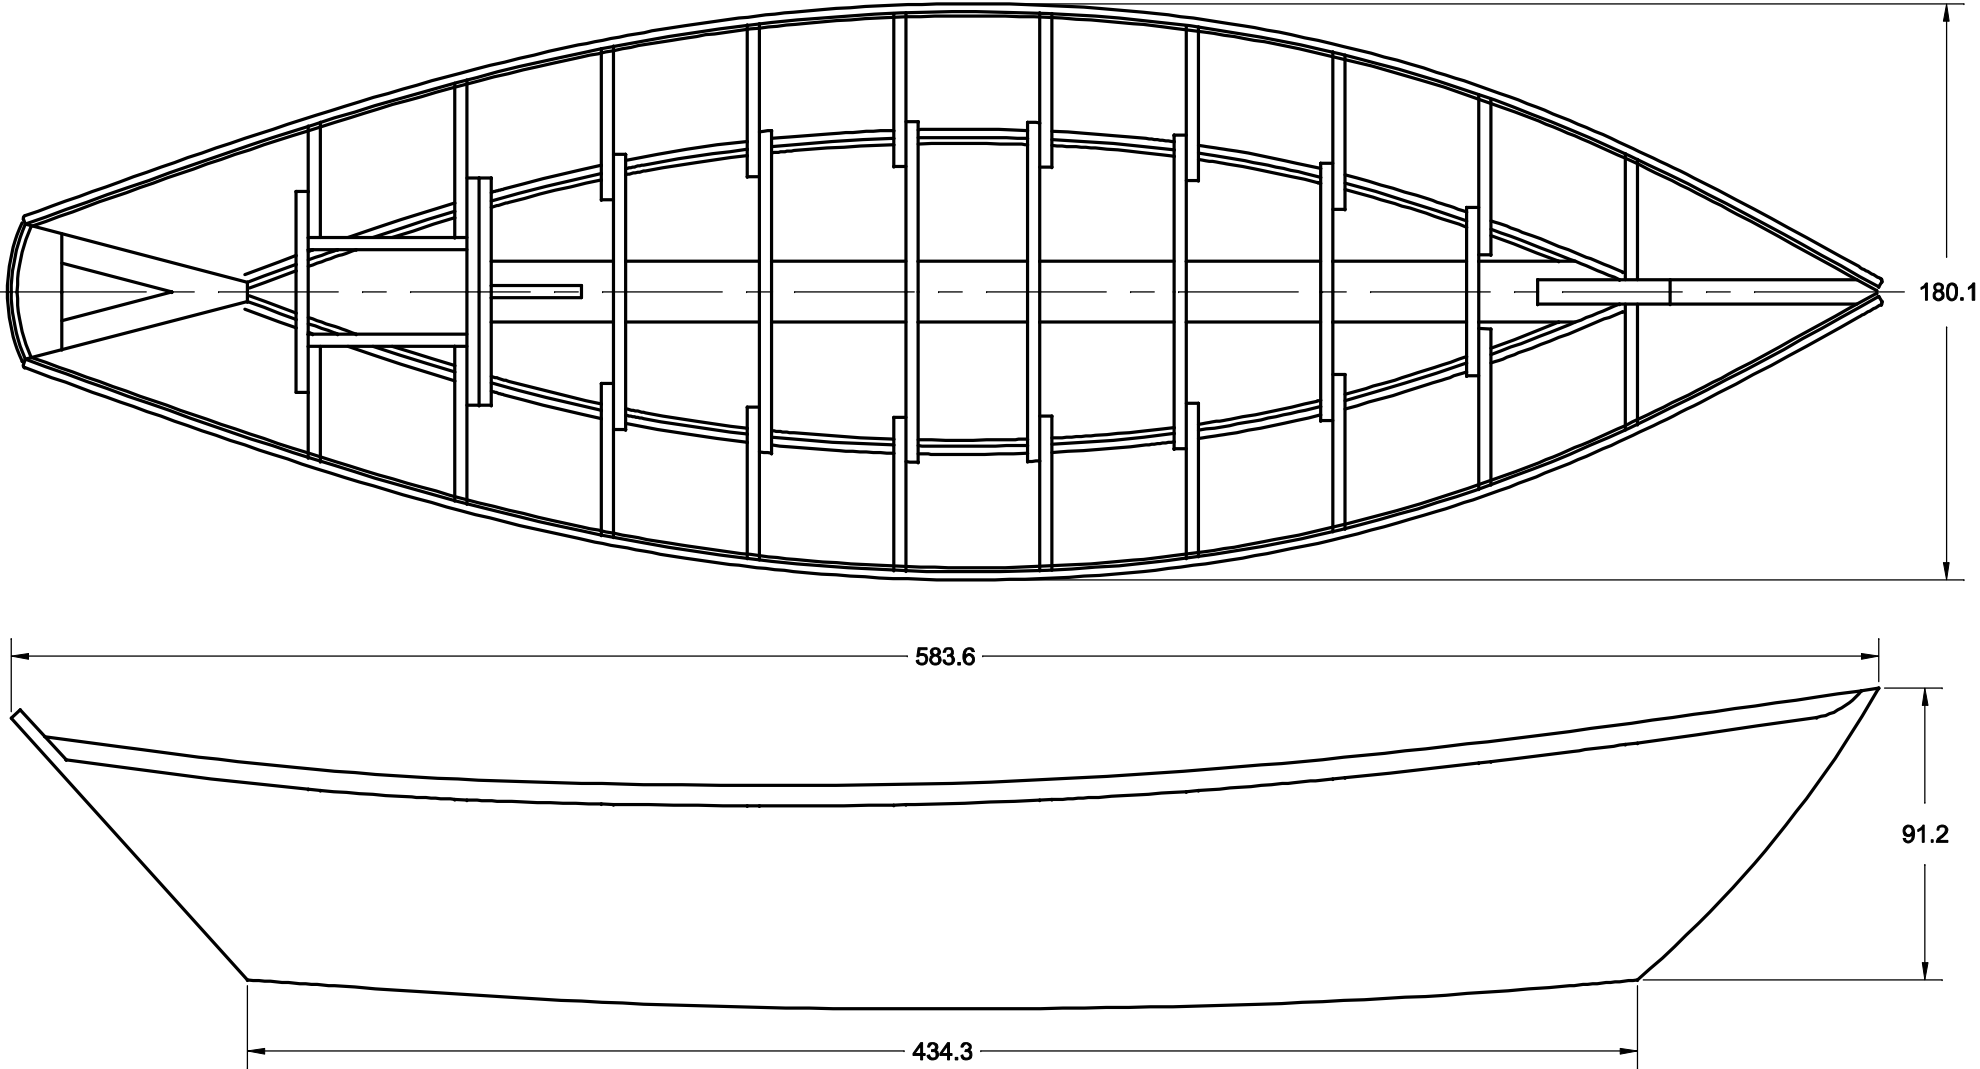

Spira International, Inc.
Huntington Beach, California

ALASKAN
5.8M GRAND BANKS DORY

DRAWN BY:
J. SPIRA

DATE:
06/25/09

DRAWING NO.
ALAS01




SCALE 1/30

SHEET OF












ALL DIMENSIONS IN CENTIMETERS

NOTICE
THIS DRAWING CONTAINS A PROPRIETARY DESIGN ASSIGNED TO SPIRA INTERNATIONAL, INC. ALL RIGHTS TO DUPLICATE, TRANSFER OR SELL THIS DESIGN ARE EXPRESSLY RESERVED. THE BUYER IS LICENSED TO BUILD ONE ASSEMBLY FROM THESE PLANS.

REVISIONS				
ZONE	LTR	DESCRIPTION	DATE	APPROVED

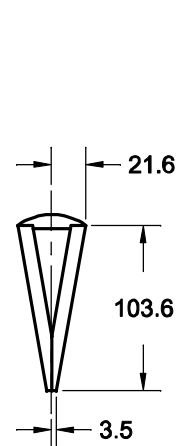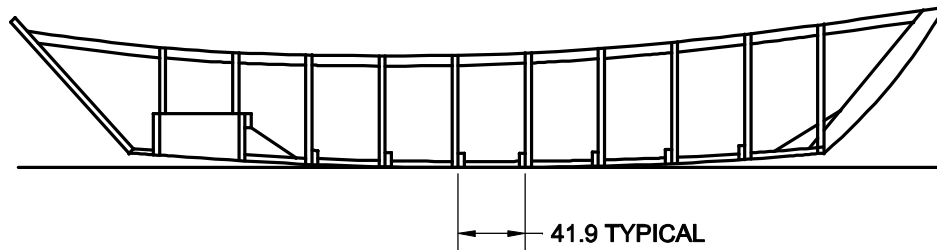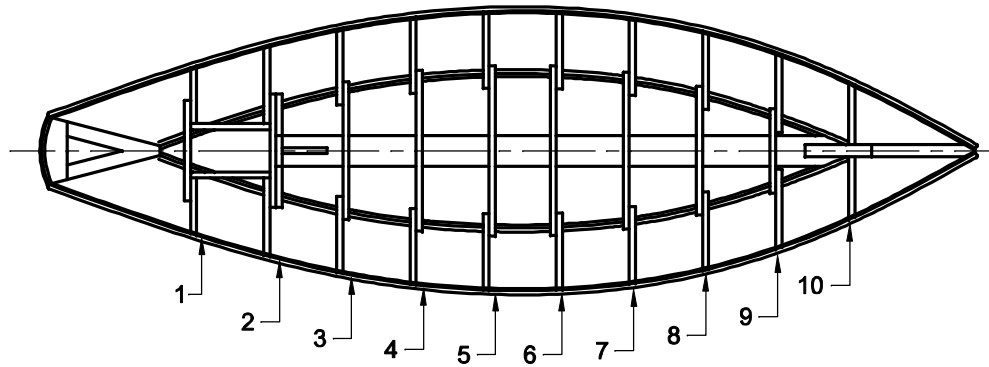

TRANSOM

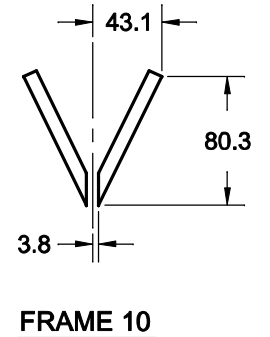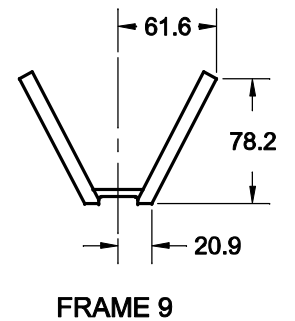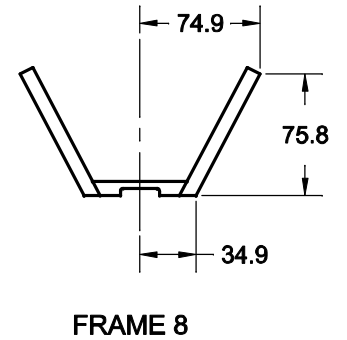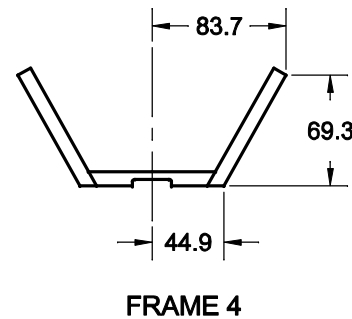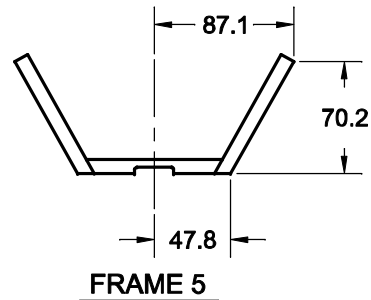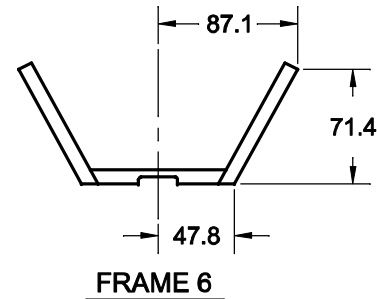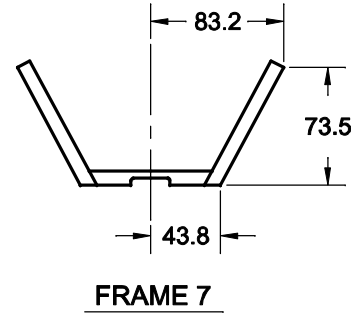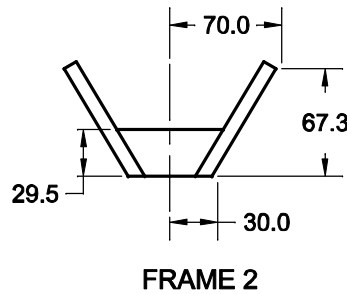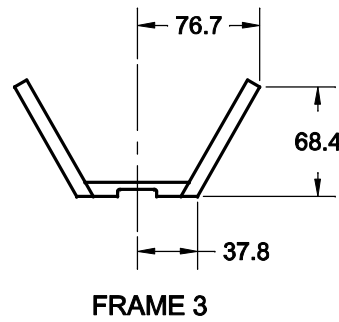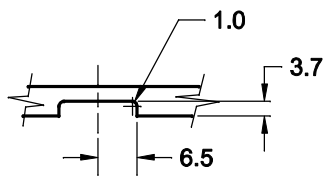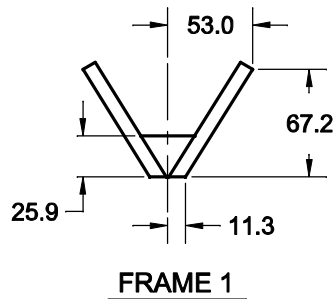

Spira International, Inc.
Huntington Beach, California

**ALASKAN
FRAMING PLAN**

DRAWN BY: J. SPIRA	DATE: 05/25/09	DRAWING NO. ALAS02M
SCALE 1/60	SHEET OF	