


NOTICE
THIS DRAWING CONTAINS A PROPRIETARY DESIGN ASSIGNED TO SPIRA INTERNATIONAL, INC. ALL RIGHTS TO DUPLICATE, TRANSFER OR SELL THIS DESIGN ARE EXPRESSLY RESERVED. THE BUYER IS LICENSED TO BUILD ONE ASSEMBLY FROM THESE PLANS.

REVISIONS				
ZONE	LTR	DESCRIPTION	DATE	APPROVED
	A	UPDATED TO NEW FORMAT	09/20/08	JJS

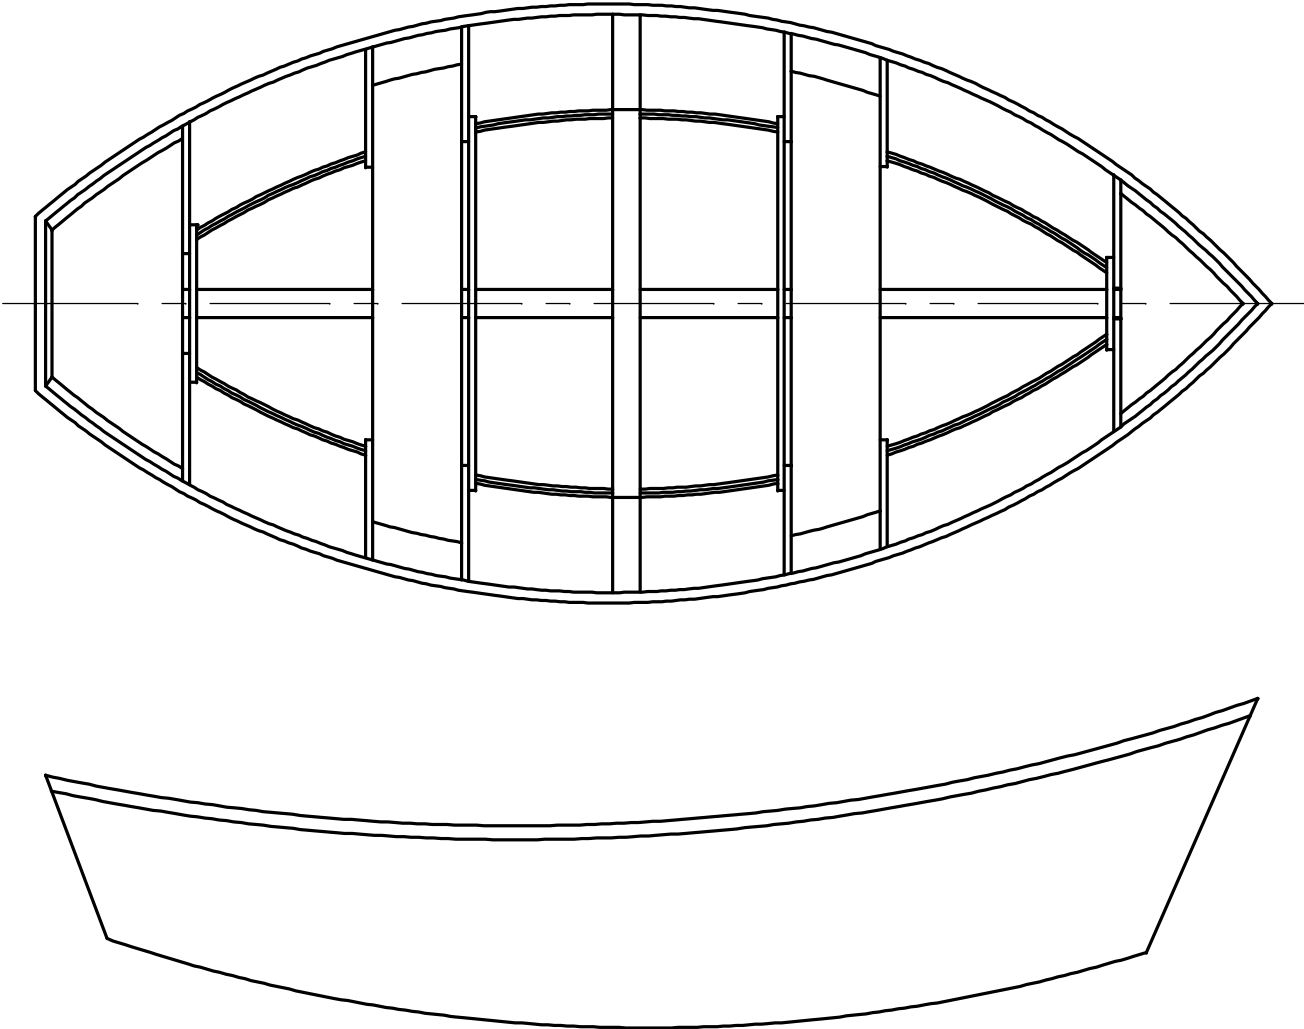

MACKINAW	
LENGTH	12' 10"
BEAM	6' 3"
FREEBOARD	28"


Spira International, Inc. <i>Huntington Beach, California</i>		
MACKINAW MCKENZIE RIVER DRIFT BOAT		
DRAWN BY: J. SPIRA	DATE: 02/27/00	DRAWING NO. MACK01
SCALE 1" = 1'	SHEET OF	

NOTICE


THIS DRAWING CONTAINS A PROPRIETARY DESIGN ASSIGNED TO SPIRA INTERNATIONAL, INC. ALL RIGHTS TO DUPLICATE, TRANSFER OR SELL THIS DESIGN ARE EXPRESSLY RESERVED. THE BUYER IS LICENSED TO BUILD ONE ASSEMBLY FROM THESE PLANS.

REVISIONS

ZONE	LTR	DESCRIPTION	DATE	APPROVED
	A	UPDATED TO NEW FORMAT	09/20/08	JJS

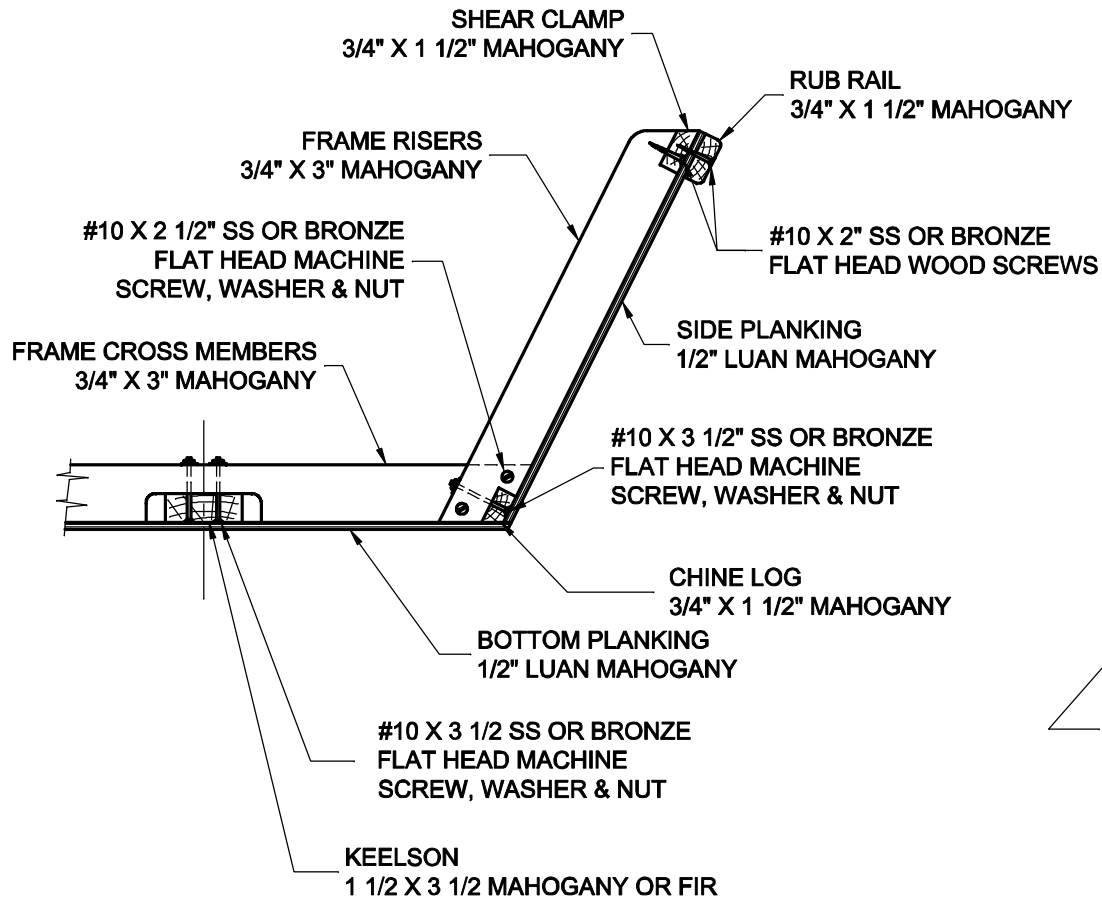

CONSTRUCTION METHOD
TYPICAL AT EACH FRAME

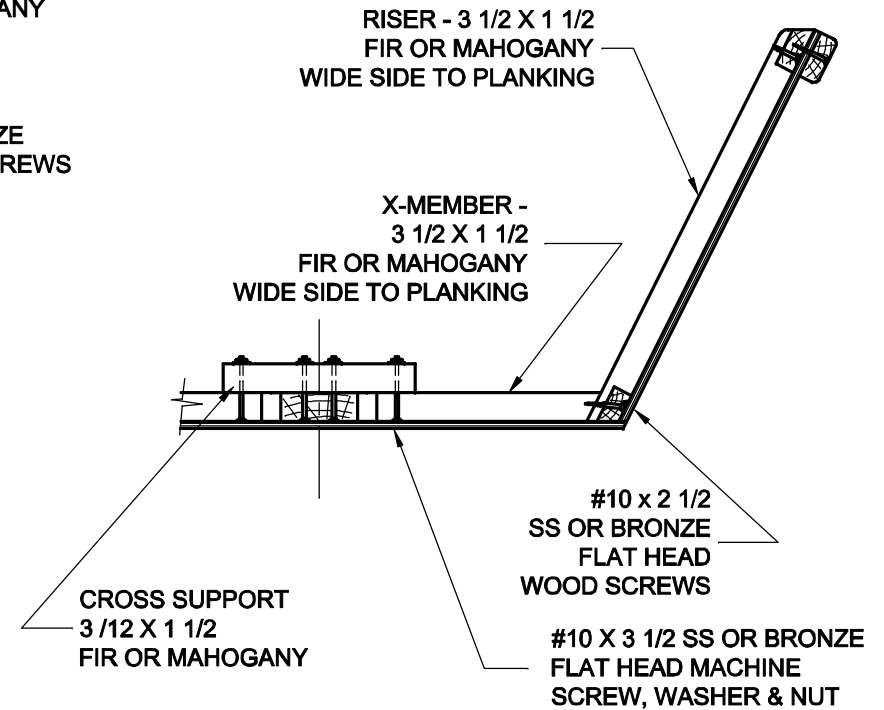

CONSTRUCTION METHOD
CENTER FRAME ONLY
WIDE FRAMS SERVES AS BUTT BLOCK
FOR PLYWOOD PLANKING JOINT

Spira International, Inc.
Huntington Beach, California

MACKINAW
CONSTRUCTION DETAILS

DRAWN BY: J. SPIRA	DATE: 3/07/00	DRAWING NO. MACK03
SCALE 1/5 & NOTED	SHEET	OF