

4

3


2

1

NOTICE

THIS DRAWING CONTAINS A PROPRIETARY DESIGN ASSIGNED TO SPIRA INTERNATIONAL, INC. ALL RIGHTS TO DUPLICATE, TRANSFER OR USE ARE EXPRESSLY RESERVED BY SPIRA INTERNATIONAL. THE BUYER IS LICENSED TO BUILD ONE ASSEMBLY FROM THESE PLANS.

REVISIONS				
ZONE	LTR	DESCRIPTION	DATE	APPROVED

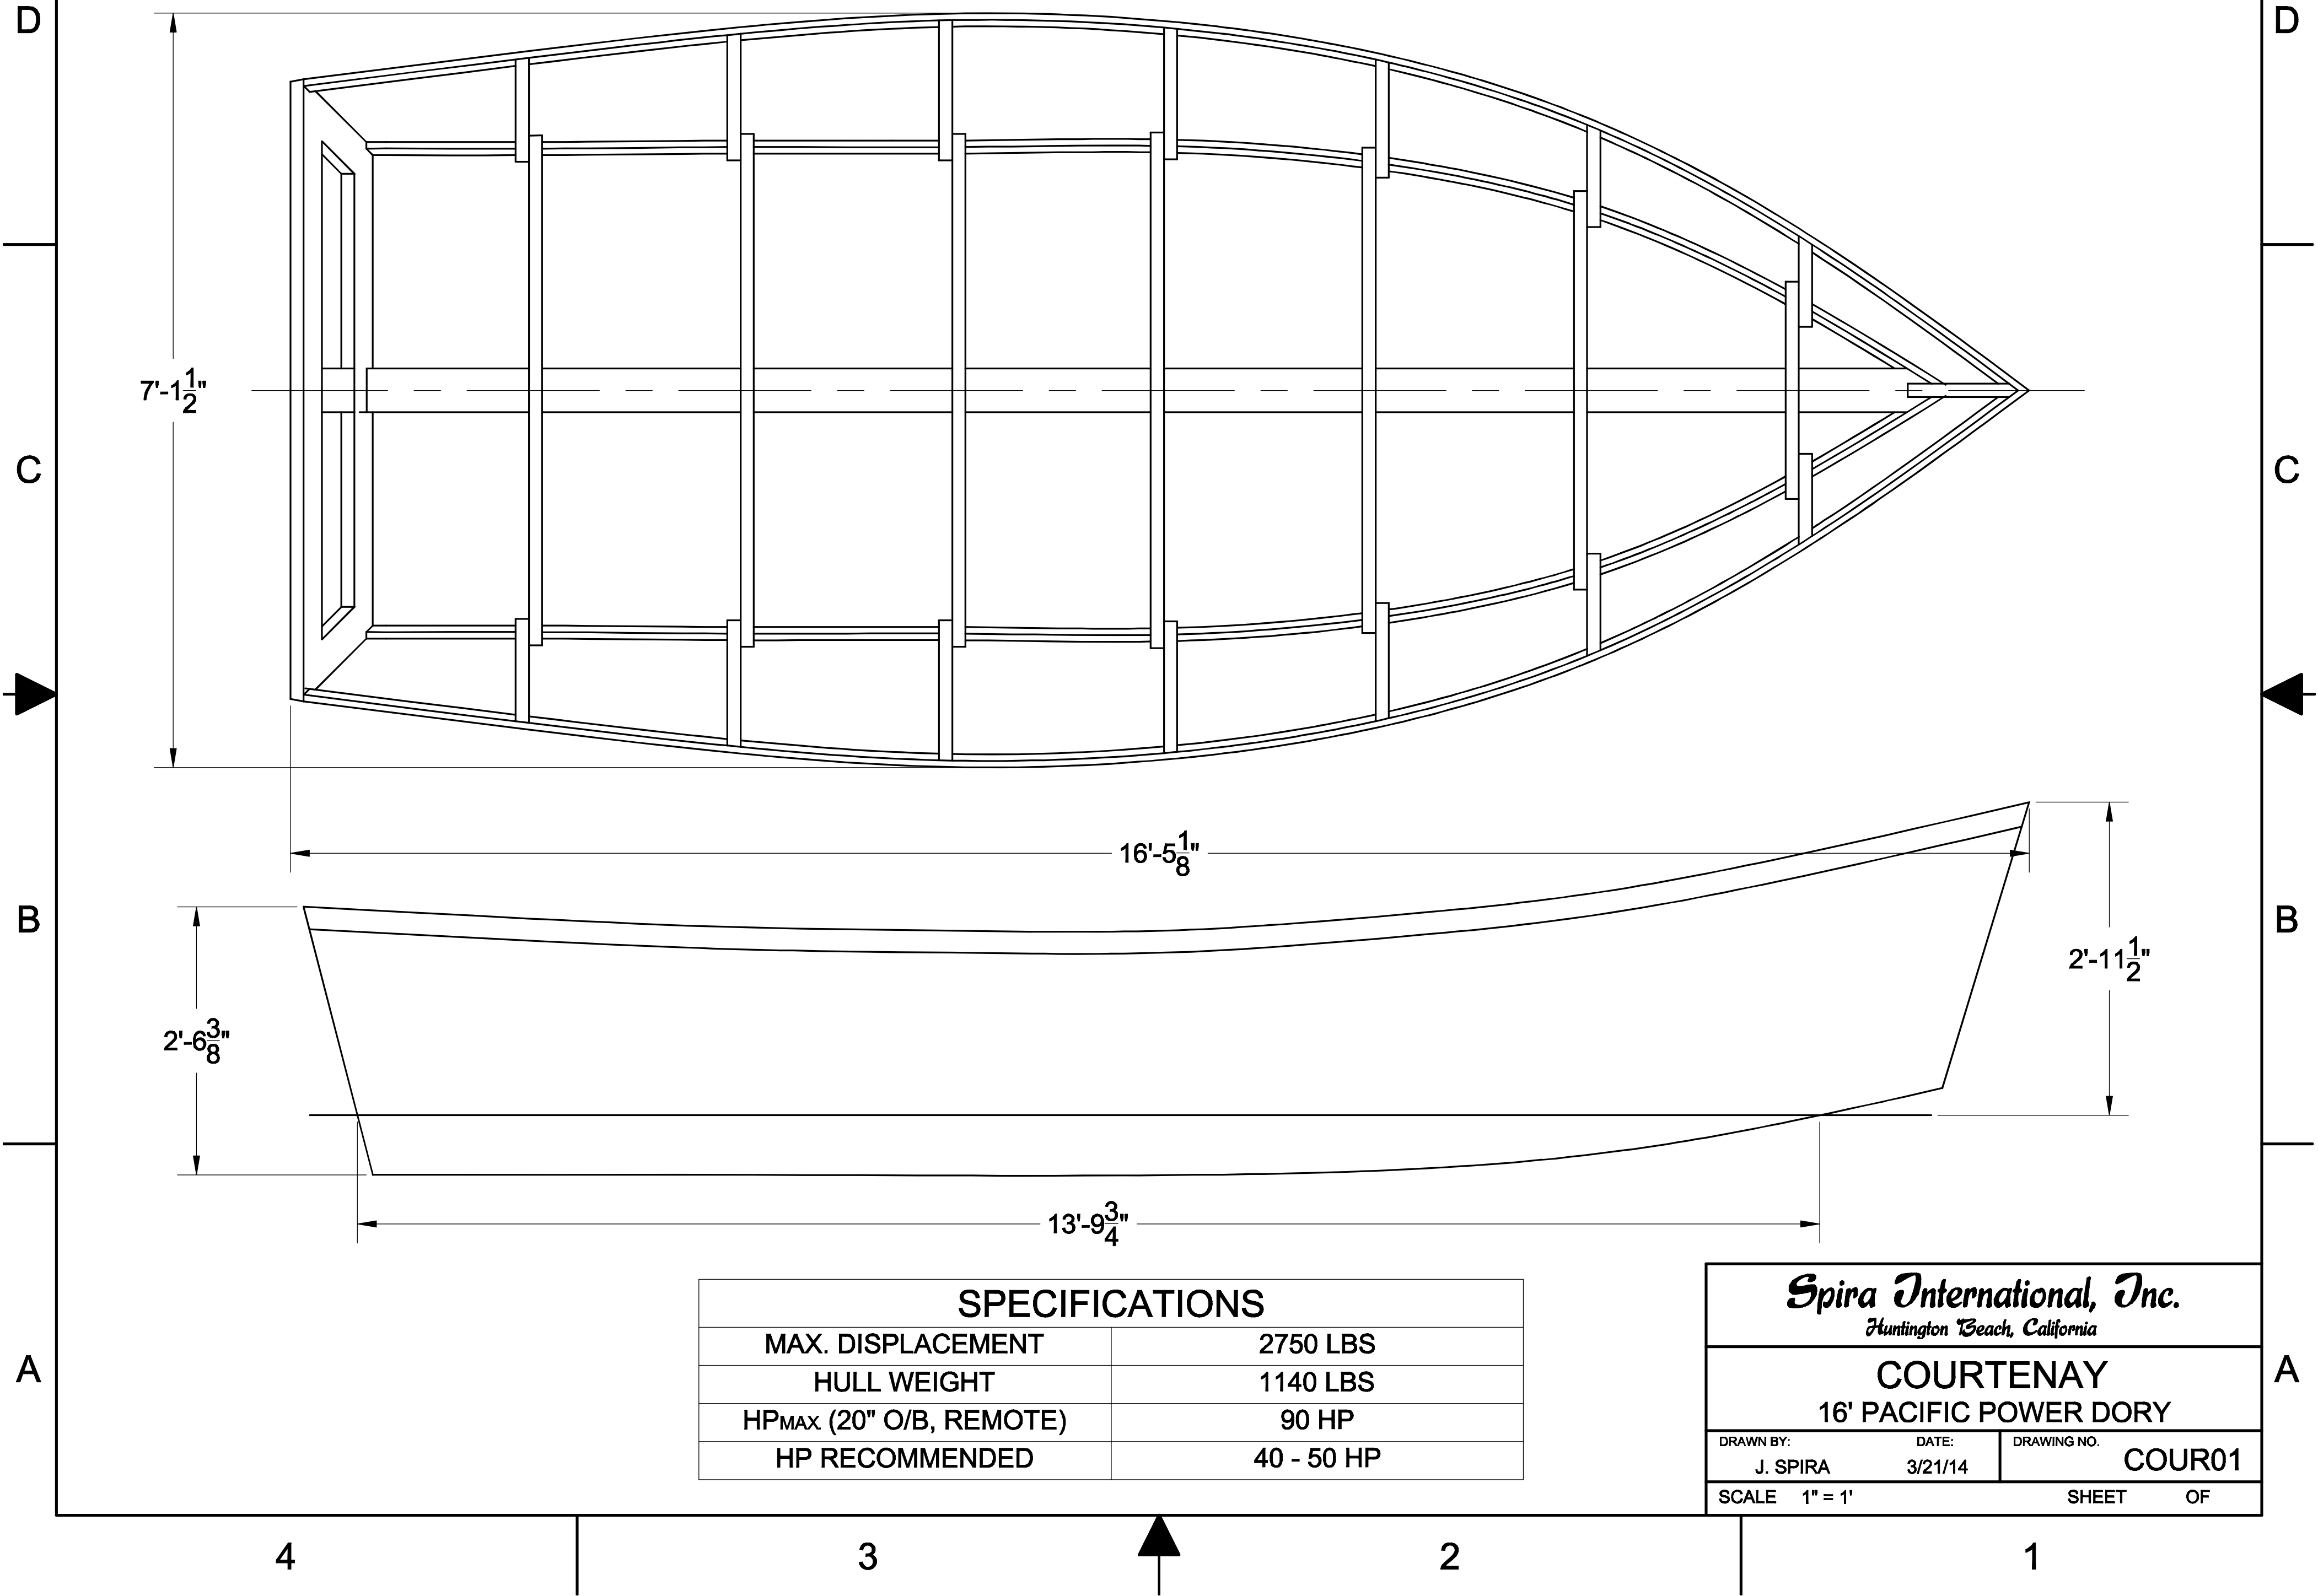

4

3

2

1

NOTICE

THIS DRAWING CONTAINS A PROPRIETARY DESIGN ASSIGNED TO SPIRA INTERNATIONAL, INC. ALL RIGHTS TO DUPLICATE, TRANSFER OR USE ARE EXPRESSLY RESERVED BY SPIRA INTERNATIONAL. THE BUYER IS LICENSED TO BUILD ONE ASSEMBLY FROM THESE PLANS.

REVISIONS

ZONE	LTR	DESCRIPTION	DATE	APPROVED

D

D

C


C

B

B

A

A

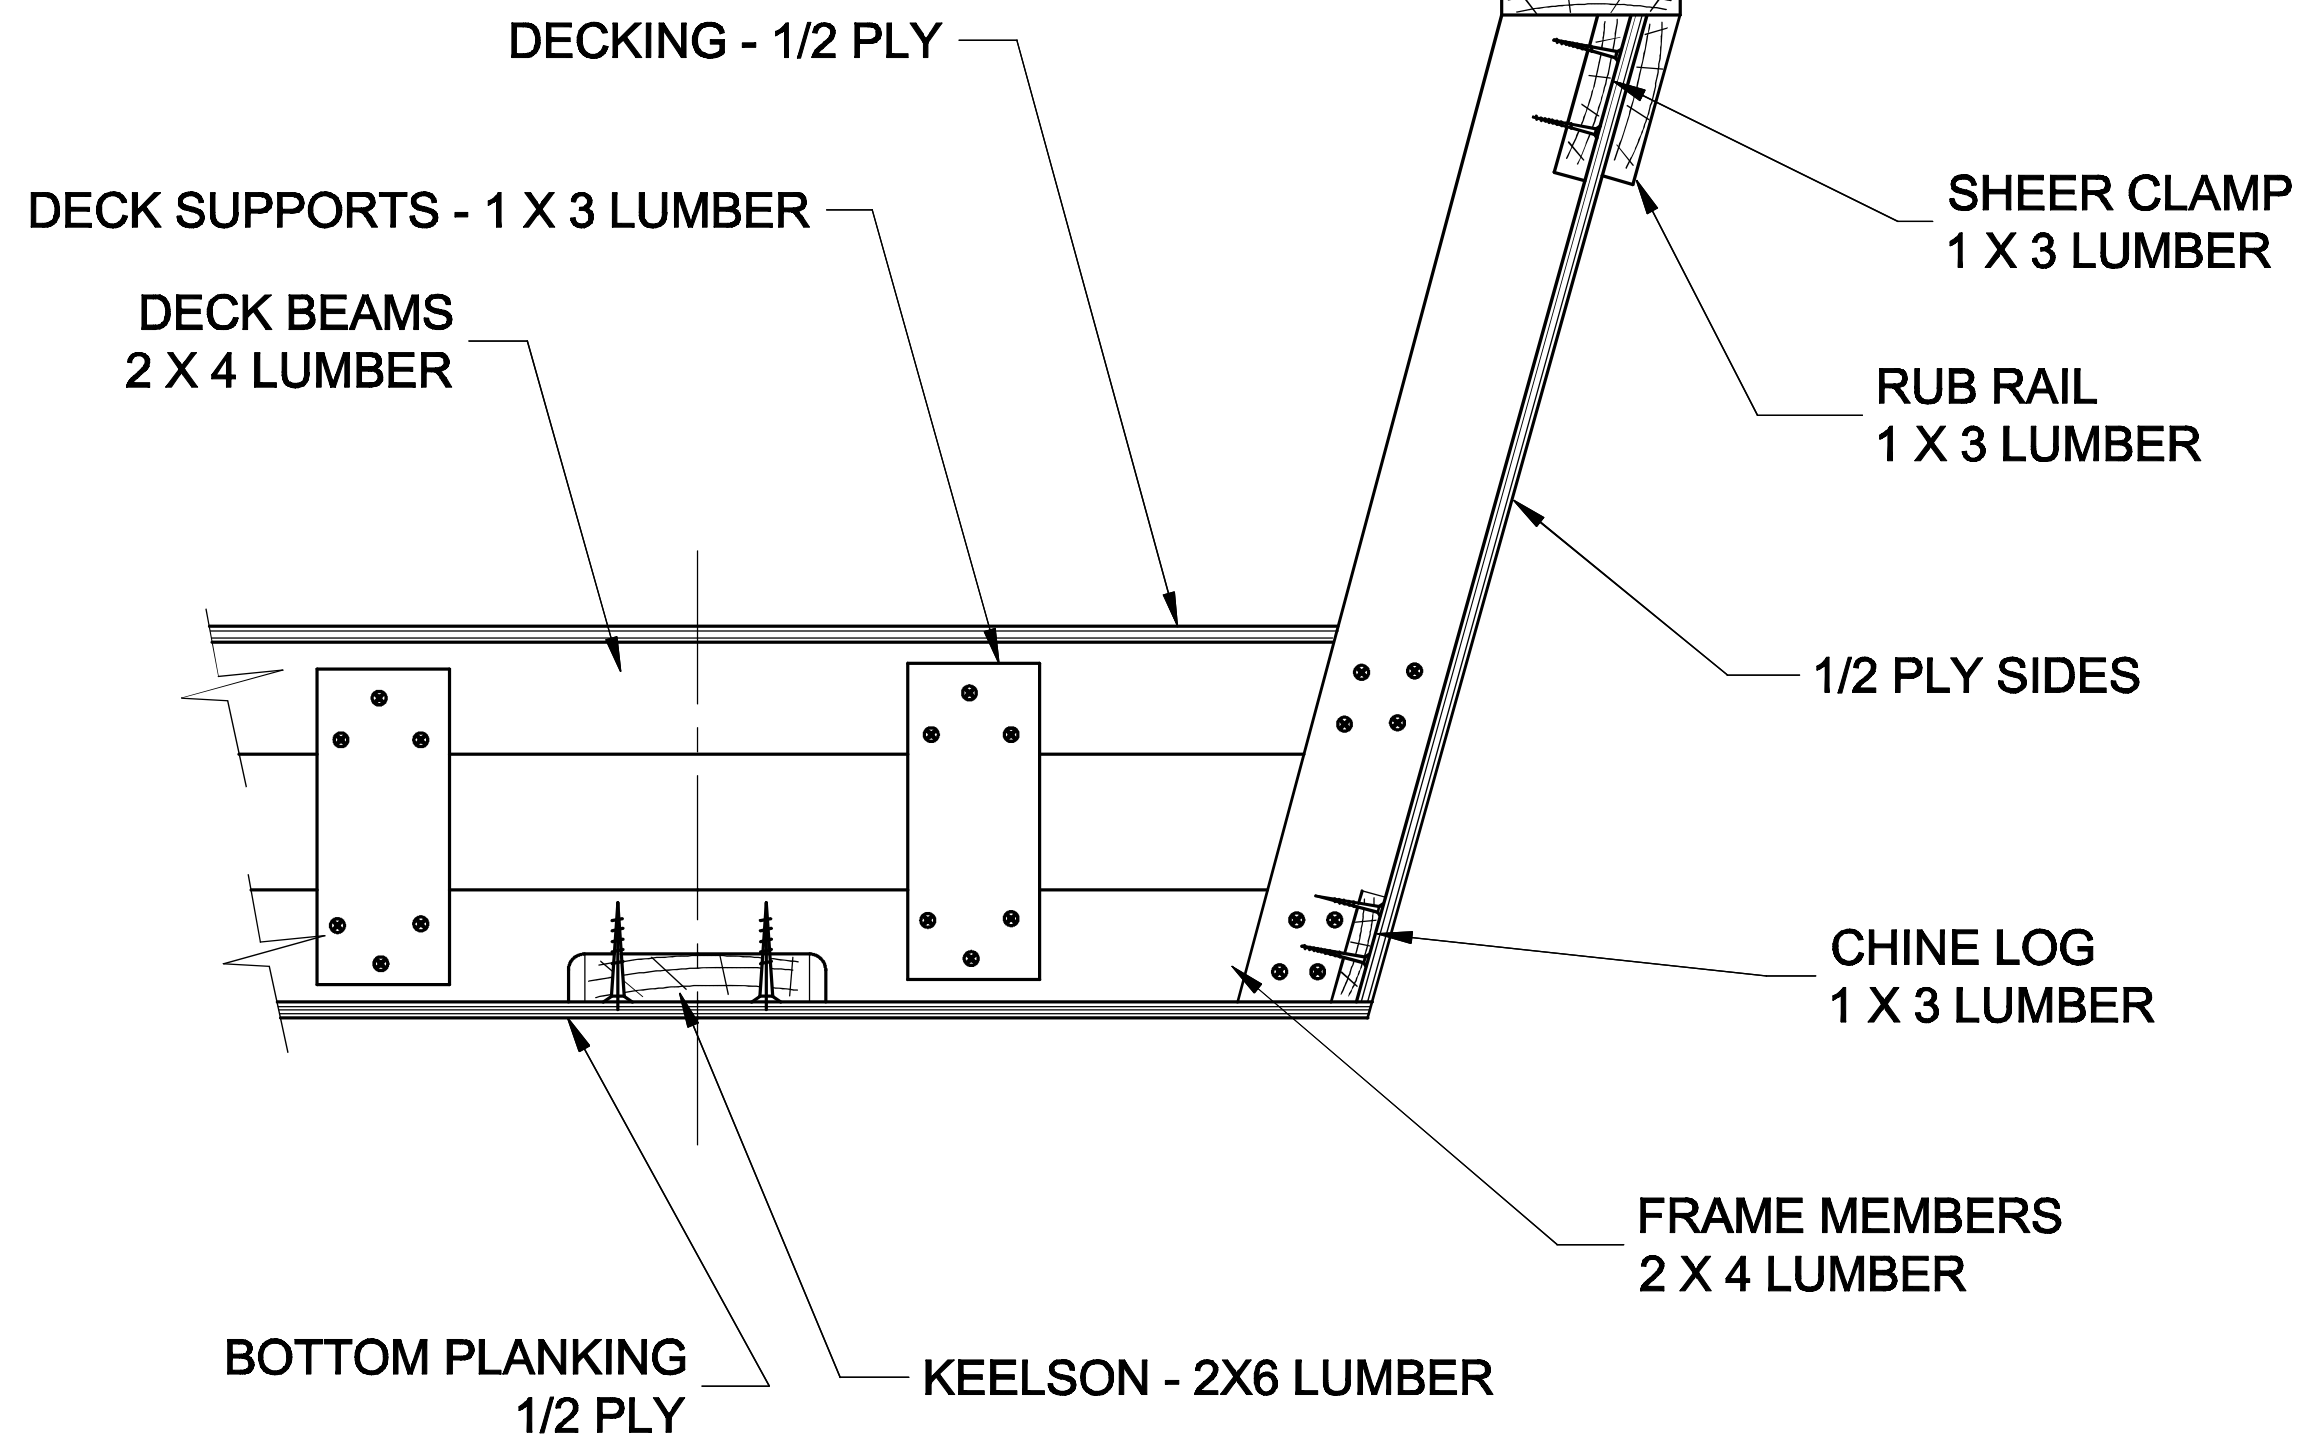

BILL OF MATERIALS

FRAMES: 148 FT 2X4S
FRAMES: 24 FT 2X6S
S/C, C/L & R/R: 110' 1X3S
RAIL CAP: 40' 1X8
SIDES: 4 SHTS 1/2" PLY
BOTTOM & DECK: 6 SHTS 1/2" PLY
GLASS: 30 YDS - 6 OZ CLOTH
EPOXY: 3 GAL
FRAMES: 200 - #10 X 3" SCREWS
LONG'S: 100 - #8 X 2" SCREWS
PLANKING: 600 - #8 X 1-1/2" SCREWS

TYPICAL CONSTRUCTION METHOD
ALL FRAME STATIONS

SCALE 2" = 1'

NOTES:

1. YOU MAY SCARF TOGETHER SHORTER PIECES TO CREATE THE LONGITUDINAL ELEMENTS.
2. NOMINAL LUMBER SIZED CALLED OUT, E.G. A 2 X 4 LUMBER IS ACTUAL SIZE 1-1/2" X 3-1/2"

FASTENING SCHEDULE

KEELSON TO FRAMES: #10 X 3 DECK SCREWS
FRAMES TO FRAMES: #10 X 3 DECK SCREWS
LONGITUDINALS: #8 X 2 DECK SCREWS
PLY TO FRAMES: #8 X 1-1/2 DECK SCREWS

Spira International, Inc.
Huntington Beach, California

COURTENAY
16' PACIFIC POWER DORY

DRAWN BY: J. SPIRA	DATE: 3/21/14	DRAWING NO. COUR02
SCALE 1" = 1'		SHEET OF

4

3

2

1