
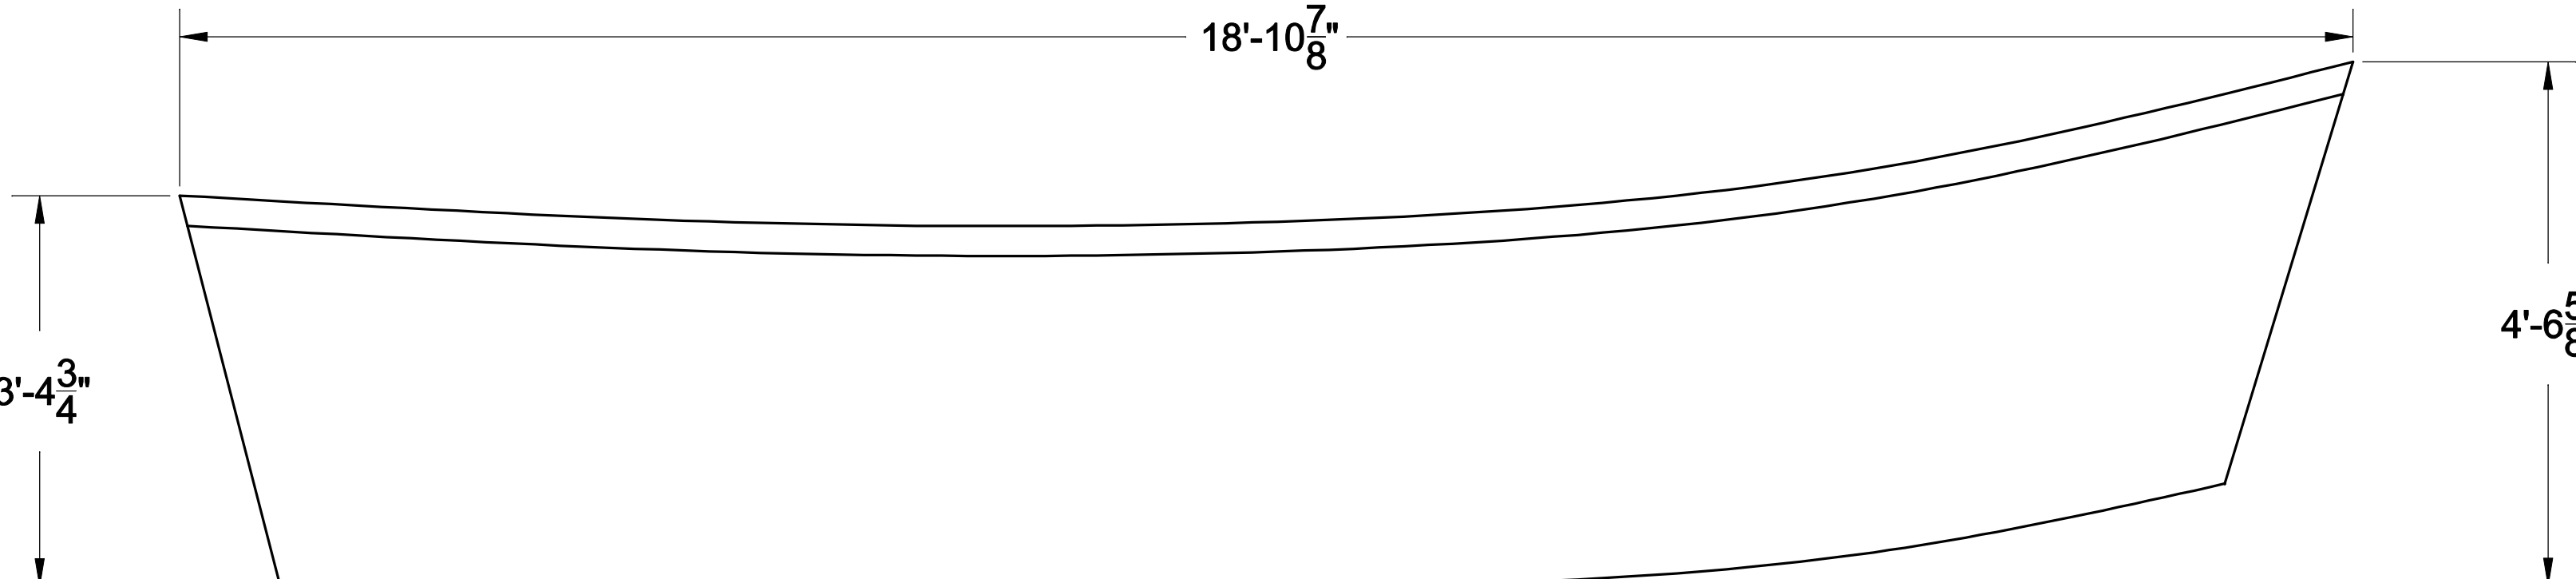


4

NOTICE
THIS DRAWING CONTAINS A PROPRIETARY DESIGN ASSIGNED TO SPIRA INTERNATIONAL, INC. ALL RIGHTS TO DUPLICATE, TRANSFER OR SELL THIS DESIGN ARE EXPRESSLY RESERVED. THE BUYER IS LICENSED TO BUILD ONE ASSEMBLY FROM THESE PLANS.

REVISIONS				
ZONE	LTR	DESCRIPTION	DATE	APPROVED

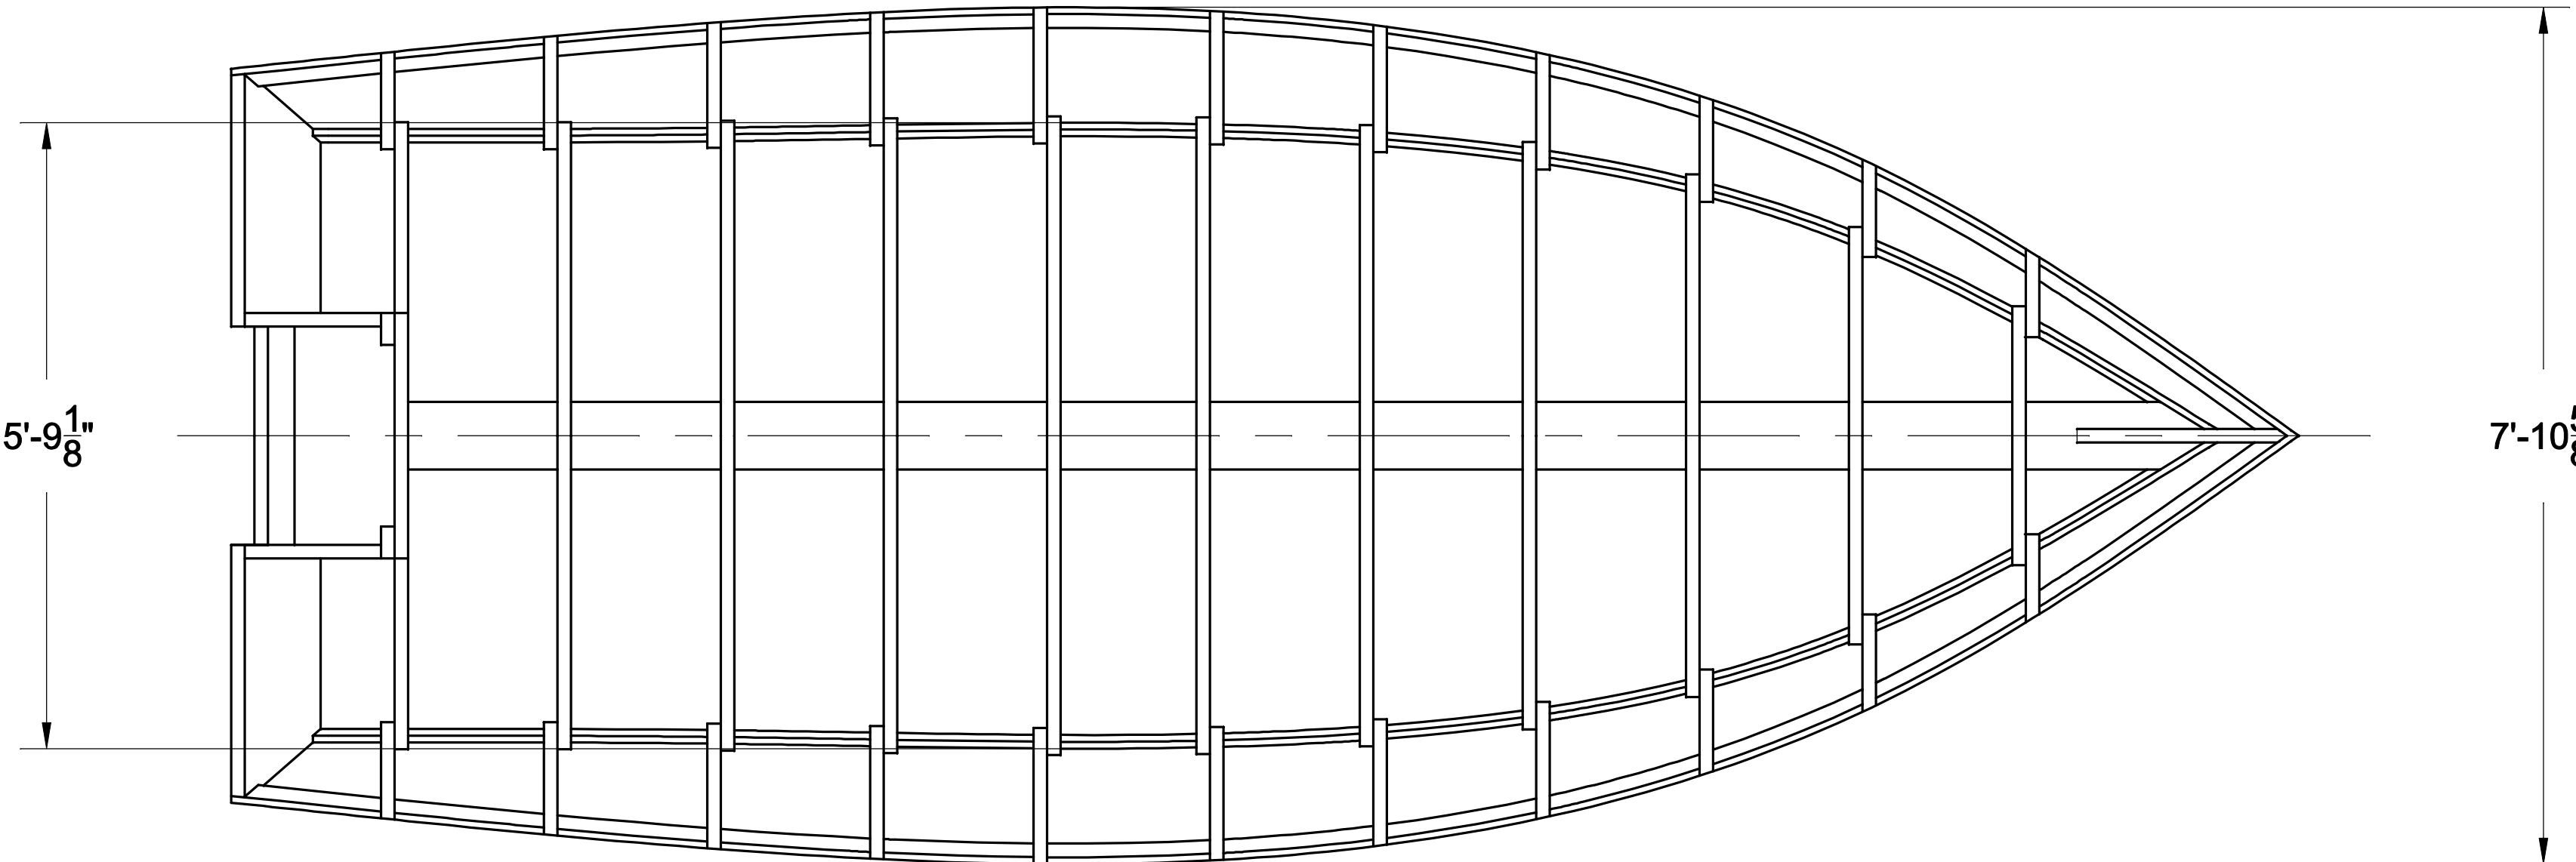


Spira International, Inc.
Huntington Beach, California

ANACAPA
19' OFFSHORE PACIFIC POWER DORY

DRAWN BY: J. SPIRA	DATE: 07/25/10	DRAWING NO. ANAC01
SCALE 3/4" = 1'		SHEET OF

NOTICE
THIS DRAWING CONTAINS A PROPRIETARY DESIGN ASSIGNED TO SPIRA INTERNATIONAL, INC. ALL RIGHTS TO DUPLICATE, TRANSFER OR SELL THIS DESIGN ARE EXPRESSLY RESERVED. THE BUYER IS LICENSED TO BUILD ONE ASSEMBLY FROM THESE PLANS.

REVISIONS				
ZONE	LTR	DESCRIPTION	DATE	APPROVED

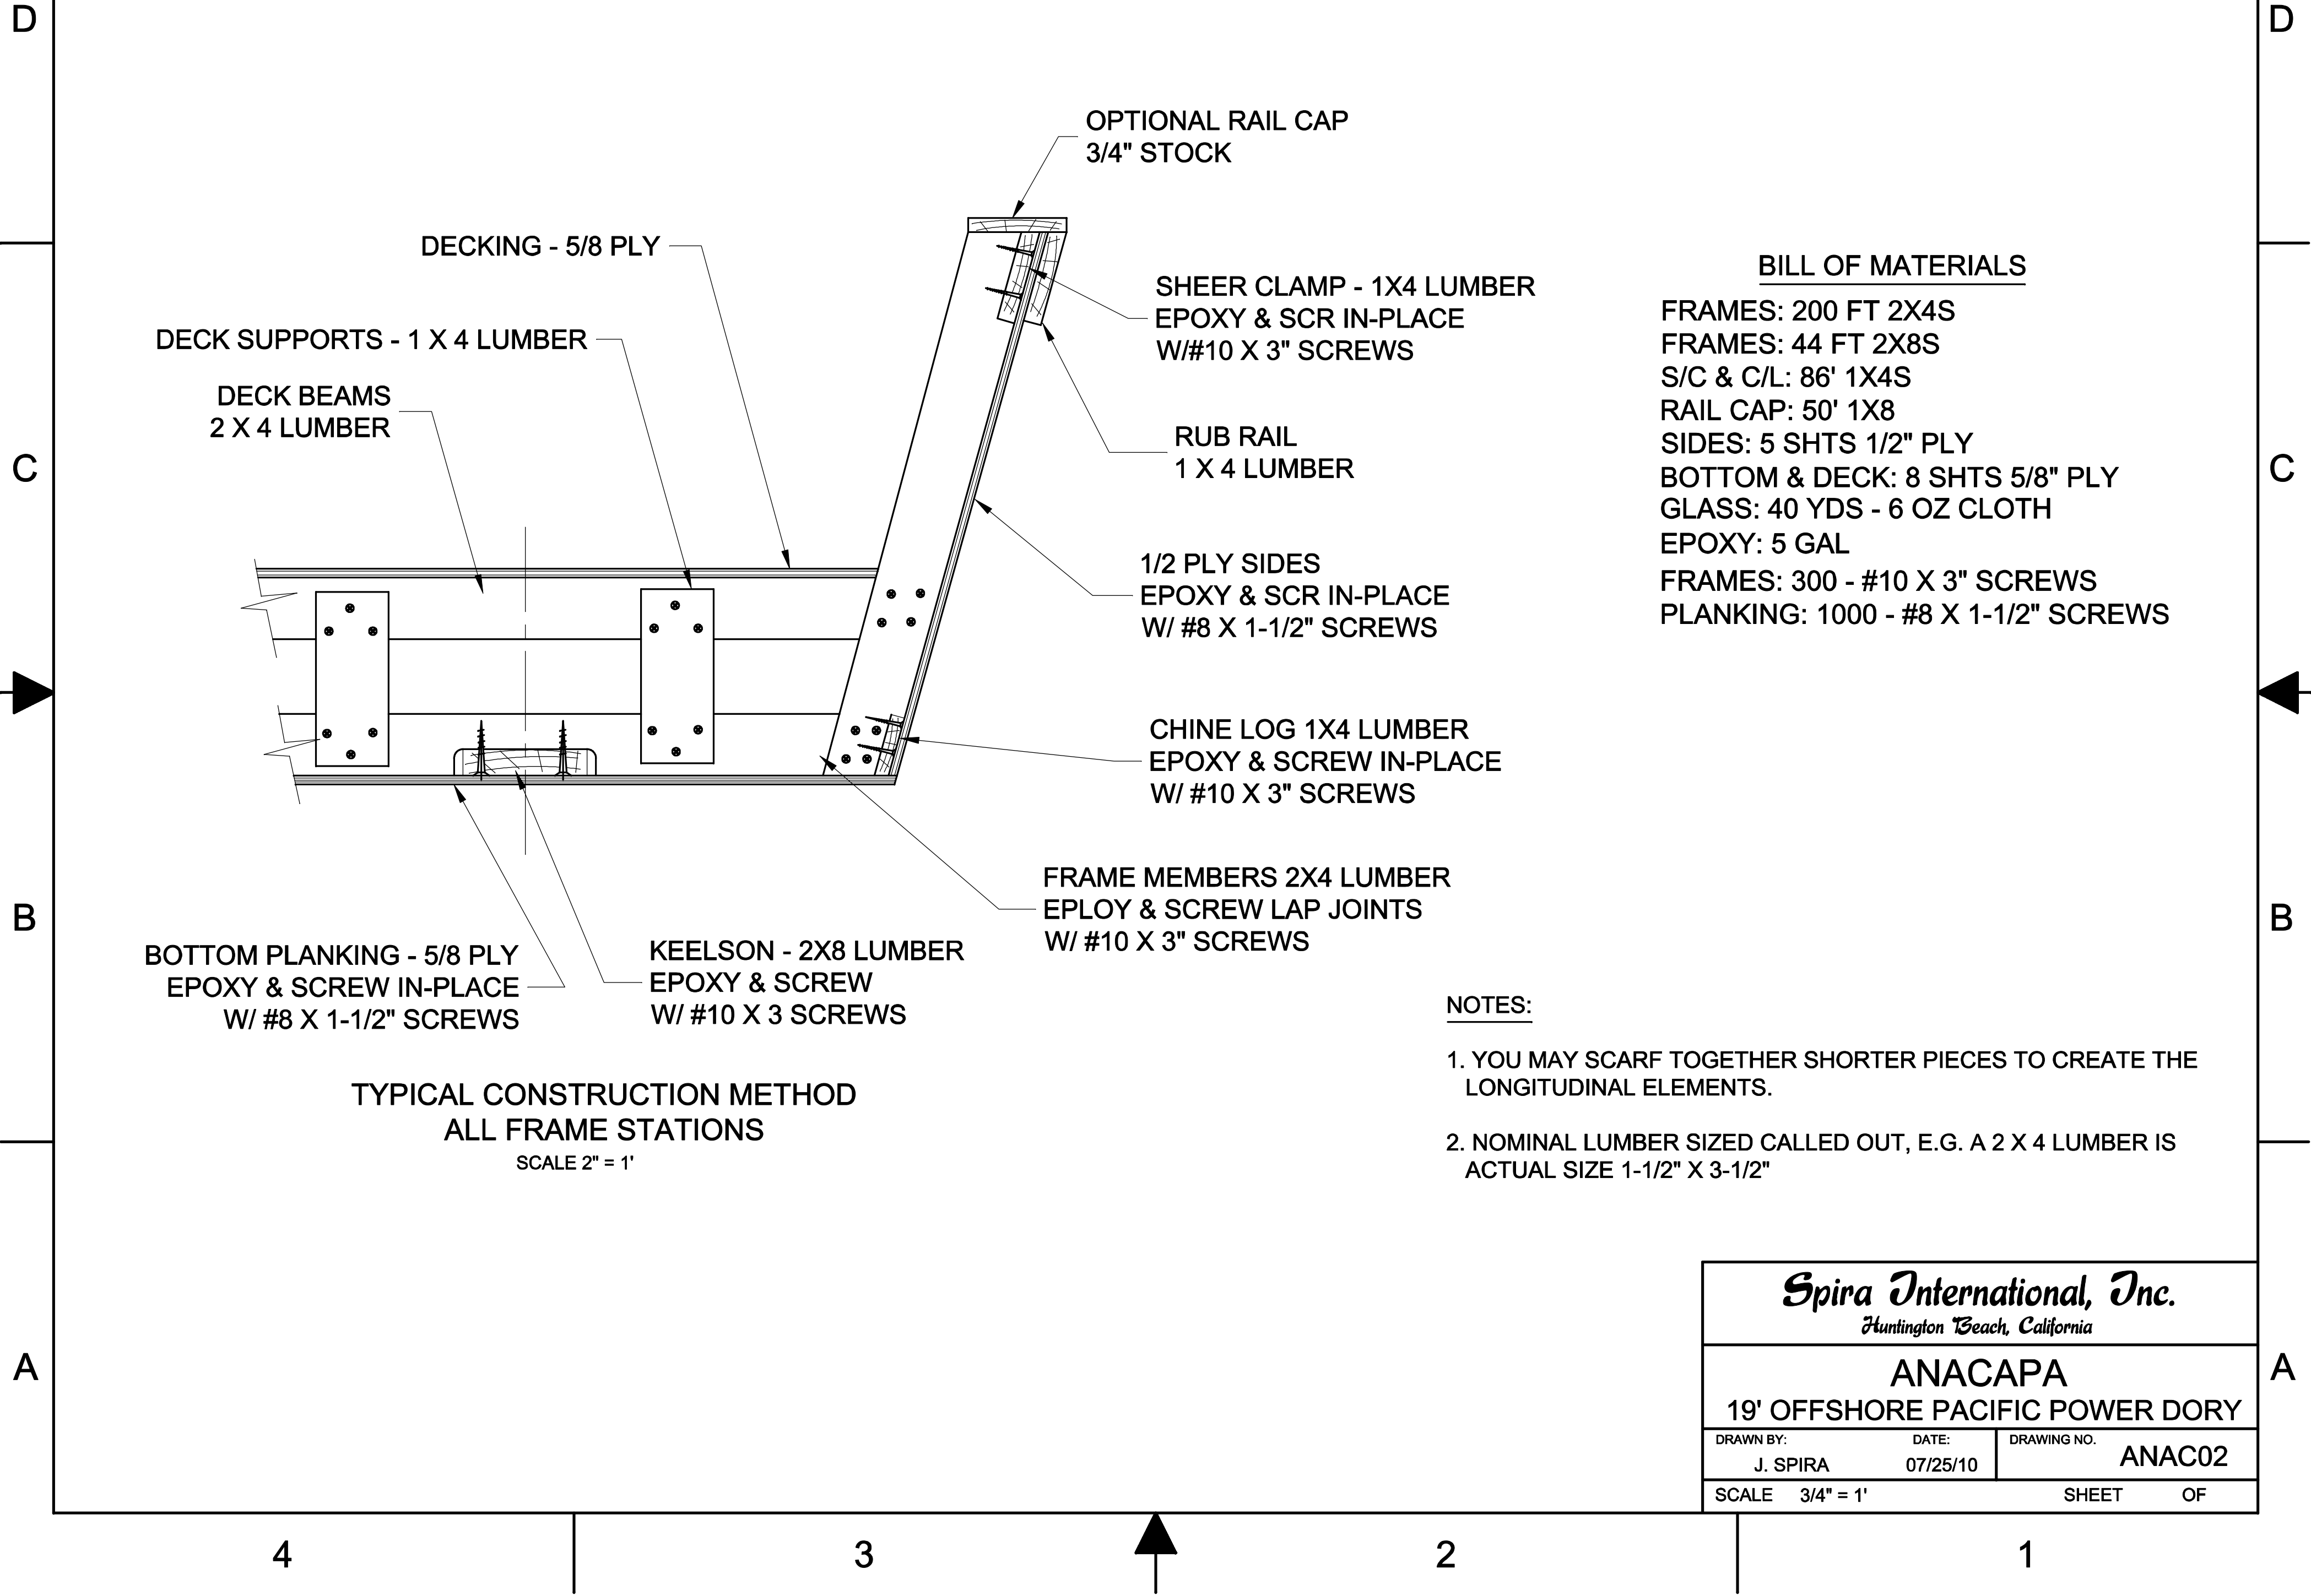

BILL OF MATERIALS

FRAMES: 200 FT 2X4S
FRAMES: 44 FT 2X8S
S/C & C/L: 86' 1X4S
RAIL CAP: 50' 1X8
SIDES: 5 SHTS 1/2" PLY
BOTTOM & DECK: 8 SHTS 5/8" PLY
GLASS: 40 YDS - 6 OZ CLOTH
EPOXY: 5 GAL
FRAMES: 300 - #10 X 3" SCREWS
PLANKING: 1000 - #8 X 1-1/2" SCREWS

NOTES:

1. YOU MAY SCARF TOGETHER SHORTER PIECES TO CREATE THE LONGITUDINAL ELEMENTS.
2. NOMINAL LUMBER SIZED CALLED OUT, E.G. A 2 X 4 LUMBER IS ACTUAL SIZE 1-1/2" X 3-1/2"

TYPICAL CONSTRUCTION METHOD
ALL FRAME STATIONS
SCALE 2" = 1'

Spira International, Inc. <i>Huntington Beach, California</i>			
ANACAPA 19' OFFSHORE PACIFIC POWER DORY			
DRAWN BY: J. SPIRA	DATE: 07/25/10	DRAWING NO. ANAC02	
SCALE 3/4" = 1'	SHEET OF		