

4

3




2

1

NOTICE

THIS DRAWING CONTAINS A PROPRIETARY DESIGN ASSIGNED TO SPIRA INTERNATIONAL, INC. ALL RIGHTS TO DUPLICATE, TRANSFER OR USE ARE EXPRESSLY RESERVED BY SPIRA INTERNATIONAL. THE BUYER IS LICENSED TO BUILD ONE ASSEMBLY FROM THESE PLANS.

REVISIONS				
ZONE	LTR	DESCRIPTION	DATE	APPROVED

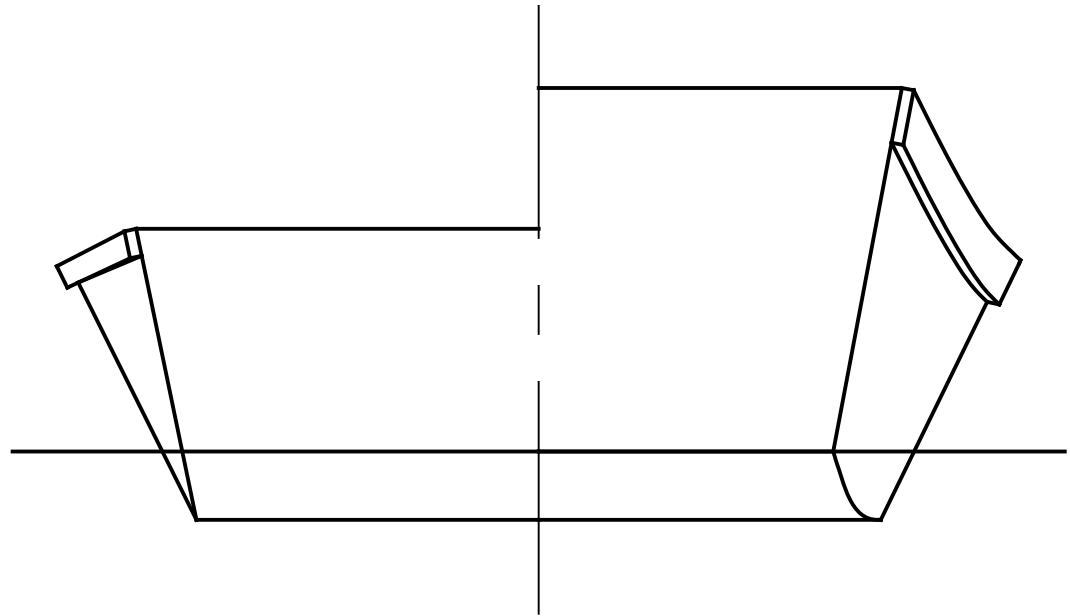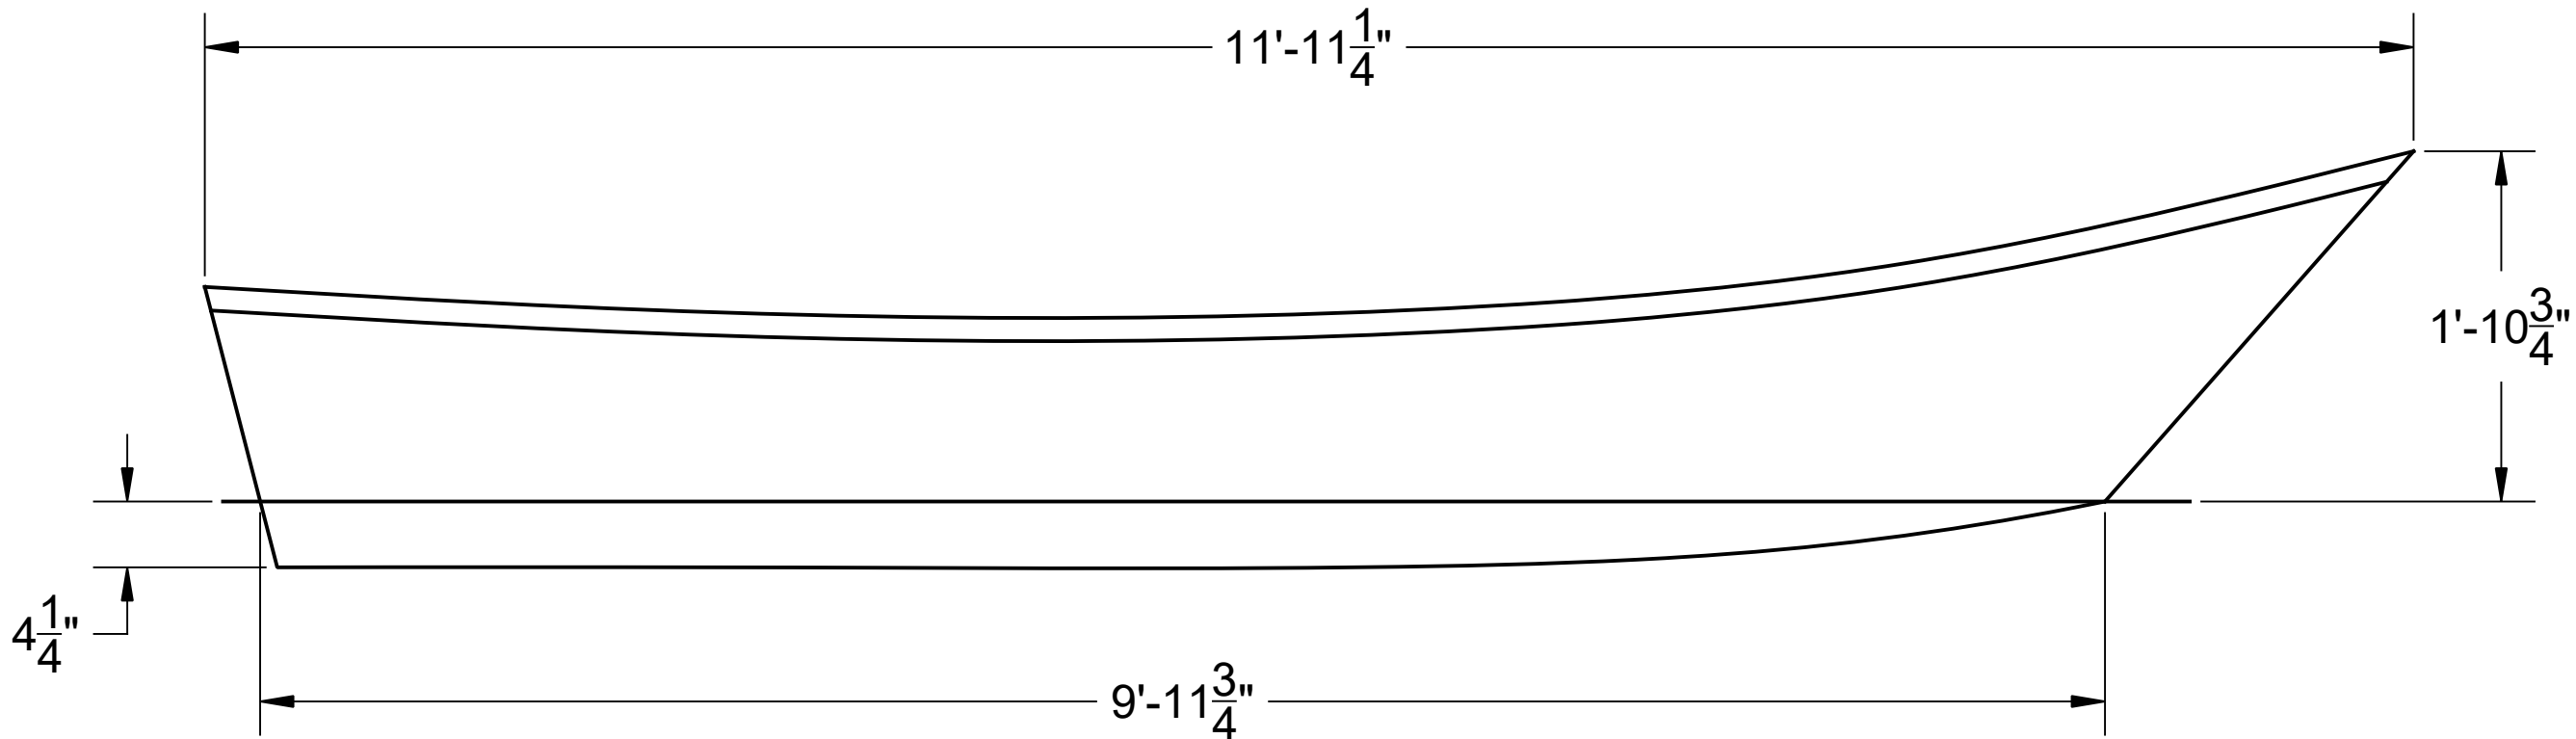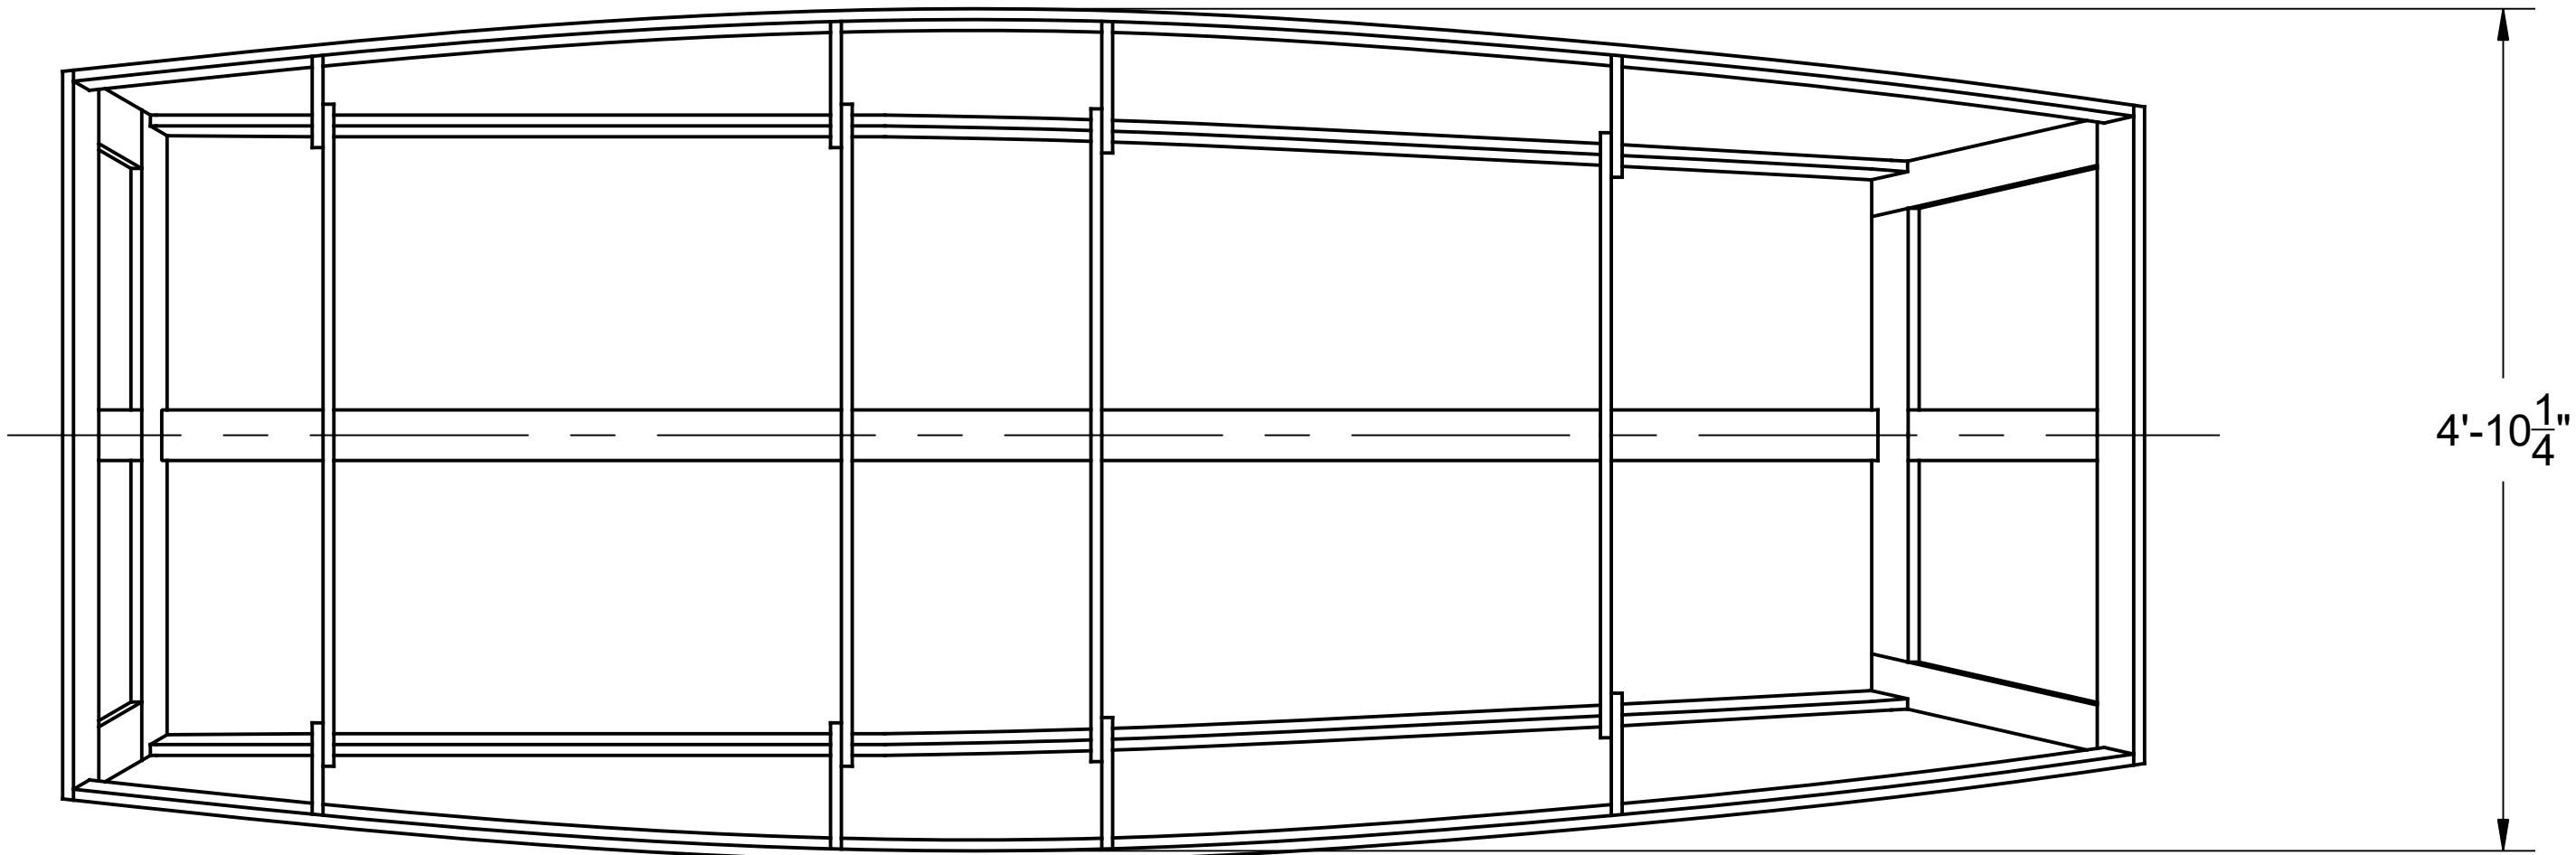

SPECIFICATIONS	
MAX. DISPLACEMENT	980 LBS
HULL WEIGHT	180 LBS
MAX. HP	7 1/2 HP
MAX HP	5 HP

 **Spira International, Inc.**
Huntington Beach, California

AVILA
12' GARVEY DORY

DRAWN BY: J. SPIRA	DATE: 07/29/16	DRAWING NO. AVIL01
SCALE 1' = 1' & NOTED		SHEET OF

4

3


2

1

NOTICE

THIS DRAWING CONTAINS A PROPRIETARY DESIGN ASSIGNED TO SPIRA INTERNATIONAL, INC. ALL RIGHTS TO DUPLICATE, TRANSFER OR USE ARE EXPRESSLY RESERVED BY SPIRA INTERNATIONAL. THE BUYER IS LICENSED TO BUILD ONE ASSEMBLY FROM THESE PLANS.

REVISIONS				
ZONE	LTR	DESCRIPTION	DATE	APPROVED

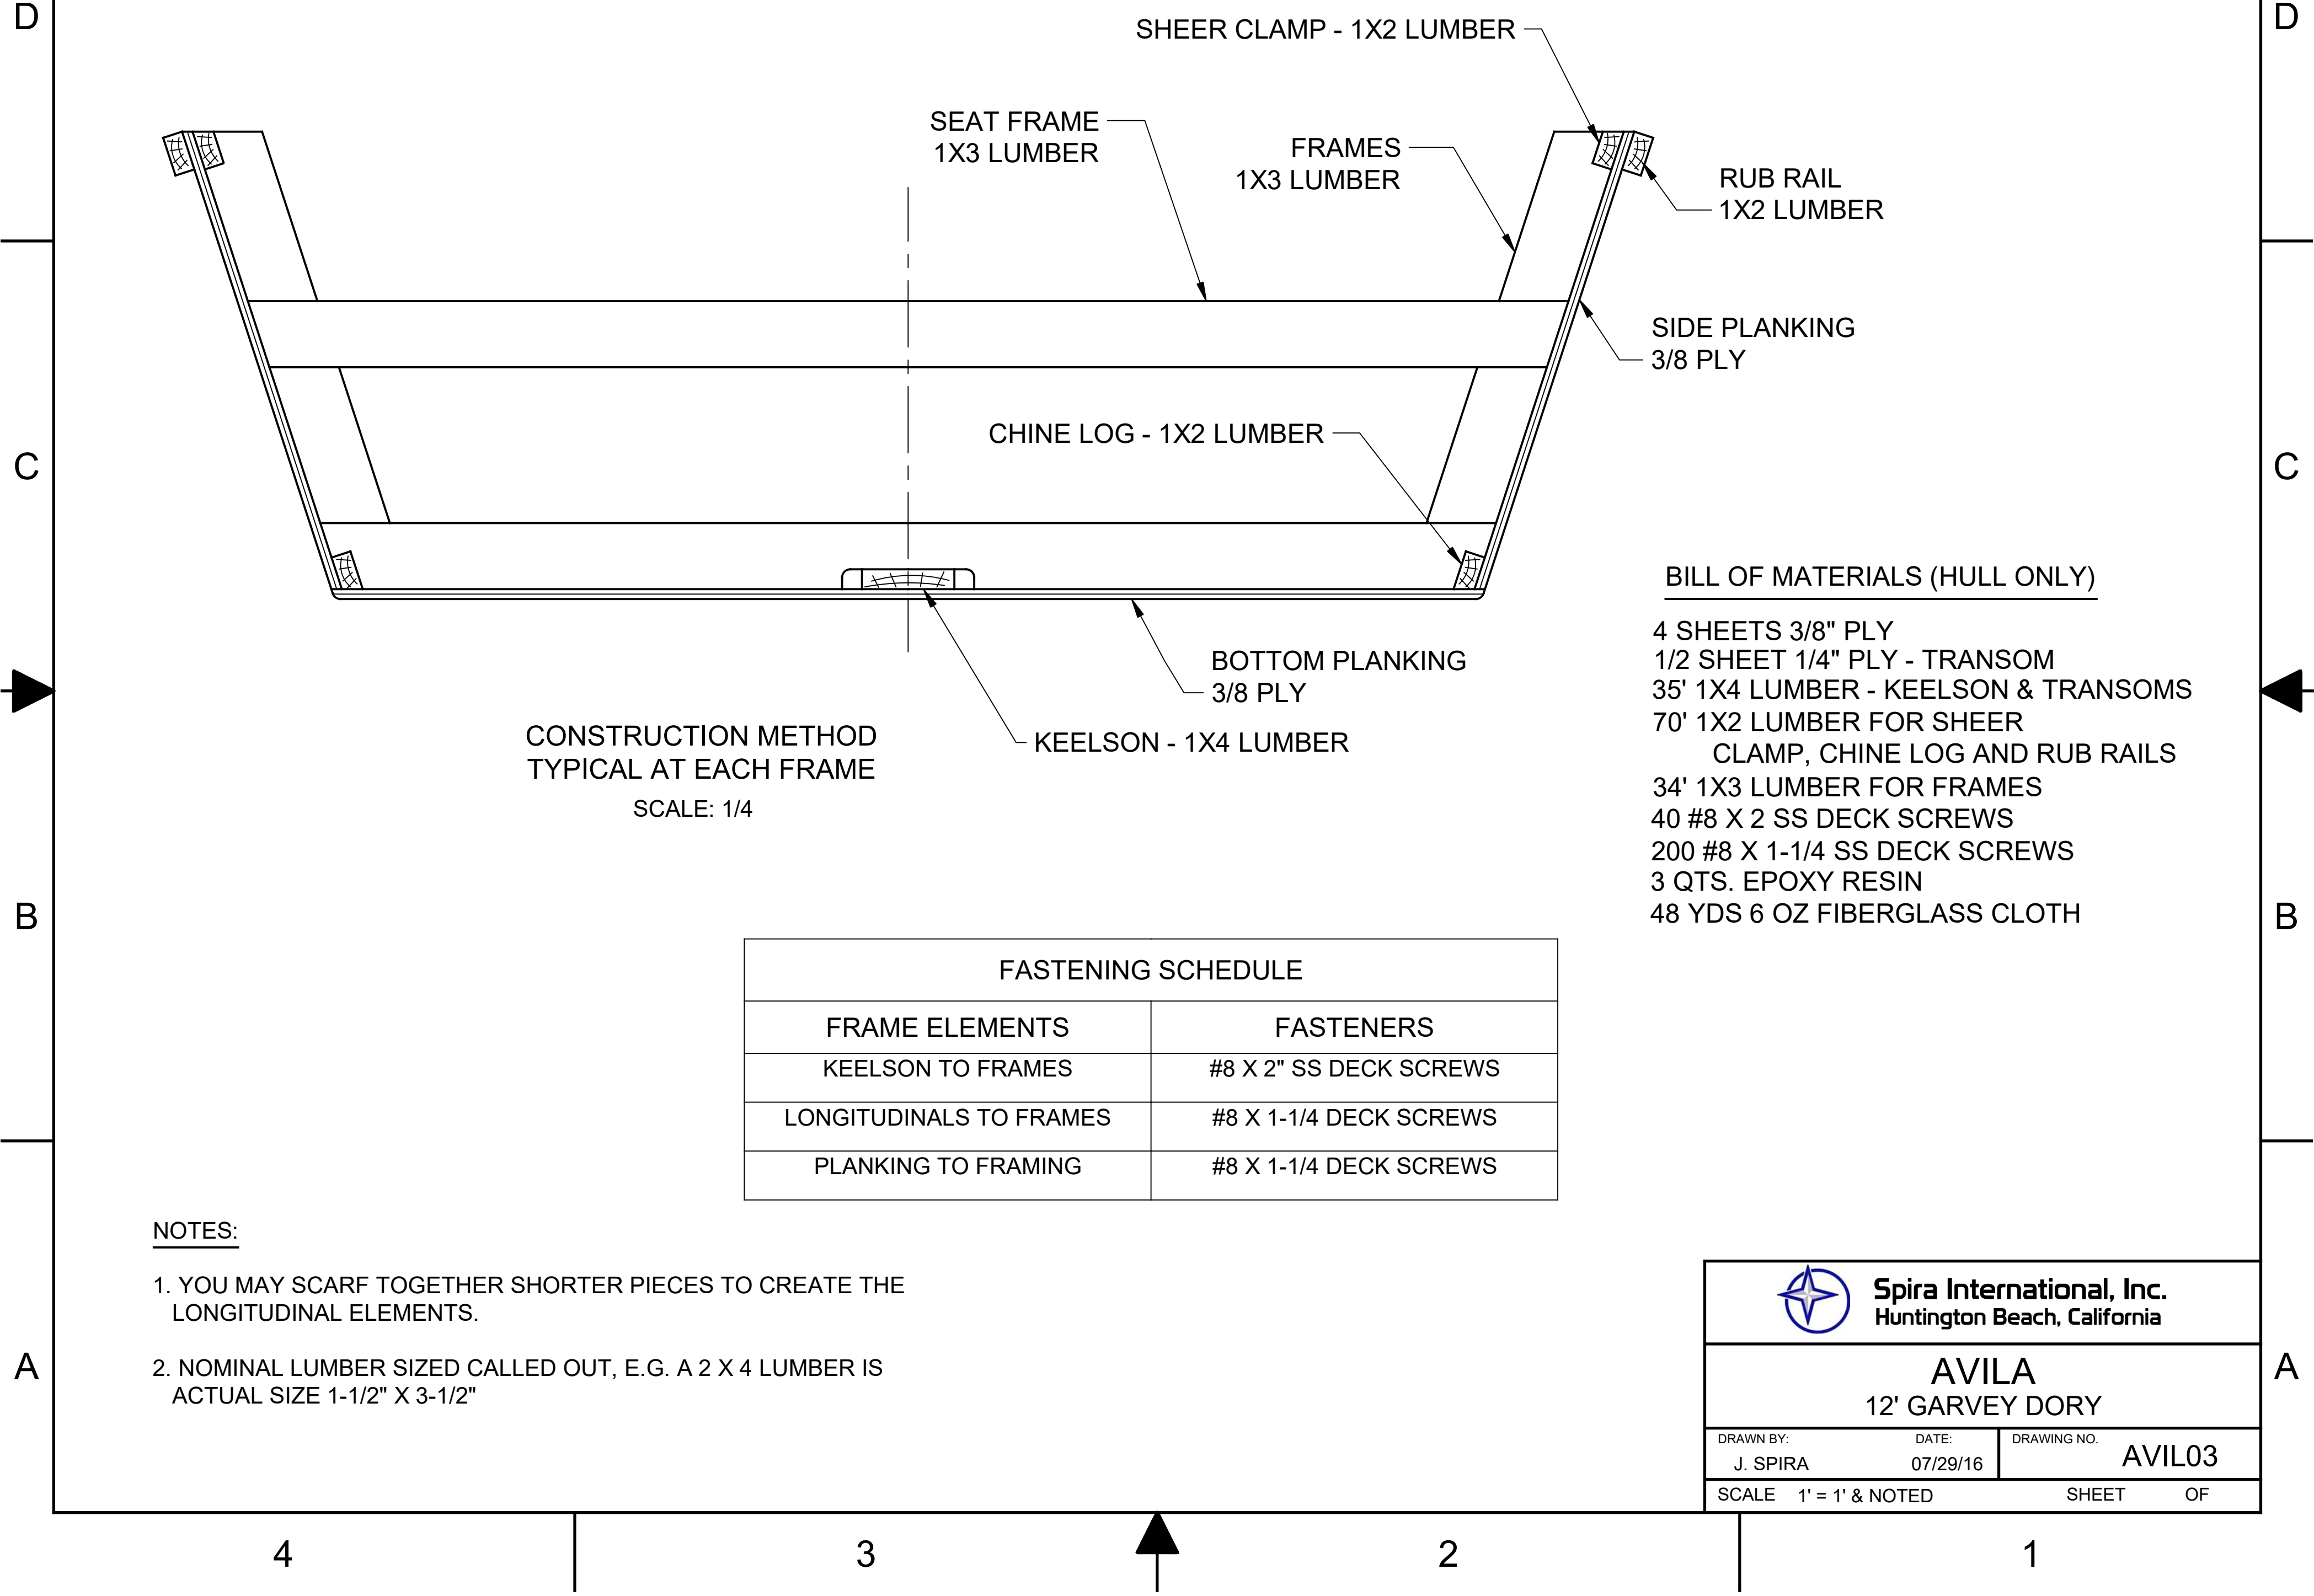

CONSTRUCTION METHOD
TYPICAL AT EACH FRAME
SCALE: 1/4

BILL OF MATERIALS (HULL ONLY)

- 4 SHEETS 3/8" PLY
- 1/2 SHEET 1/4" PLY - TRANSOM
- 35' 1X4 LUMBER - KEELSON & TRANSOMS
- 70' 1X2 LUMBER FOR SHEER CLAMP, CHINE LOG AND RUB RAILS
- 34' 1X3 LUMBER FOR FRAMES
- 40 #8 X 2 SS DECK SCREWS
- 200 #8 X 1-1/4 SS DECK SCREWS
- 3 QTS. EPOXY RESIN
- 48 YDS 6 OZ FIBERGLASS CLOTH

FASTENING SCHEDULE	
FRAME ELEMENTS	FASTENERS
KEELSON TO FRAMES	#8 X 2" SS DECK SCREWS
LONGITUDINALS TO FRAMES	#8 X 1-1/4 DECK SCREWS
PLANKING TO FRAMING	#8 X 1-1/4 DECK SCREWS

NOTES:

- 1. YOU MAY SCARF TOGETHER SHORTER PIECES TO CREATE THE LONGITUDINAL ELEMENTS.
- 2. NOMINAL LUMBER SIZED CALLED OUT, E.G. A 2 X 4 LUMBER IS ACTUAL SIZE 1-1/2" X 3-1/2"



Spira International, Inc.
Huntington Beach, California

AVILA

12' GARVEY DORY

DRAWN BY:
J. SPIRA

DATE:
07/29/16

DRAWING NO.
AVIL03

SCALE 1' = 1' & NOTED

SHEET OF