


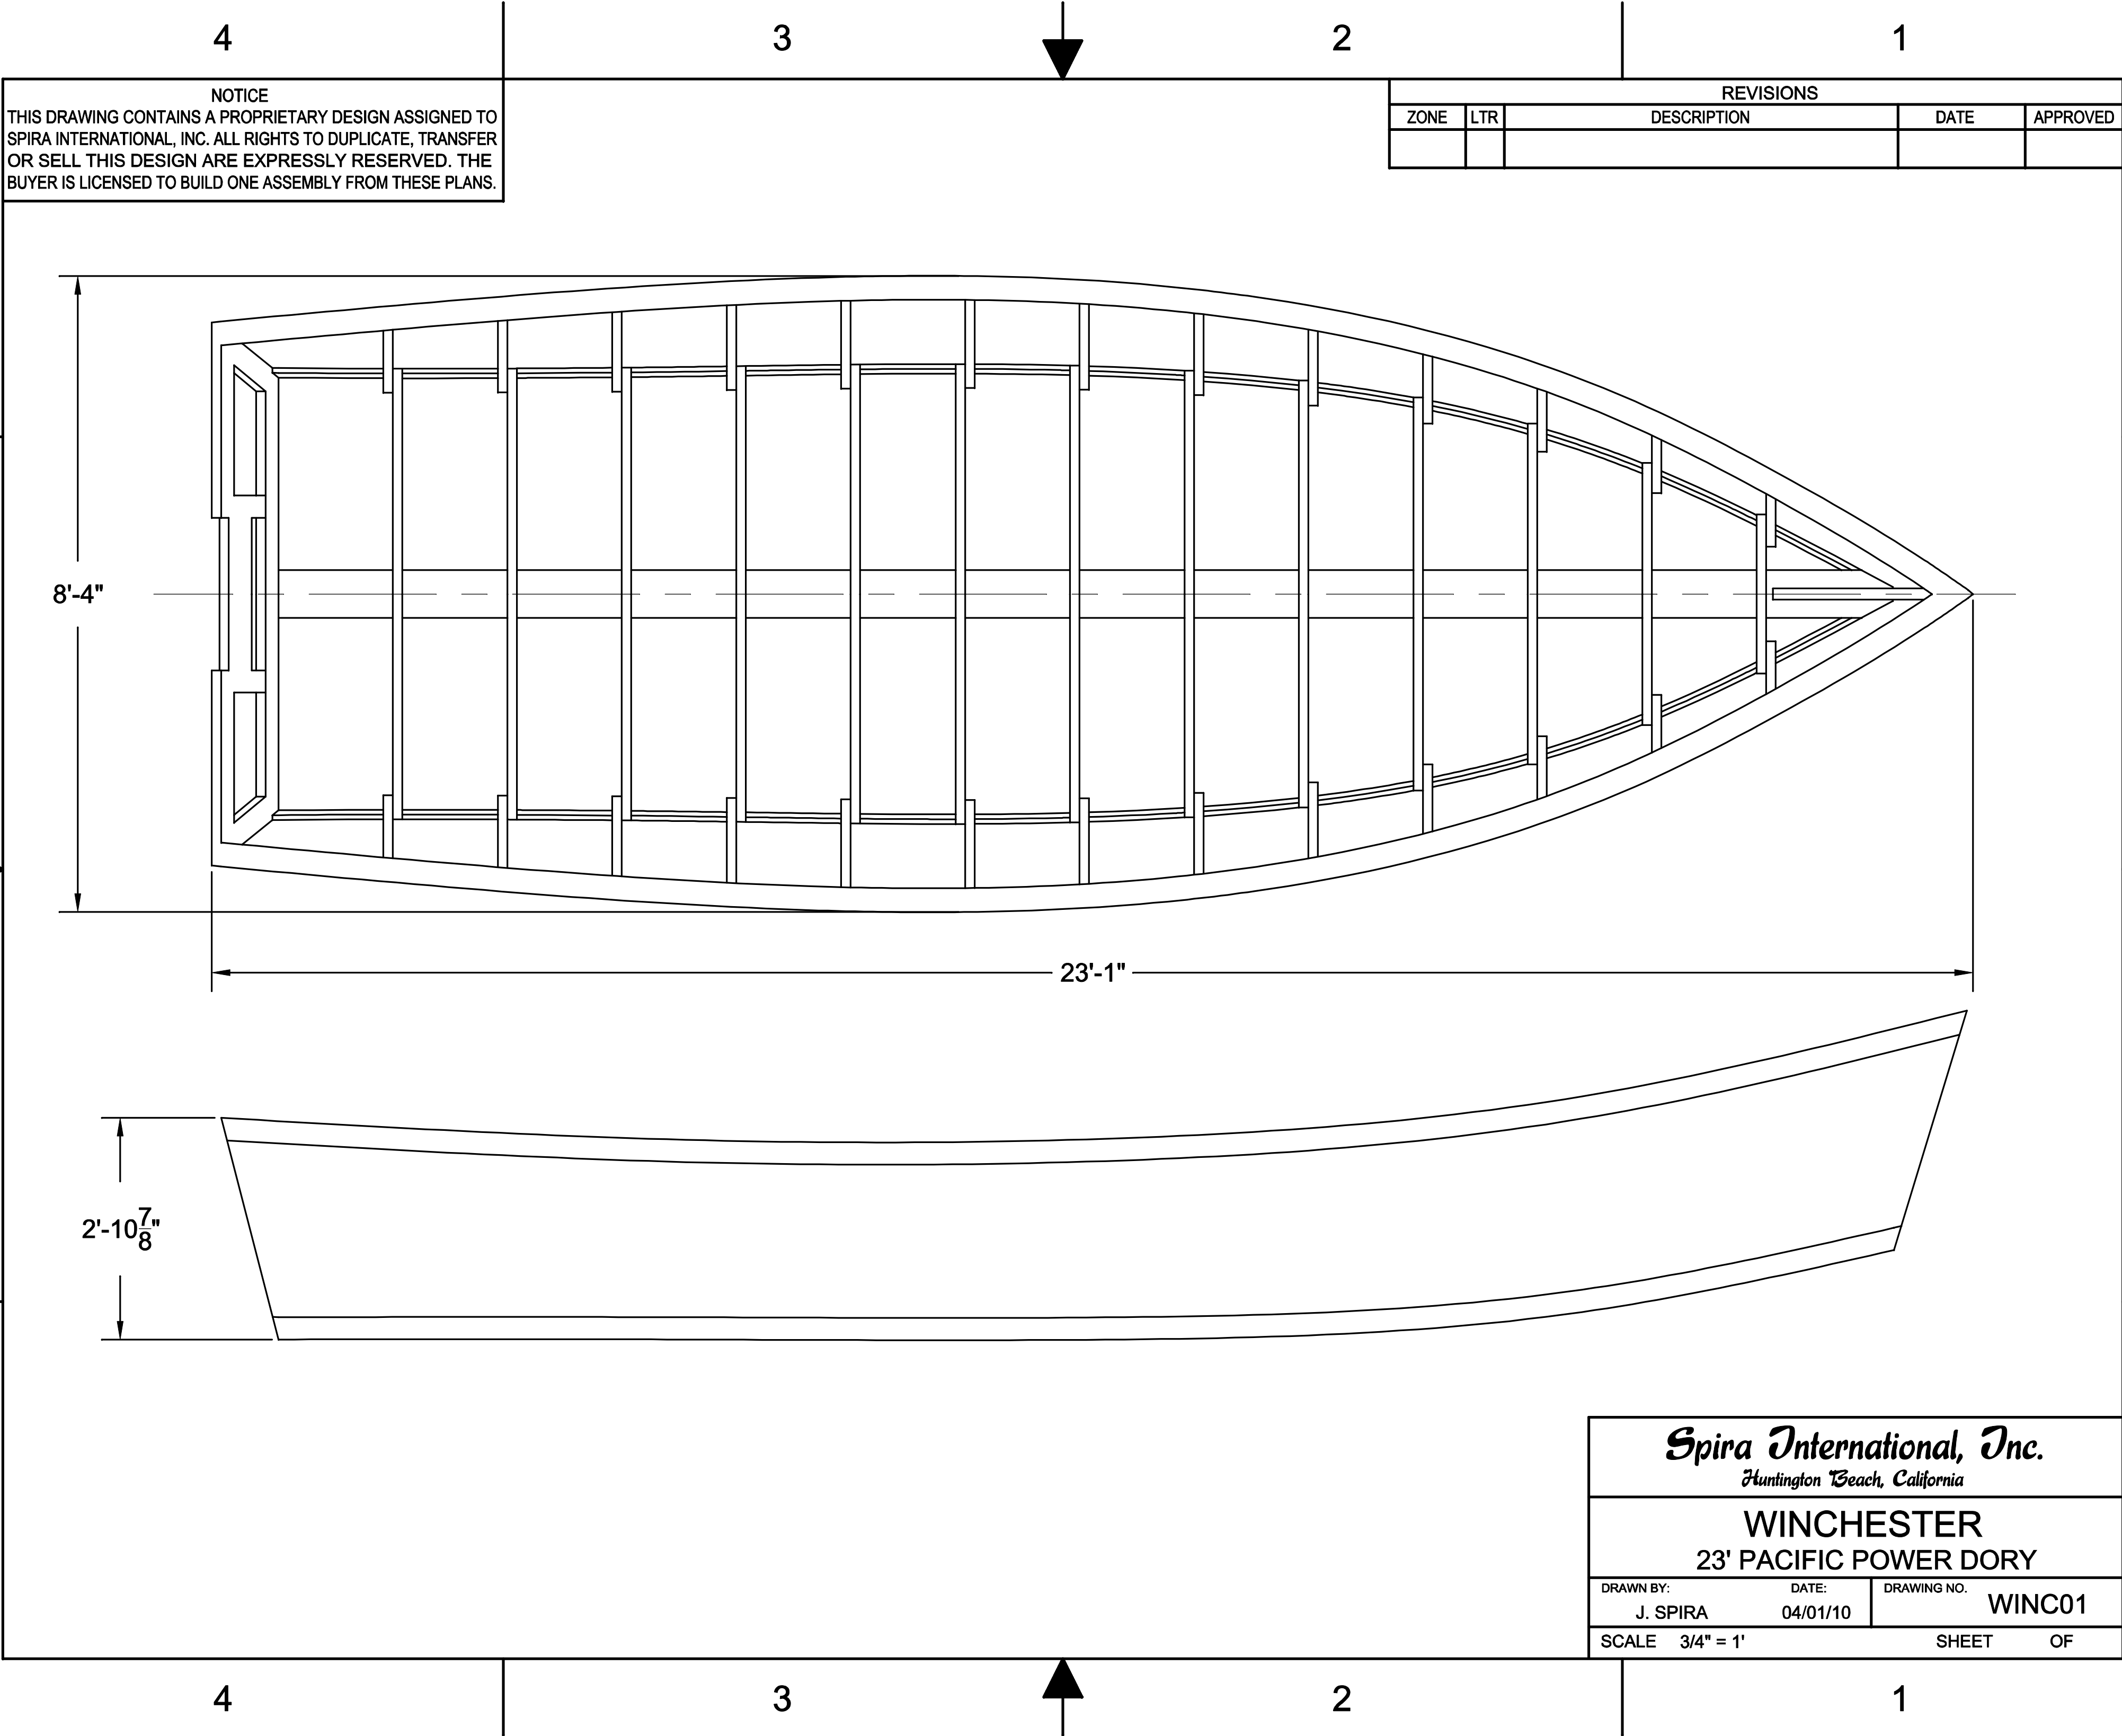

4 3 2 1

NOTICE
THIS DRAWING CONTAINS A PROPRIETARY DESIGN ASSIGNED TO SPIRA INTERNATIONAL, INC. ALL RIGHTS TO DUPLICATE, TRANSFER OR SELL THIS DESIGN ARE EXPRESSLY RESERVED. THE BUYER IS LICENSED TO BUILD ONE ASSEMBLY FROM THESE PLANS.


REVISIONS				
ZONE	LTR	DESCRIPTION	DATE	APPROVED
	A	CORRECTED BOM - BOTTOM PLY	03/31/10	JJS

BILL OF MATERIALS

FRAMES: 160 FT 2X4S
KEELSON & TRANSOM: 30 FT 2X8S
S/C & C/L: 82' 1X4S
SIDES: 6 SHTS 5/8" PLY
BOTTOM: 5 SHTS 3/4" PLY
GLASS: 40 YDS - 6 OZ CLOTH
EPOXY: 5 GAL
FRAMES: 180 - #10 X 3" SCREWS
PLANKING: 1200 - #8 X 1-1/2" SCREWS

OPTIONAL

DECKING: 550 FT 1X2S
RAIL CAP: 60' 1X8

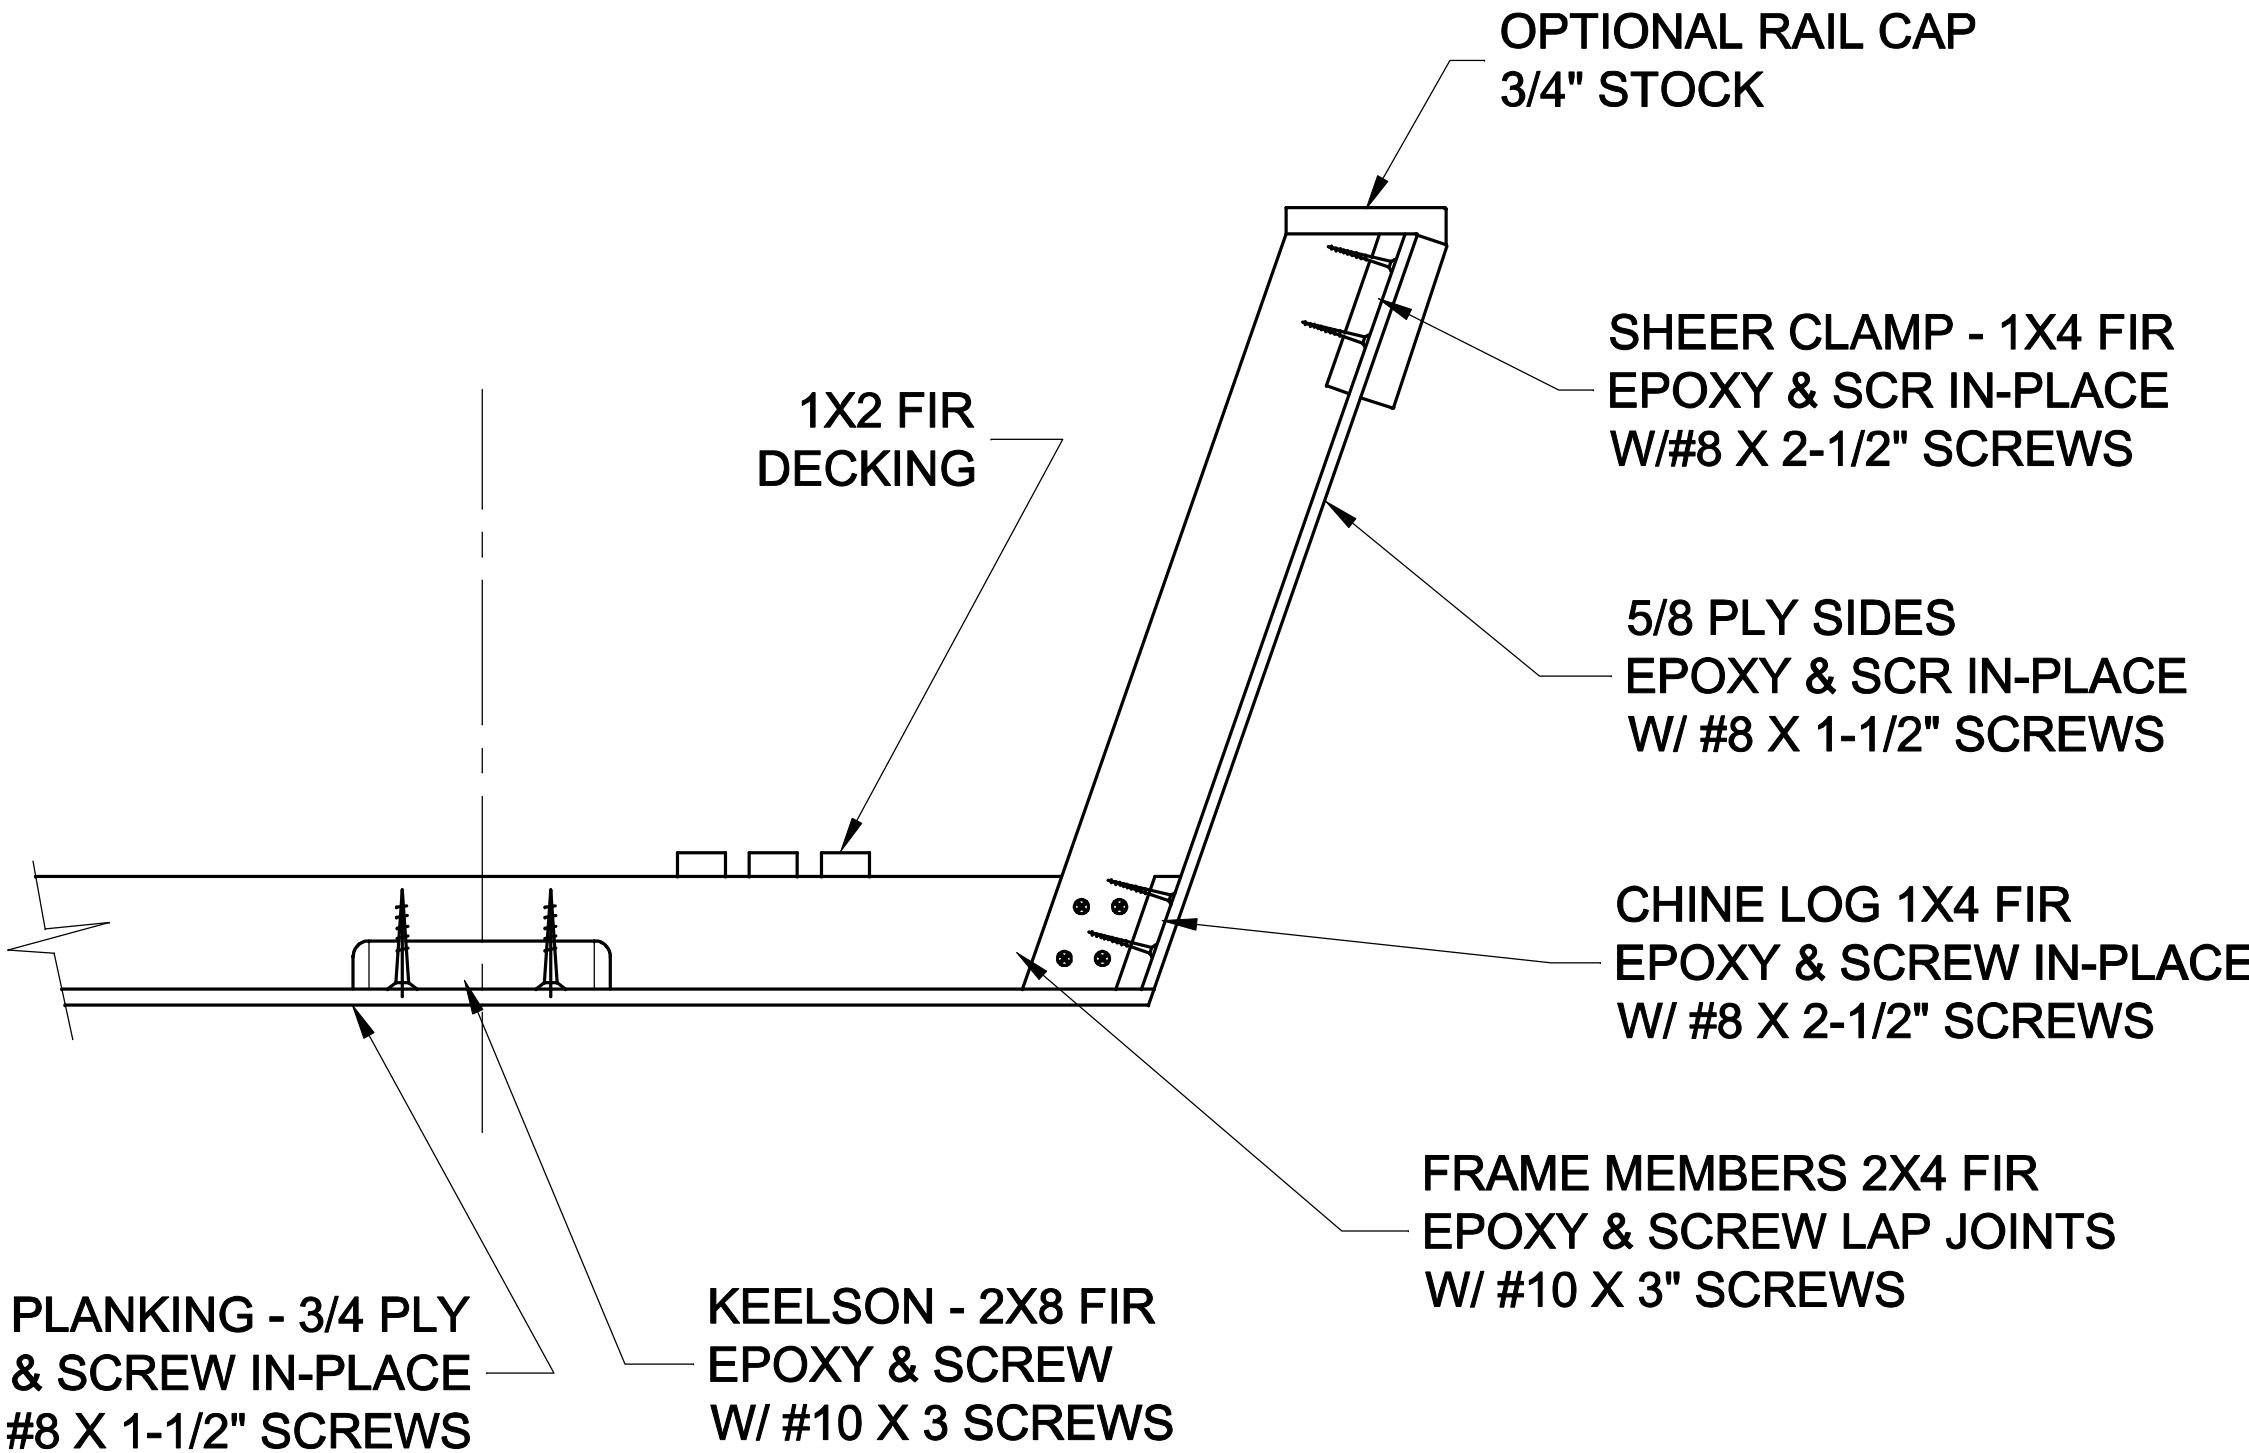

TYPICAL CONSTRUCTION METHOD
ALL FRAME STATIONS
SCALE 2" = 1'

Spira International, Inc.
Huntington Beach, California

WINCHESTER
23' PACIFIC POWER DORY

DRAWN BY: J. SPIRA	DATE: 04/01/10	DRAWING NO. WINC02
SCALE 1" = 1' & NOTED		SHEET OF