

4

3


2

1

NOTICE
THIS DRAWING CONTAINS A PROPRIETARY DESIGN ASSIGNED TO SPIRA INTERNATIONAL, INC. ALL RIGHTS TO DUPLICATE, TRANSFER OR USE ARE EXPRESSLY RESERVED BY SPIRA INTERNATIONAL. THE BUYER IS LICENSED TO BUILD ONE ASSEMBLY FROM THESE PLANS.

REVISIONS				
ZONE	LTR	DESCRIPTION	DATE	APPROVED

SPECIFICATIONS	
LENGTH O'ALL	26' 8"
LENGTH, HULL	23' 11"
LENGTH W/L	21' 11"
MAX BEAM	7' 6"
SAIL AREA	186 SQ. FT
FREEBOARD	1' 8"
EMPTY WEIGHT	1480 LBS

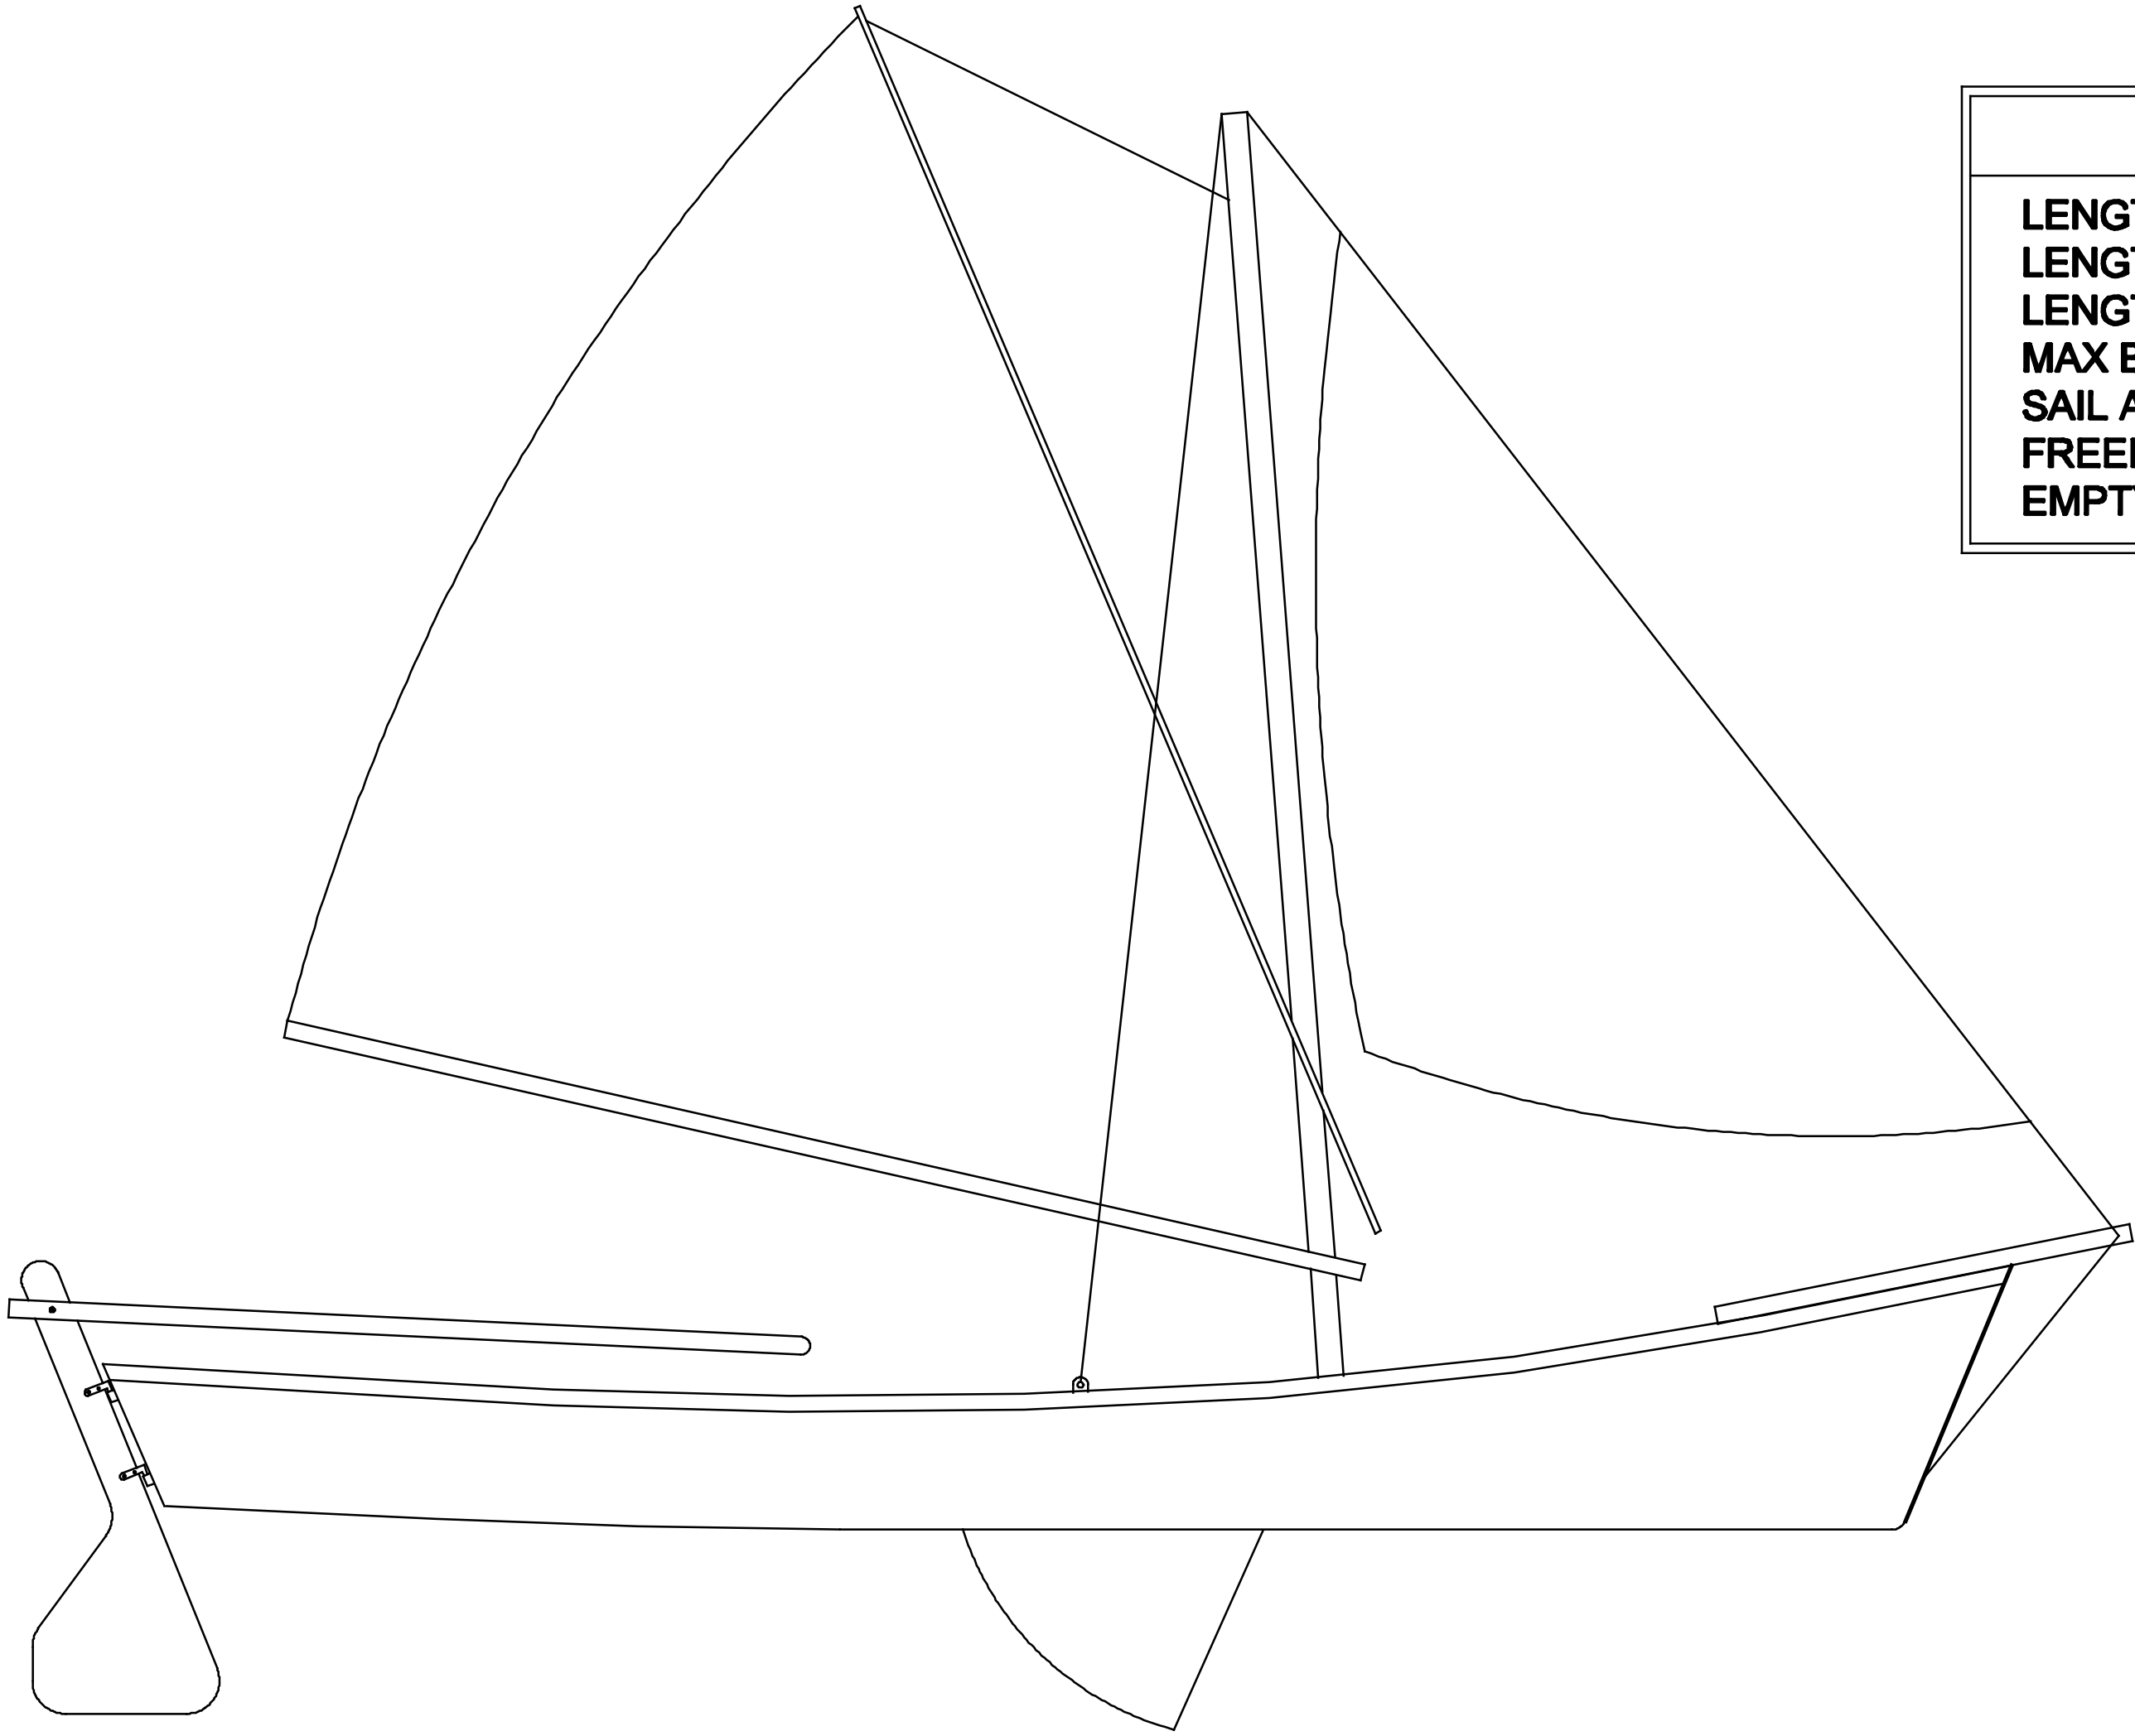

Spira International, Inc. <i>Huntington Beach, California</i>		
ANDROS 24' SAILING SHARPIE		
DRAWN BY: J. SPIRA	DATE: 06/04/10	DRAWING NO. ANDR01
SCALE 1/2" = 1'		SHEET OF

4

3

2

1

1

REVISIONS

ZONE	LTR	DESCRIPTION	DATE	APPROVED



10 SHEETS 1/2" PLY
4 SHEETS 3/8" PLY
115' 2X4 LUMBER FOR FRAMES
180' 1X4 LUMBER FOR COCKPIT AND DECK BEAMS
144' 1X2 CLEAR LUMBER FOR SHEER
CLAMP, CHINE LOG AND RUB RAILS
80' 1X2 LUMBER FOR COCKPIT DECKING
22" 2X8 LUMBER FOR KEELSON
10' 2X6 LUMBER FOR TRANSOM AND STEM
100 #10 X 3 SS OR BRONZE FLAT HEAD SCREWS
500 #8 X 2-1/2 SS OR BRONZE FLAT HEAD SCREWS
2000 #6 X 1-1/2 SS SCREWS OR BRONZE NAILS
3 GAL EPOXY RESIN
35 YDS 6 OZ FIBERGLASS CLOTH

1. YOU MAY SCARF TOGETHER SHORTER PIECES TO CREATE THE LONGITUDINAL ELEMENTS.
2. NOMINAL LUMBER SIZED CALLED OUT, E.G. A 2 X 4 LUMBER IS ACTUAL SIZE 1-1/2" X 3-1/2"

TYPICAL AT EACH FRAME
SCALE: 1/5

ANDROS

'SAILING SHARPS'

DRAWN BY: J. SPIRA	DATE: 06/04/10	DRAWING NO. ANDR02
SCALE 1/2" = 1'		SHEET OF

1