

4

3

2

1

NOTICE
THIS DRAWING CONTAINS A PROPRIETARY DESIGN ASSIGNED TO SPIRA INTERNATIONAL, INC. ALL RIGHTS TO DUPLICATE, TRANSFER OR USE ARE EXPRESSLY RESERVED BY SPIRA INTERNATIONAL. THE BUYER IS LICENSED TO BUILD ONE ASSEMBLY FROM THESE PLANS.

REVISIONS				
ZONE	LTR	DESCRIPTION	DATE	APPROVED
	A	UPDATED TO NEW FORMAT	8/26/08	JJS

D

D

C



C

B

B

A

A

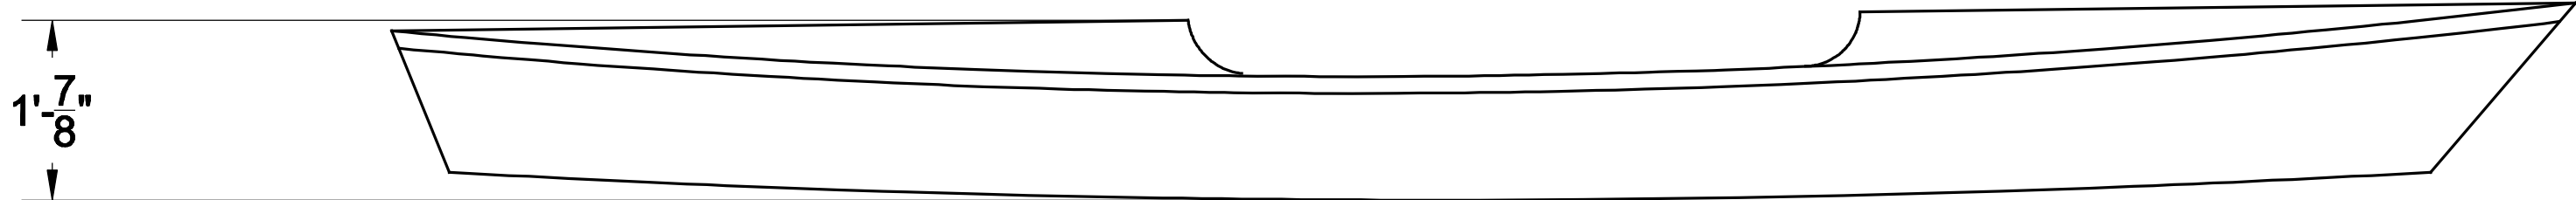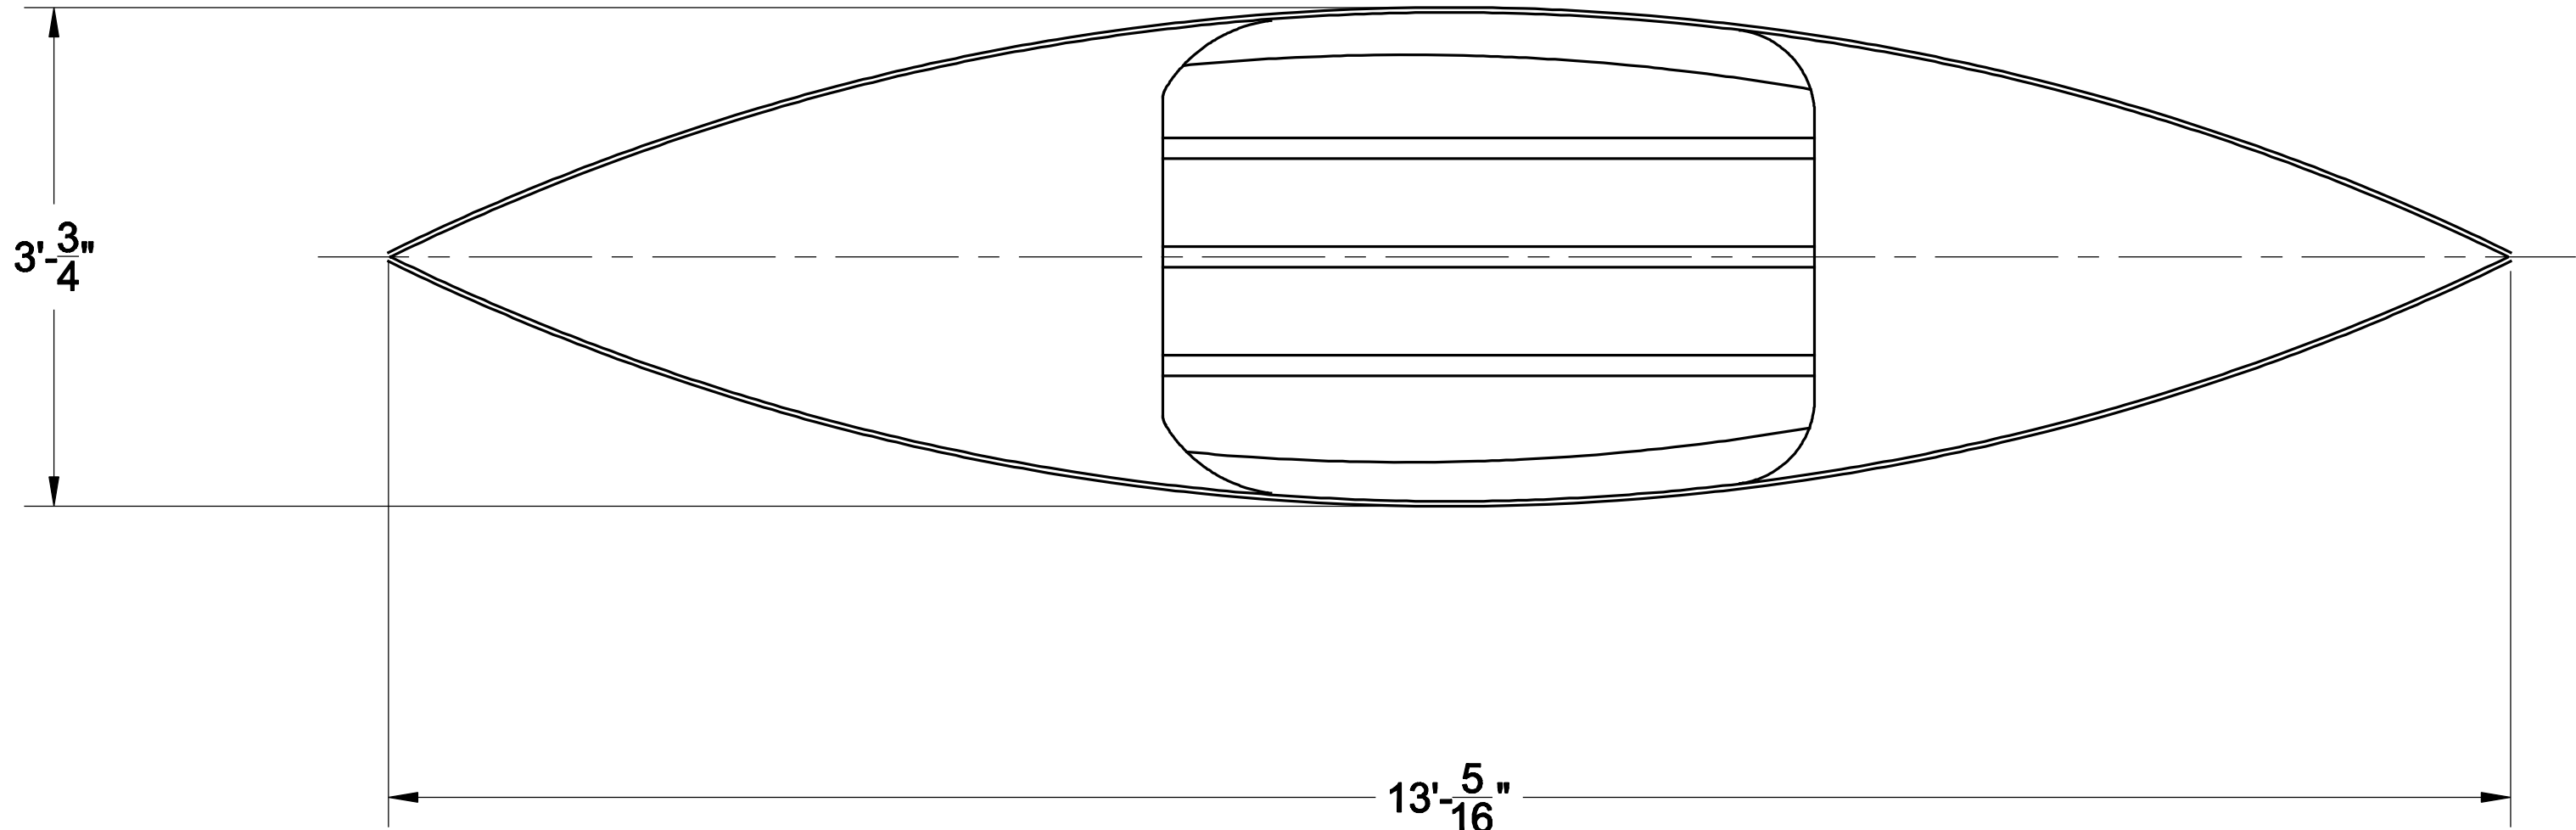

Spira International, Inc.
Huntington Beach, California

ARROW POINT
13' STITCH & GLUE KAYAK

DRAWN BY:
JJS

DATE:
03/28/04


DRAWING NO.
ARRO 01

SCALE 1" = 1'


SHEET OF

NOTICE
THIS DRAWING CONTAINS A PROPRIETARY DESIGN ASSIGNED TO SPIRA INTERNATIONAL, INC. ALL RIGHTS TO DUPLICATE, TRANSFER OR USE ARE EXPRESSLY RESERVED BY SPIRA INTERNATIONAL. THE BUYER IS LICENSED TO BUILD ONE ASSEMBLY FROM THESE PLANS.


REVISIONS				
ZONE	LTR	DESCRIPTION	DATE	APPROVED
	A	ADDED BOM MOVED VIEWS	07/07/12	JJS

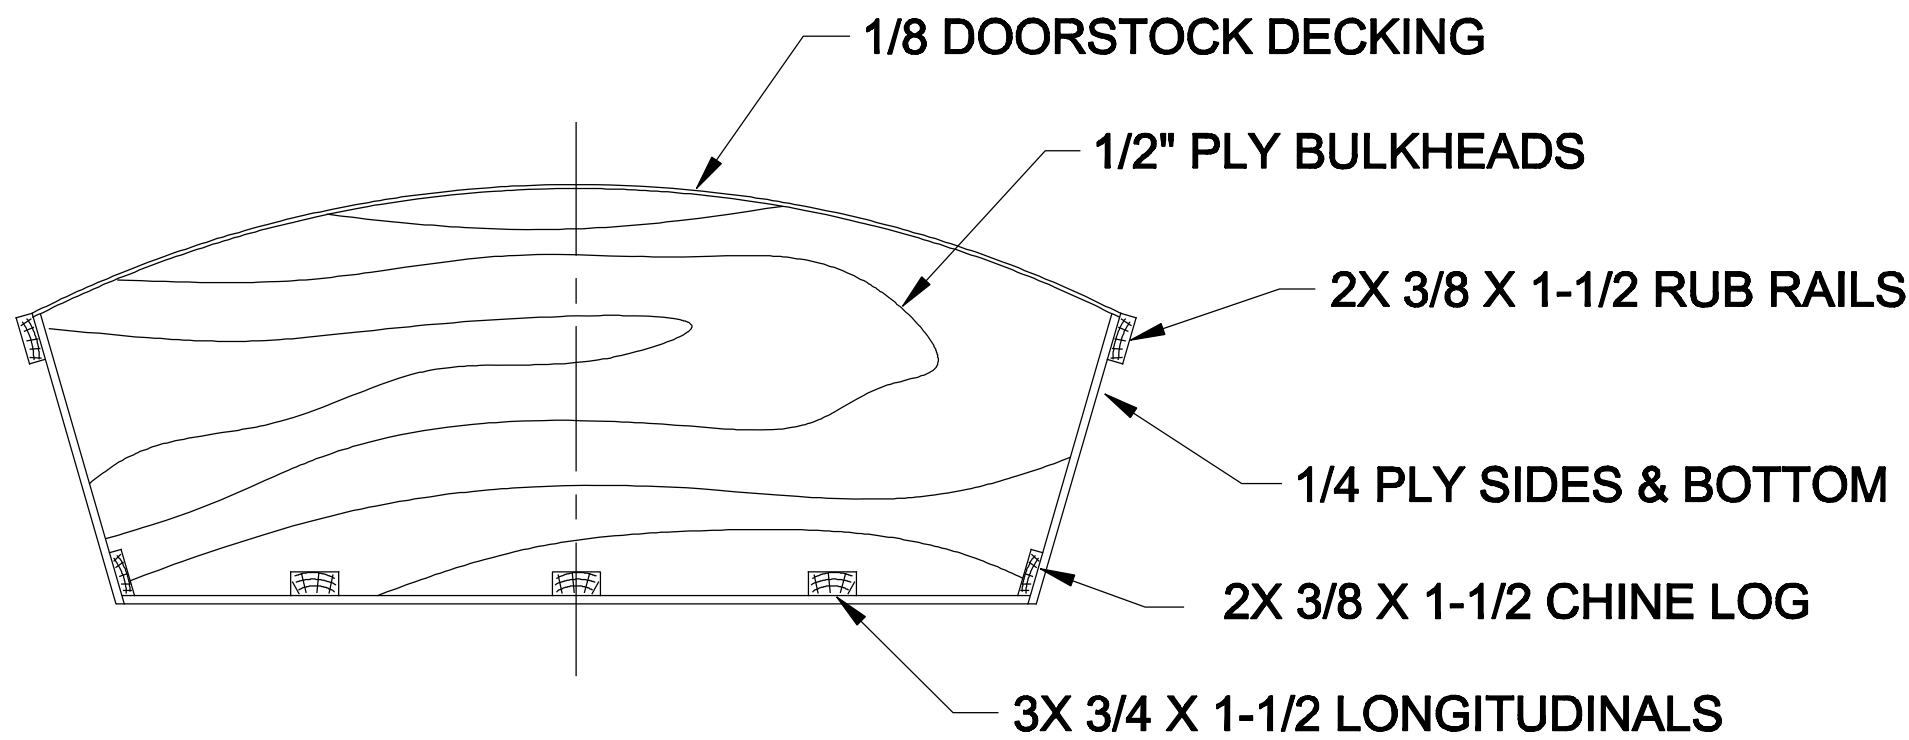

CONSTRUCTION DETAILS

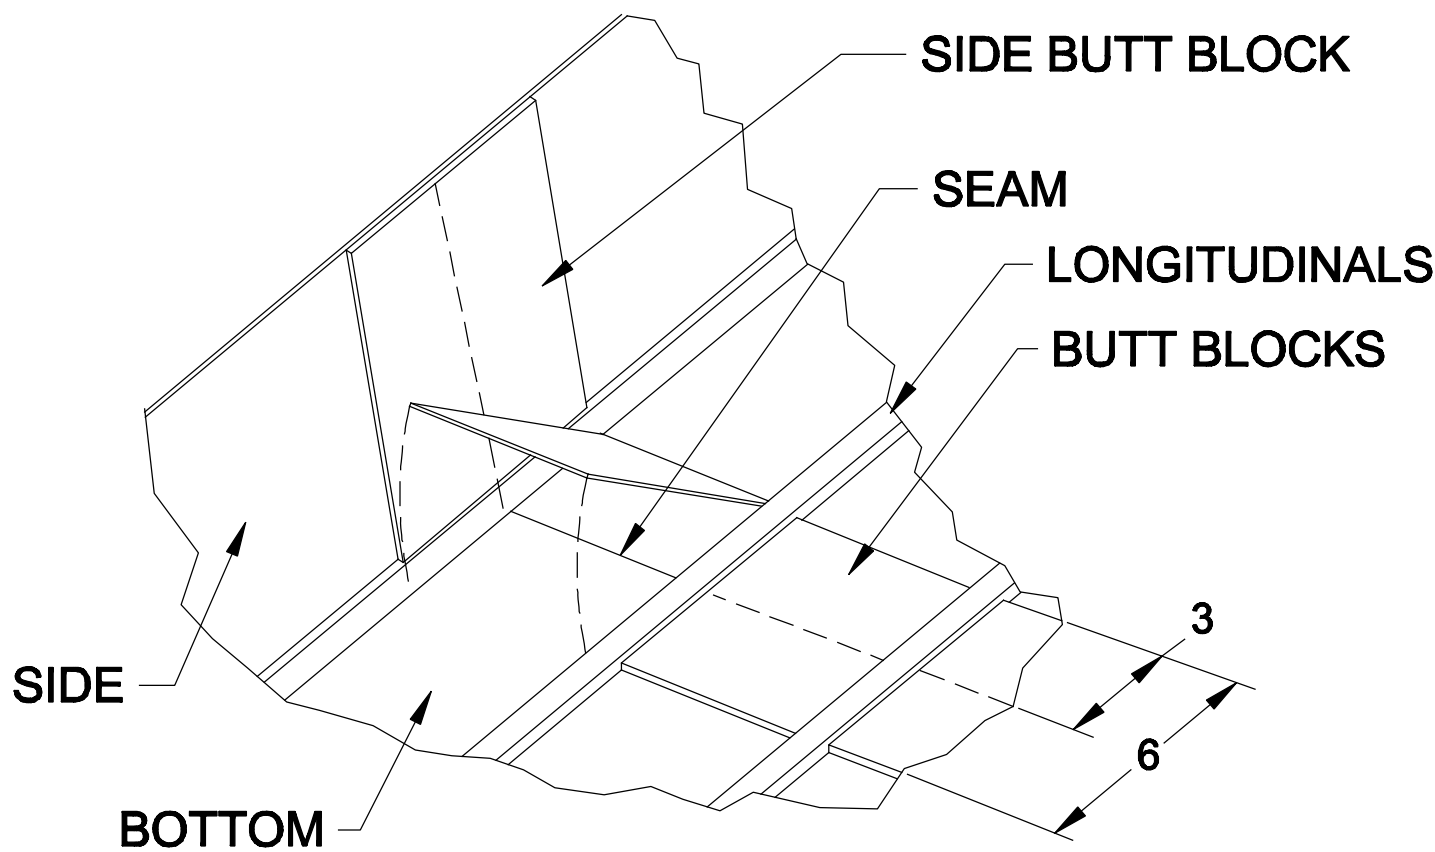


BUTT BLOCK PLACEMENT
(VIEW FROM INSIDE OF BOAT)

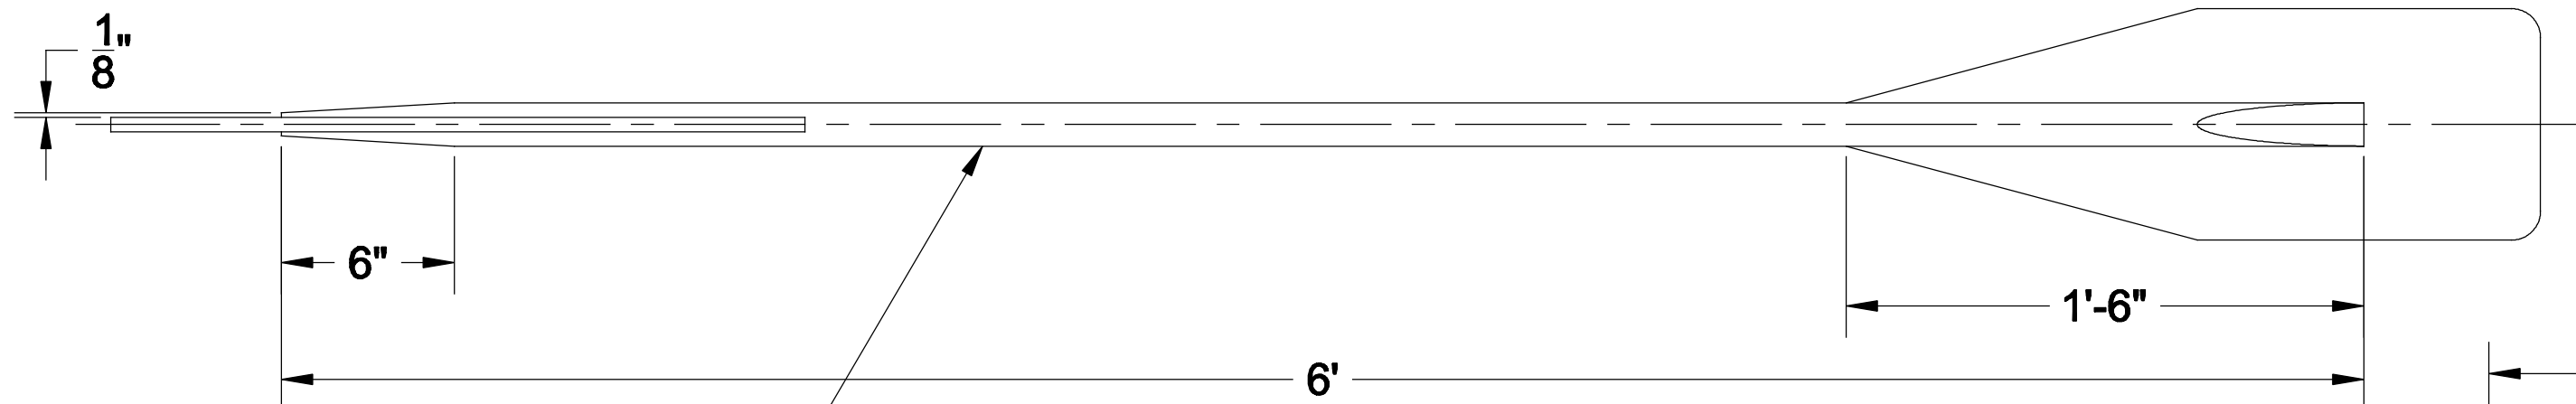

CLOSET POLE
1-3/8 DIA (APPROX)

PADDLE ASSEMBLY

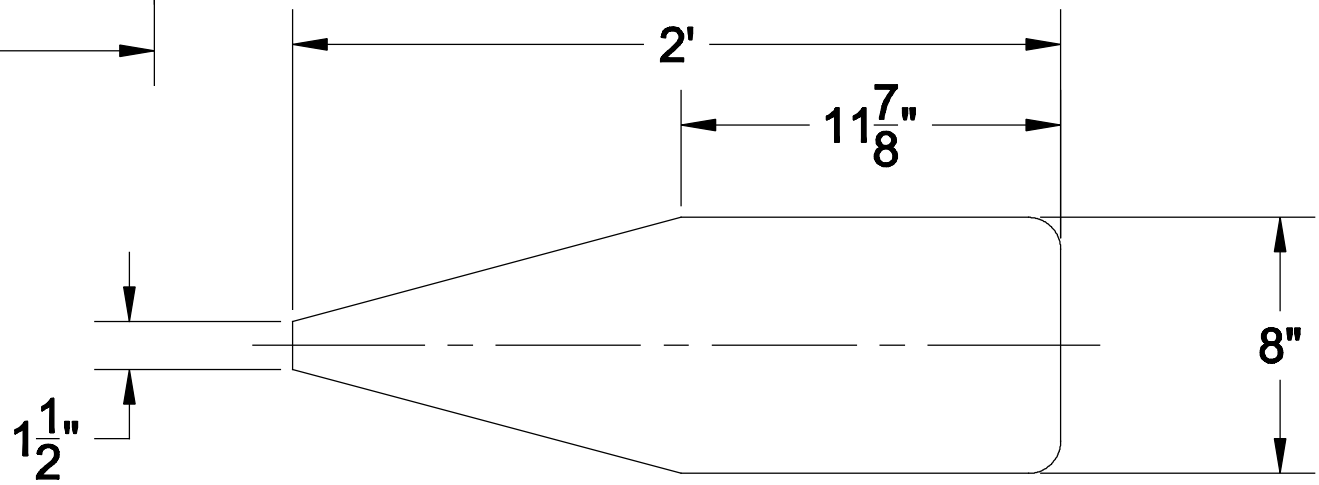

PADDLE BLADE - 1/2 PLY - 2 REQ'D

BILL OF MATERIALS

SHEETS - 1/4" PLYWOOD (4' X 8')
1/2 SHEET - 1/2" PLYWOOD (4' X 4')
1/2 SHEET - 1/8" DOORSTOCK (4' X 4')
24 FT. - 1 X 2 LUMBER
64 FT. - /8" X 1-1/2" CLEAR MOLDING
3 QTS. - EPOXY RESIN
2 QTS. - EPOXY THICKENING AGENT
25 YDS. - 3" FIBERGLASS TAPE

NOTES:

1. YOU MAY SCARF TOGETHER SHORTER PIECES TO CREATE THE LONGITUDINAL ELEMENTS.
2. NOMINAL LUMBER SIZED CALLED OUT, E.G. A 2 X 4 LUMBER IS ACTUAL SIZE 1-1/2" X 3-1/2"

Spira International, Inc.
Huntington Beach, California

ARROW POINT
13' STITCH & GLUE KAYAK

DRAWN BY: JJS	DATE: 03/28/04	DRAWING NO. ARRO 02
SCALE 2" = 1' & NOTED	SHEET	OF