

4

3


2

1

NOTICE

THIS DRAWING CONTAINS A PROPRIETARY DESIGN ASSIGNED TO SPIRA INTERNATIONAL, INC. ALL RIGHTS TO DUPLICATE, TRANSFER OR USE ARE EXPRESSLY RESERVED BY SPIRA INTERNATIONAL. THE BUYER IS LICENSED TO BUILD ONE ASSEMBLY FROM THESE PLANS.

REVISIONS				
ZONE	LTR	DESCRIPTION	DATE	APPROVED

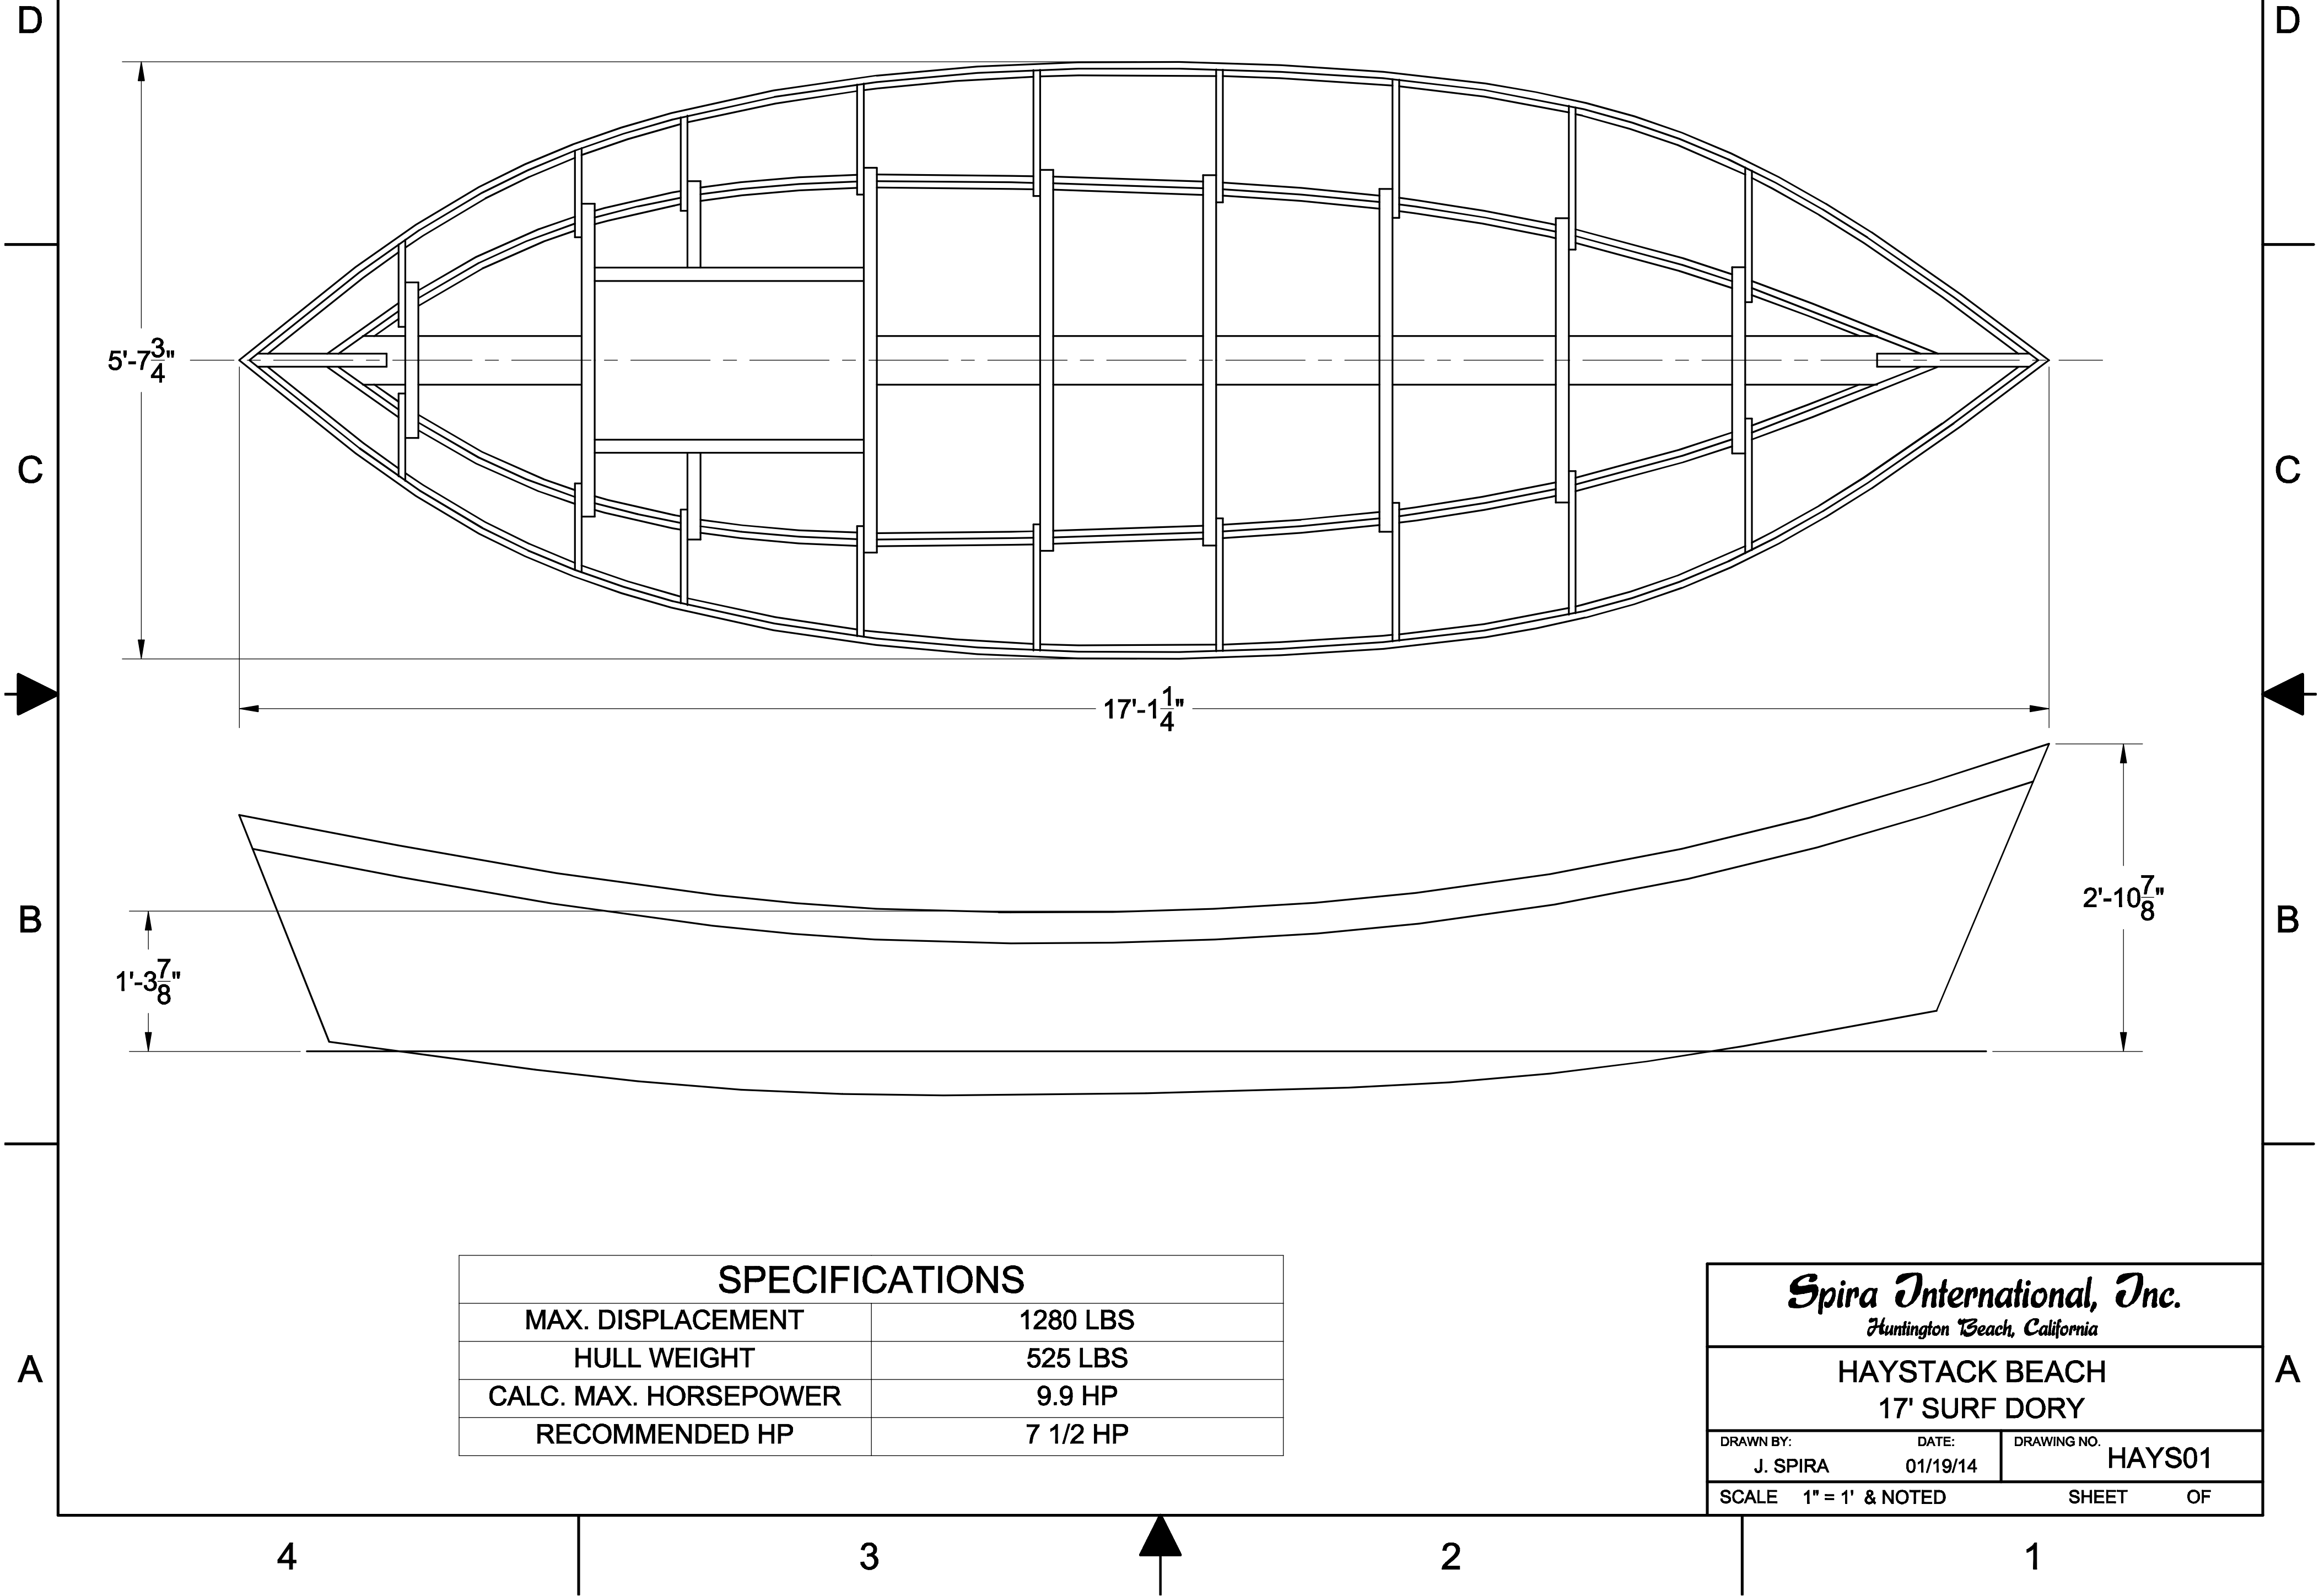

4

3

2

1

NOTICE

THIS DRAWING CONTAINS A PROPRIETARY DESIGN ASSIGNED TO SPIRA INTERNATIONAL, INC. ALL RIGHTS TO DUPLICATE, TRANSFER OR USE ARE EXPRESSLY RESERVED BY SPIRA INTERNATIONAL. THE BUYER IS LICENSED TO BUILD ONE ASSEMBLY FROM THESE PLANS.

REVISIONS				
ZONE	LTR	DESCRIPTION	DATE	APPROVED

BILL OF MATERIALS

4 SHEETS 3/8" PLY
3 SHEETS 1/2" PLY
75' 1X3 LUMBER - FRAMES & RUB RAIL
36' 2X4 LUMBER - FRAMES & MOTOR WELL
80' 1X2 CLEAR LUMBER - SHEER CLAMP
CHINE LOG
24' 2X6 LUMBER FOR KEELSON & STEMS
50 - #10 X 2-1/2 DECK SCREWS
500 - #8 X 1-1/4 DECK SCREWS
100 - #8 X 2 DECK SCREWS
1 GAL EPOXY RESIN
12 YDS 6 OZ FIBERGLASS CLOTH

FASTENING SCHEDULE

KEELSON TO FRAMES: #10 X 2-1/2 DECK SCREWS
FRAMES TO FRAMES: #8 X 1-1/4 DECK SCREWS
LONGITUDINALS: #8 X 2 DECK SCREWS
PLY TO FRAMES: #8 X 1-1/4 DECK SCREWS

NOTES:

1. YOU MAY SCARF TOGETHER SHORTER PIECES TO CREATE THE LONGITUDINAL ELEMENTS.
2. NOMINAL LUMBER SIZED CALLED OUT, E.G. A 1 X 3 LUMBER IS ACTUAL SIZE 3/4" X 2-1/2"

Spira International, Inc. <i>Huntington Beach, California</i>		
HAYSTACK BEACH 17' SURF DORY		
DRAWN BY: J. SPIRA	DATE: 01/19/14	DRAWING NO. HAYS02
SCALE 2" = 1'		SHEET OF