

4

3

2

1

NOTICE
THIS DRAWING CONTAINS A PROPRIETARY DESIGN ASSIGNED TO SPIRA INTERNATIONAL, INC. ALL RIGHTS TO DUPLICATE, TRANSFER OR USE ARE EXPRESSLY RESERVED BY SPIRA INTERNATIONAL. THE BUYER IS LICENSED TO BUILD ONE ASSEMBLY FROM THESE PLANS.

REVISIONS				
ZONE	LTR	DESCRIPTION	DATE	APPROVED

D

D

C


C

B

B

A

A

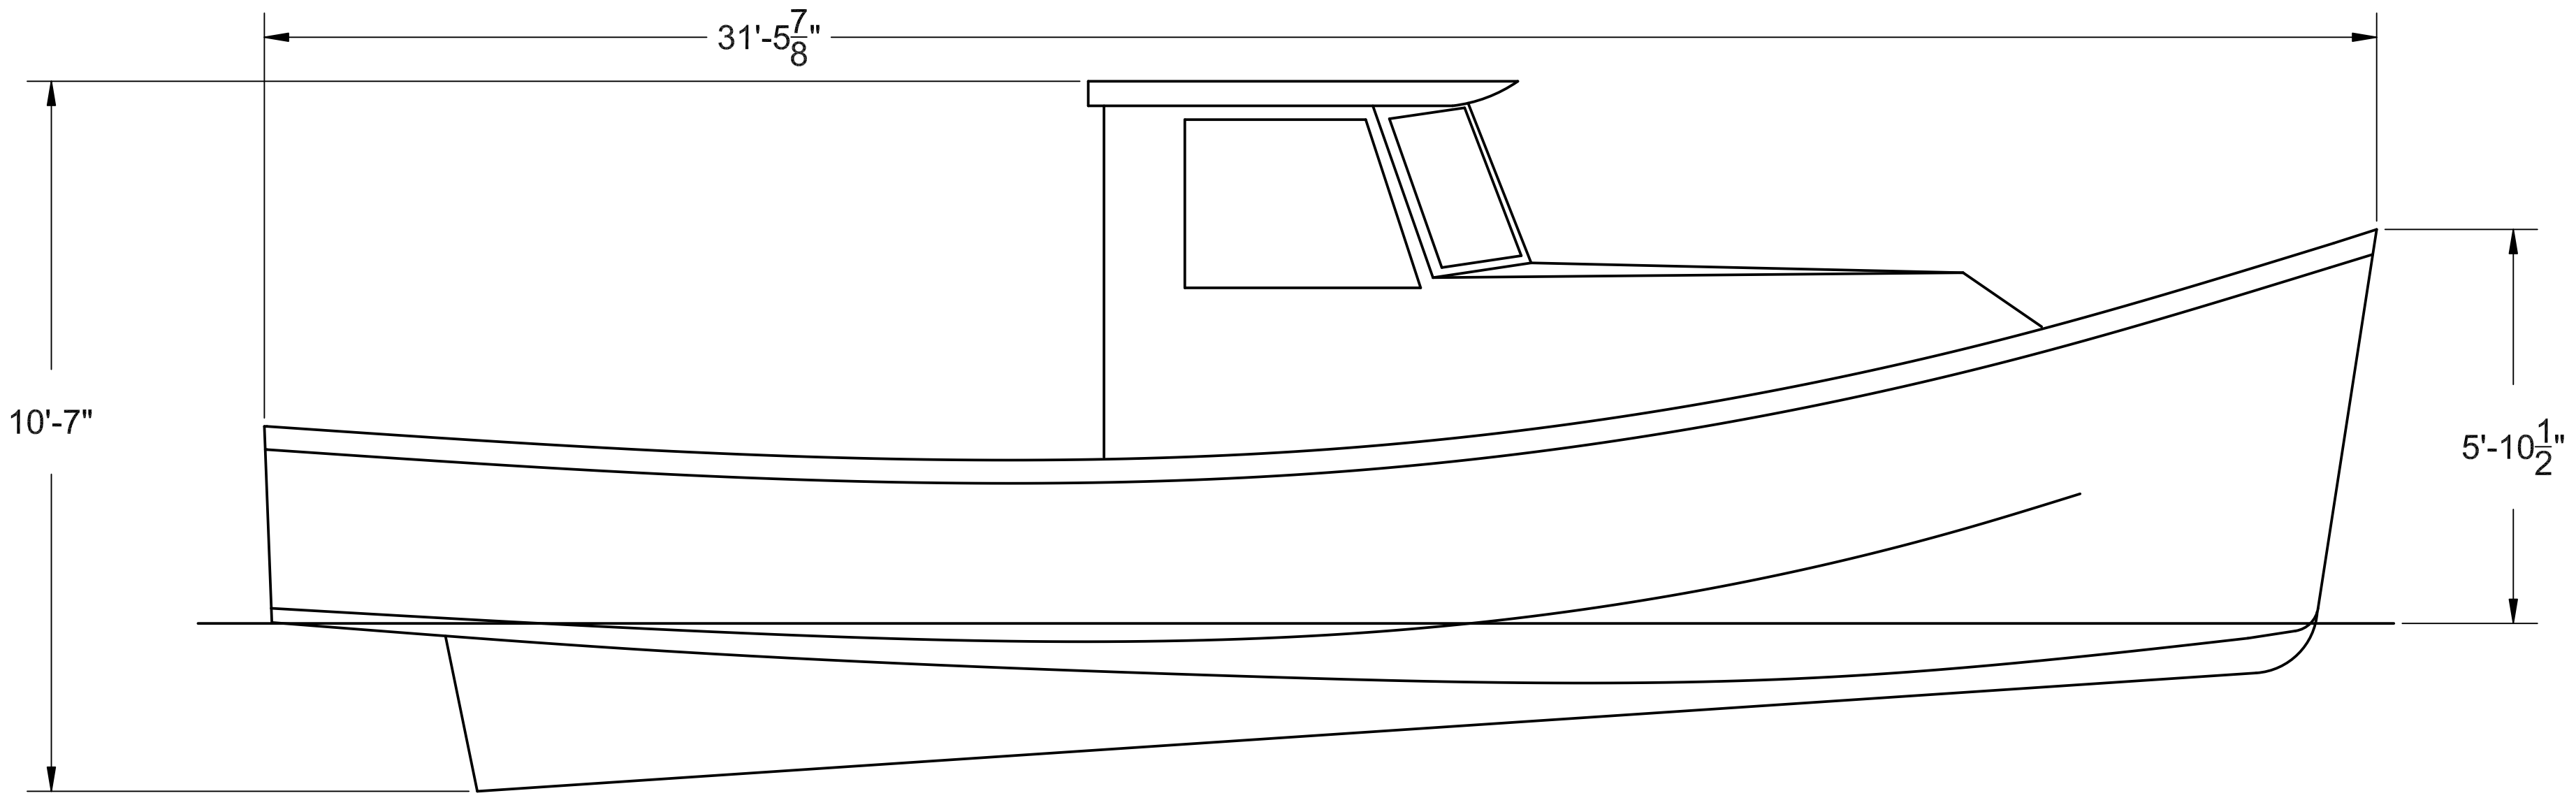

Spira International, Inc.
Huntington Beach, California

HILO
31' HAWAIIAN SAMPA

DRAWN BY:
J. SPIRA

DATE:
04/19/09

DRAWING NO.
HILO01

SCALE 1/2" = 1' & NOTED

SHEET OF

4

3

2

1

NOTICE

THIS DRAWING CONTAINS A PROPRIETARY DESIGN ASSIGNED TO SPIRA INTERNATIONAL, INC. ALL RIGHTS TO DUPLICATE, TRANSFER OR USE ARE EXPRESSLY RESERVED BY SPIRA INTERNATIONAL. THE BUYER IS LICENSED TO BUILD ONE ASSEMBLY FROM THESE PLANS.

REVISIONS

ZONE	LTR	DESCRIPTION	DATE	APPROVED

D

D

C

C

B

B

A

A

SHEAR CLAMP
3/4" X 3-1/2" FIR OR MAHOGANY

FRAME RISERS
1 1/2" X 3 1/2" FIR OR MAHOGANY

#10 X 2 1/2 SS DECK SCREWS

DECK - 5/8 PLY

DECK BEAMS
1 1/2 X 3 1/2 FIR

DECK RISERS
3/4 X 1 1/2 FIR

RAIL CAP
3/4 FIR OR MAHOGANY

RUB RAIL
3/4 X 1 1/2 FIR
OR MAHOGANY

#10 X 2" SS OR BRONZE
FLAT HEAD WOOD SCREWS

3/4 X 1 1/2 FIR

SIDES - 2 LAYERS 1/2 PLY
FIBERGLASS BETWEEN
AND COVERING

1/4" X 3 1/2" SS OR BRONZE
FLAT HEAD MACHINE
SCREW, WASHER & NUT

CHINE LOG - 3/4" X 3-1/2"
MAHOGANY OR FIR

BOTTOM - 2 LAYERS 5/8" PLY
FIBERGLASS IN BETWEEN & ON BOTTOM

5/16" X 4" SS OR BRONZE F/H'D
MACHINE SCREW, WASHER & NUT

KEELSON 1 1/2" X 7 1/2" FIR

FRAME X-MEMBERS - 1 1/2 X 3 1/2 FIR

FLOOR TIMBERS
1 1/2 X 3 1/2 FIR

5/16 SS.
KEEL BOLTS

KEEL 1 1/2 X 7 1/2 FIR

VEE BOTTOM CONSTRUCTION

FORWARD SECTIONS
NO SCALE

CONSTRUCTION

TYPICAL AT AFT SECTION
NO SCALE

Spira International, Inc.
Huntington Beach, California

HILO
31' HAWAIIAN SAMPAN

DRAWN BY:
J. SPIRA

DATE:
06/29/10

DRAWING NO.
HILO02

SCALE 1/2" = 1' & NOTED

SHEET OF

4

3

2

1