

4

3


2

1

NOTICE

THIS DRAWING CONTAINS A PROPRIETARY DESIGN ASSIGNED TO SPIRA INTERNATIONAL, INC. ALL RIGHTS TO DUPLICATE, TRANSFER OR USE ARE EXPRESSLY RESERVED BY SPIRA INTERNATIONAL. THE BUYER IS LICENSED TO BUILD ONE ASSEMBLY FROM THESE PLANS.

REVISIONS				
ZONE	LTR	DESCRIPTION	DATE	APPROVED

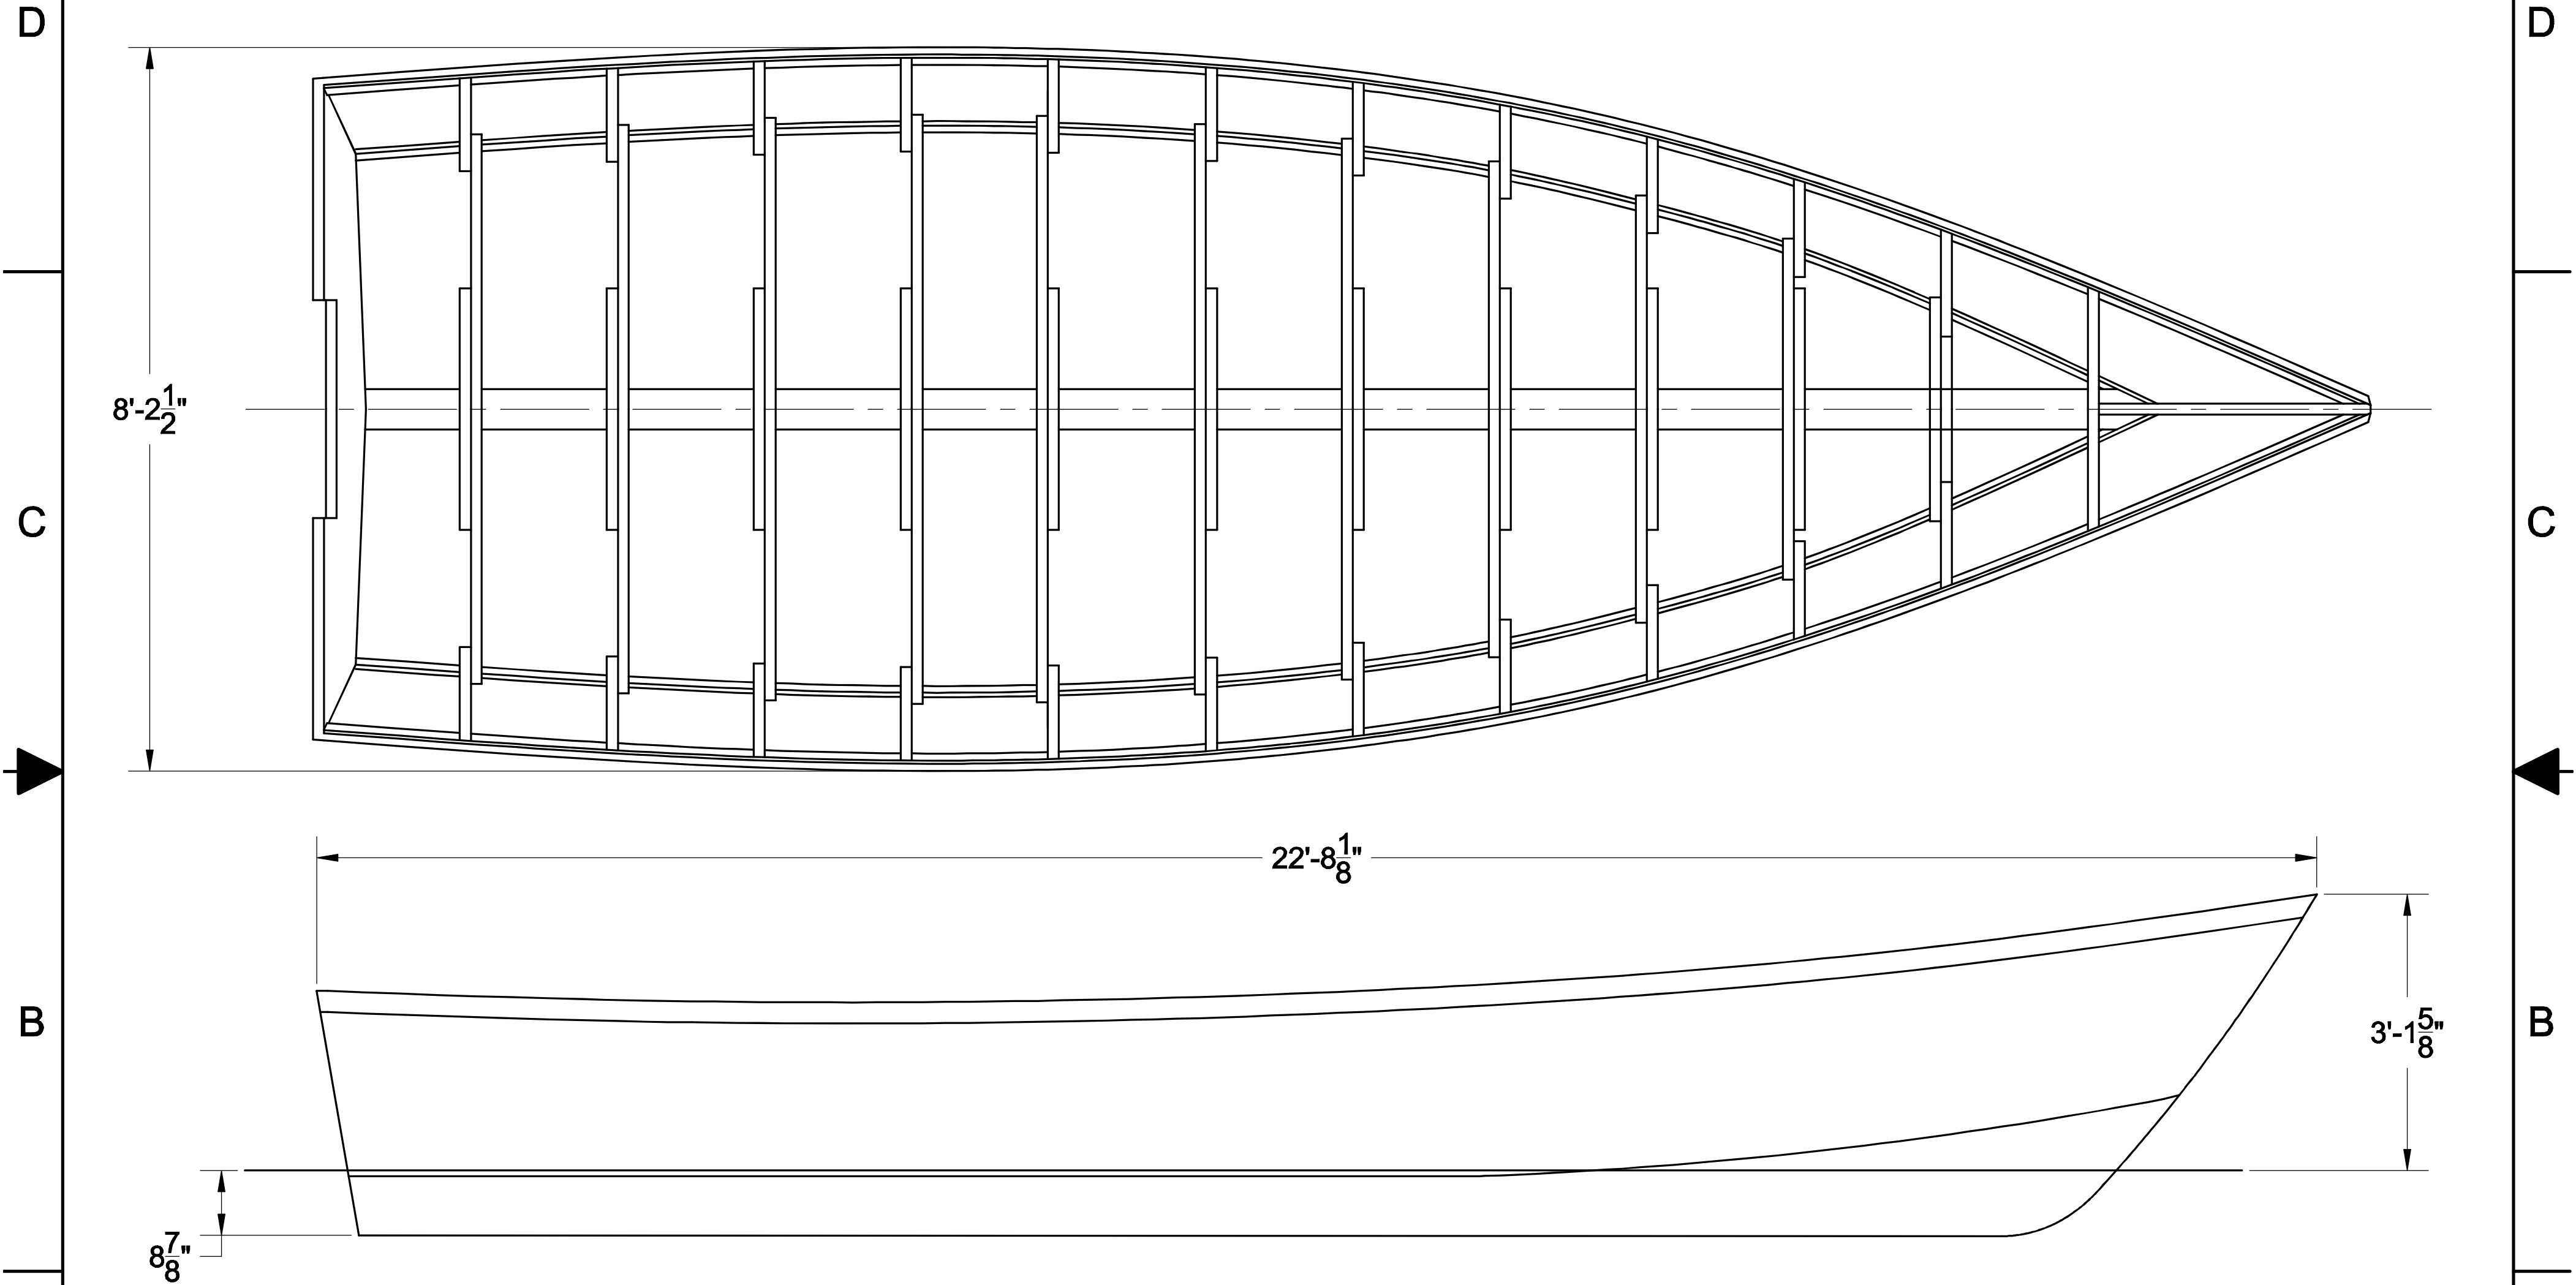

SPECIFICATIONS	
MAX. DISPLACEMENT	5900 LBS
HULL WEIGHT	1700 LBS
CALC. MAX. HORSEPOWER	275 HP
RECOMMENDED HP	90 HP

Spira International, Inc. <i>Huntington Beach, California</i>		
IXTAPA 23' SUPER PANGA		
DRAWN BY: J. SPIRA	DATE: 05/25/13	DRAWING NO. IXTA01
SCALE 3/4" = 1'	SHEET OF	

4

3

2

1

NOTICE

THIS DRAWING CONTAINS A PROPRIETARY DESIGN ASSIGNED TO SPIRA INTERNATIONAL, INC. ALL RIGHTS TO DUPLICATE, TRANSFER OR USE ARE EXPRESSLY RESERVED BY SPIRA INTERNATIONAL. THE BUYER IS LICENSED TO BUILD ONE ASSEMBLY FROM THESE PLANS.

REVISIONS				
ZONE	LTR	DESCRIPTION	DATE	APPROVED

BILL OF MATERIALS (HULL ONLY)

10 SHEETS 5/8" PLY
8 SHEETS 1/2" PLY
200' 2X4 LUMBER FOR FRAMES
180' 1X3 CLEAR LUMBER FOR SHEER
CLAMP, CHINE LOG AND RUB RAILS
24' 2X6 LUMBER FOR KEELSON
16' 2X8 LUMBER FOR TRANSOM & STEM
250 #10 X 2-1/2 SS DECK SCREWS
250 #8 X 2 SS DECK SCREWS
2500 #8 X 1-1/2 SS DECK SCREWS
6 GAL EPOXY RESIN
48 YDS 6 OZ FIBERGLASS CLOTH

FASTENING SCHEDULE


2x FRAME TO 2x FRAME: #10 X 2 -1/2 DECK SCREWS
LONGITUDINAL TO FRAME: #8 X 2 DECK SCREWS
PLANKING TO FRAME: #8 X 1-1/2 DECK SCREWS

NOTES:


1. YOU MAY SCARF TOGETHER SHORTER PIECES TO CREATE THE LONGITUDINAL ELEMENTS.
2. NOMINAL LUMBER SIZED CALLED OUT, E.G. A 2 X 4 LUMBER IS ACTUAL SIZE 1-1/2" X 3-1/2"

SEQUENCE FOR MAKING FRAMES


NO SCALE

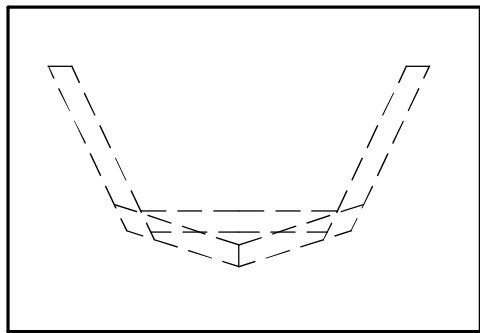


DRAW FRAME ON
SCRAP PLYWOOD

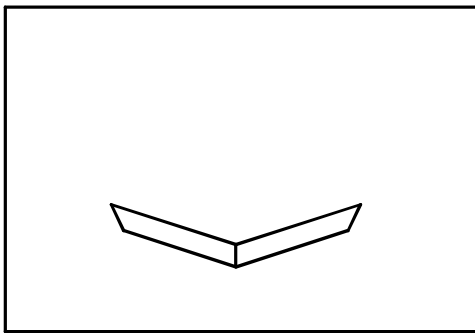


CUT OUT LOWER FRAME
ELEMENTS AND LOCATE
IN POSITION - EPOXY
CENTER JOINT

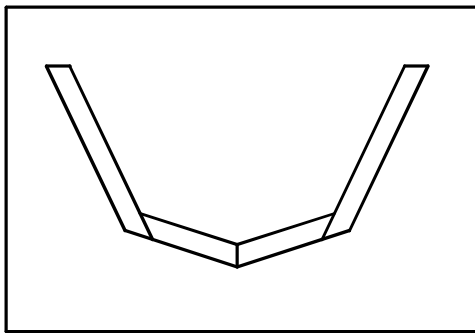

REPEAT FOR SIDE
FRAMES - EPOXY &
SCREW IN POSITION
ATOP BOTTOM FRAMES

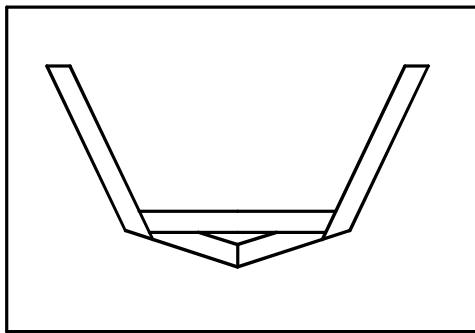

CUT OUT DECK
BEAM, LOCATE IN
POSITION, EPOXY &
SCREW IN PLACE

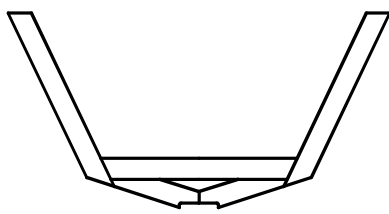

CUT OUT KEELSON
NOTCH AFTER EPOXY
HAS SET FULLY

Spira International, Inc.
Huntington Beach, California

IXTAPA
23' SUPER PANGA

DRAWN BY:
J. SPIRA

DATE:
05/25/13

DRAWING NO.
IXTA02

SCALE 3/4" = 1'

SHEET OF