


4 3 2 1

NOTICE
THIS DRAWING CONTAINS A PROPRIETARY DESIGN ASSIGNED TO SPIRA INTERNATIONAL, INC. ALL RIGHTS TO DUPLICATE, TRANSFER OR USE ARE EXPRESSLY RESERVED BY SPIRA INTERNATIONAL. THE BUYER IS LICENSED TO BUILD ONE ASSEMBLY FROM THESE PLANS.


REVISIONS				
ZONE	LTR	DESCRIPTION	DATE	APPROVED

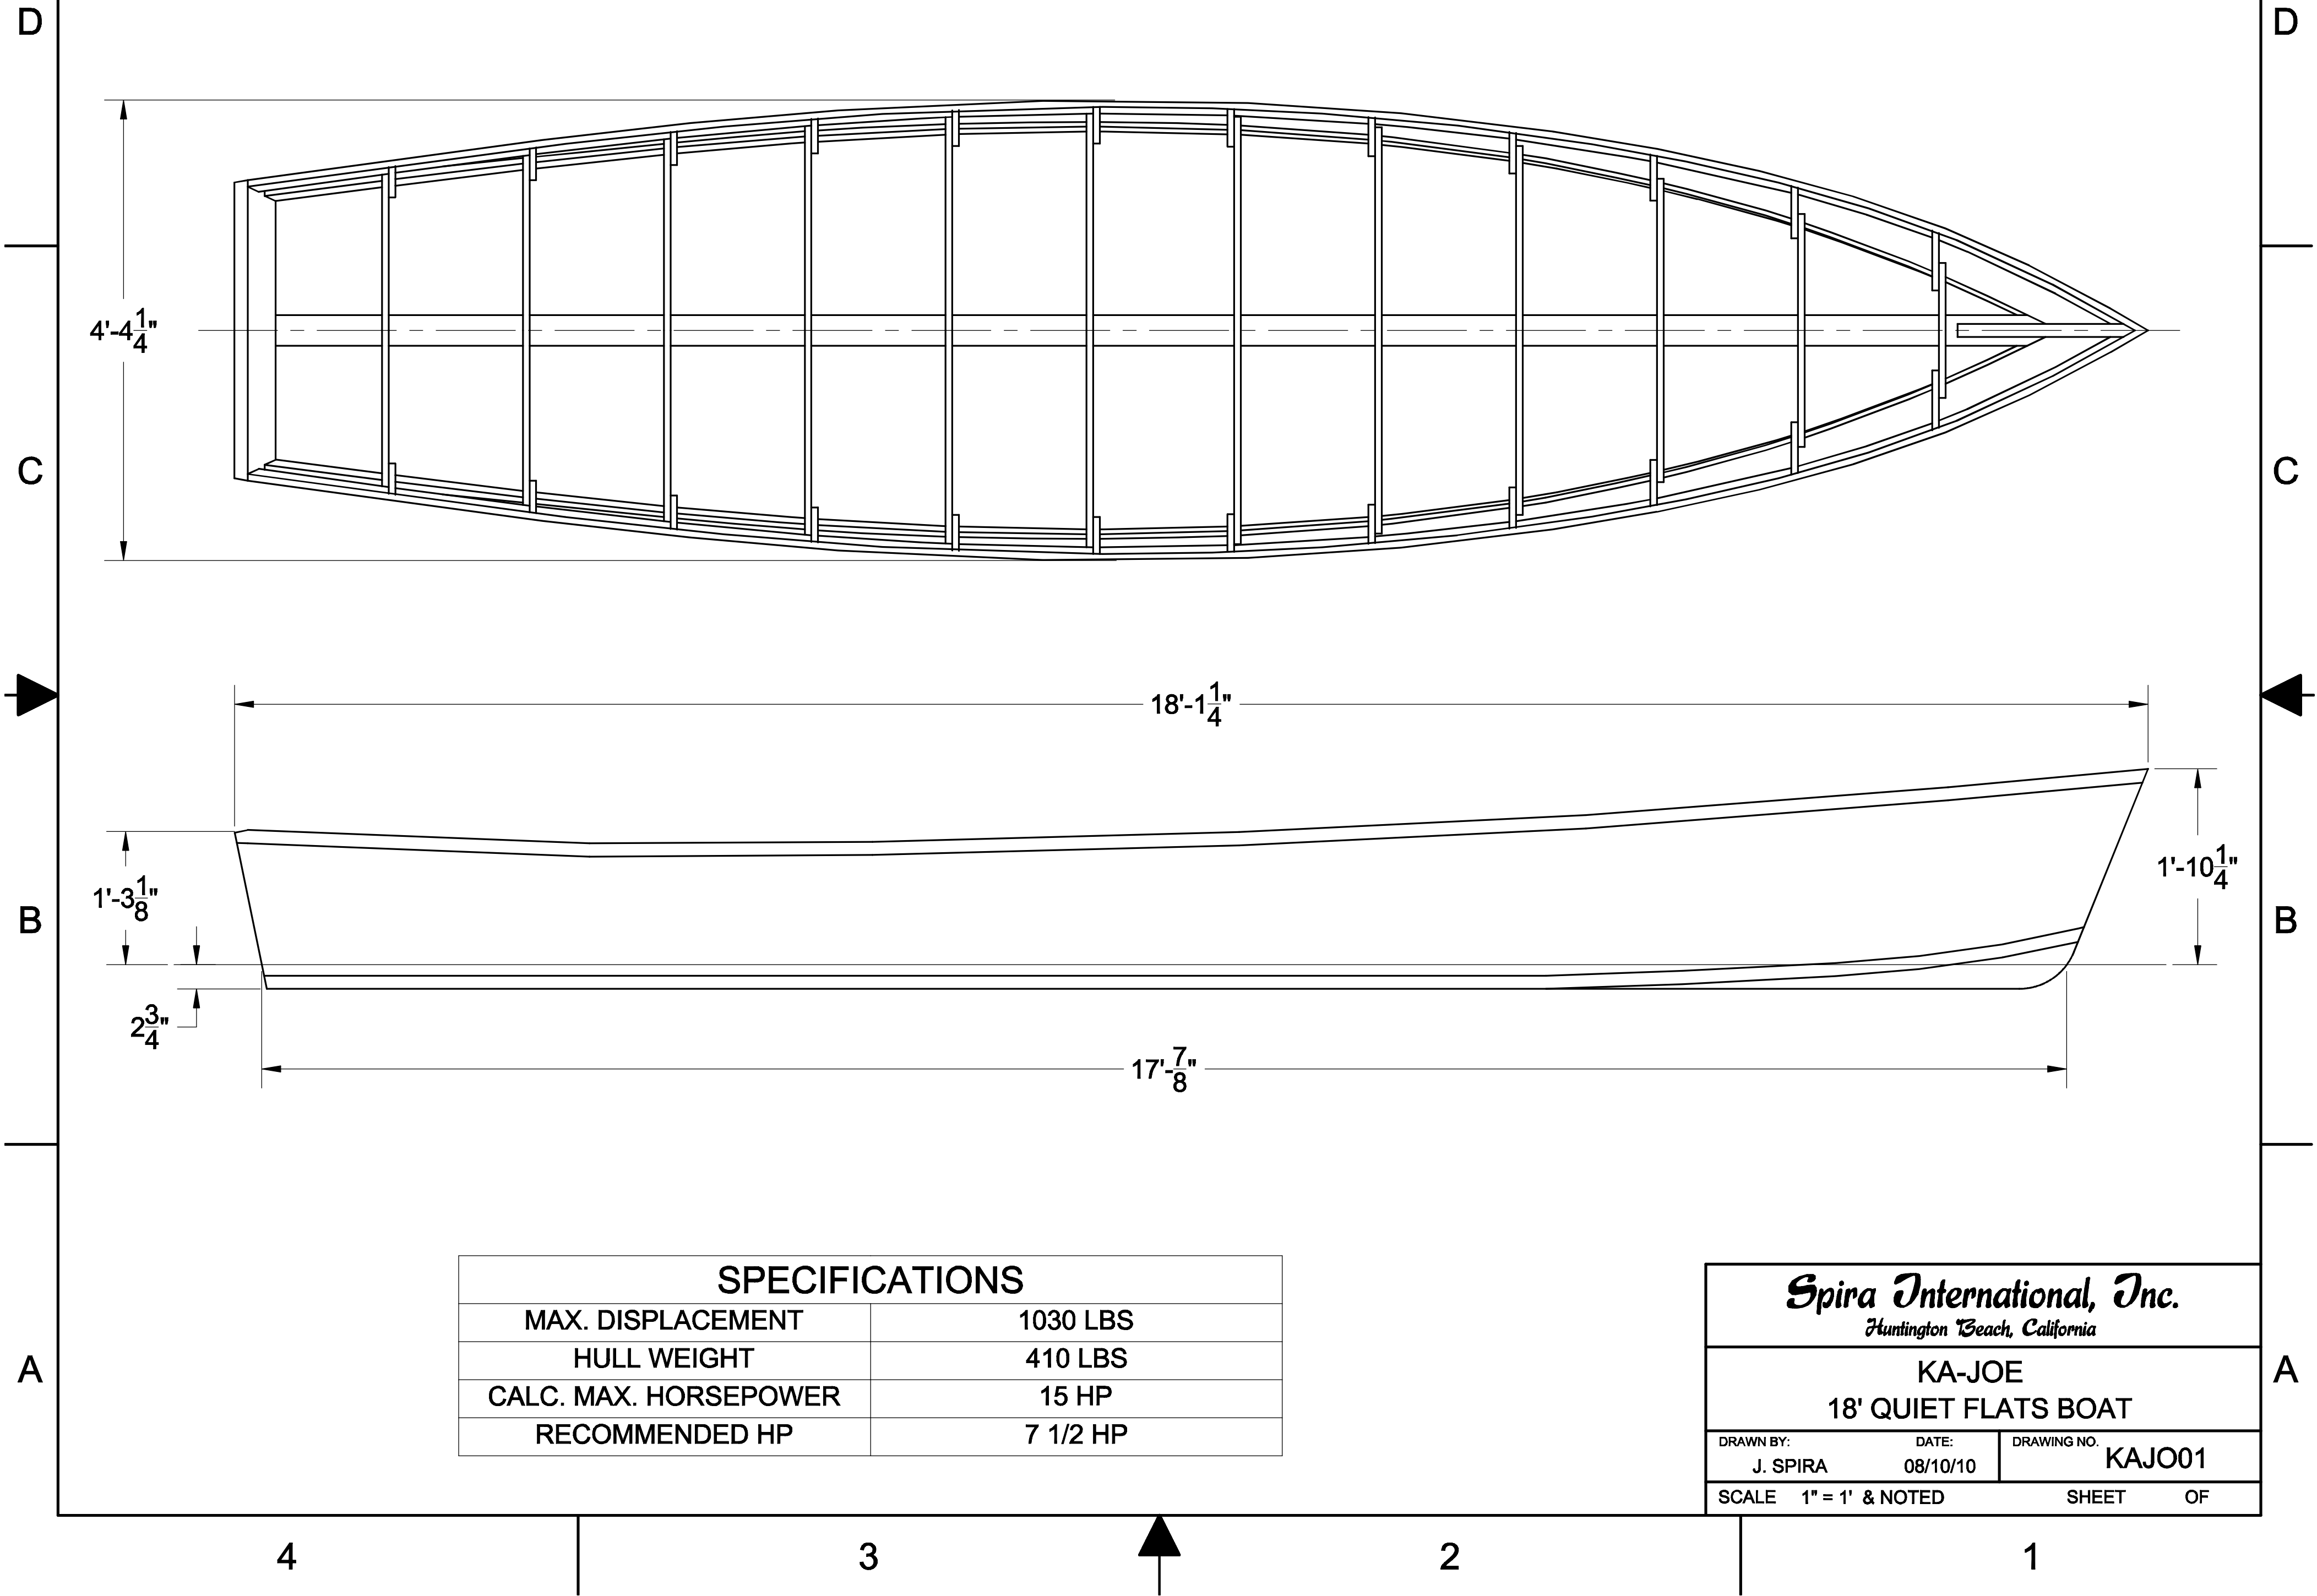

1

THIS DRAWING CONTAINS A PROPRIETARY DESIGN ASSIGNED TO SPIRA INTERNATIONAL, INC. ALL RIGHTS TO DUPLICATE, TRANSFER OR USE ARE EXPRESSLY RESERVED BY SPIRA INTERNATIONAL. THE BUYER IS LICENSED TO BUILD ONE ASSEMBLY FROM THESE PLANS.

REVISIONS				
ZONE	LTR	DESCRIPTION	DATE	APPROVED

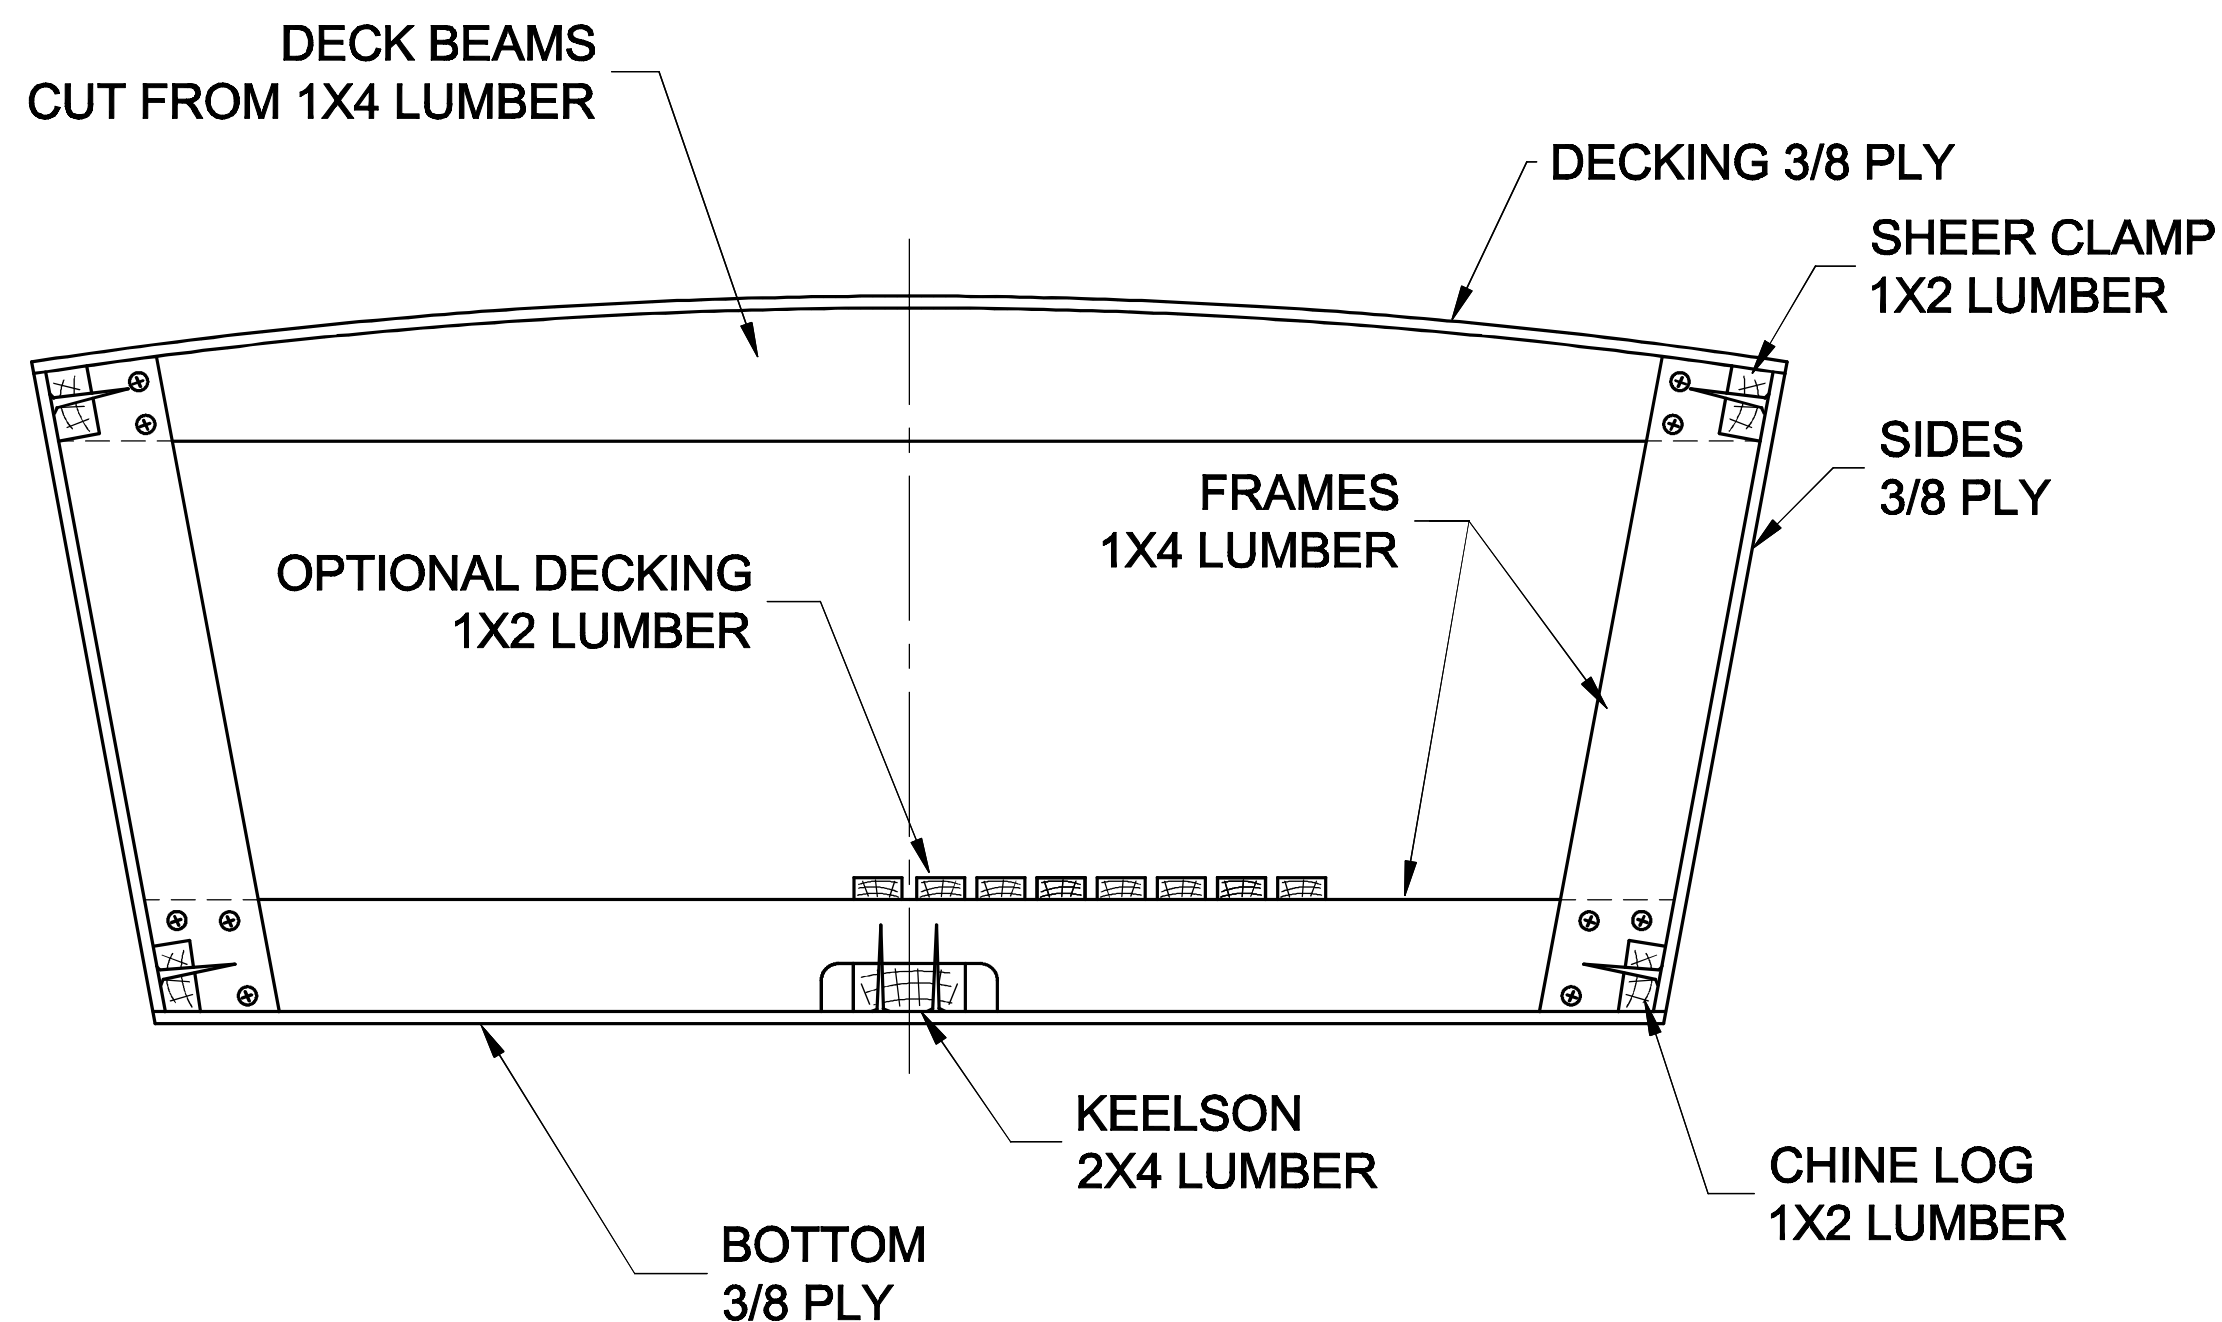

7 SHEETS 3/8" PLY
90' 1X4 LUMBER FOR FRAMES
80' 1X2 CLEAR LUMBER FOR SHEER CLAMP
CHINE LOG
32' 2X4 LUMBER FOR KEELSON TRANSOM STEM
50 - #10 X 2-1/2 DECK SCREWS
100 - #8 X 1-1/4 DECK SCREWS
100 - #8 X 2 DECK SCREWS
400 - #6 X 1 DECK SCREWS
1 GAL EPOXY RESIN
12 YDS 6 OZ FIBERGLASS CLOTH

KEELSON TO FRAMES: #10 X 2-1/2 DECK SCREWS
FRAMES TO FRAMES: #8 X 1-1/4 DECK SCREWS
LONGITUDINALS: #8 X 2 DECK SCREWS
PLY TO FRAMES: #6 X 1 DECK SCREWS

1. YOU MAY SCARF TOGETHER SHORTER PIECES TO CREATE THE LONGITUDINAL ELEMENTS.
2. NOMINAL LUMBER SIZED CALLED OUT, E.G. A 1 X 3 LUMBER IS ACTUAL SIZE 3/4" X 2-1/2"

Spira International, Inc.
Huntington Beach, California

KA-JOE
18' QUIET FLATS BOAT

DRAWN BY:
J. SPIRA

DATE:
08/10/10

DRAWING NO. **KAJO02**

SCALE 2" = 1'

SHEET OF