

4

3



2

1

NOTICE

THIS DRAWING CONTAINS A PROPRIETARY DESIGN ASSIGNED TO SPIRA INTERNATIONAL, INC. ALL RIGHTS TO DUPLICATE, TRANSFER OR USE ARE EXPRESSLY RESERVED BY SPIRA INTERNATIONAL. THE BUYER IS LICENSED TO BUILD ONE ASSEMBLY FROM THESE PLANS.

REVISIONS				
ZONE	LTR	DESCRIPTION	DATE	APPROVED

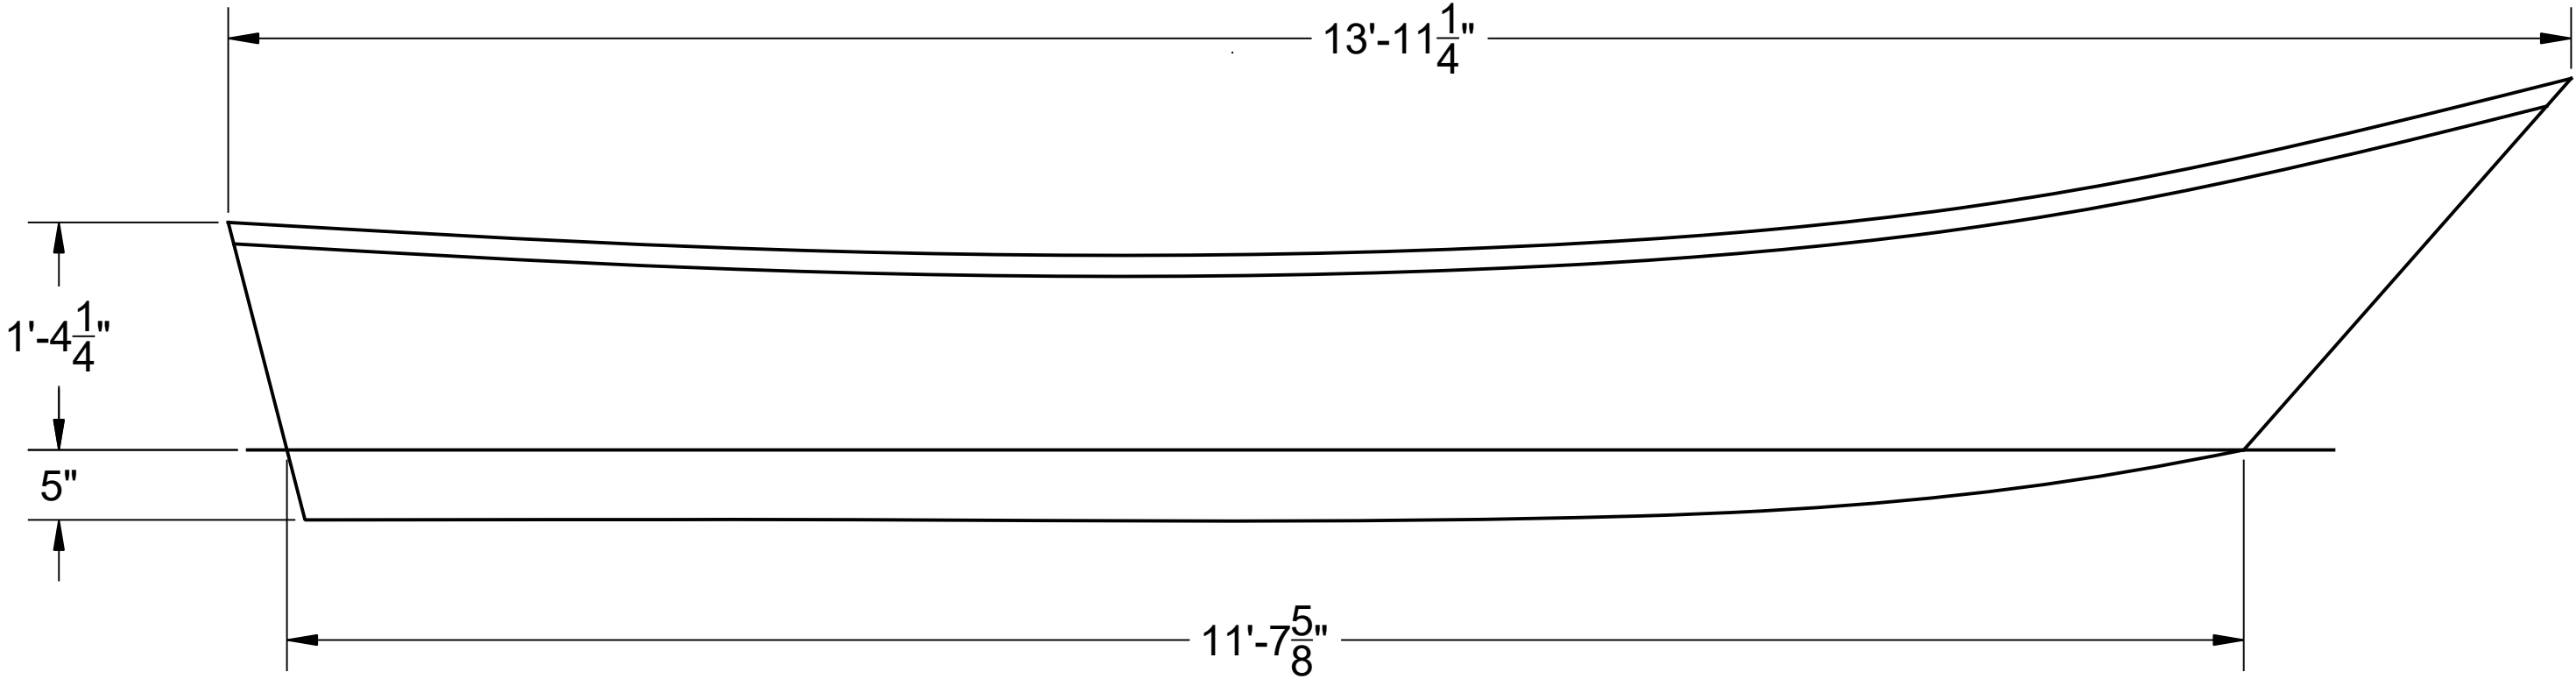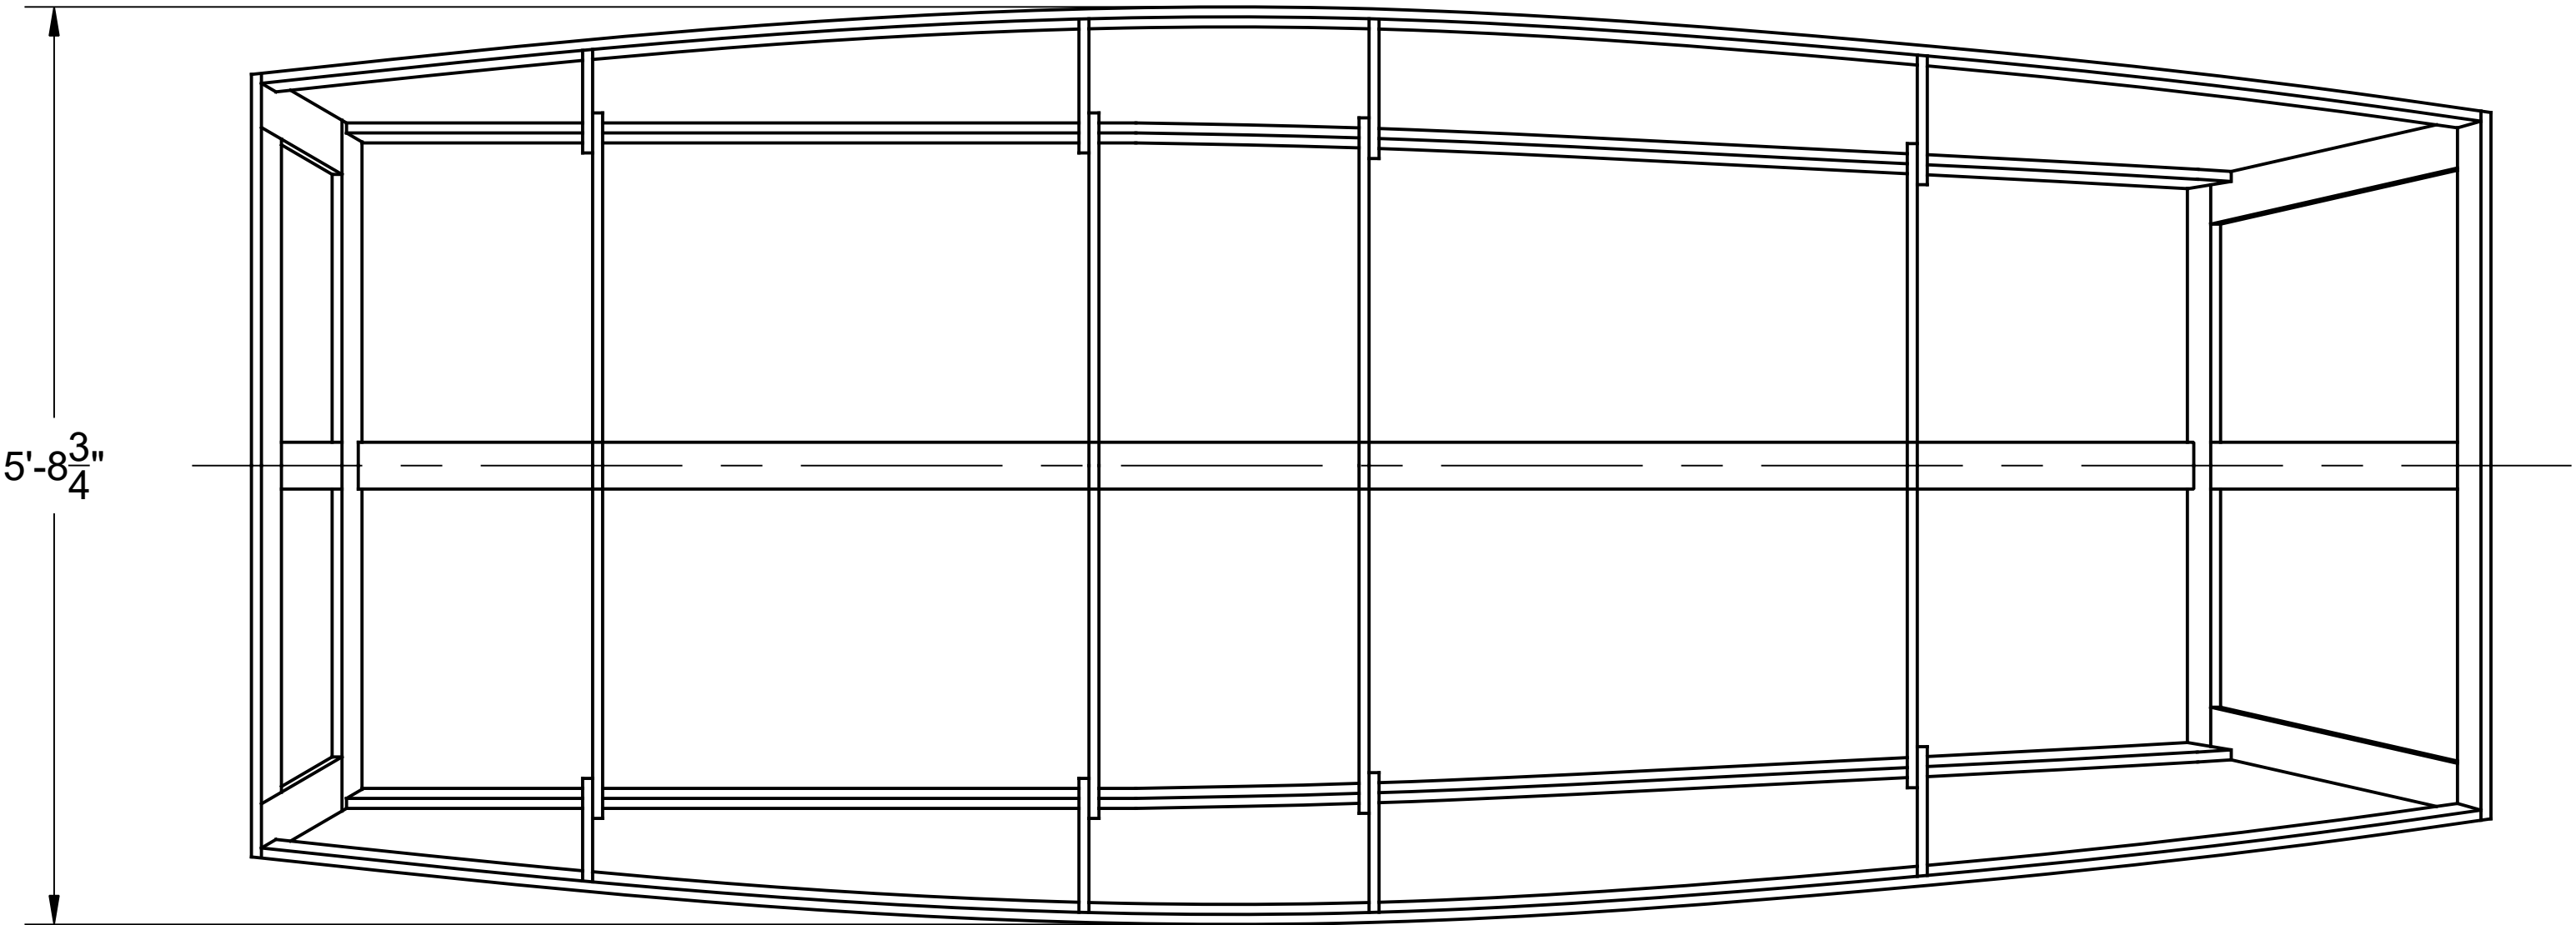

SPECIFICATIONS	
MAX. DISPLACEMENT	1160 LBS
HULL WEIGHT	195 LBS
MAX. HP	15 HP
RECOMMENDED HP	9.9 HP

 **Spira International, Inc.**
Huntington Beach, California

NOLA
14' GARVEY DORY

DRAWN BY: J. SPIRA	DATE: 10/09/16	DRAWING NO. NOLA01
SCALE 1' = 1' & NOTED		SHEET OF

4

3


2

1

NOTICE

THIS DRAWING CONTAINS A PROPRIETARY DESIGN ASSIGNED TO SPIRA INTERNATIONAL, INC. ALL RIGHTS TO DUPLICATE, TRANSFER OR USE ARE EXPRESSLY RESERVED BY SPIRA INTERNATIONAL. THE BUYER IS LICENSED TO BUILD ONE ASSEMBLY FROM THESE PLANS.

REVISIONS				
ZONE	LTR	DESCRIPTION	DATE	APPROVED

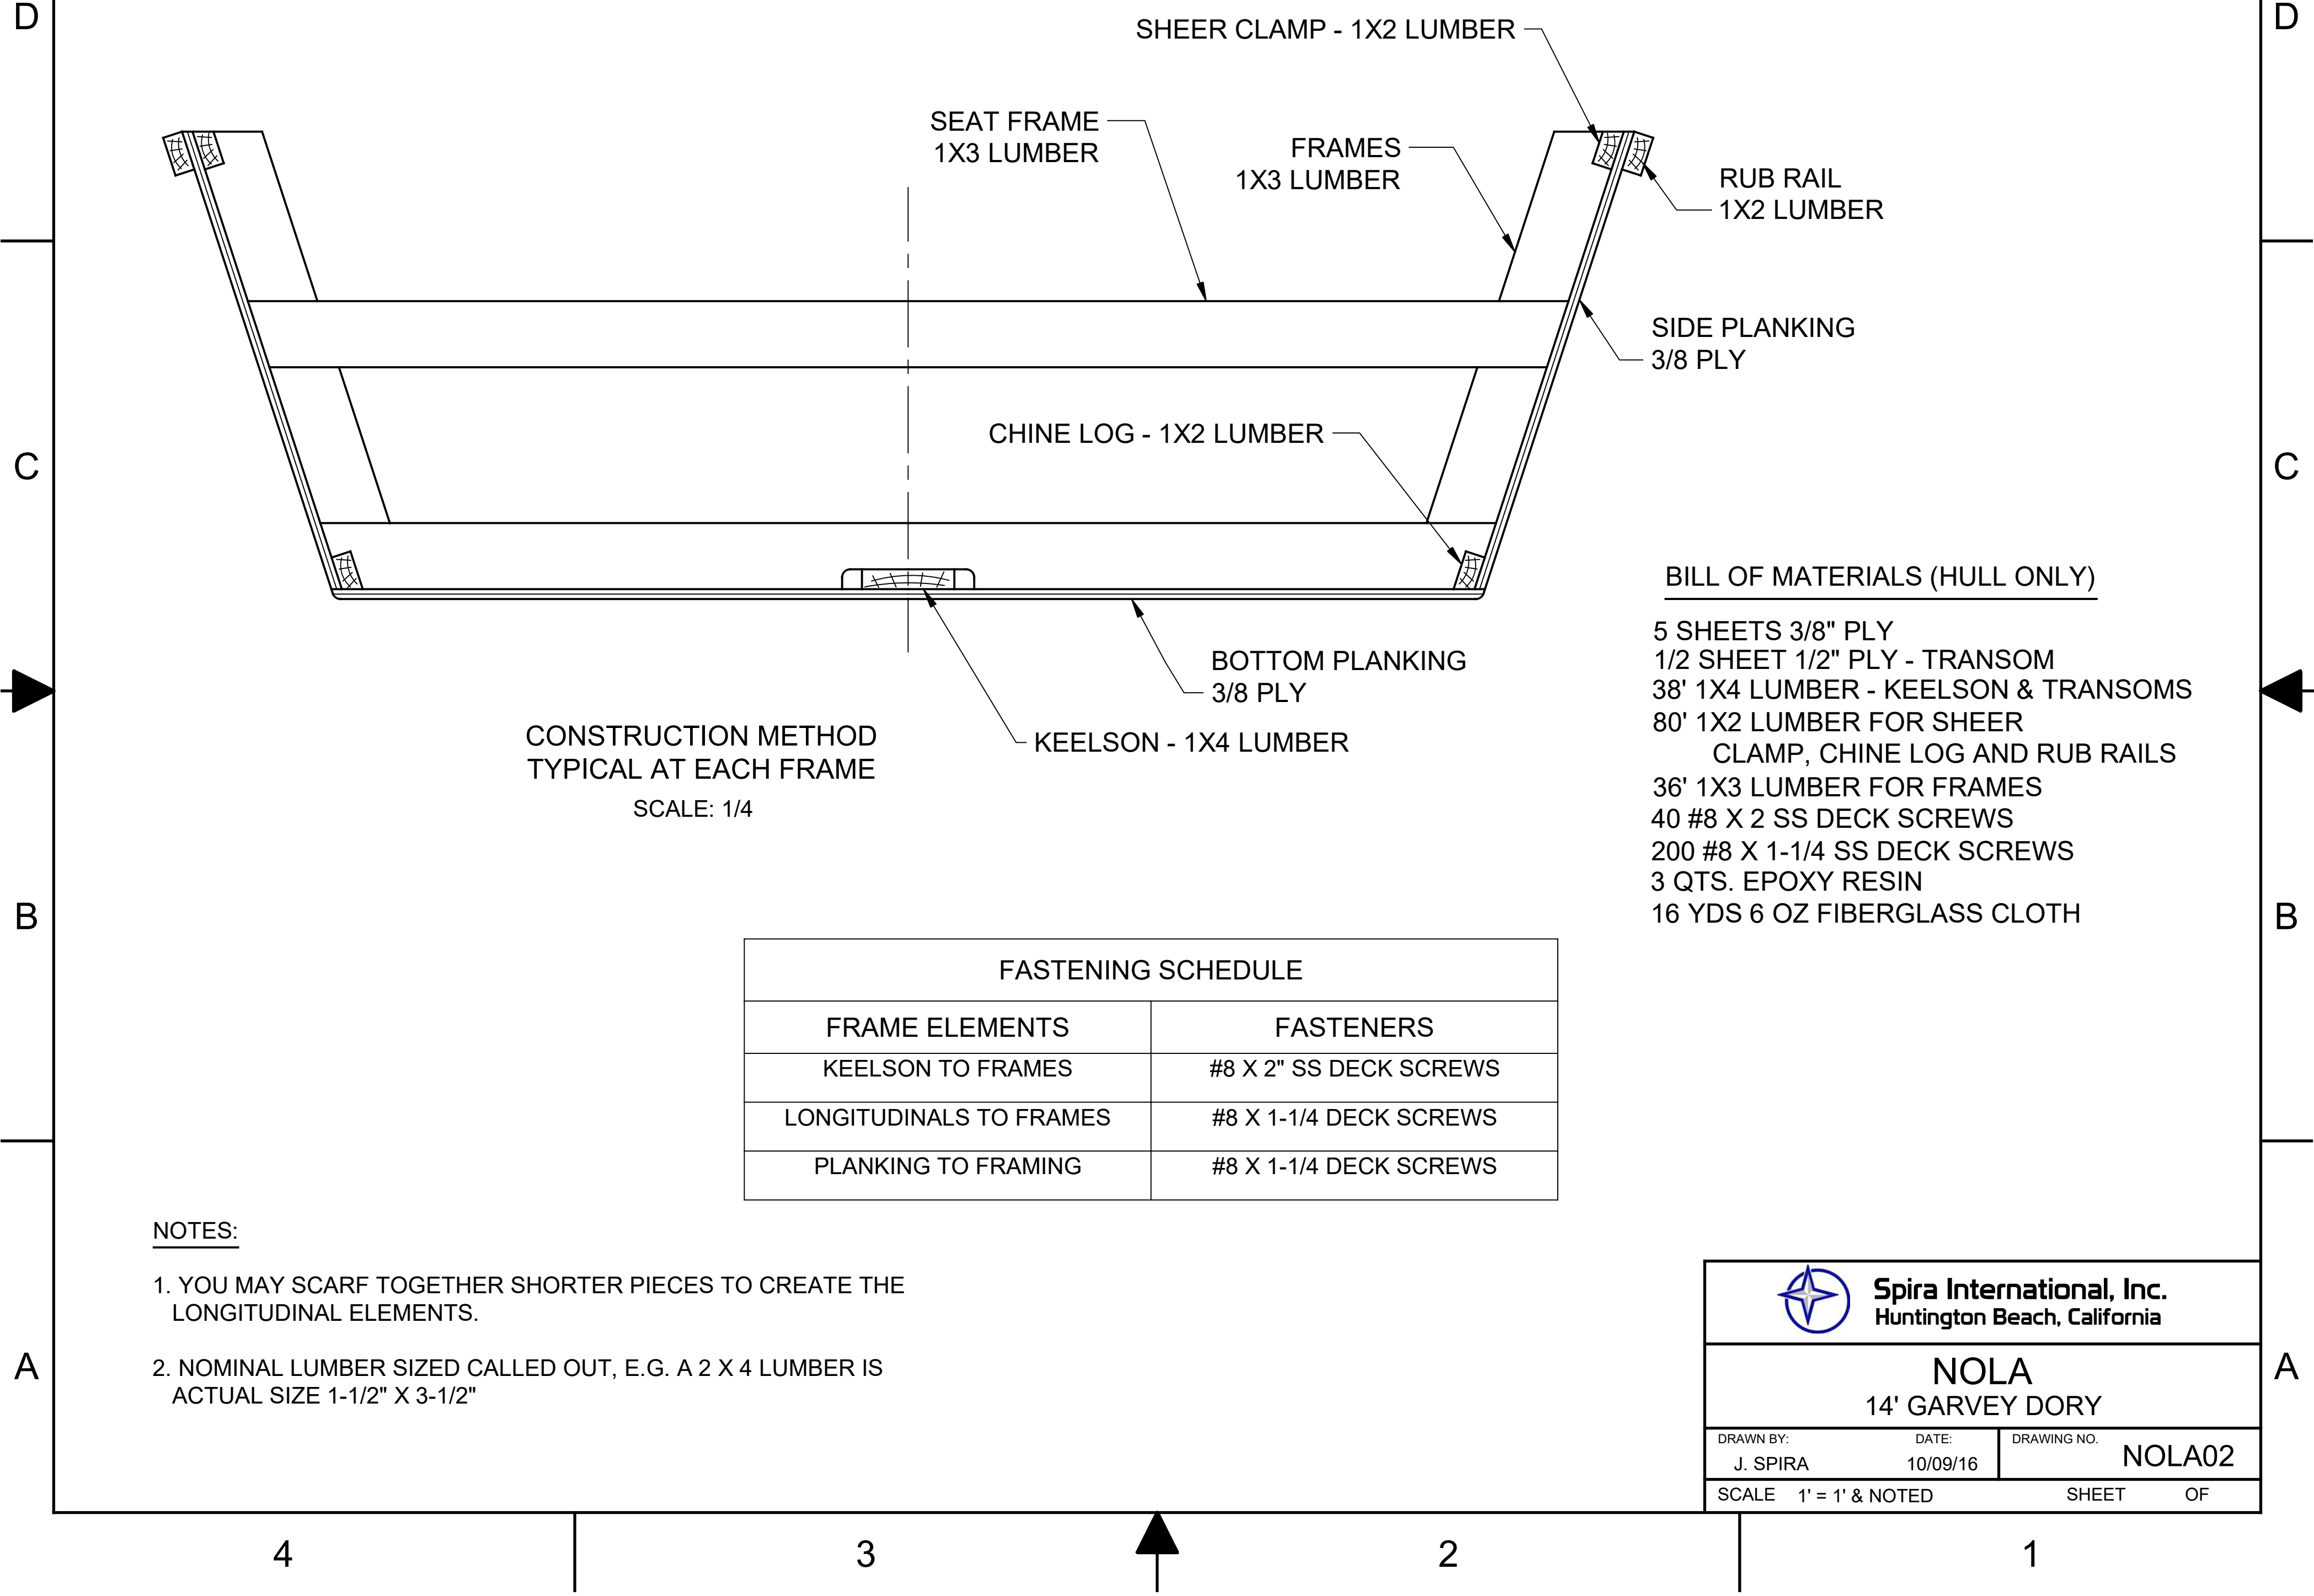

BILL OF MATERIALS (HULL ONLY)

- 5 SHEETS 3/8" PLY
- 1/2 SHEET 1/2" PLY - TRANSOM
- 38' 1X4 LUMBER - KEELSON & TRANSOMS
- 80' 1X2 LUMBER FOR SHEER CLAMP, CHINE LOG AND RUB RAILS
- 36' 1X3 LUMBER FOR FRAMES
- 40 #8 X 2 SS DECK SCREWS
- 200 #8 X 1-1/4 SS DECK SCREWS
- 3 QTS. EPOXY RESIN
- 16 YDS 6 OZ FIBERGLASS CLOTH

FASTENING SCHEDULE	
FRAME ELEMENTS	FASTENERS
KEELSON TO FRAMES	#8 X 2" SS DECK SCREWS
LONGITUDINALS TO FRAMES	#8 X 1-1/4 DECK SCREWS
PLANKING TO FRAMING	#8 X 1-1/4 DECK SCREWS

NOTES:

- 1. YOU MAY SCARF TOGETHER SHORTER PIECES TO CREATE THE LONGITUDINAL ELEMENTS.
- 2. NOMINAL LUMBER SIZED CALLED OUT, E.G. A 2 X 4 LUMBER IS ACTUAL SIZE 1-1/2" X 3-1/2"



Spira International, Inc.
Huntington Beach, California

NOLA

14' GARVEY DORY

DRAWN BY:
J. SPIRA

DATE:
10/09/16

DRAWING NO.
NOLA02

SCALE 1' = 1' & NOTED

SHEET OF