


NOTICE
THIS DRAWING CONTAINS A PROPRIETARY DESIGN ASSIGNED TO SPIRA INTERNATIONAL, INC. ALL RIGHTS TO DUPLICATE, TRANSFER OR SELL THIS DESIGN ARE EXPRESSLY RESERVED. THE BUYER IS LICENSED TO BUILD ONE ASSEMBLY FROM THESE PLANS.

REVISIONS				
ZONE	LTR	DESCRIPTION	DATE	APPROVED

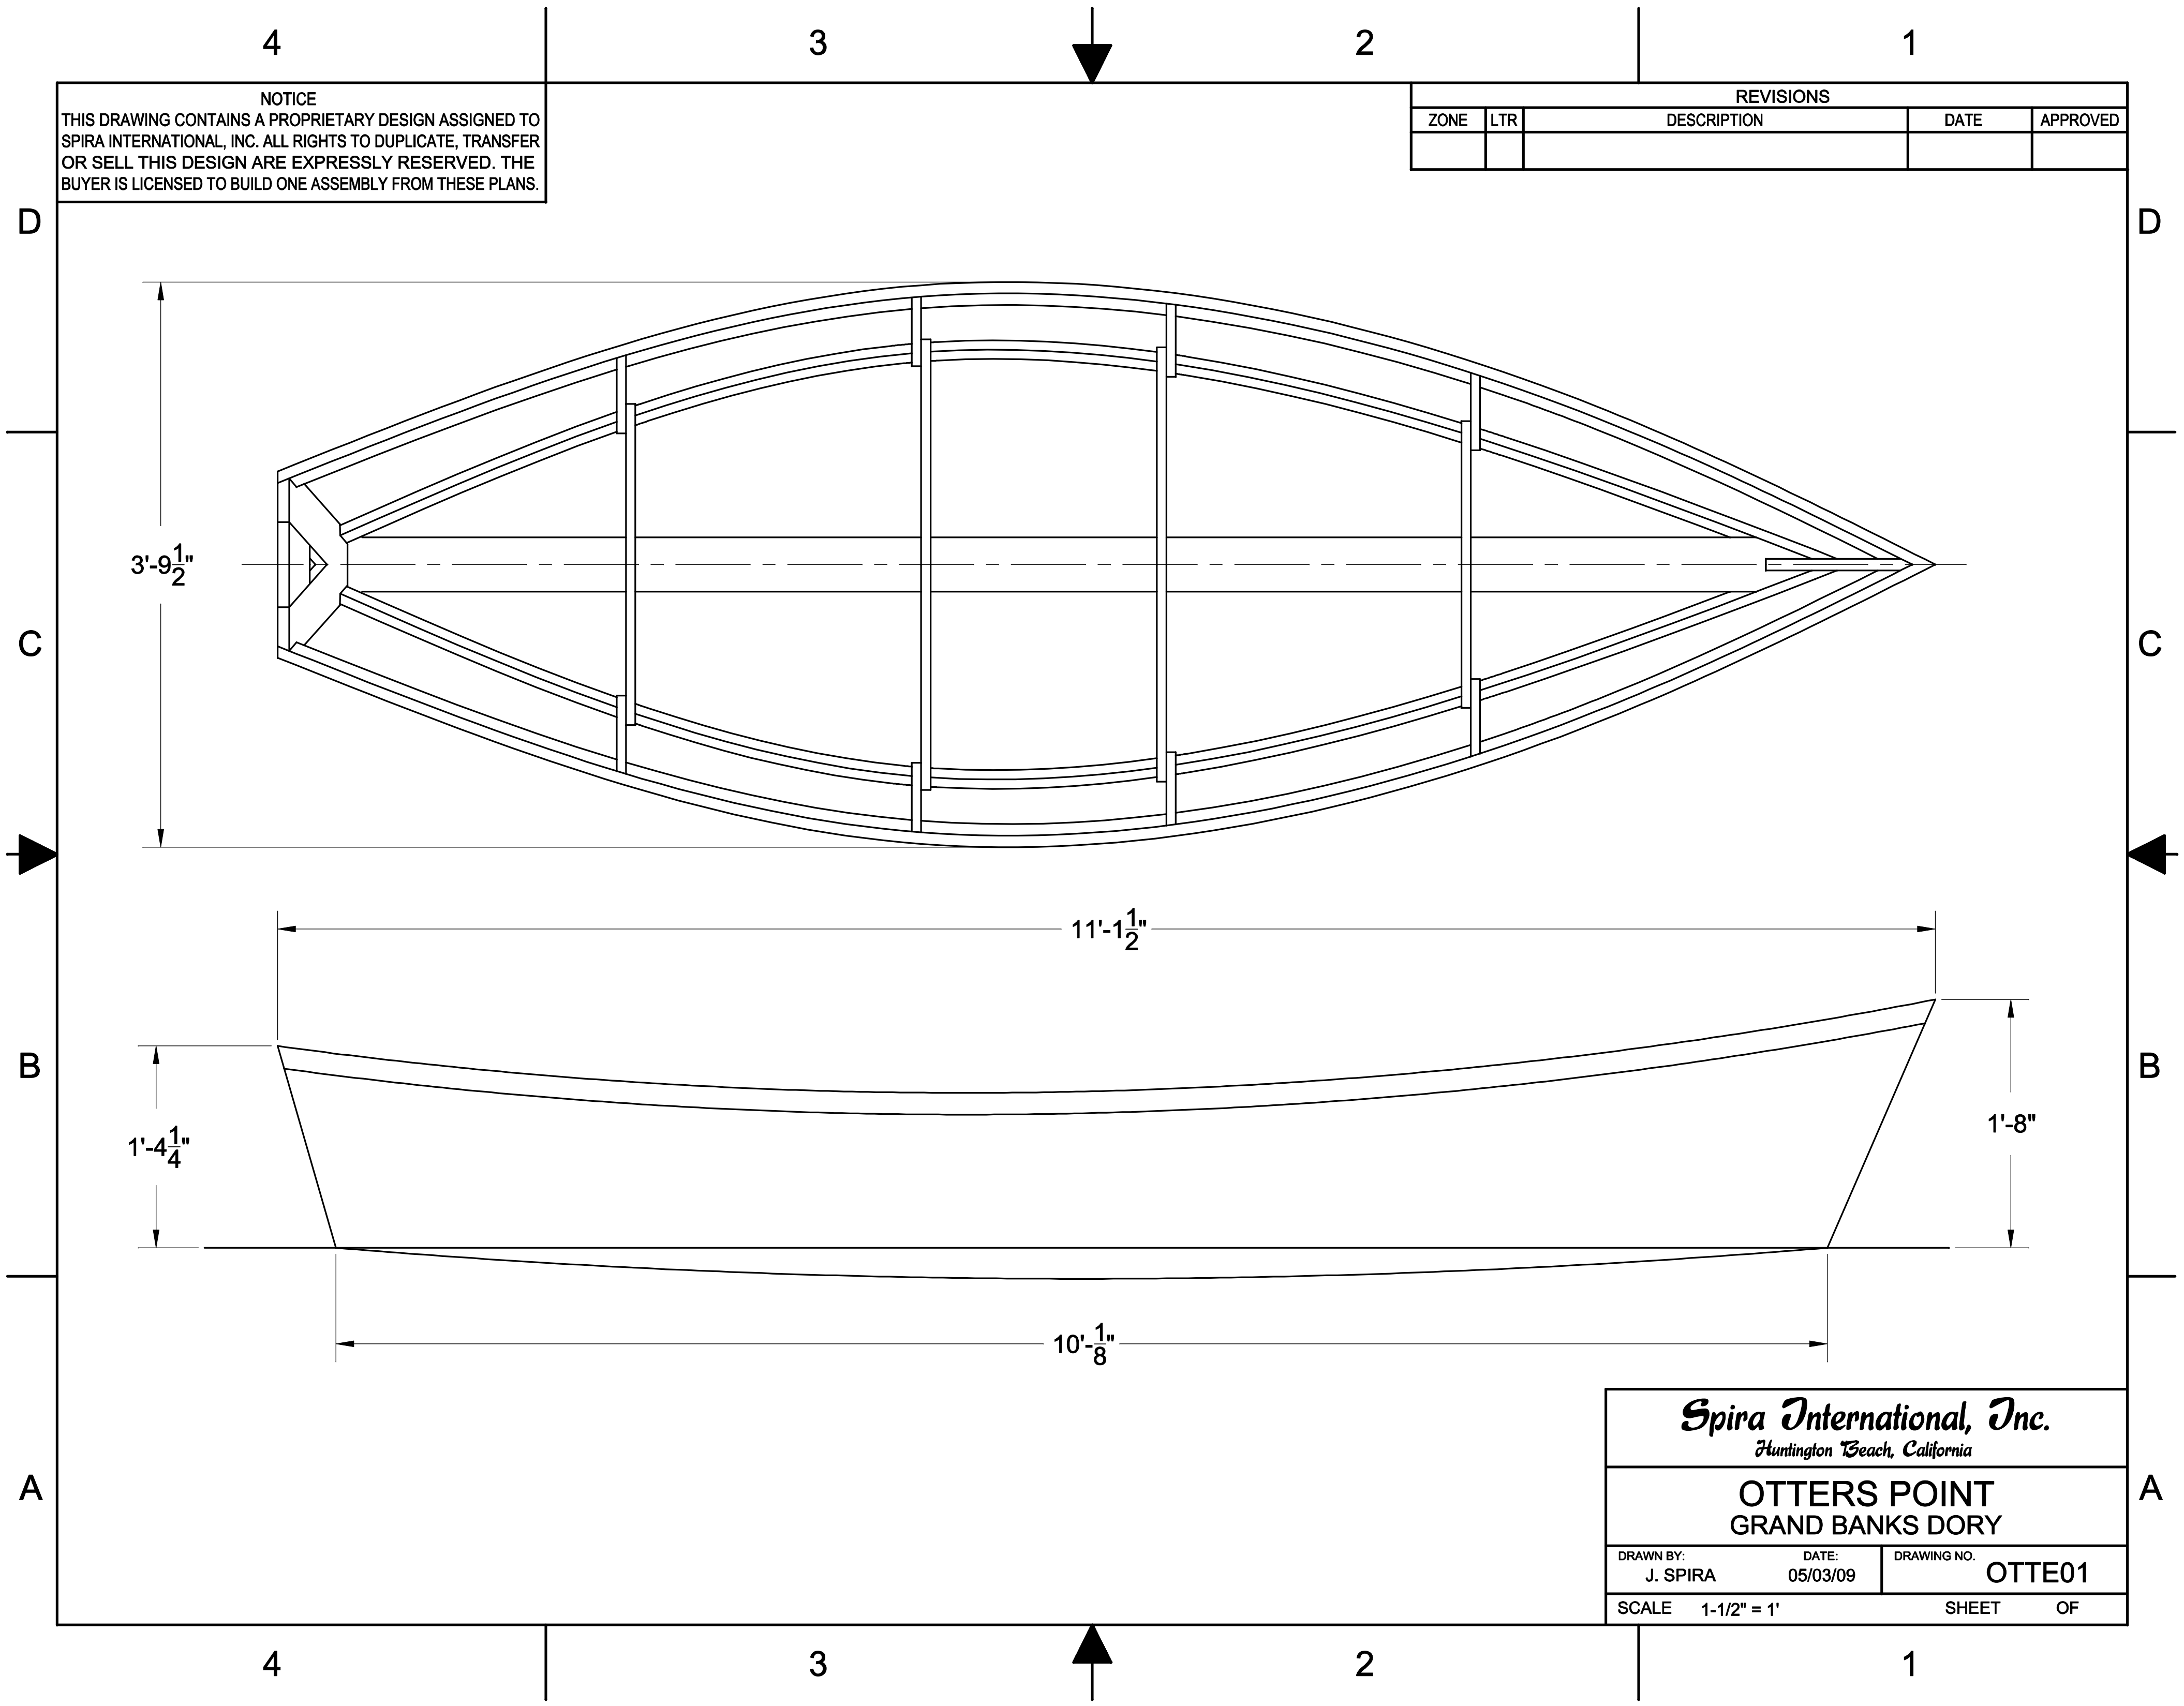

Spira International, Inc.
Huntington Beach, California

**OTTERS POINT
GRAND BANKS DORY**

DRAWN BY: J. SPIRA	DATE: 05/03/09	DRAWING NO. OTTE01
SCALE 1-1/2" = 1'		SHEET OF

NOTICE
THIS DRAWING CONTAINS A PROPRIETARY DESIGN ASSIGNED TO SPIRA INTERNATIONAL, INC. ALL RIGHTS TO DUPLICATE, TRANSFER OR SELL THIS DESIGN ARE EXPRESSLY RESERVED. THE BUYER IS LICENSED TO BUILD ONE ASSEMBLY FROM THESE PLANS.

REVISIONS				
ZONE	LTR	DESCRIPTION	DATE	APPROVED
	A	CORRECTED TYPOS IN BOM	08/02/10	JJS

BILL OF MATERIALS

2 SHEETS 1/4" PLY (SIDES)
1 SHEET 3/8" PLY (BOTTOM)
28' 1X3 LUMBER FOR FRAMES
40' 1X2 CLEAR LUMBER FOR SHEER
CLAMP, CHINE LOG AND RUB RAILS
13' 1X6 LUMBER FOR KEELSON & STEM
60 #8 X 1-1/4 DECK SCREWS
100 #8 X 2 DECK SCREWS
150 #6 X 1-1/4 DECK SCREWS
3 QTS EPOXY RESIN
10 YDS 6 OZ FIBERGLASS CLOTH

NOTES:

1. YOU MAY SCARF TOGETHER SHORTER PIECES TO CREATE THE LONGITUDINAL ELEMENTS.
2. NOMINAL LUMBER SIZED CALLED OUT, E.G. A 1 X 3 LUMBER IS ACTUAL SIZE 3/4" X 2-1/2"

CONSTRUCTION METHOD

TYPICAL AT EACH FRAME
NO SCALE

FASTENING SCHEDULE

FRAME TO FRAME: #8 X 1-1/4 DECK SCREWS
LONGITUDINAL TO FRAME: #8 X 2 DECK SCREWS
PLANKING TO FRAME: #6 X 1-1/4 DECK SCREWS

Spira International, Inc.
Huntington Beach, California

OTTERS POINT
GRAND BANKS DORY

DRAWN BY: J. SPIRA	DATE: 08/01/10	DRAWING NO. OTTE02
-----------------------	-------------------	-----------------------

SCALE	1-1/2" = 1' & NOTED	SHEET	OF
-------	---------------------	-------	----