

4

3

2

1

NOTICE
THIS DRAWING CONTAINS A PROPRIETARY DESIGN ASSIGNED TO SPIRA INTERNATIONAL, INC. ALL RIGHTS TO DUPLICATE, TRANSFER OR USE ARE EXPRESSLY RESERVED BY SPIRA INTERNATIONAL. THE BUYER IS LICENSED TO BUILD ONE ASSEMBLY FROM THESE PLANS.

REVISIONS				
ZONE	LTR	DESCRIPTION	DATE	APPROVED

D

D

C



C

B

B

A

A

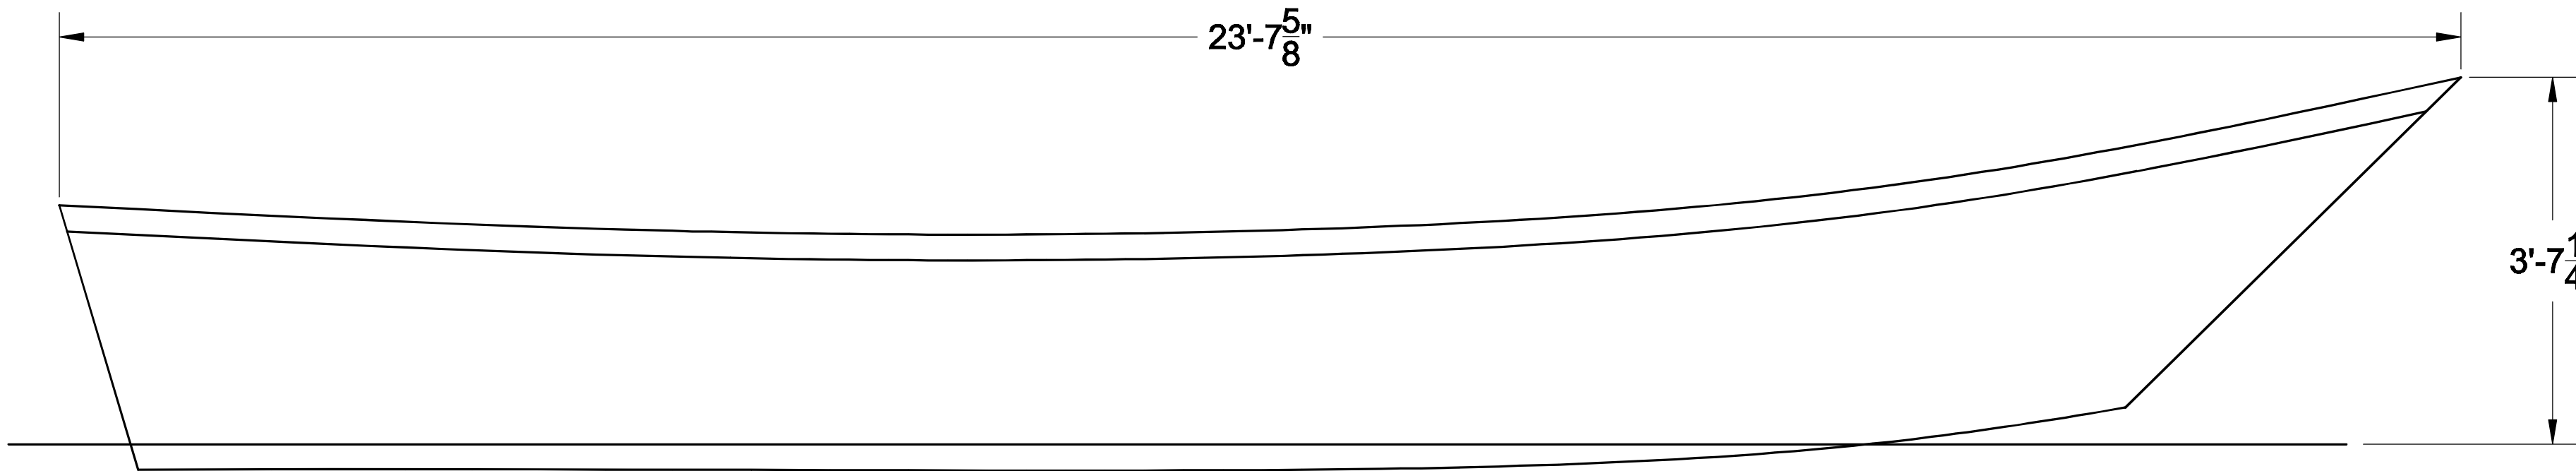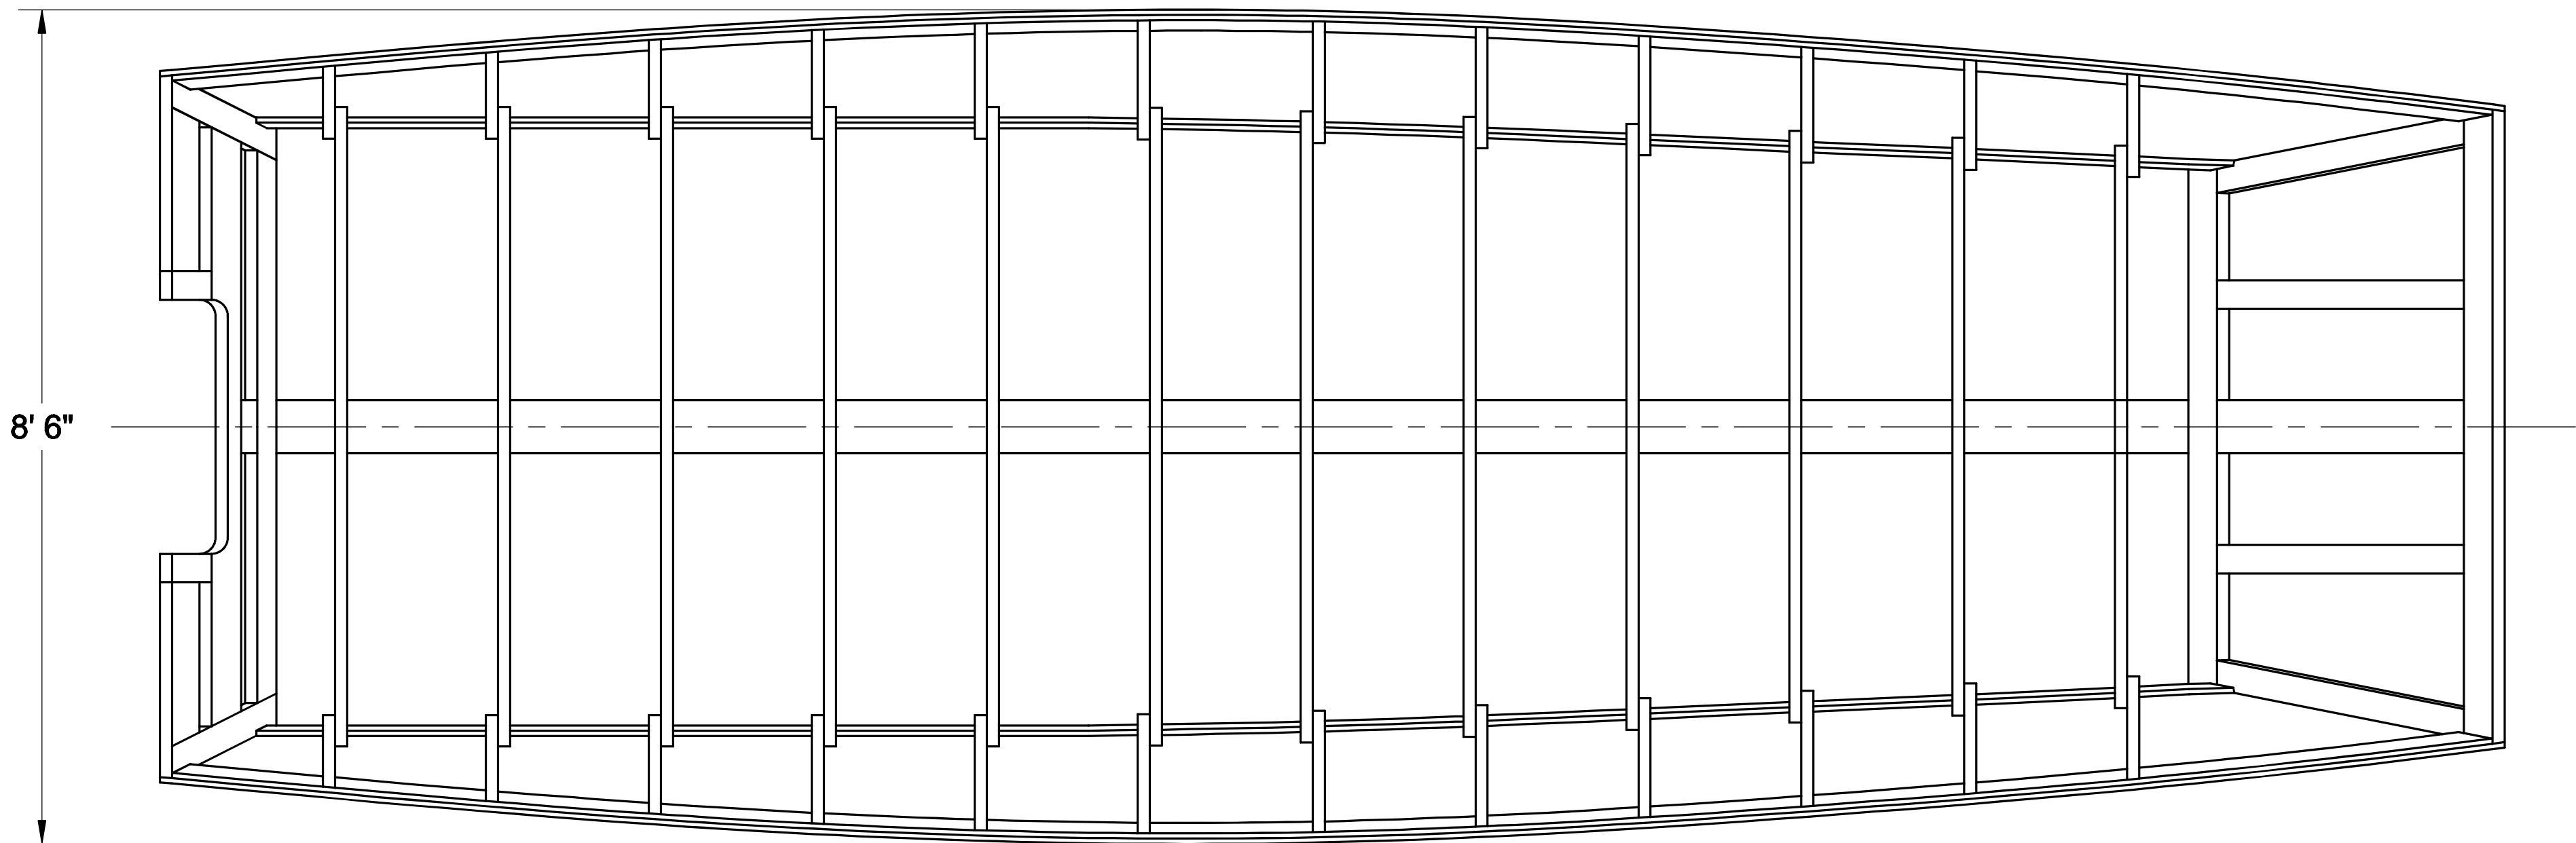

Spira International, Inc.
Huntington Beach, California

PUCHIE SPECIAL
24' GARVEY DORY

DRAWN BY: J. SPIRA	DATE: 11/12/12	DRAWING NO. PUCH01
SCALE 3/4" = 1' & NOTED	SHEET	OF

4

3

2

1

4

3


2

1

NOTICE

THIS DRAWING CONTAINS A PROPRIETARY DESIGN ASSIGNED TO SPIRA INTERNATIONAL, INC. ALL RIGHTS TO DUPLICATE, TRANSFER OR USE ARE EXPRESSLY RESERVED BY SPIRA INTERNATIONAL. THE BUYER IS LICENSED TO BUILD ONE ASSEMBLY FROM THESE PLANS.

REVISIONS				
ZONE	LTR	DESCRIPTION	DATE	APPROVED

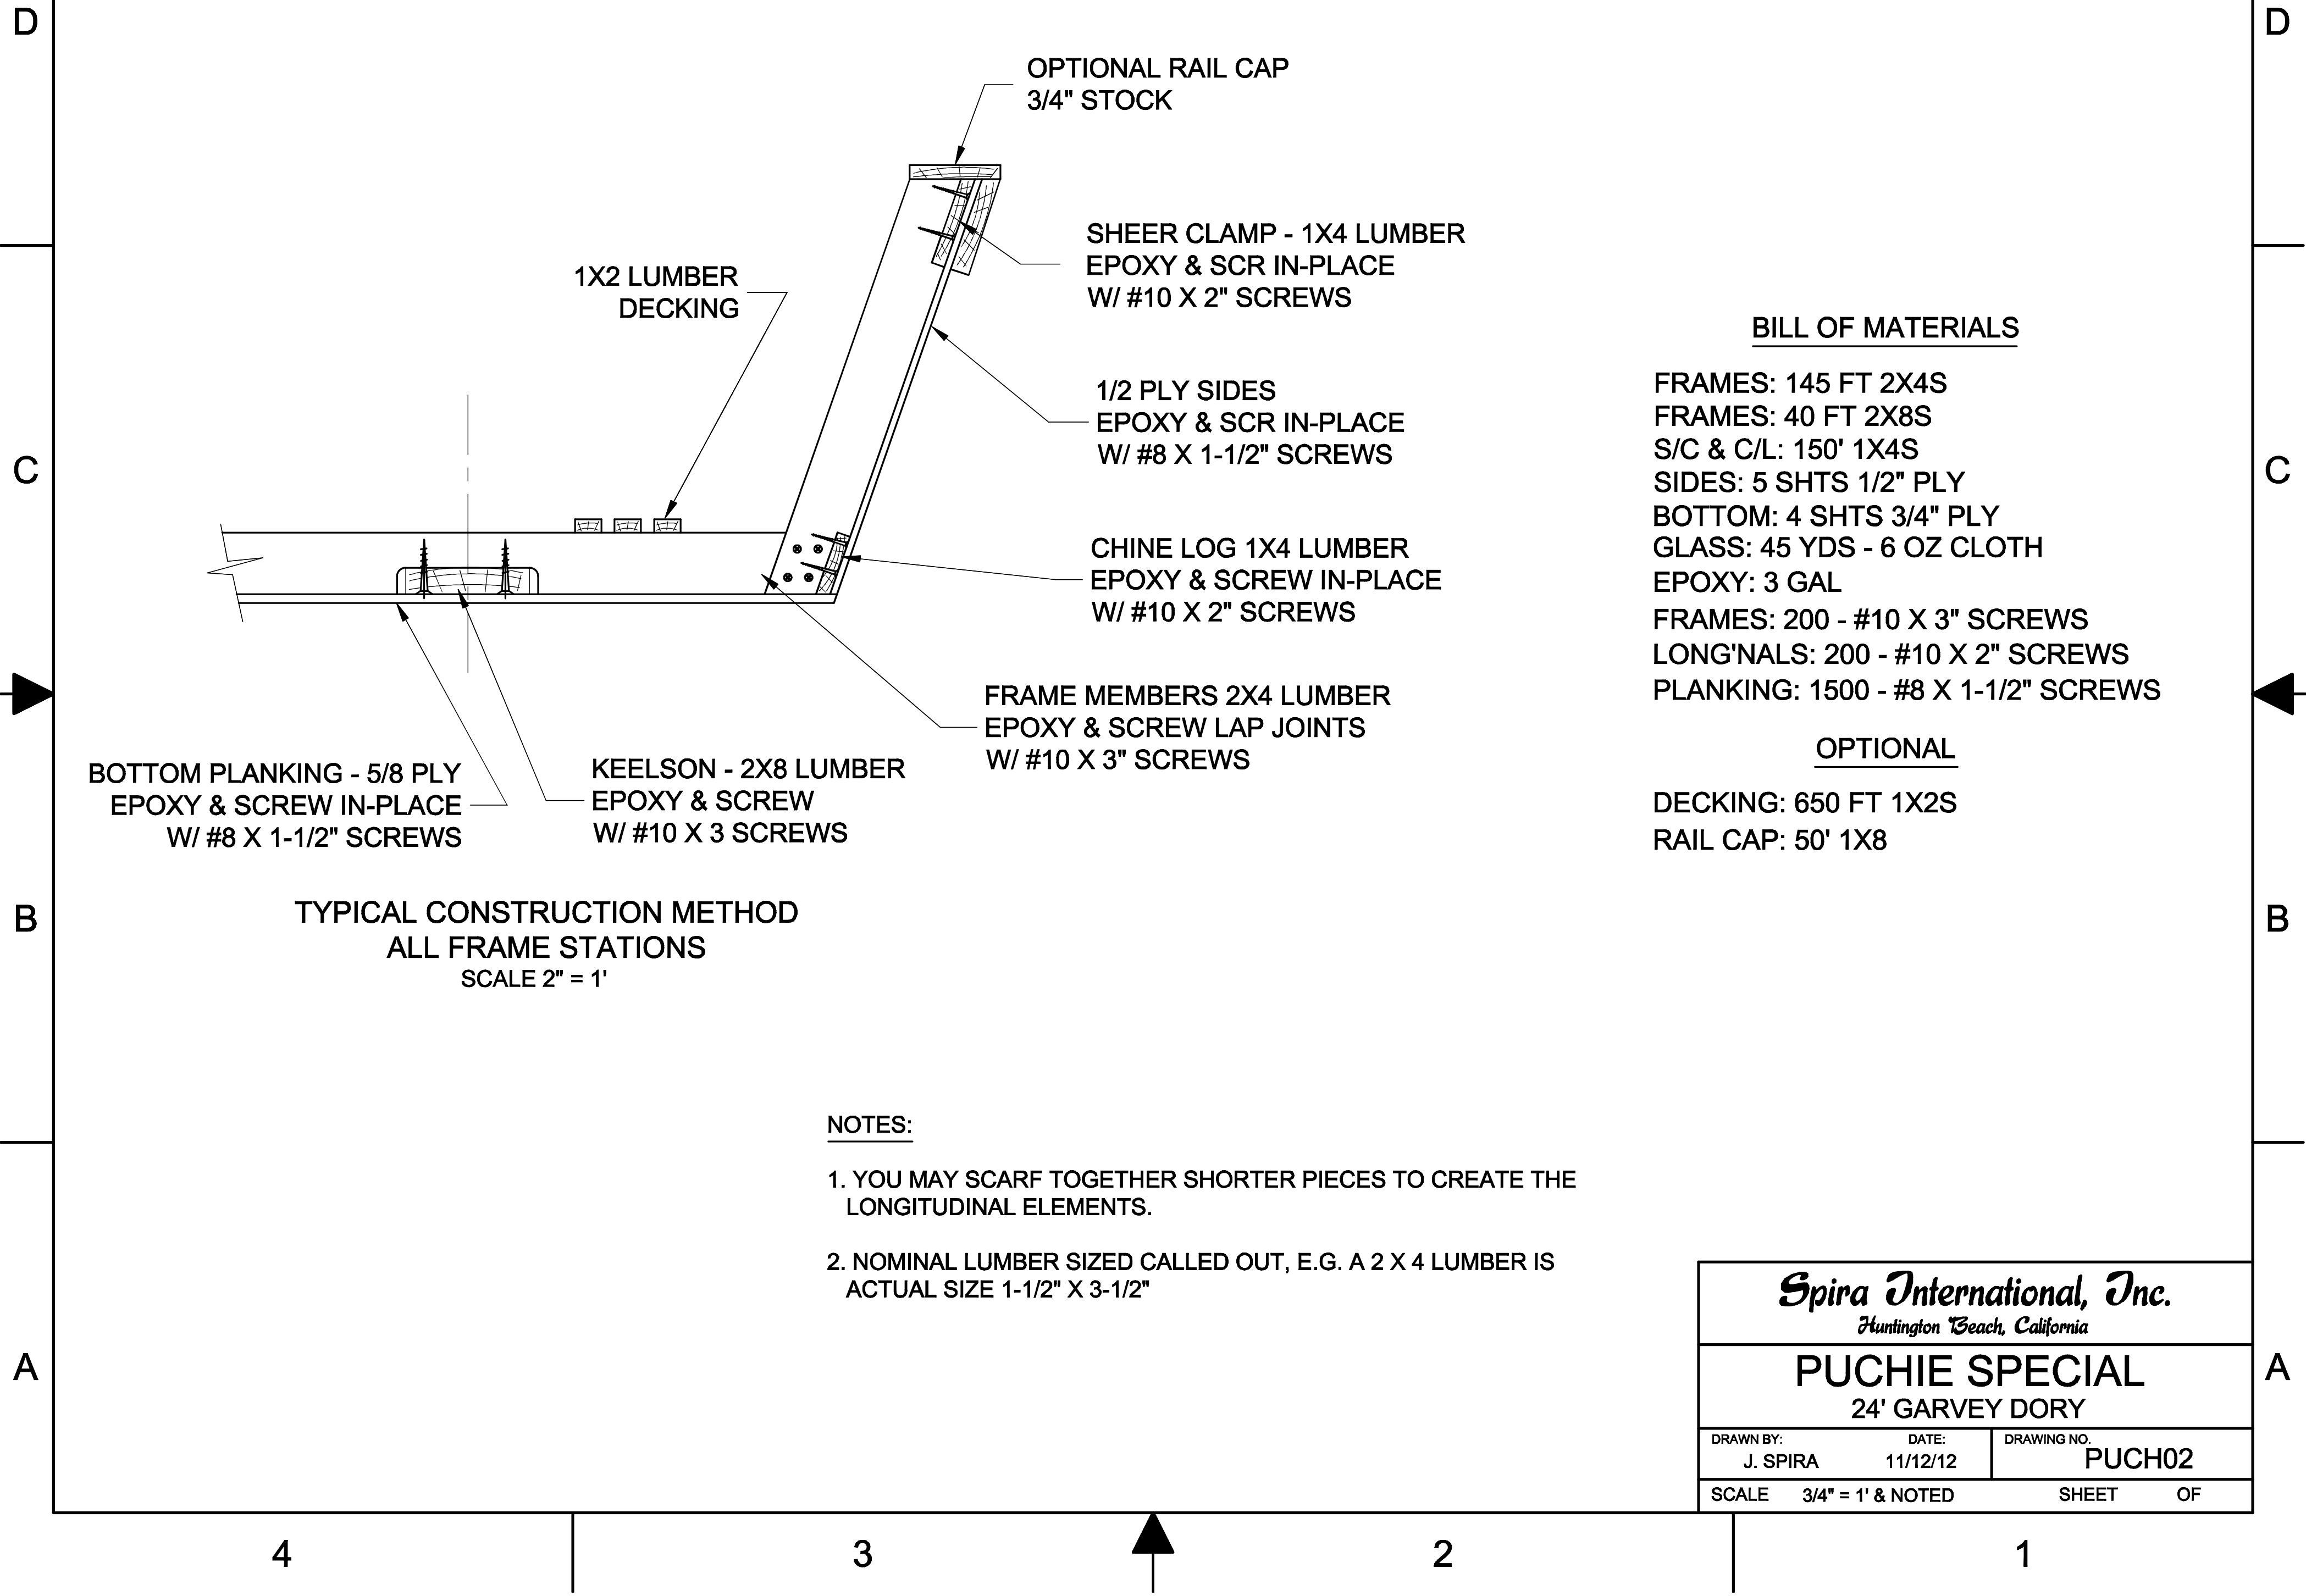

BILL OF MATERIALS

FRAMES: 145 FT 2X4S
FRAMES: 40 FT 2X8S
S/C & C/L: 150' 1X4S
SIDES: 5 SHTS 1/2" PLY
BOTTOM: 4 SHTS 3/4" PLY
GLASS: 45 YDS - 6 OZ CLOTH
EPOXY: 3 GAL
FRAMES: 200 - #10 X 3" SCREWS
LONG'NALS: 200 - #10 X 2" SCREWS
PLANKING: 1500 - #8 X 1-1/2" SCREWS

OPTIONAL

DECKING: 650 FT 1X2S
RAIL CAP: 50' 1X8

TYPICAL CONSTRUCTION METHOD
ALL FRAME STATIONS
SCALE 2" = 1'

- NOTES:
- 1. YOU MAY SCARF TOGETHER SHORTER PIECES TO CREATE THE LONGITUDINAL ELEMENTS.
 - 2. NOMINAL LUMBER SIZED CALLED OUT, E.G. A 2 X 4 LUMBER IS ACTUAL SIZE 1-1/2" X 3-1/2"

Spira International, Inc. <i>Huntington Beach, California</i>		
PUCHIE SPECIAL 24' GARVEY DORY		
DRAWN BY: J. SPIRA	DATE: 11/12/12	DRAWING NO. PUCH02
SCALE 3/4" = 1' & NOTED	SHEET OF	