

4

3


2

1

NOTICE

THIS DRAWING CONTAINS A PROPRIETARY DESIGN ASSIGNED TO SPIRA INTERNATIONAL, INC. ALL RIGHTS TO DUPLICATE, TRANSFER OR USE ARE EXPRESSLY RESERVED BY SPIRA INTERNATIONAL. THE BUYER IS LICENSED TO BUILD ONE ASSEMBLY FROM THESE PLANS.

REVISIONS				
ZONE	LTR	DESCRIPTION	DATE	APPROVED
	B	ADDED WL LENGTH	11/24/14	JJS

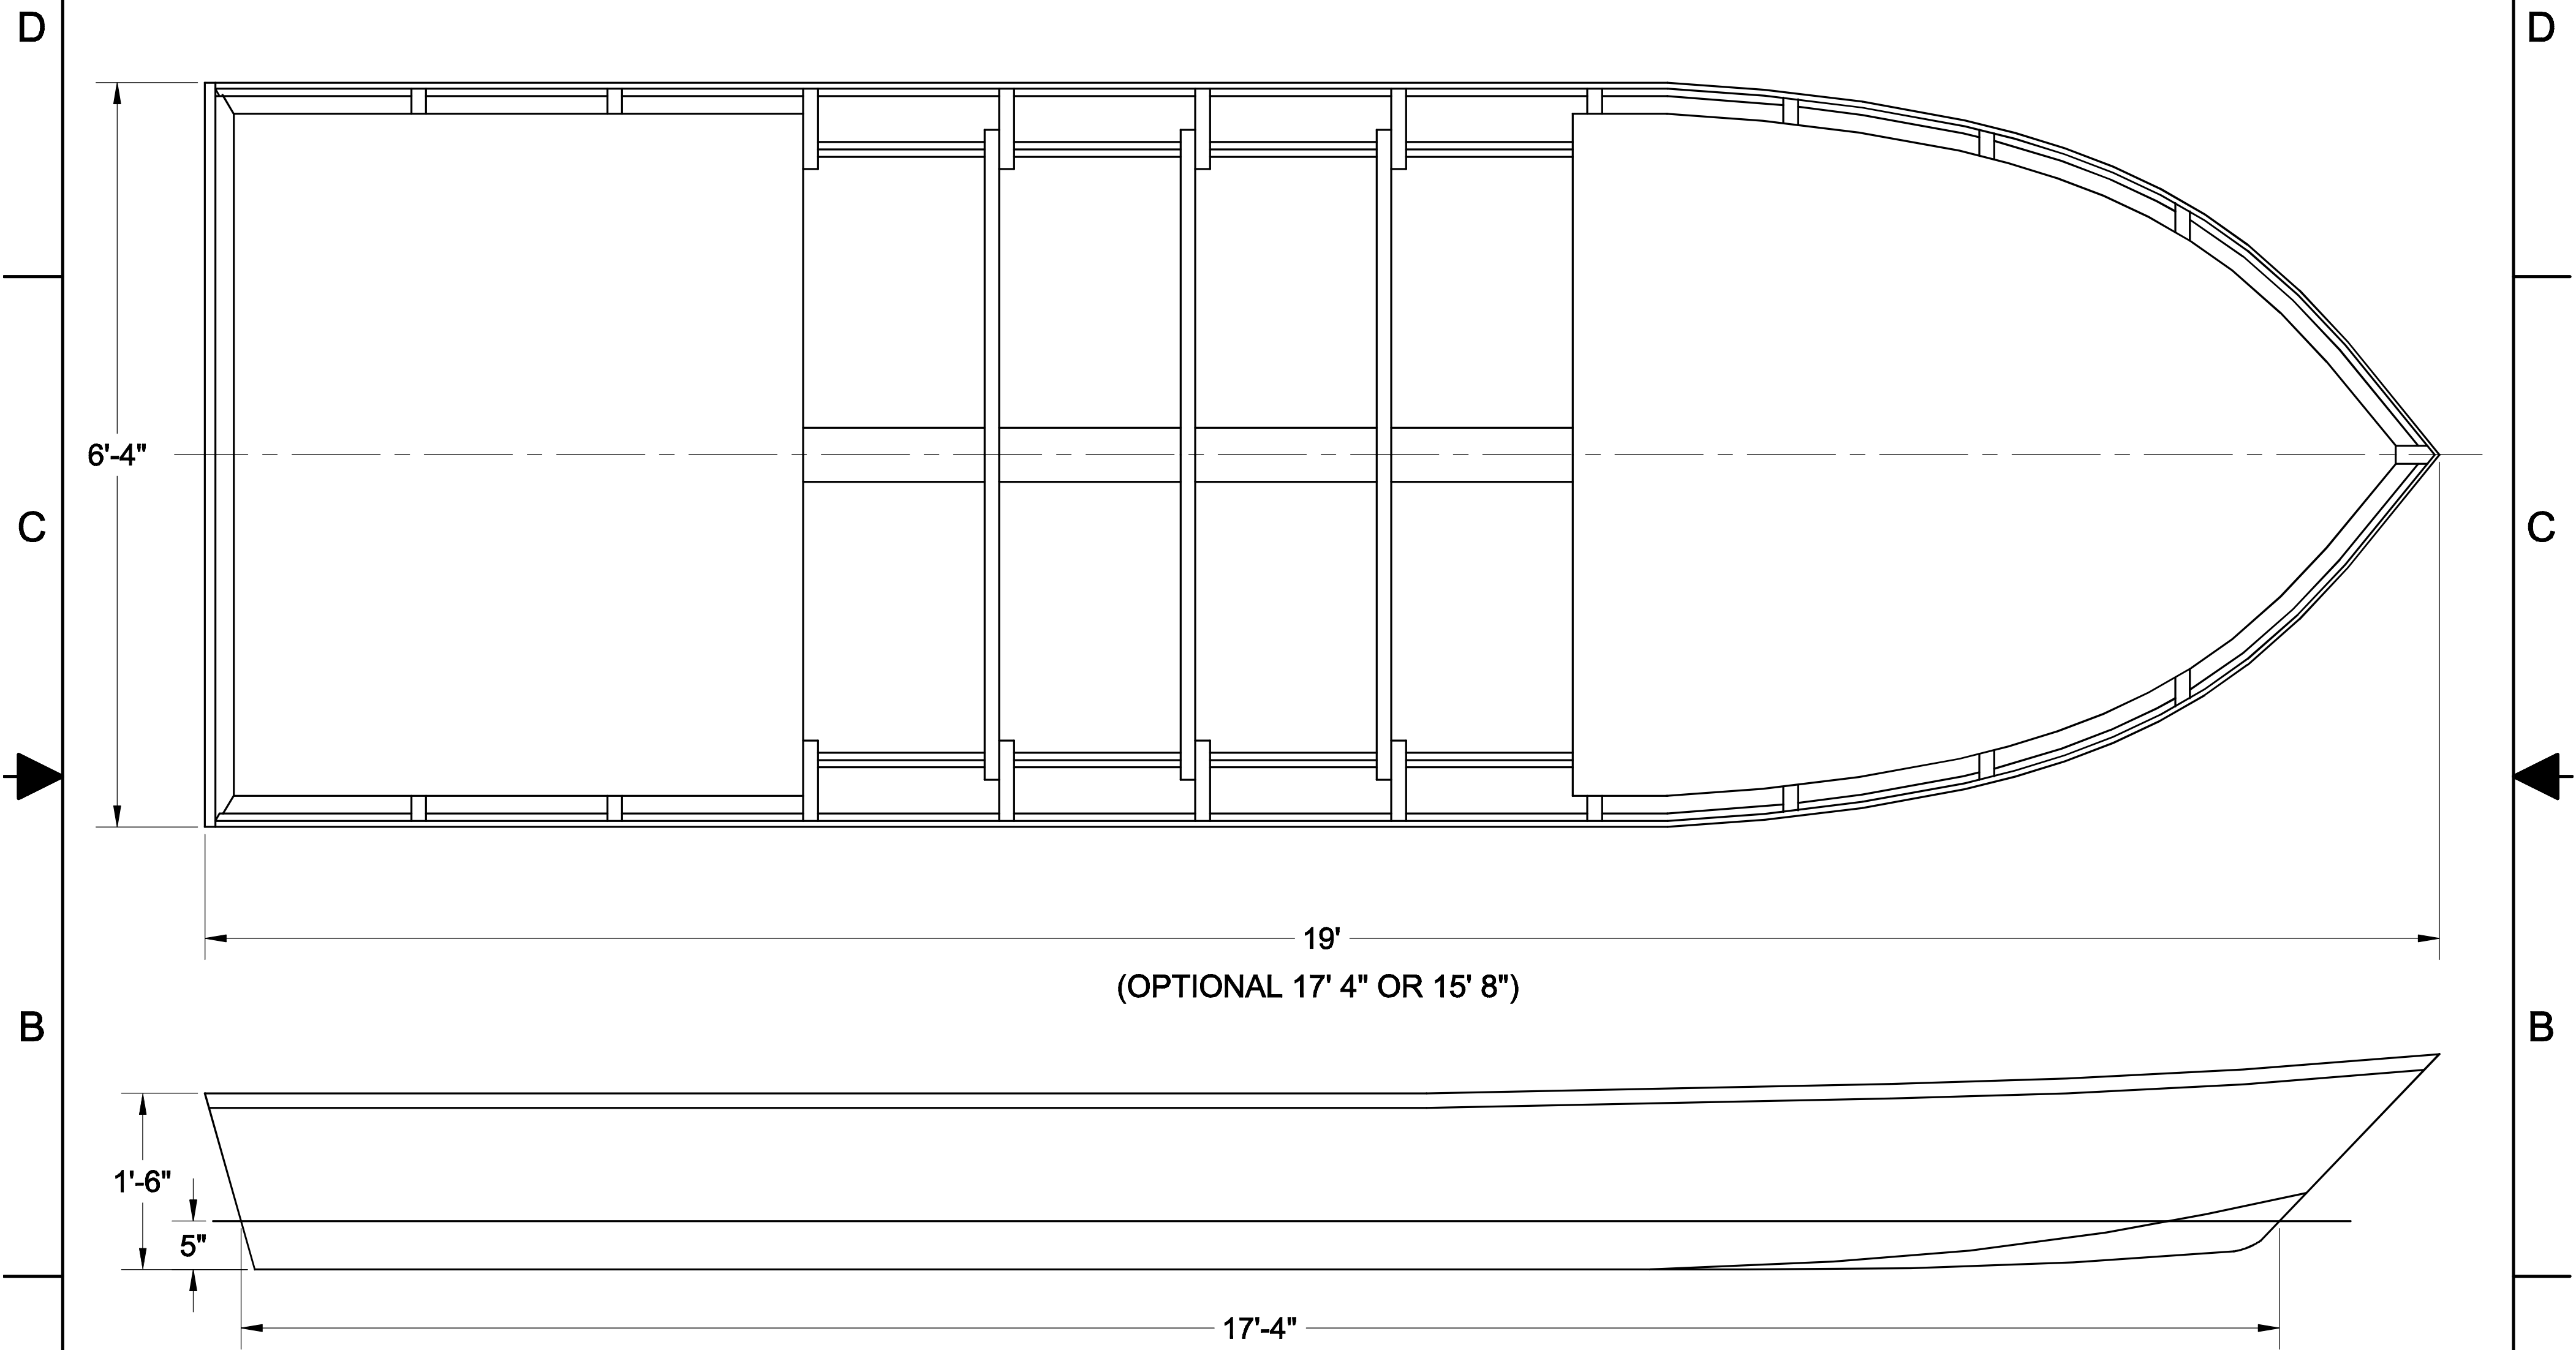

SPECIFICATIONS	
MAX. DISPLACEMENT	3360 LBS
HULL WEIGHT	740 LBS
CALC. MAX. HORSEPOWER	120 HP
RECOMMENDED HP	40 HP



Spira International, Inc.
Huntington Beach, California

SABINE
15-1/2', 17-1/2' OR 19' FLATS BOAT

DRAWN BY: J. SPIRA	DATE: 04/21/12	DRAWING NO. SABI01
SCALE 1" = 1'	SHEET	OF

4

3


2

1

NOTICE

THIS DRAWING CONTAINS A PROPRIETARY DESIGN ASSIGNED TO SPIRA INTERNATIONAL, INC. ALL RIGHTS TO DUPLICATE, TRANSFER OR USE ARE EXPRESSLY RESERVED BY SPIRA INTERNATIONAL. THE BUYER IS LICENSED TO BUILD ONE ASSEMBLY FROM THESE PLANS.

REVISIONS				
ZONE	LTR	DESCRIPTION	DATE	APPROVED

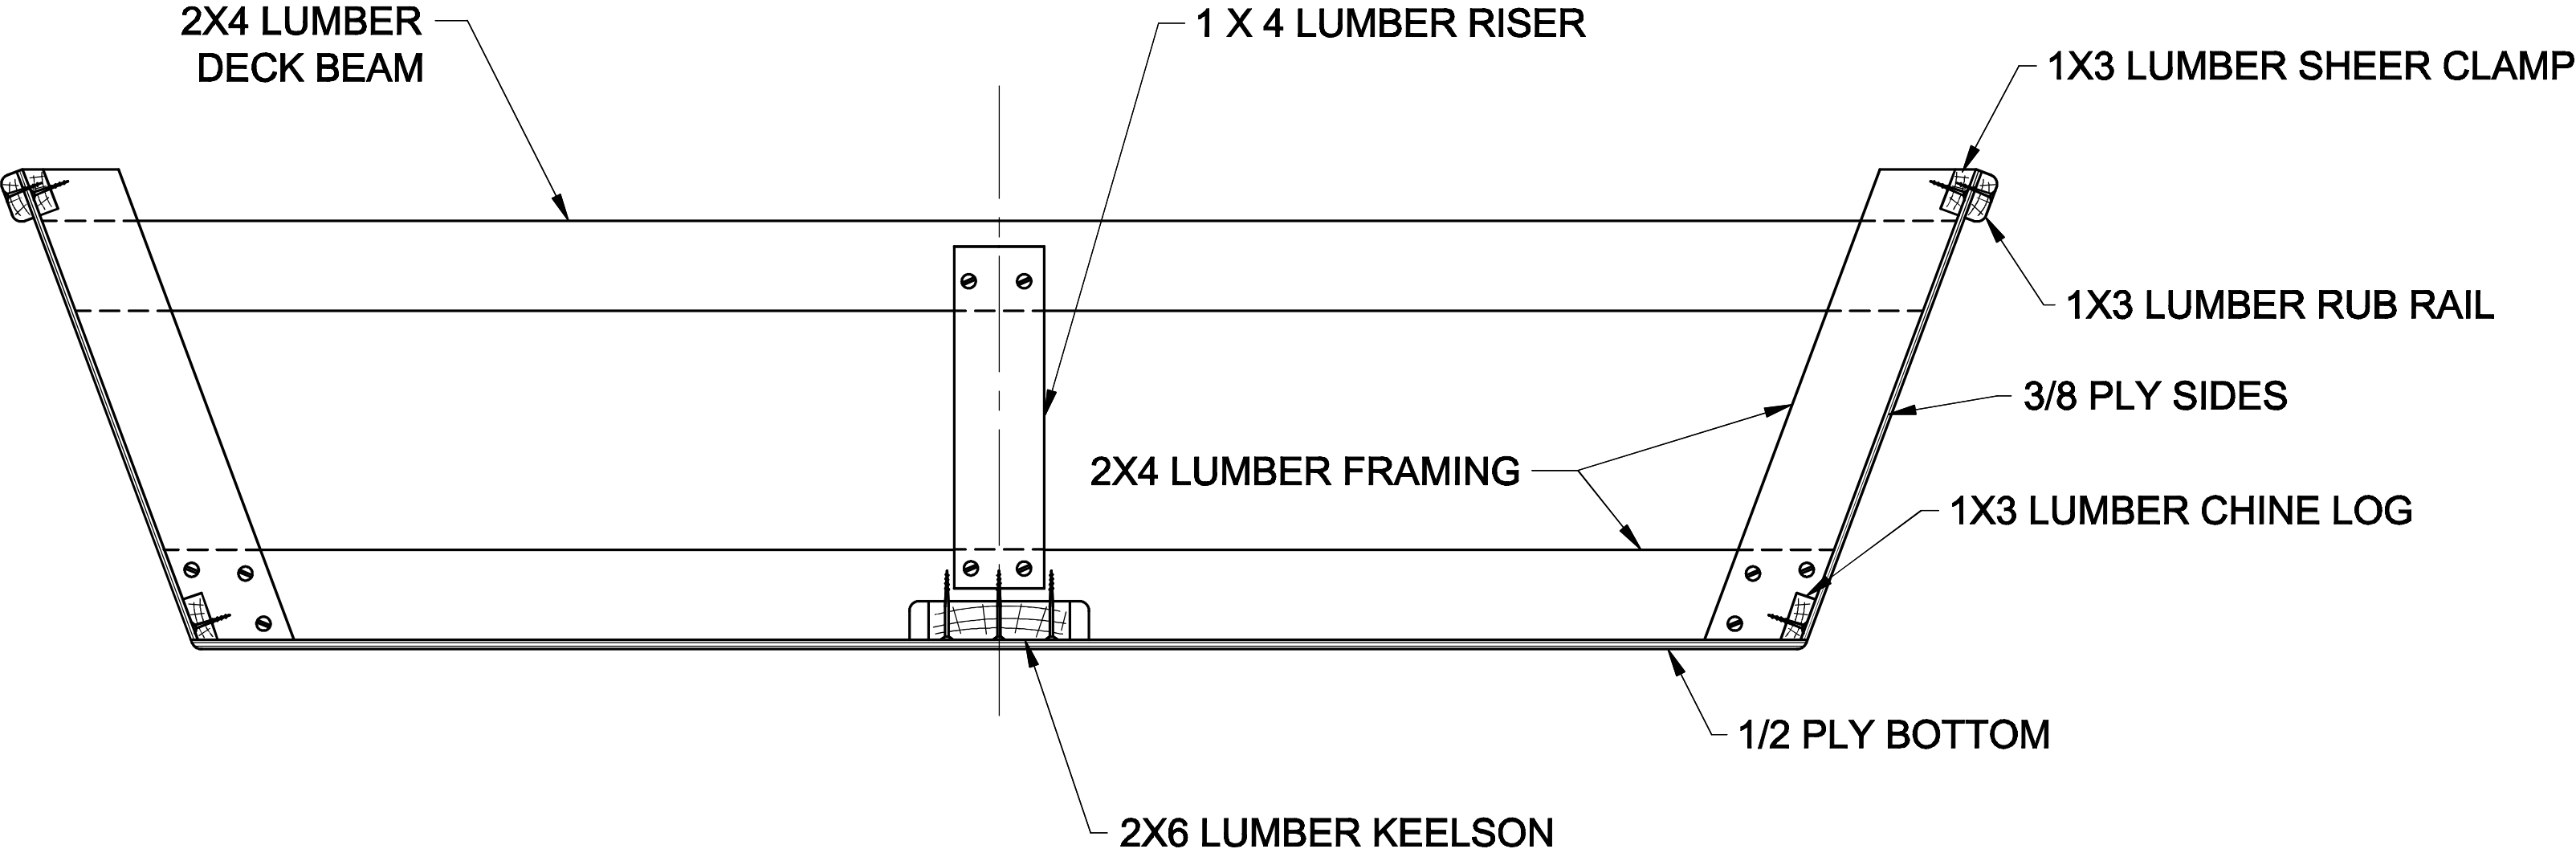

TYPICAL CONSTRUCTION

FASTENING SCHEDULE

FRAME TO FRAME: #10 X 2-1/2 DECK SCREWS
LONGITUDINAL TO FRAME: #8 X 2 DECK SCREWS
PLANKING TO FRAME: #8 X 1-1/4 DECK SCREWS

BILL OF MATERIALS

4 SHEETS 3/8" PLY FOR SIDES
4 SHEETS 1/2" PLY FOR BOTTOM
110' 2X4 LUMBER FOR FRAMES
120' 1X3 LUMBER FOR SHEER CLAMP
CHINE LOG AND RUB RAILS
16' 2X8 LUMBER FOR STEM & TRANSOM
18' 2X6 LUMBER FOR KEELSON
12' 1X4 LUMBER FOR DECK RISERS
100 #8 X 2-1/2" DECK SCREWS
200 #8 X 2 DECK SCREWS
500 #8 X 1-1/4 DECK SCREWS
2 GAL EPOXY RESIN
24 YDS 6 OZ FIBERGLASS CLOTH

NOTES:

1. YOU MAY SCARF TOGETHER SHORTER PIECES TO CREATE THE LONGITUDINAL ELEMENTS.
2. NOMINAL LUMBER SIZED CALLED OUT, E.G. A 2 X 4 LUMBER IS ACTUAL SIZE 1-1/2" X 3-1/2"



Spira International, Inc.
Huntington Beach, California

SABINE

15-1/2', 17-1/2' OR 19' FLATS BOAT

DRAWN BY: J. SPIRA	DATE: 04/21/12	DRAWING NO. SABI02
SCALE 2" = 1'	SHEET	OF