

4

3


2

1

NOTICE

THIS DRAWING CONTAINS A PROPRIETARY DESIGN ASSIGNED TO SPIRA INTERNATIONAL, INC. ALL RIGHTS TO DUPLICATE, TRANSFER OR USE ARE EXPRESSLY RESERVED BY SPIRA INTERNATIONAL. THE BUYER IS LICENSED TO BUILD ONE ASSEMBLY FROM THESE PLANS.


REVISIONS				
ZONE	LTR	DESCRIPTION	DATE	APPROVED

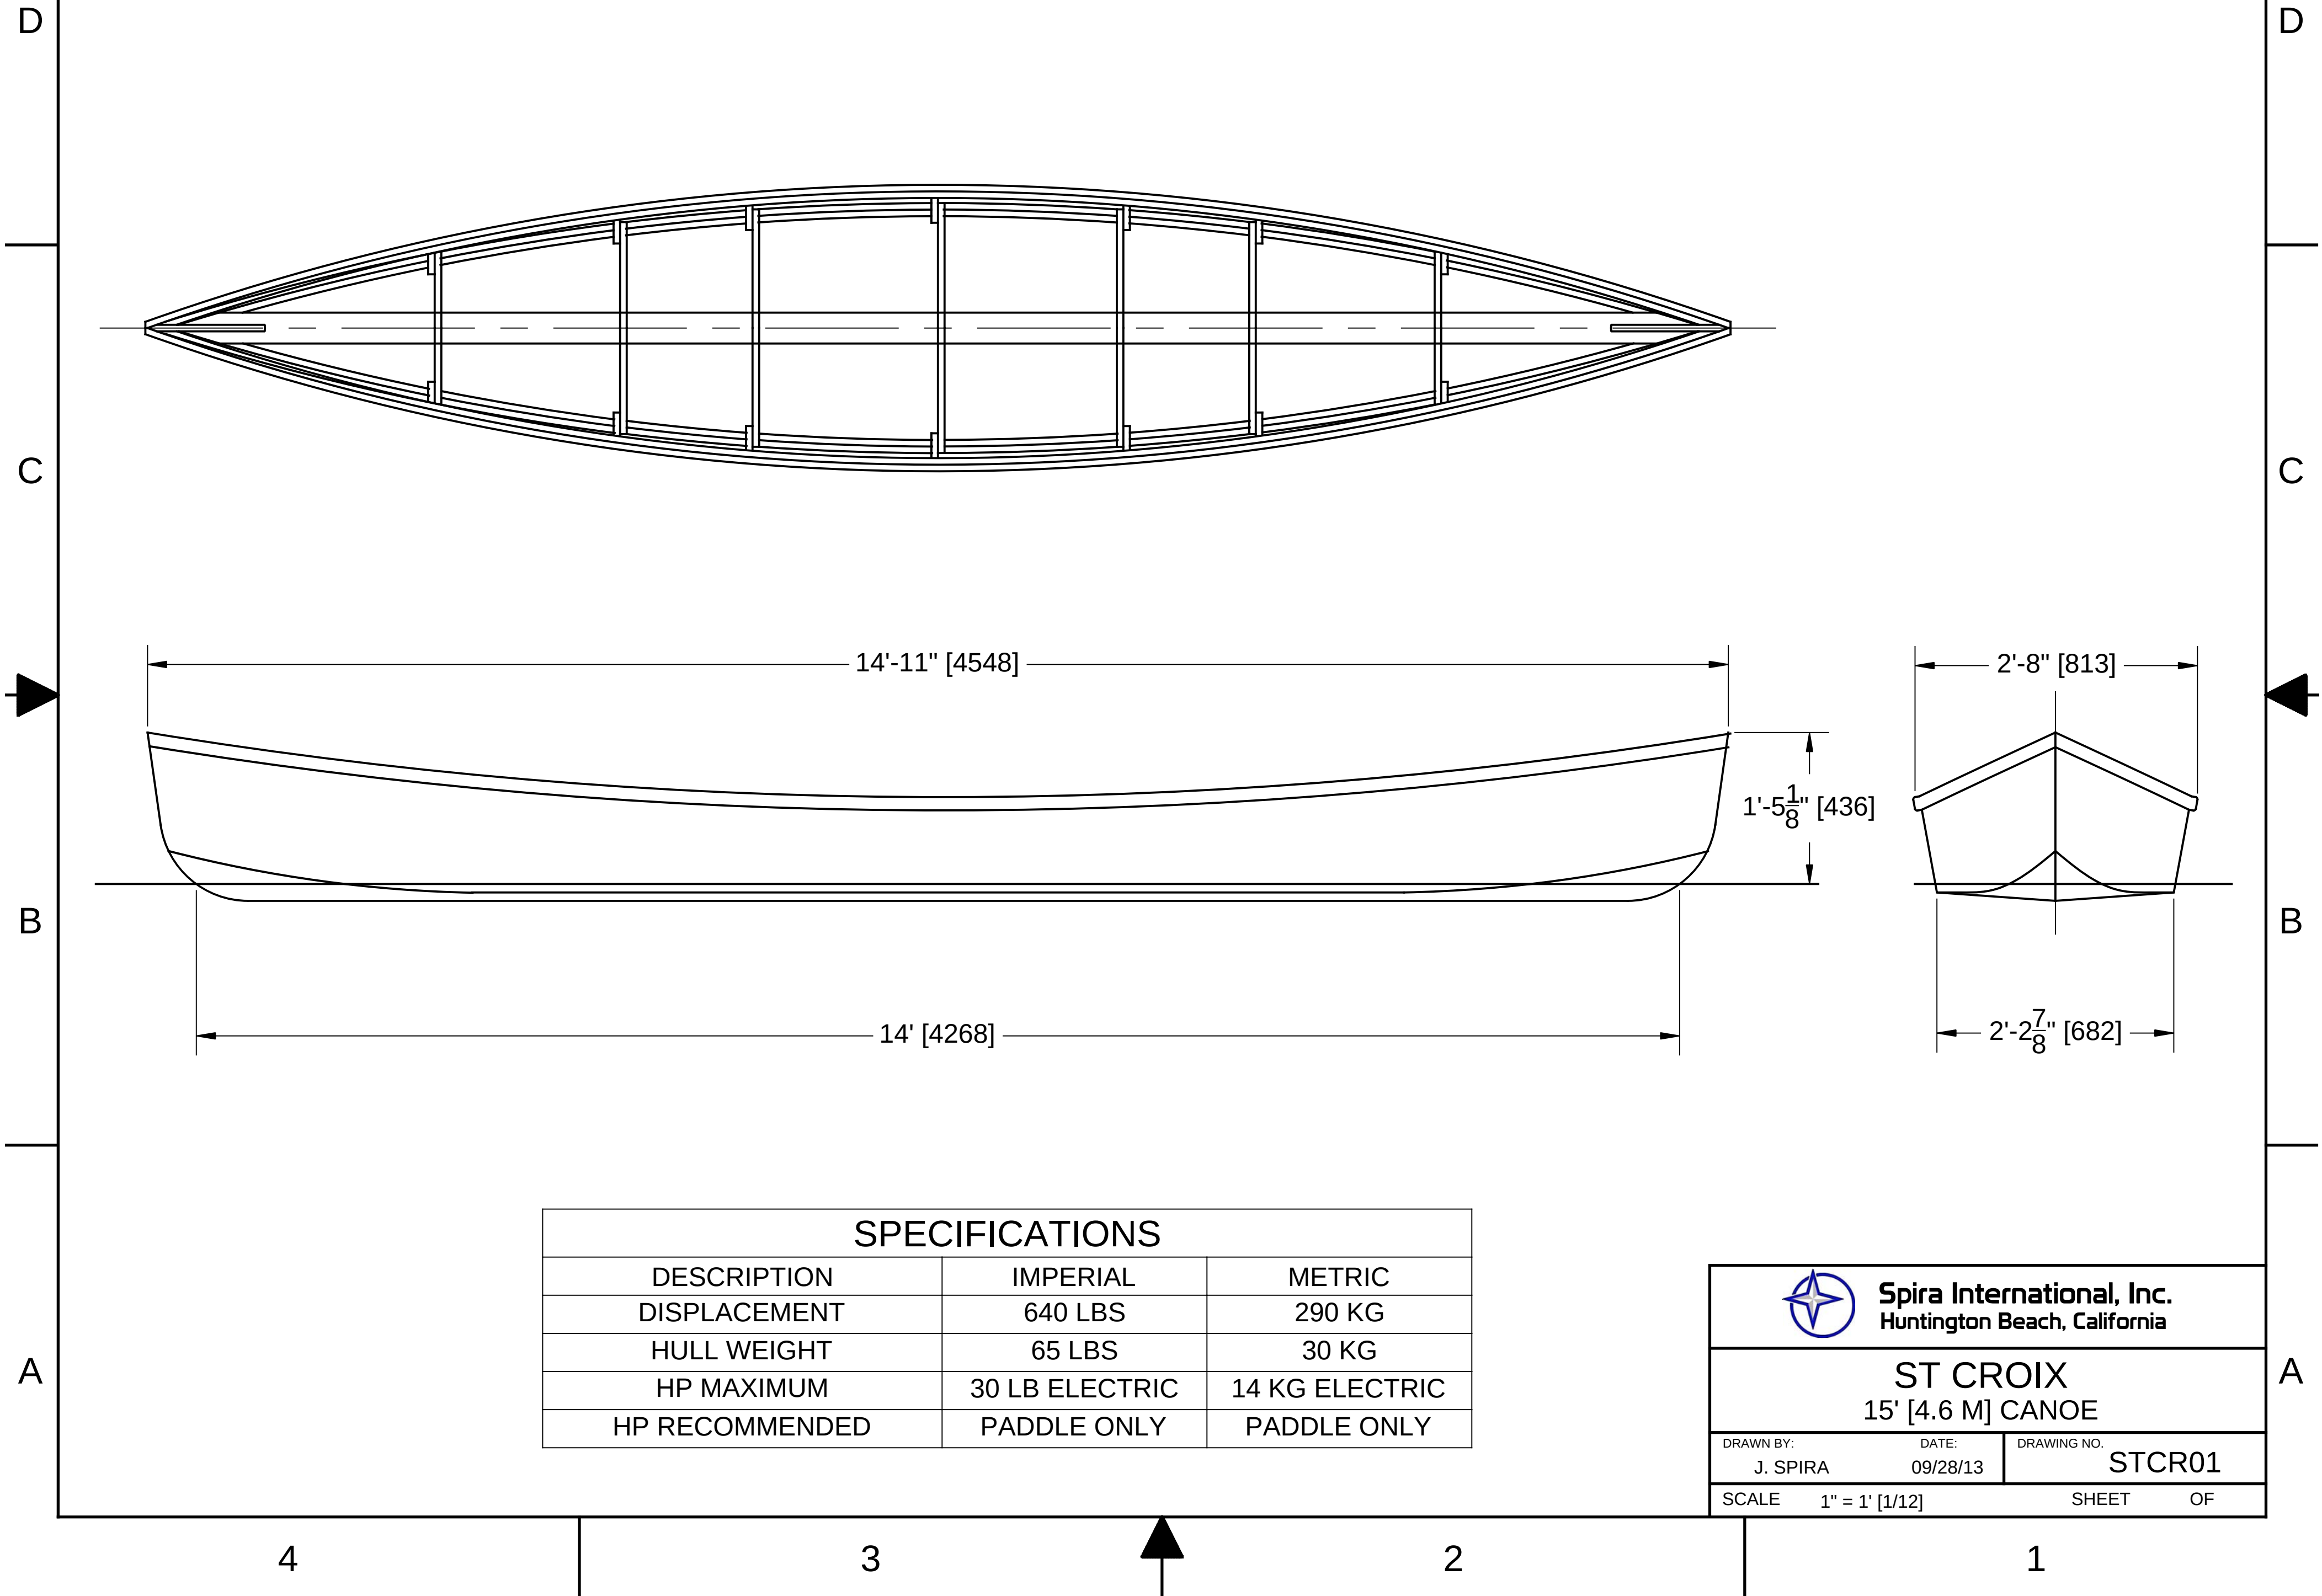


4 3 2 1

NOTICE
THIS DRAWING CONTAINS A PROPRIETARY DESIGN ASSIGNED TO SPIRA INTERNATIONAL, INC. ALL RIGHTS TO DUPLICATE, TRANSFER OR USE ARE EXPRESSLY RESERVED BY SPIRA INTERNATIONAL. THE BUYER IS LICENSED TO BUILD ONE ASSEMBLY FROM THESE PLANS.

REVISIONS				
ZONE	LTR	DESCRIPTION	DATE	APPROVED

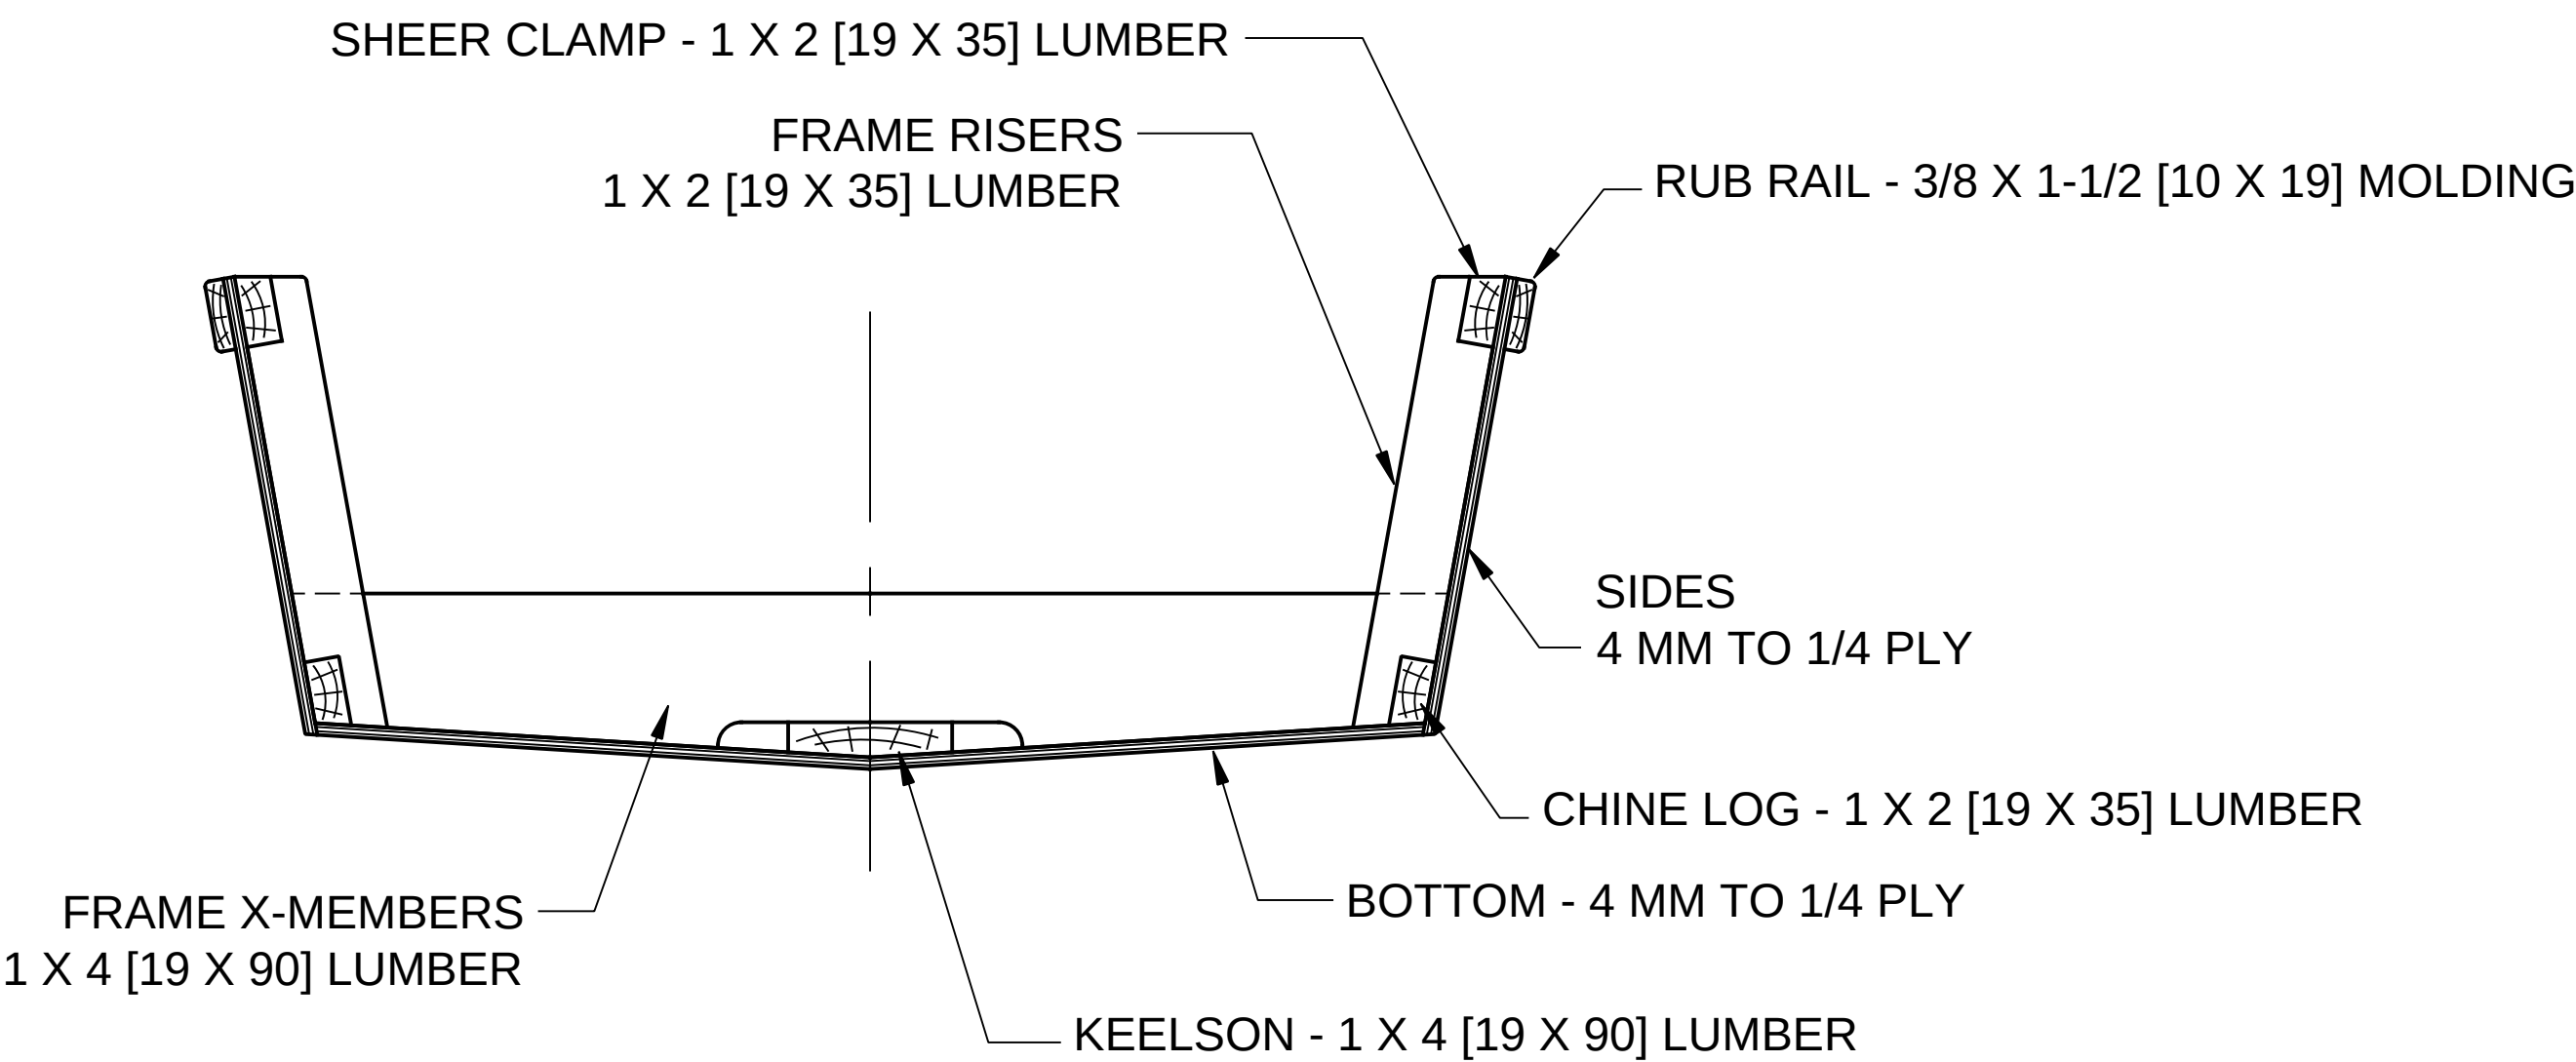

CROSS SECTION
TYPICAL

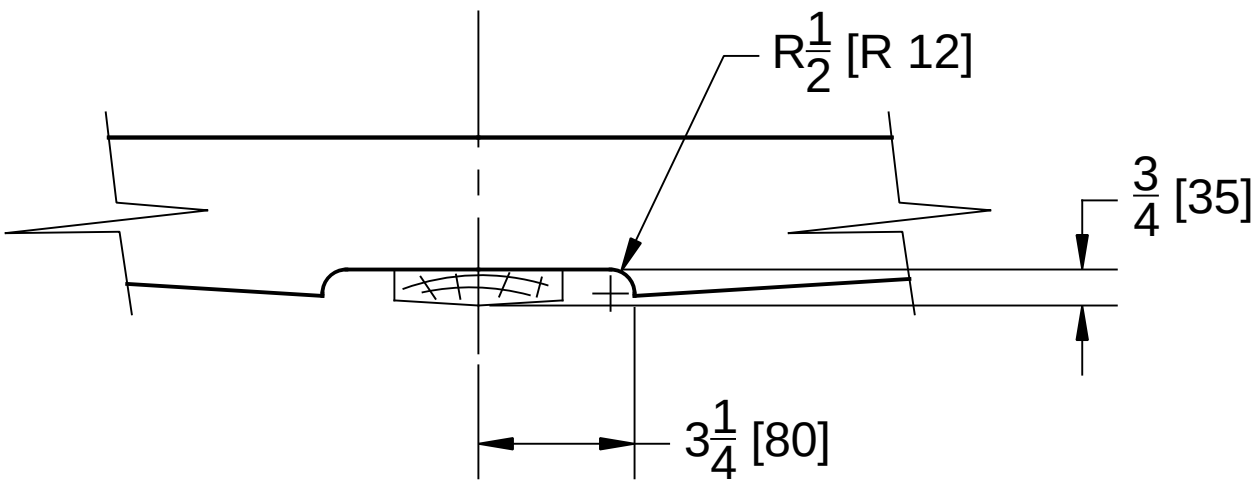

KEELSON CUTOUT
TYPICAL - ALL FRAMES

BILL OF MATERIALS

- 4 SHEETS - 5MM, 6MM OR 1/4 PLY
30' [10M] - 1 X 4 [19 x 90] LUMBER (KEELSON & FRAMES)
32' [10M] - 3/8 X 1-1/2 [10 x 19] MOLDINGS (RUB RAIL)
12' [3 M] - 1 X 2 [19 X 35] LUMBER (FRAMING)
4' [1M] - 1 X 6 [19 X 140] LUMBER (STEMS)
50 - #8 X 2 [M4 X 50] DECK SCREWS (FRAMING)
150 - #6 X 1-1/4 [M3 X 35] DECK SCREWS (PLANKING)
3 QT [3L] - EPOXY RESIN
14 YDS [14 M] - 50" [1250 MM] WIDE 6 OZ F'GLASS CLOTH

NOTES:

1. YOU MAY SCARF TOGETHER SHORTER PIECES TO CREATE THE LONGITUDINAL ELEMENTS.
2. NOMINAL LUMBER SIZED CALLED OUT, E.G. A 2 X 4 LUMBER IS ACTUAL SIZE 1-1/2" X 3-1/2" (MOLDINGS ACTUAL SIZES)



Spira International, Inc.
Huntington Beach, California

ST CROIX
15' [4.6 M] CANOE

DRAWN BY:
J. SPIRA

DATE:
09/28/13

DRAWING NO.
STCR02

SCALE 1" = 1' [1/12]

SHEET OF