

4

3

2

1


NOTICE

THIS DRAWING CONTAINS A PROPRIETARY DESIGN ASSIGNED TO SPIRA INTERNATIONAL, INC. ALL RIGHTS TO DUPLICATE, TRANSFER OR USE ARE EXPRESSLY RESERVED BY SPIRA INTERNATIONAL. THE BUYER IS LICENSED TO BUILD ONE ASSEMBLY FROM THESE PLANS.

REVISIONS				
ZONE	LTR	DESCRIPTION	DATE	APPROVED

SPECIFICATIONS	
MAX. DISPLACEMENT	800 [364 KG] LBS
HULL WEIGHT	209 LBS
MAXIMUM AUX POWER	2-1/2 HP
RECOMMENDED AUX POWER	40 LB ELECTRIC

SAIL PLAN: STANDARD SUNFISH SAIL AND SPARS,
LATEEN RIG, 75 SQ FT.

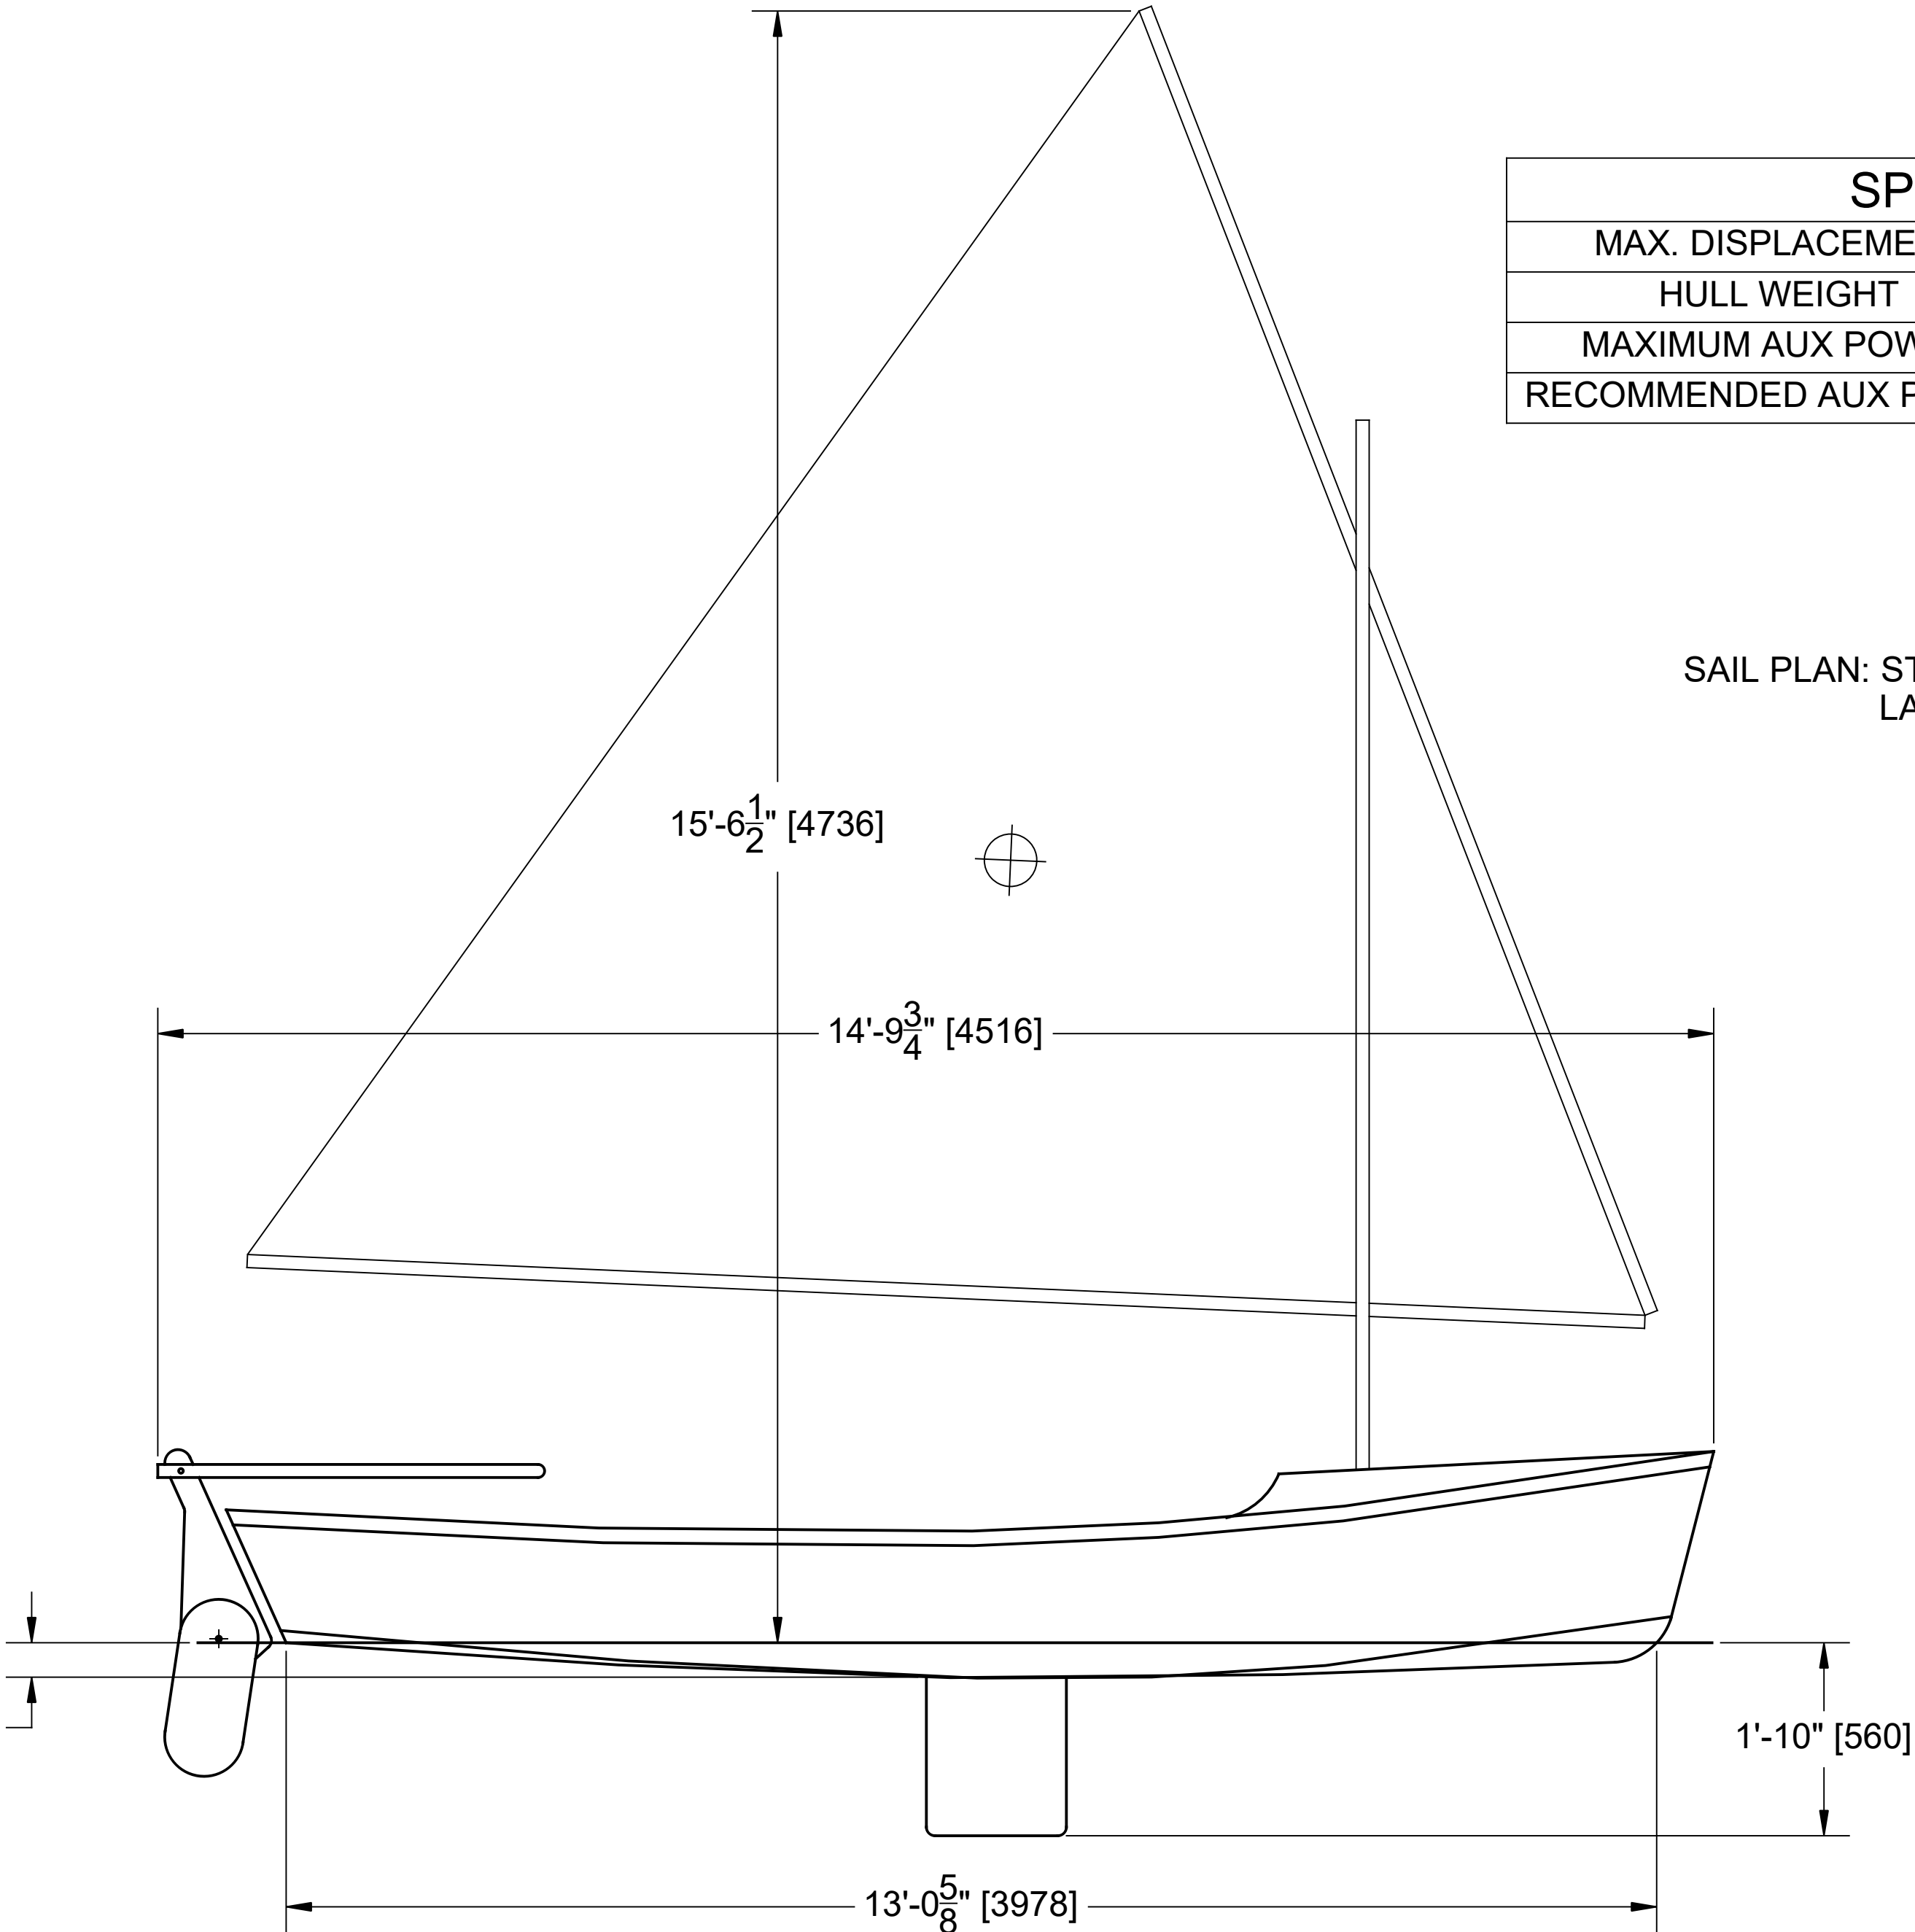



Spira International, Inc.
Huntington Beach, California

ARANSAS
13' [4.0M] SAILING SKIPJACK/SHARPIE

DRAWN BY:
J. SPIRA

DATE:
09/20/12

DRAWING NO.
ARAN01

SCALE 1" = 1' [1/12]SHEET OF

4

3

2

1

NOTICE


THIS DRAWING CONTAINS A PROPRIETARY DESIGN ASSIGNED TO SPIRA INTERNATIONAL, INC. ALL RIGHTS TO DUPLICATE, TRANSFER OR USE ARE EXPRESSLY RESERVED BY SPIRA INTERNATIONAL. THE BUYER IS LICENSED TO BUILD ONE ASSEMBLY FROM THESE PLANS.

REVISIONS

ZONE	LTR	DESCRIPTION	DATE	APPROVED

D

D

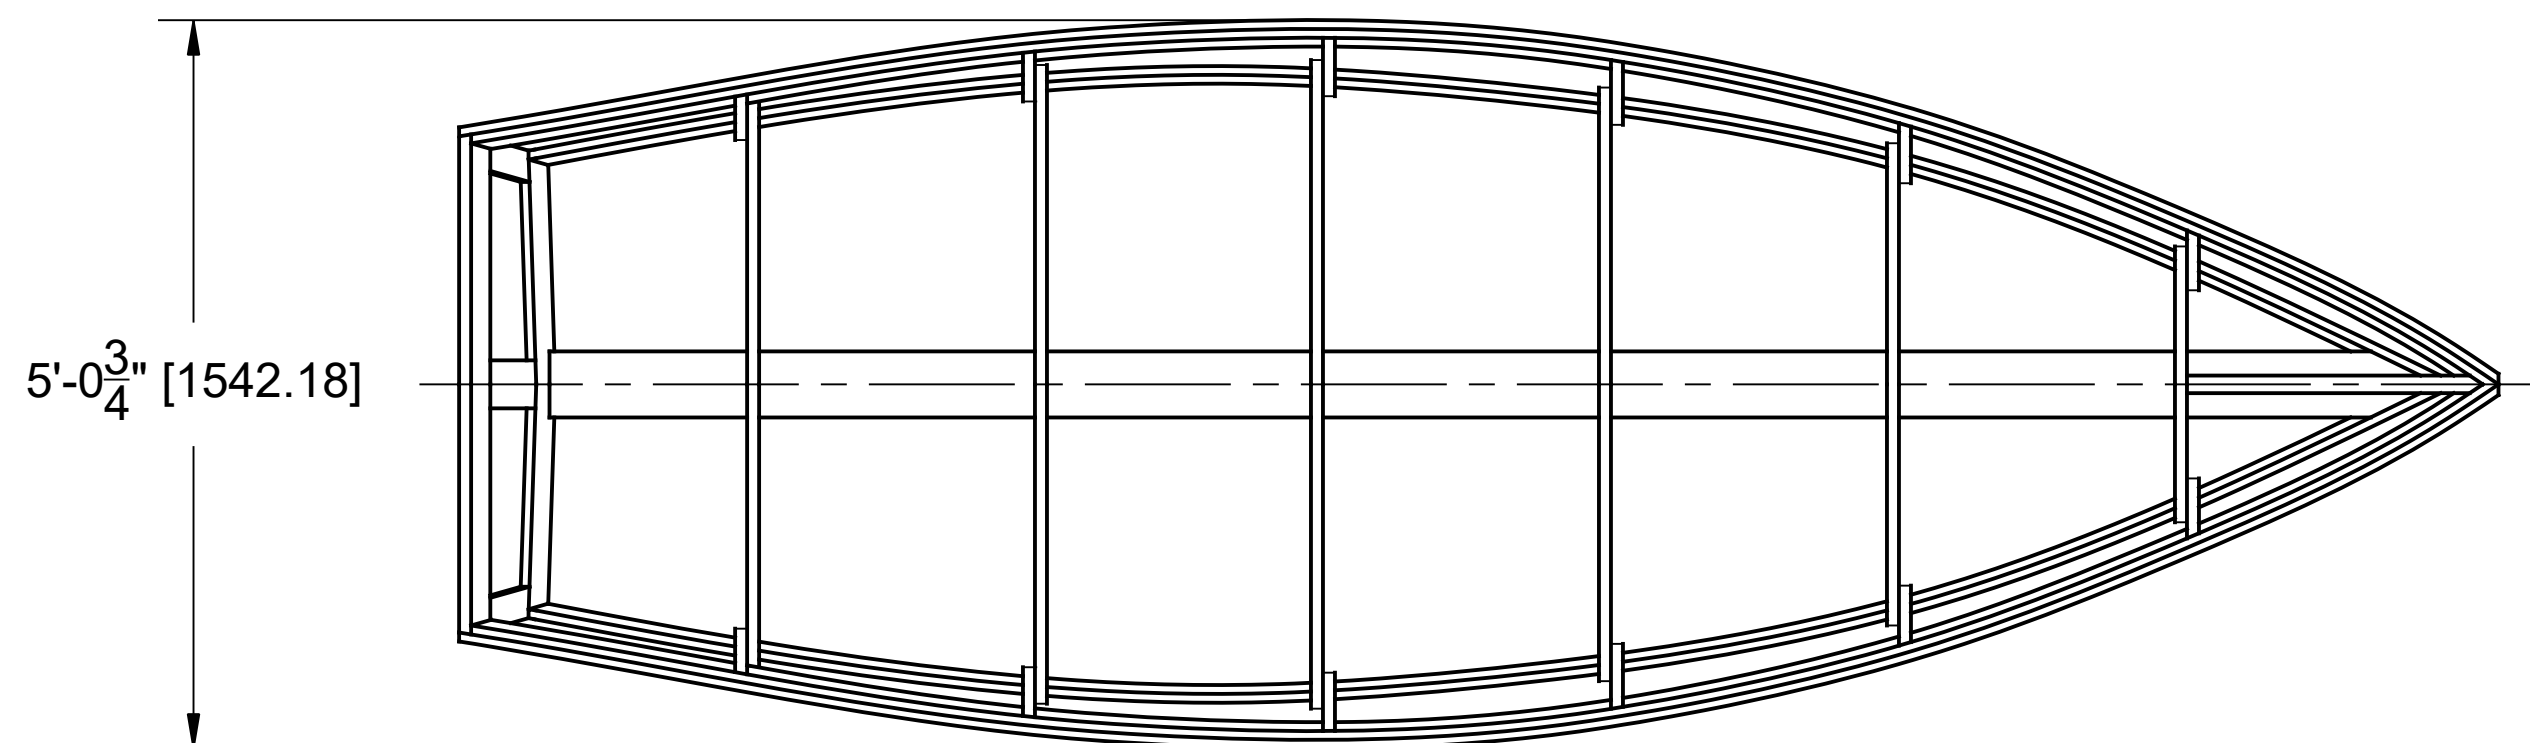



C

C



B

B

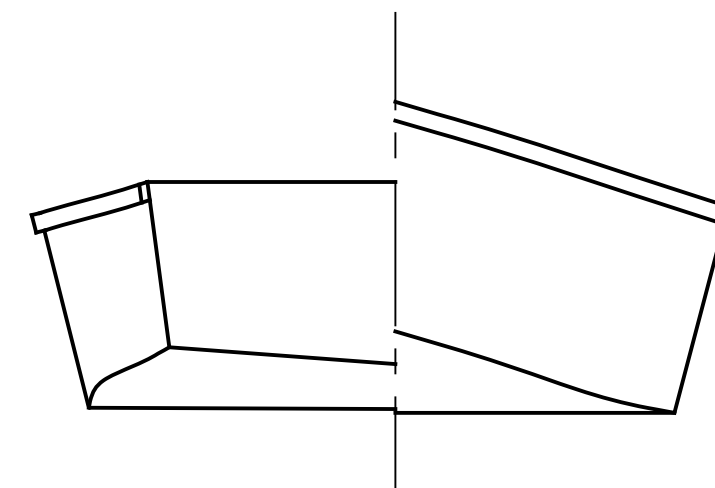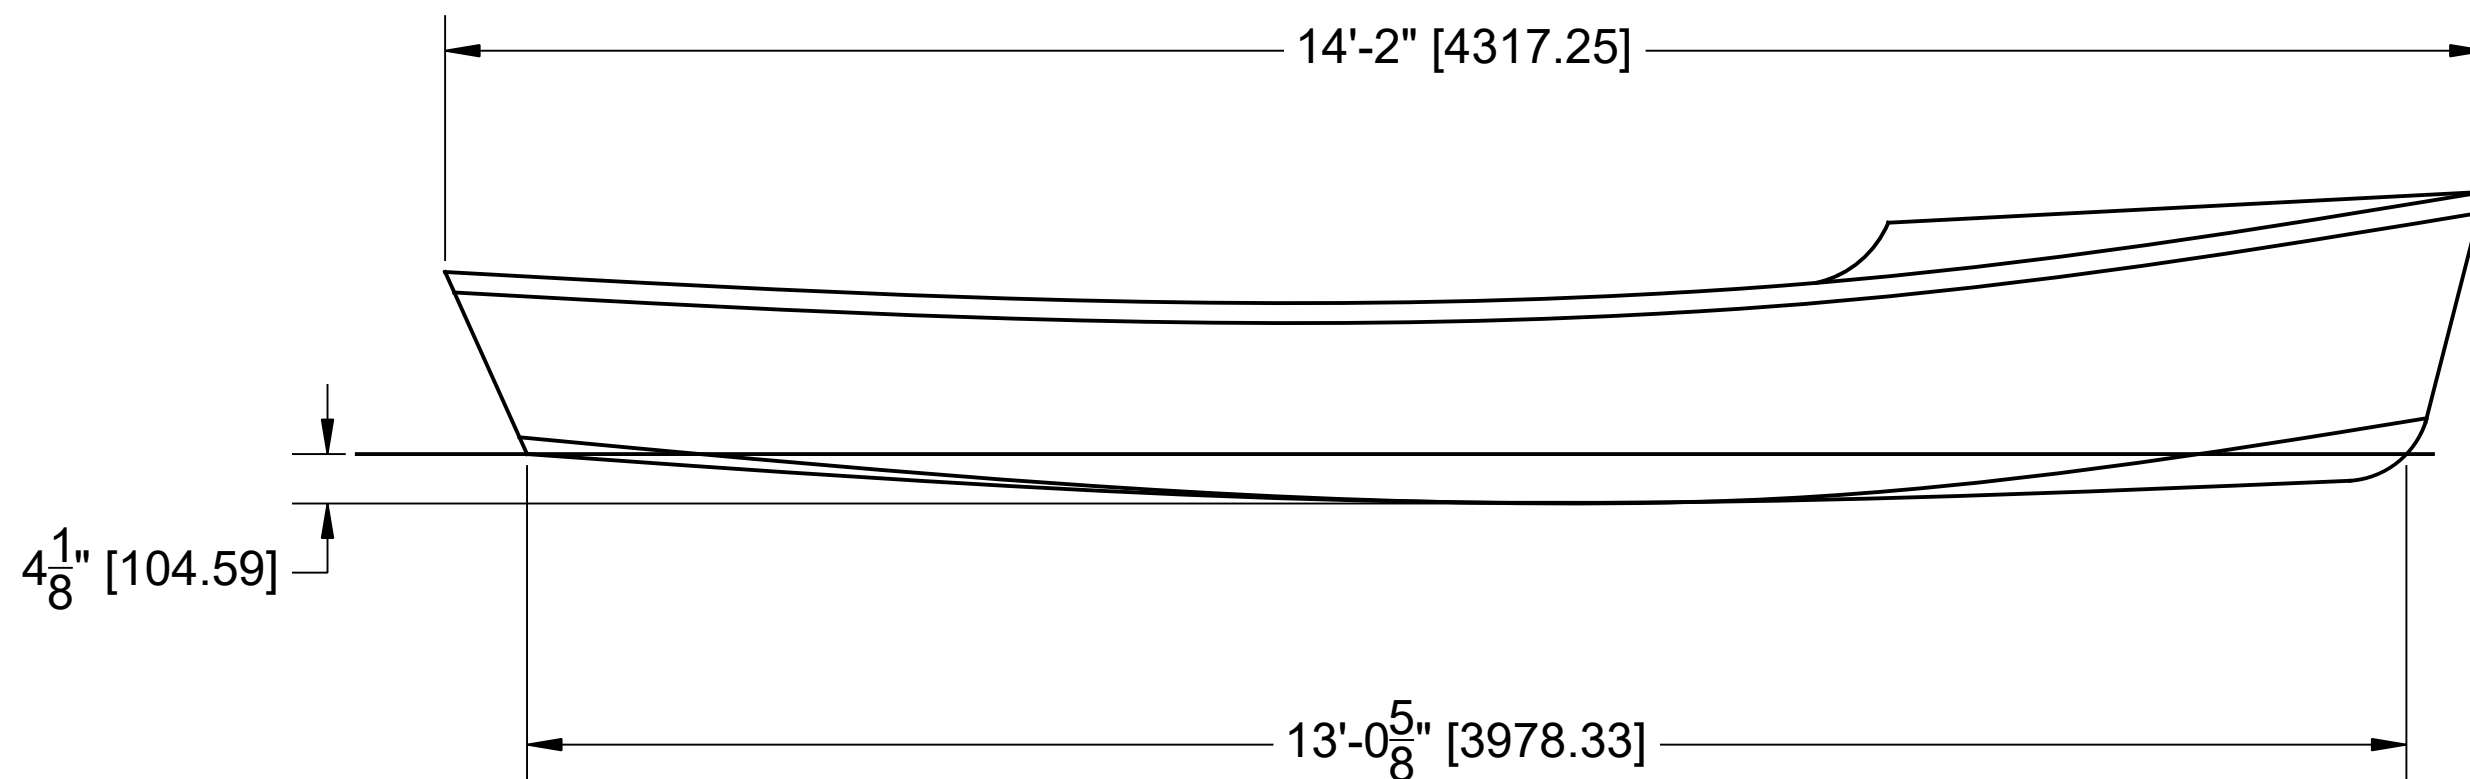

A

A

4

3

2

1



Spira International, Inc.
Huntington Beach, California

ARANSAS
13' [4.0M] SAILING SKIPJACK/SHARPIE

DRAWN BY: J. SPIRA	DATE: 09/20/12	DRAWING NO. ARAN02
-----------------------	-------------------	------------------------------

SCALE 1" = 1' [1/12]	SHEET OF
----------------------	----------

4

3


2

1

NOTICE

THIS DRAWING CONTAINS A PROPRIETARY DESIGN ASSIGNED TO SPIRA INTERNATIONAL, INC. ALL RIGHTS TO DUPLICATE, TRANSFER OR USE ARE EXPRESSLY RESERVED BY SPIRA INTERNATIONAL. THE BUYER IS LICENSED TO BUILD ONE ASSEMBLY FROM THESE PLANS.

REVISIONS				
ZONE	LTR	DESCRIPTION	DATE	APPROVED

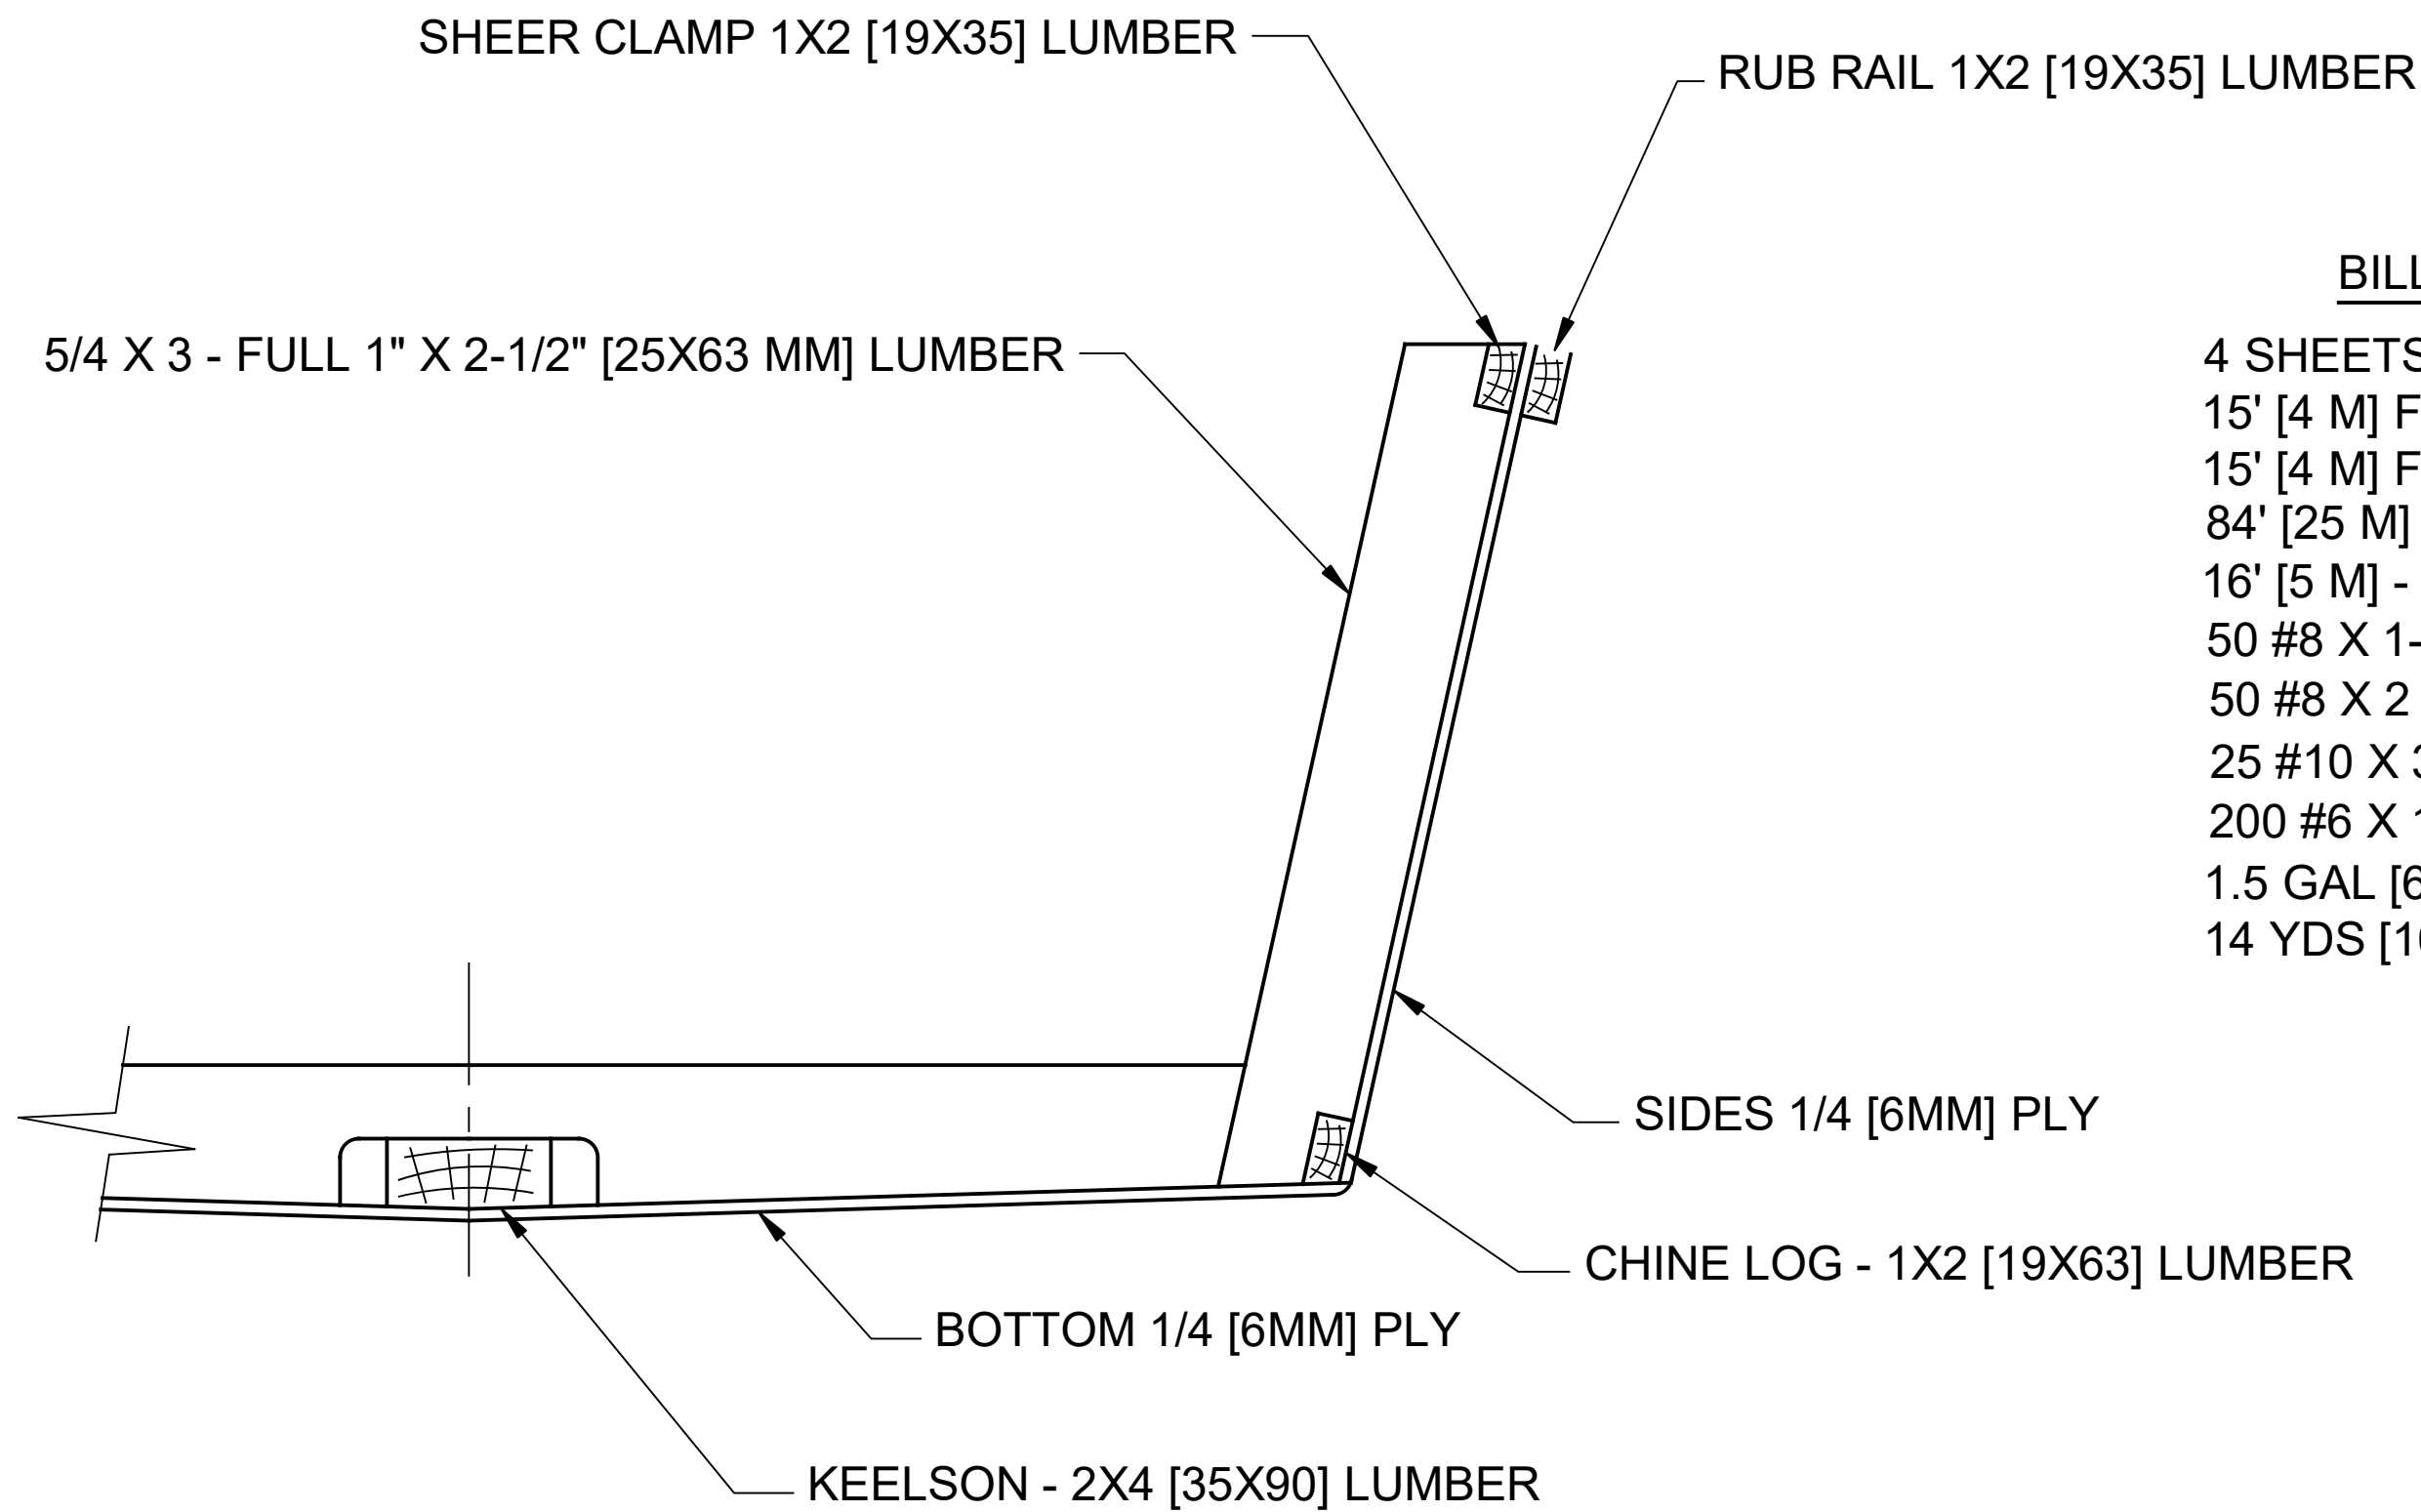

BILL OF MATERIALS

4 SHEETS 1/4 [6MM] PLY
15' [4 M] FULL 1 X 6 [25 X 150] LUMBER (FRAMES)
15' [4 M] FULL 1 X 2-1/2 [25 X 63] LUMBER (FRAMES)
84' [25 M] - 1X4 [19 X 35] LUMBER (S/C C/L R/R)
16' [5 M] - 2X4 [35 X 90] LUMBER (KEELSON & STEM)
50 #8 X 1-3/4 [M4 X 40] DECK SCREWS
50 #8 X 2 [M4 X 50] DECK SCREWS
25 #10 X 3 [M5 X 75] DECK SCREWS
200 #6 X 1-1/4 [M3 X 35] DECK SCREWS
1.5 GAL [6 L] - EPOXY RESIN
14 YDS [10 M] - 50" [1.3 M] WIDE 6 OZ F'GLASS CLOTH

FASTENING SCHEDULE

FRAME TO FRAME: #8 X 1-3/4 [M4 X 40] DECK SCREWS
LONGITUDINAL TO FRAME: #8 X 2 [M4 X 50] DECK SCREWS
KEELSON TO FRAME: #10 X 3 [M5 X 75] DECK SCREWS
PLANKING TO FRAME: #6 X 1-1/4 [M3 X 35] DECK SCREWS

NOTES:

1. YOU MAY SCARF TOGETHER SHORTER PIECES TO CREATE THE LONGITUDINAL ELEMENTS.
2. NOMINAL LUMBER SIZED CALLED OUT, E.G. A 2 X 4 LUMBER IS ACTUAL SIZE 1-1/2" X 3-1/2" (EXCEPTE WHERE NOTED)

 **Spira International, Inc.**
Huntington Beach, California

ARANSAS
13' [4.0M] SAILING SKIPJACK/SHARPIE

DRAWN BY: J. SPIRA	DATE: 09/20/12	DRAWING NO. ARAN03
-----------------------	-------------------	-----------------------

SCALE 1" = 1' [1/12] SHEET OF