

4

3


2

1

NOTICE

THIS DRAWING CONTAINS A PROPRIETARY DESIGN ASSIGNED TO SPIRA INTERNATIONAL, INC. ALL RIGHTS TO DUPLICATE, TRANSFER OR USE ARE EXPRESSLY RESERVED BY SPIRA INTERNATIONAL. THE BUYER IS LICENSED TO BUILD ONE ASSEMBLY FROM THESE PLANS.

REVISIONS				
ZONE	LTR	DESCRIPTION	DATE	APPROVED

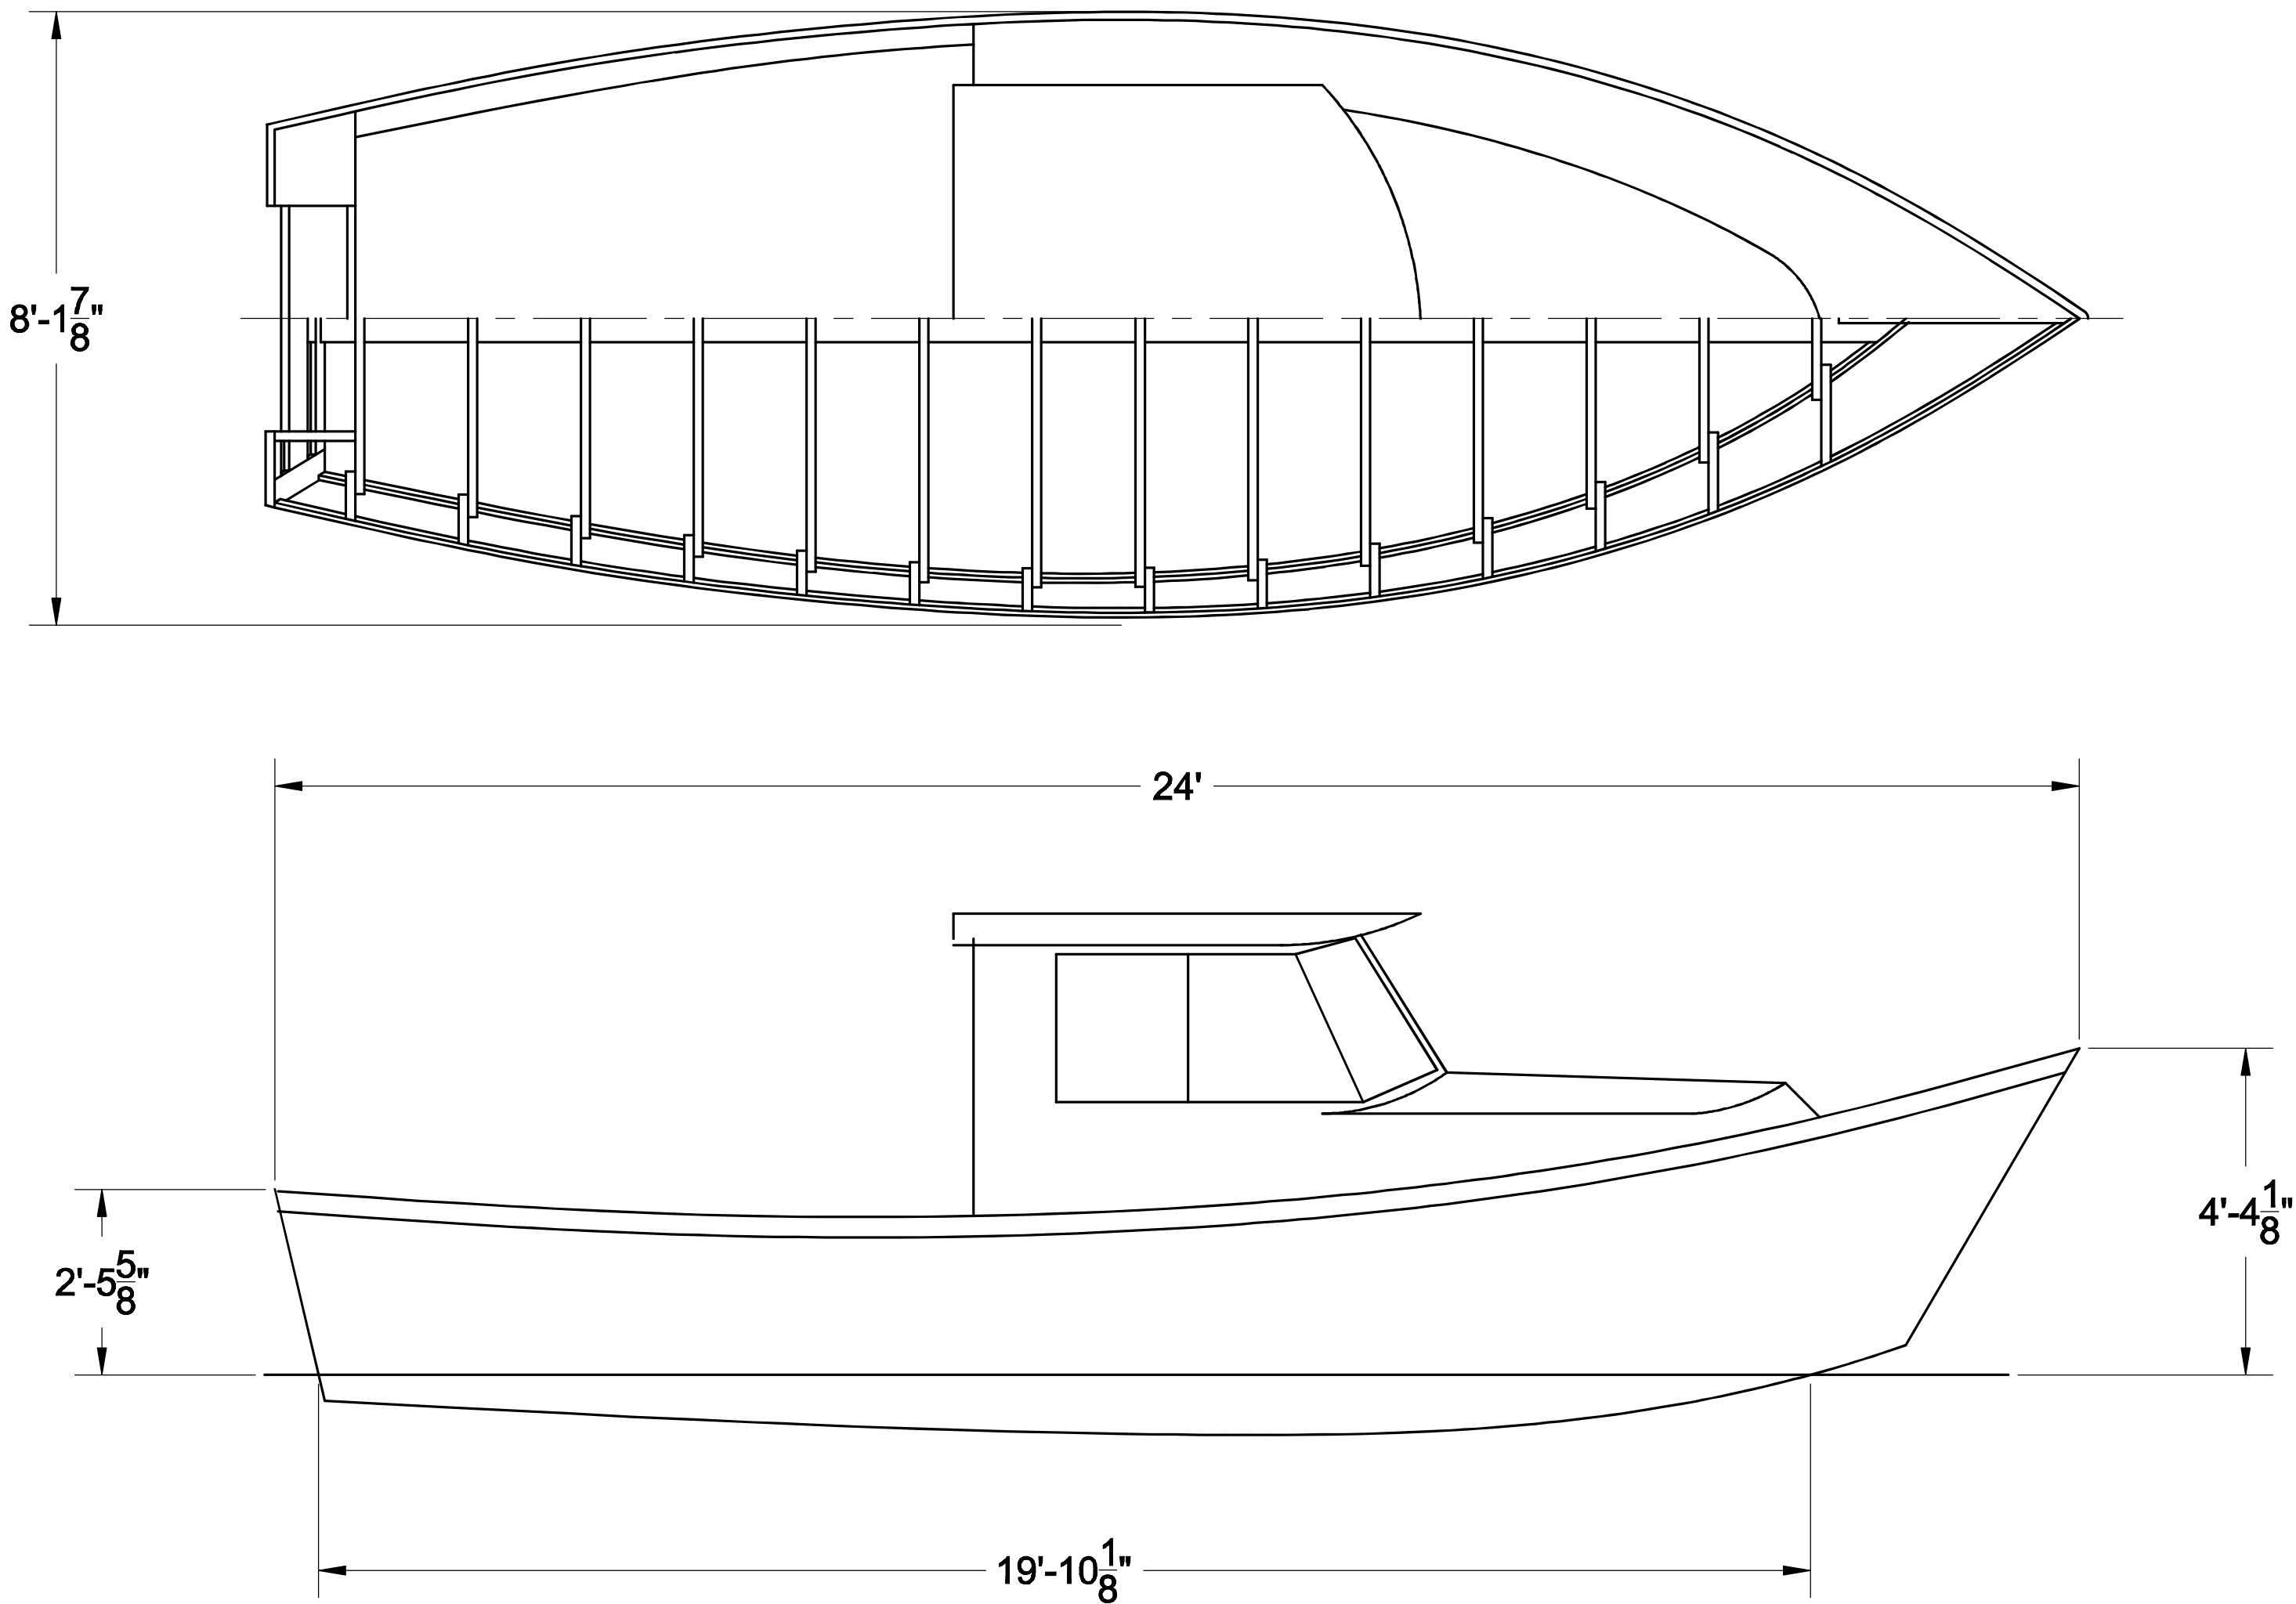

SPECIFICATIONS	
MAX. DISPLACEMENT	LBS
HULL WEIGHT	LBS
CALC. MAX. HORSEPOWER	175 HP
RECOMMENDED HP	50 HP

A



Spira International, Inc.
Huntington Beach, California

GLACIER BAY
24' POWER DRIFTER

DRAWN BY:
J. SPIRA

DATE:
11/04/14

DRAWING NO.
GLAC01

SCALE 1/2" = 1'

SHEET OF

4

3

2

1

4

3

2

1

NOTICE

THIS DRAWING CONTAINS A PROPRIETARY DESIGN ASSIGNED TO SPIRA INTERNATIONAL, INC. ALL RIGHTS TO DUPLICATE, TRANSFER OR USE ARE EXPRESSLY RESERVED BY SPIRA INTERNATIONAL. THE BUYER IS LICENSED TO BUILD ONE ASSEMBLY FROM THESE PLANS.

REVISIONS

ZONE	LTR	DESCRIPTION	DATE	APPROVED

D

D

C

C

B

B

A

A

SHEAR CLAMP
1 X 3 LUMBER

RAIL CAP
1 X (3/4" STOCK) LUMBER

FRAME ELEMENTS
2 x 4 LUMBER

RUB RAIL
1 X 3 LUMBER

DECK - 5/8 PLY

DECK BEAMS
2 X 4 LUMBER

DECK RISERS
1 X 3 LUMBER

1 X 3 LUMBER

SIDES - 5/8" PLY

CHINE LOG - 1 X 3
LUMBER

BOTTOM - 2 LAYERS 3/8" PLY
FIBERGLASS IN BETWEEN
& ON BOTTOM

KEELSON
2 X 8 LUMBER

CONSTRUCTION DETAIL

TYPICAL AT AFT SECTION
NOT TO SCALE

FASTENING SCHEDULE

2x FRAME TO 2x FRAME: #10 X 2 -1/2 DECK SCREWS
LONGITUDINAL TO FRAME: #8 X 2 DECK SCREWS
PLANKING TO FRAME: #8 X 1-1/2 DECK SCREWS

NOTES:

1. YOU MAY SCARF TOGETHER SHORTER PIECES TO CREATE THE LONGITUDINAL ELEMENTS.
2. NOMINAL LUMBER SIZED CALLED OUT, E.G. A 2 X 4 LUMBER IS ACTUAL SIZE 1-1/2" X 3-1/2"

BILL OF MATERIALS (HULL)

FRAMES: 300 FT 2X4S
KEELSON & TRANSOM: 30 FT 2X8S
S/C & C/L: 180' 1X3S
SIDES: 8 SHTS 5/8" PLY
BOTTOM: 11 SHTS 3/8" PLY
GLASS: 68 YDS - 6 OR 10 OZ CLOTH
EPOXY: 8 GAL
FRAMES: 120 - #10 X 3" SCREWS
150 - #8 X 2" SCREWS
PLANKING: 1500 - #8 X 1-1/2" SCREWS
DECKING: 5 SHTS 5/8 PLY
RAIL CAP: 54' 1X8

CABIN COVER
1/2 PLY

FORE DECK
5/8 PLY

CABIN
FRAMING
1X3 LUMBER

CONSTRUCTION DETAIL

CABIN SECTION
NOT TO SCALE

BILL OF MATERIALS (CABIN)

FRAMES: 60 FT 1X3S
36 FT 1X8S
SIDES: 4 SHTS 1/2" PLY
GLASS: 12 YDS - 6 OZ CLOTH
EPOXY: 2 GAL
SCREWS: 200 - #8 X 1-1/2" SCREWS



Spira International, Inc.
Huntington Beach, California

GLACIER BAY
24' POWER DRIFTER

DRAWN BY:
J. SPIRA

DATE:
11/04/14

DRAWING NO.

GLAC02

SCALE NONE

SHEET OF

4

3

2

1