

4

3


2

1

NOTICE

THIS DRAWING CONTAINS A PROPRIETARY DESIGN ASSIGNED TO SPIRA INTERNATIONAL, INC. ALL RIGHTS TO DUPLICATE, TRANSFER OR USE ARE EXPRESSLY RESERVED BY SPIRA INTERNATIONAL. THE BUYER IS LICENSED TO BUILD ONE ASSEMBLY FROM THESE PLANS.


REVISIONS				
ZONE	LTR	DESCRIPTION	DATE	APPROVED

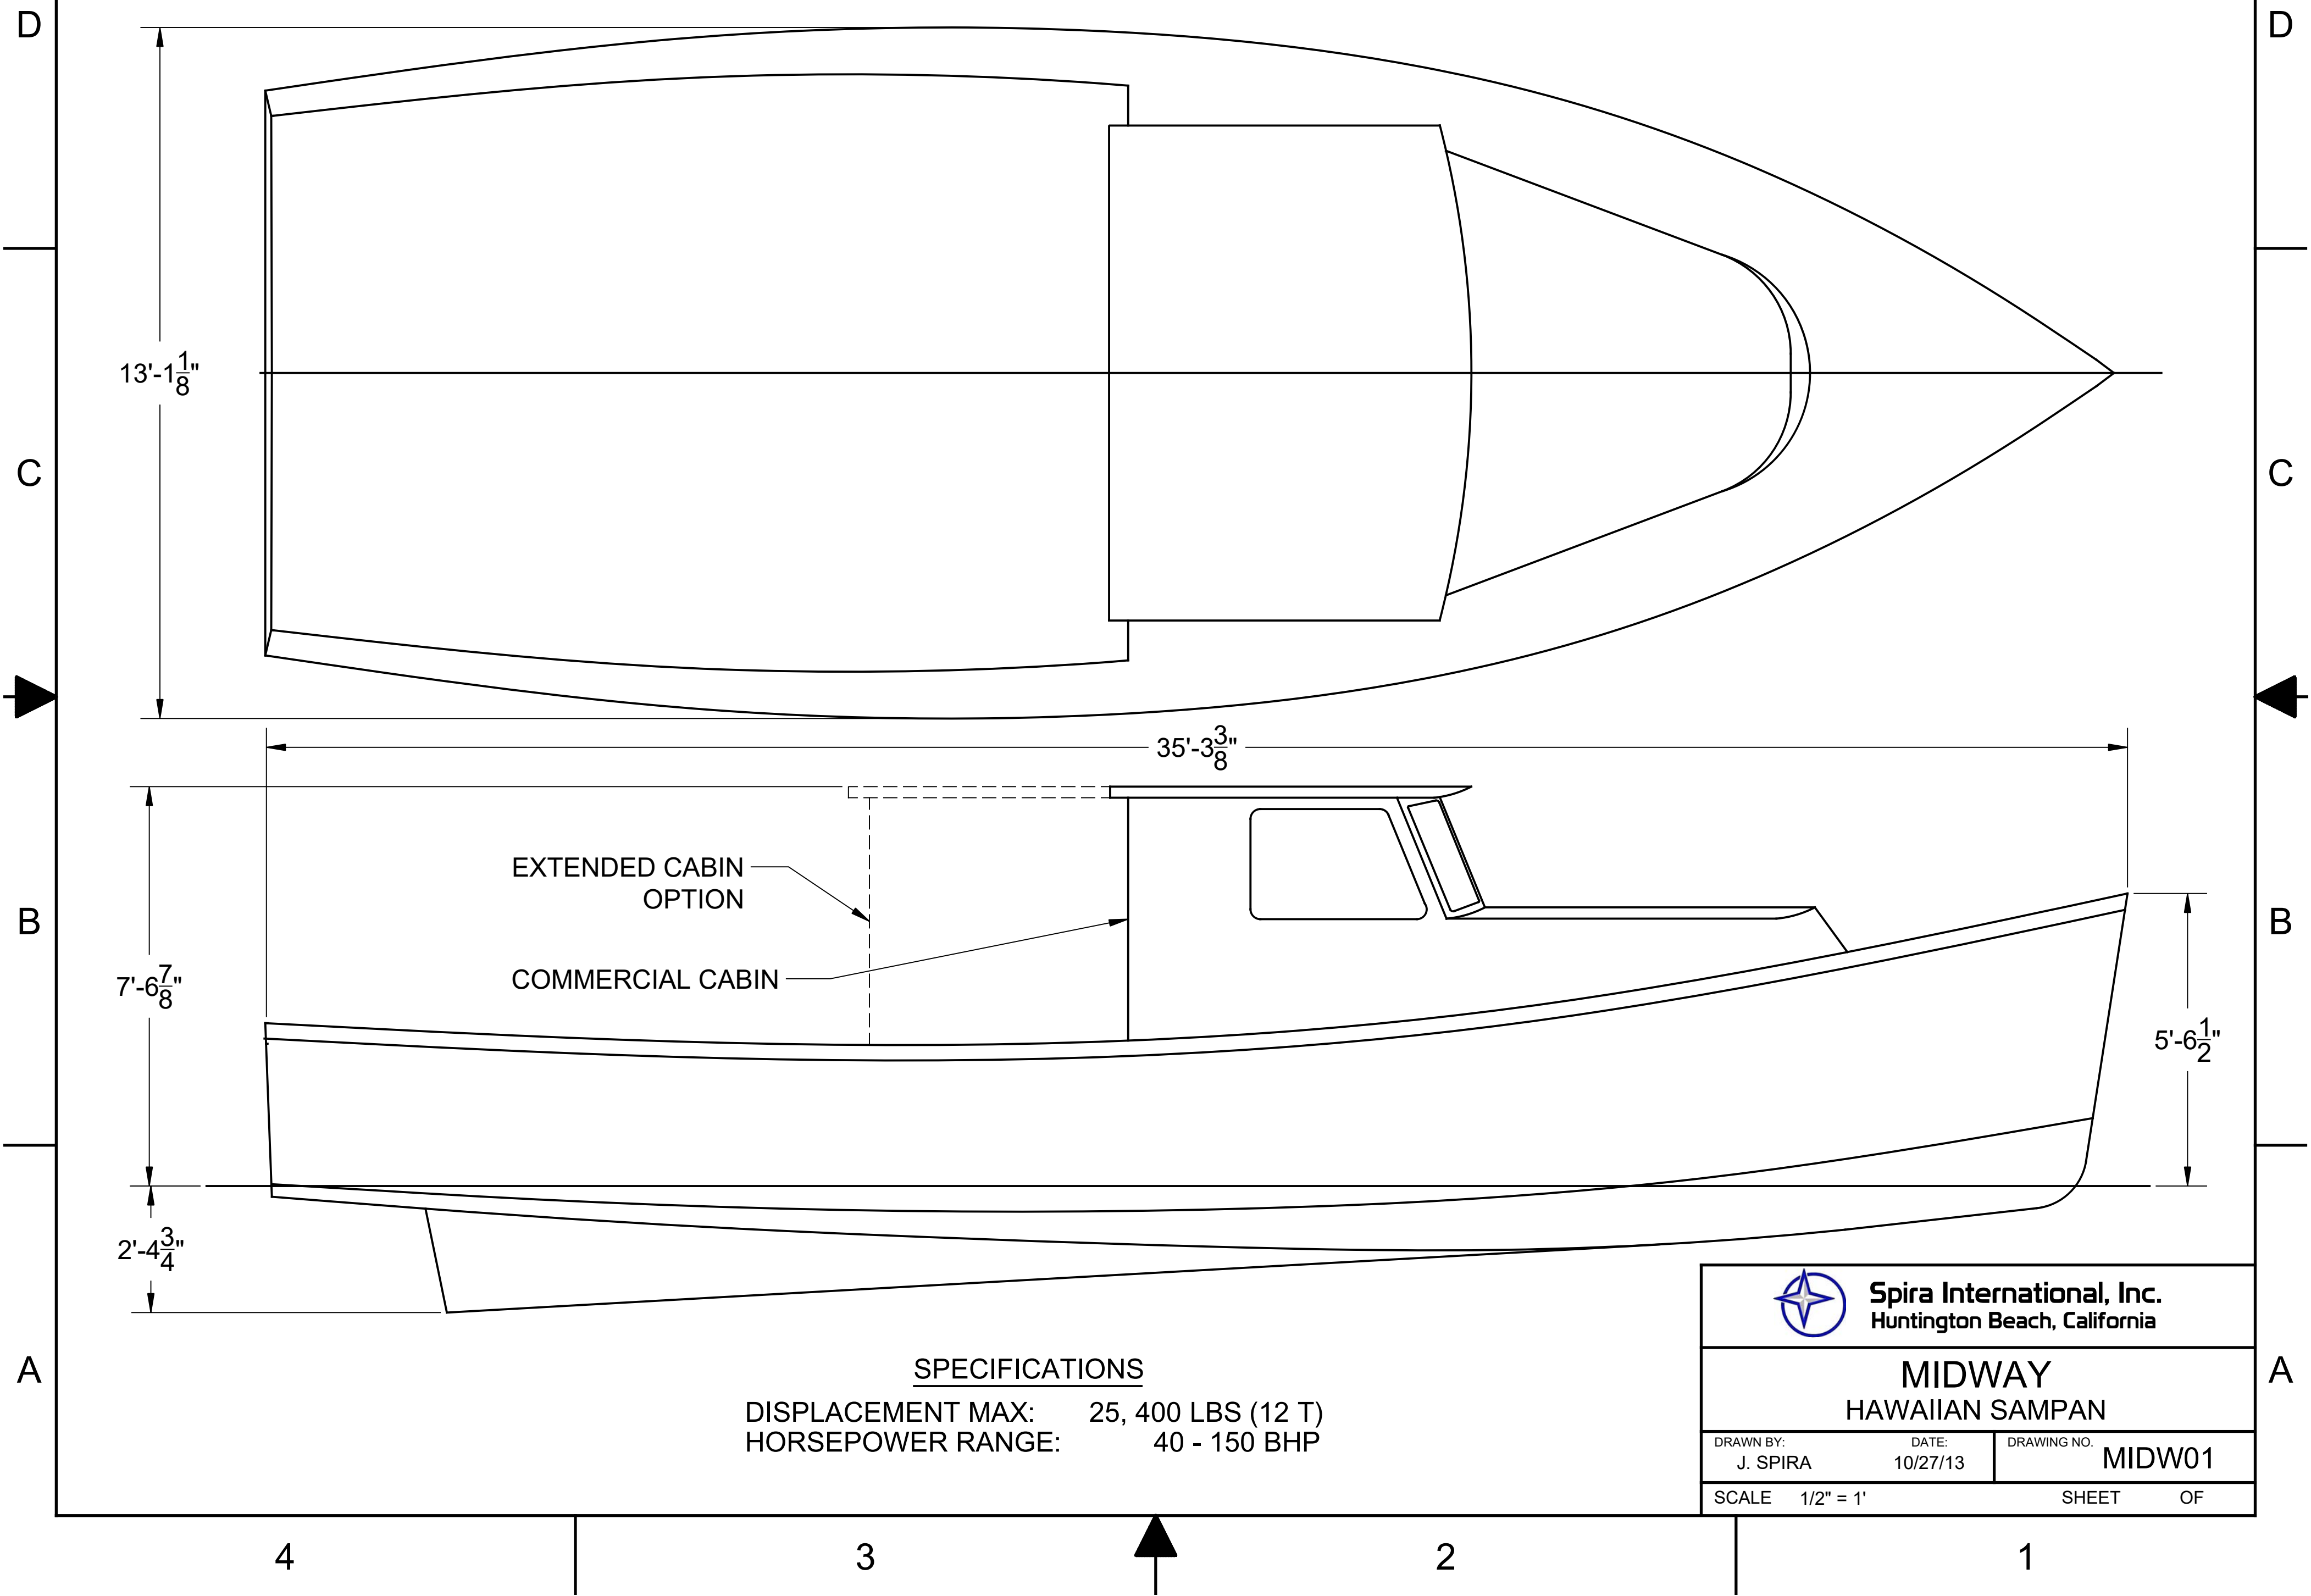

4 3 2 1

NOTICE
THIS DRAWING CONTAINS A PROPRIETARY DESIGN ASSIGNED TO SPIRA INTERNATIONAL, INC. ALL RIGHTS TO DUPLICATE, TRANSFER OR USE ARE EXPRESSLY RESERVED BY SPIRA INTERNATIONAL. THE BUYER IS LICENSED TO BUILD ONE ASSEMBLY FROM THESE PLANS.

REVISIONS				
ZONE	LTR	DESCRIPTION	DATE	APPROVED

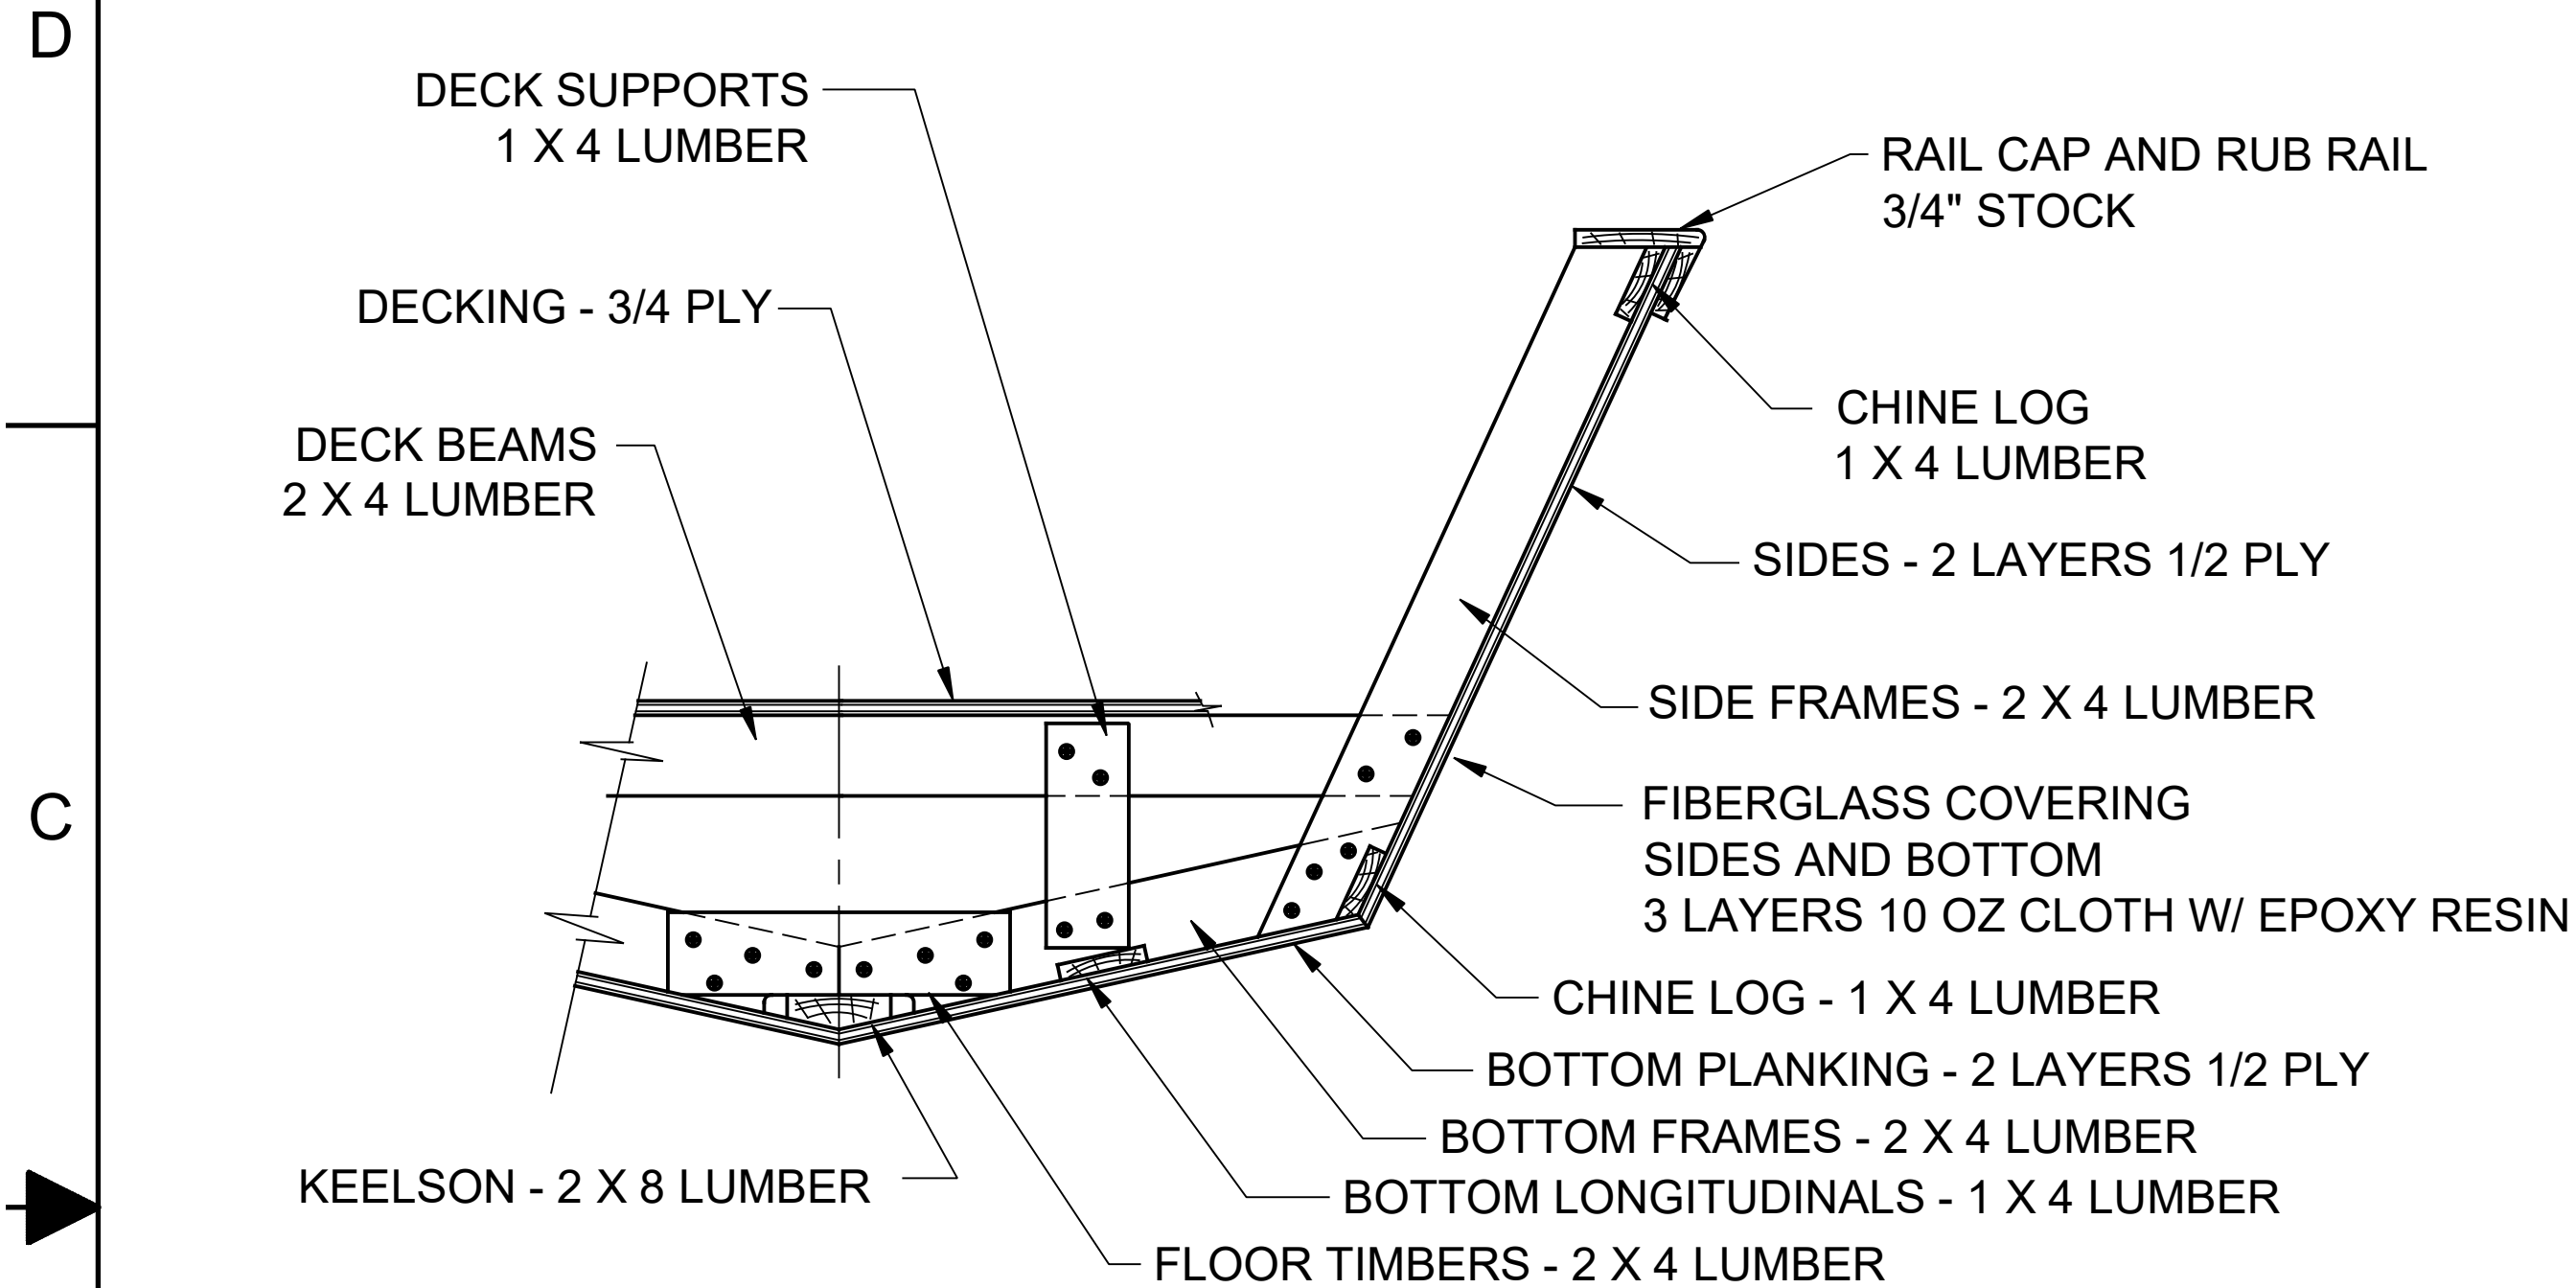

CONSTRUCTION METHOD
TYPICAL AT EACH FRAME
SCALE: NONE

BILL OF MATERIALS (HULL ONLY)


48 SHEETS 1/2" PLY
12 SHEETS 3/4" PLY
580' 2X4 LUMBER FOR FRAMES
604' 1X4 CLEAR LUMBER FOR SHEER
CLAMP, CHINE LOG AND RUB RAILS
22' 2X6 LUMBER FOR KEELSON
112' 2X8 LUMBER FOR KEELSON & STEM
200 #10 X 2-1/2 SS DECK SCREWS
500 #10 X 2 SS DECK SCREWS
4000 #8 X 2 SS DECK SCREWS
8 5/16 ALLTHREAD, WASHERS & NUTS
25 GAL EPOXY RESIN
150 YDS 10 OZ FIBERGLASS CLOTH

FASTENING SCHEDULE

2x FRAME TO 2x FRAME: #10 X 2 -1/2 DECK SCREWS
1X FRAME TO 2X FRAME: #10 X 2 DECK SCREWS
PLANKING TO FRAME: #8 X 1 1/2 DECK SCREWS
KEEL TO FRAME: 5/16 ALLTHREAD BOLTS

NOTES:

1. YOU MAY SCARF TOGETHER SHORTER PIECES TO CREATE THE LONGITUDINAL ELEMENTS.
2. NOMINAL LUMBER SIZED CALLED OUT, E.G. A 2 X 4 LUMBER IS ACTUAL SIZE 1-1/2" X 3-1/2"

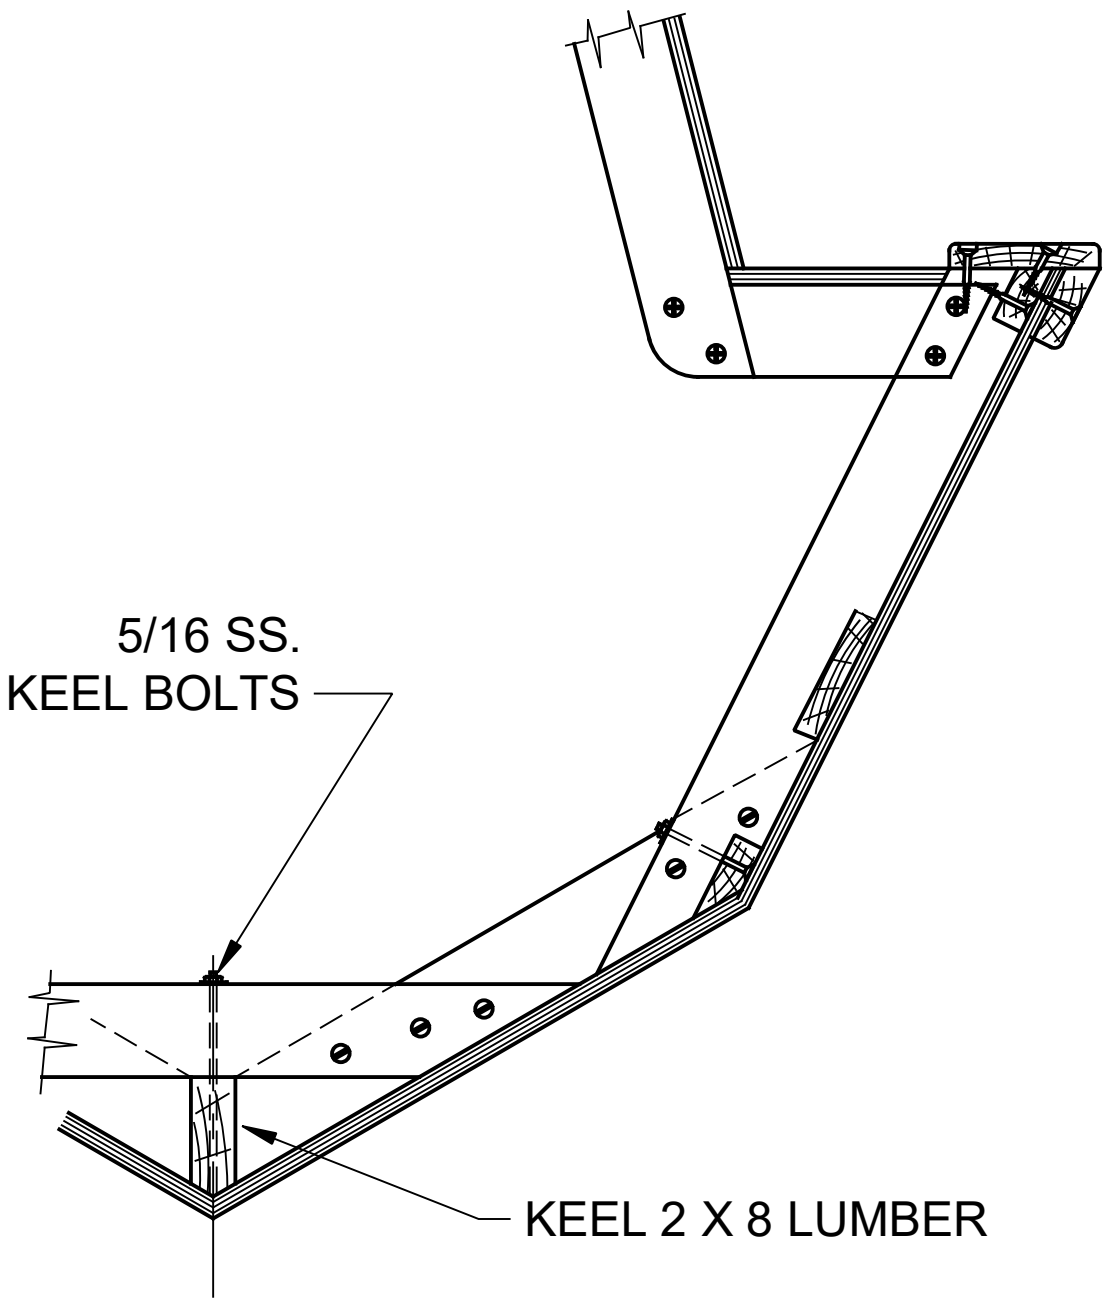

CONSTRUCTION METHOD
FORWARD SECTIONS
SCALE: NONE



Spira International, Inc.
Huntington Beach, California

**MIDWAY
HAWAIIAN SAMPAN**

DRAWN BY:
J. SPIRA

DATE:
10/27/13

DRAWING NO.
MIDW02

SCALE 1/2" = 1'

SHEET OF