


4 3 2 1

NOTICE
THIS DRAWING CONTAINS A PROPRIETARY DESIGN ASSIGNED TO SPIRA INTERNATIONAL, INC. ALL RIGHTS TO DUPLICATE, TRANSFER OR USE ARE EXPRESSLY RESERVED BY SPIRA INTERNATIONAL. THE BUYER IS LICENSED TO BUILD ONE ASSEMBLY FROM THESE PLANS.

REVISIONS				
ZONE	LTR	DESCRIPTION	DATE	APPROVED

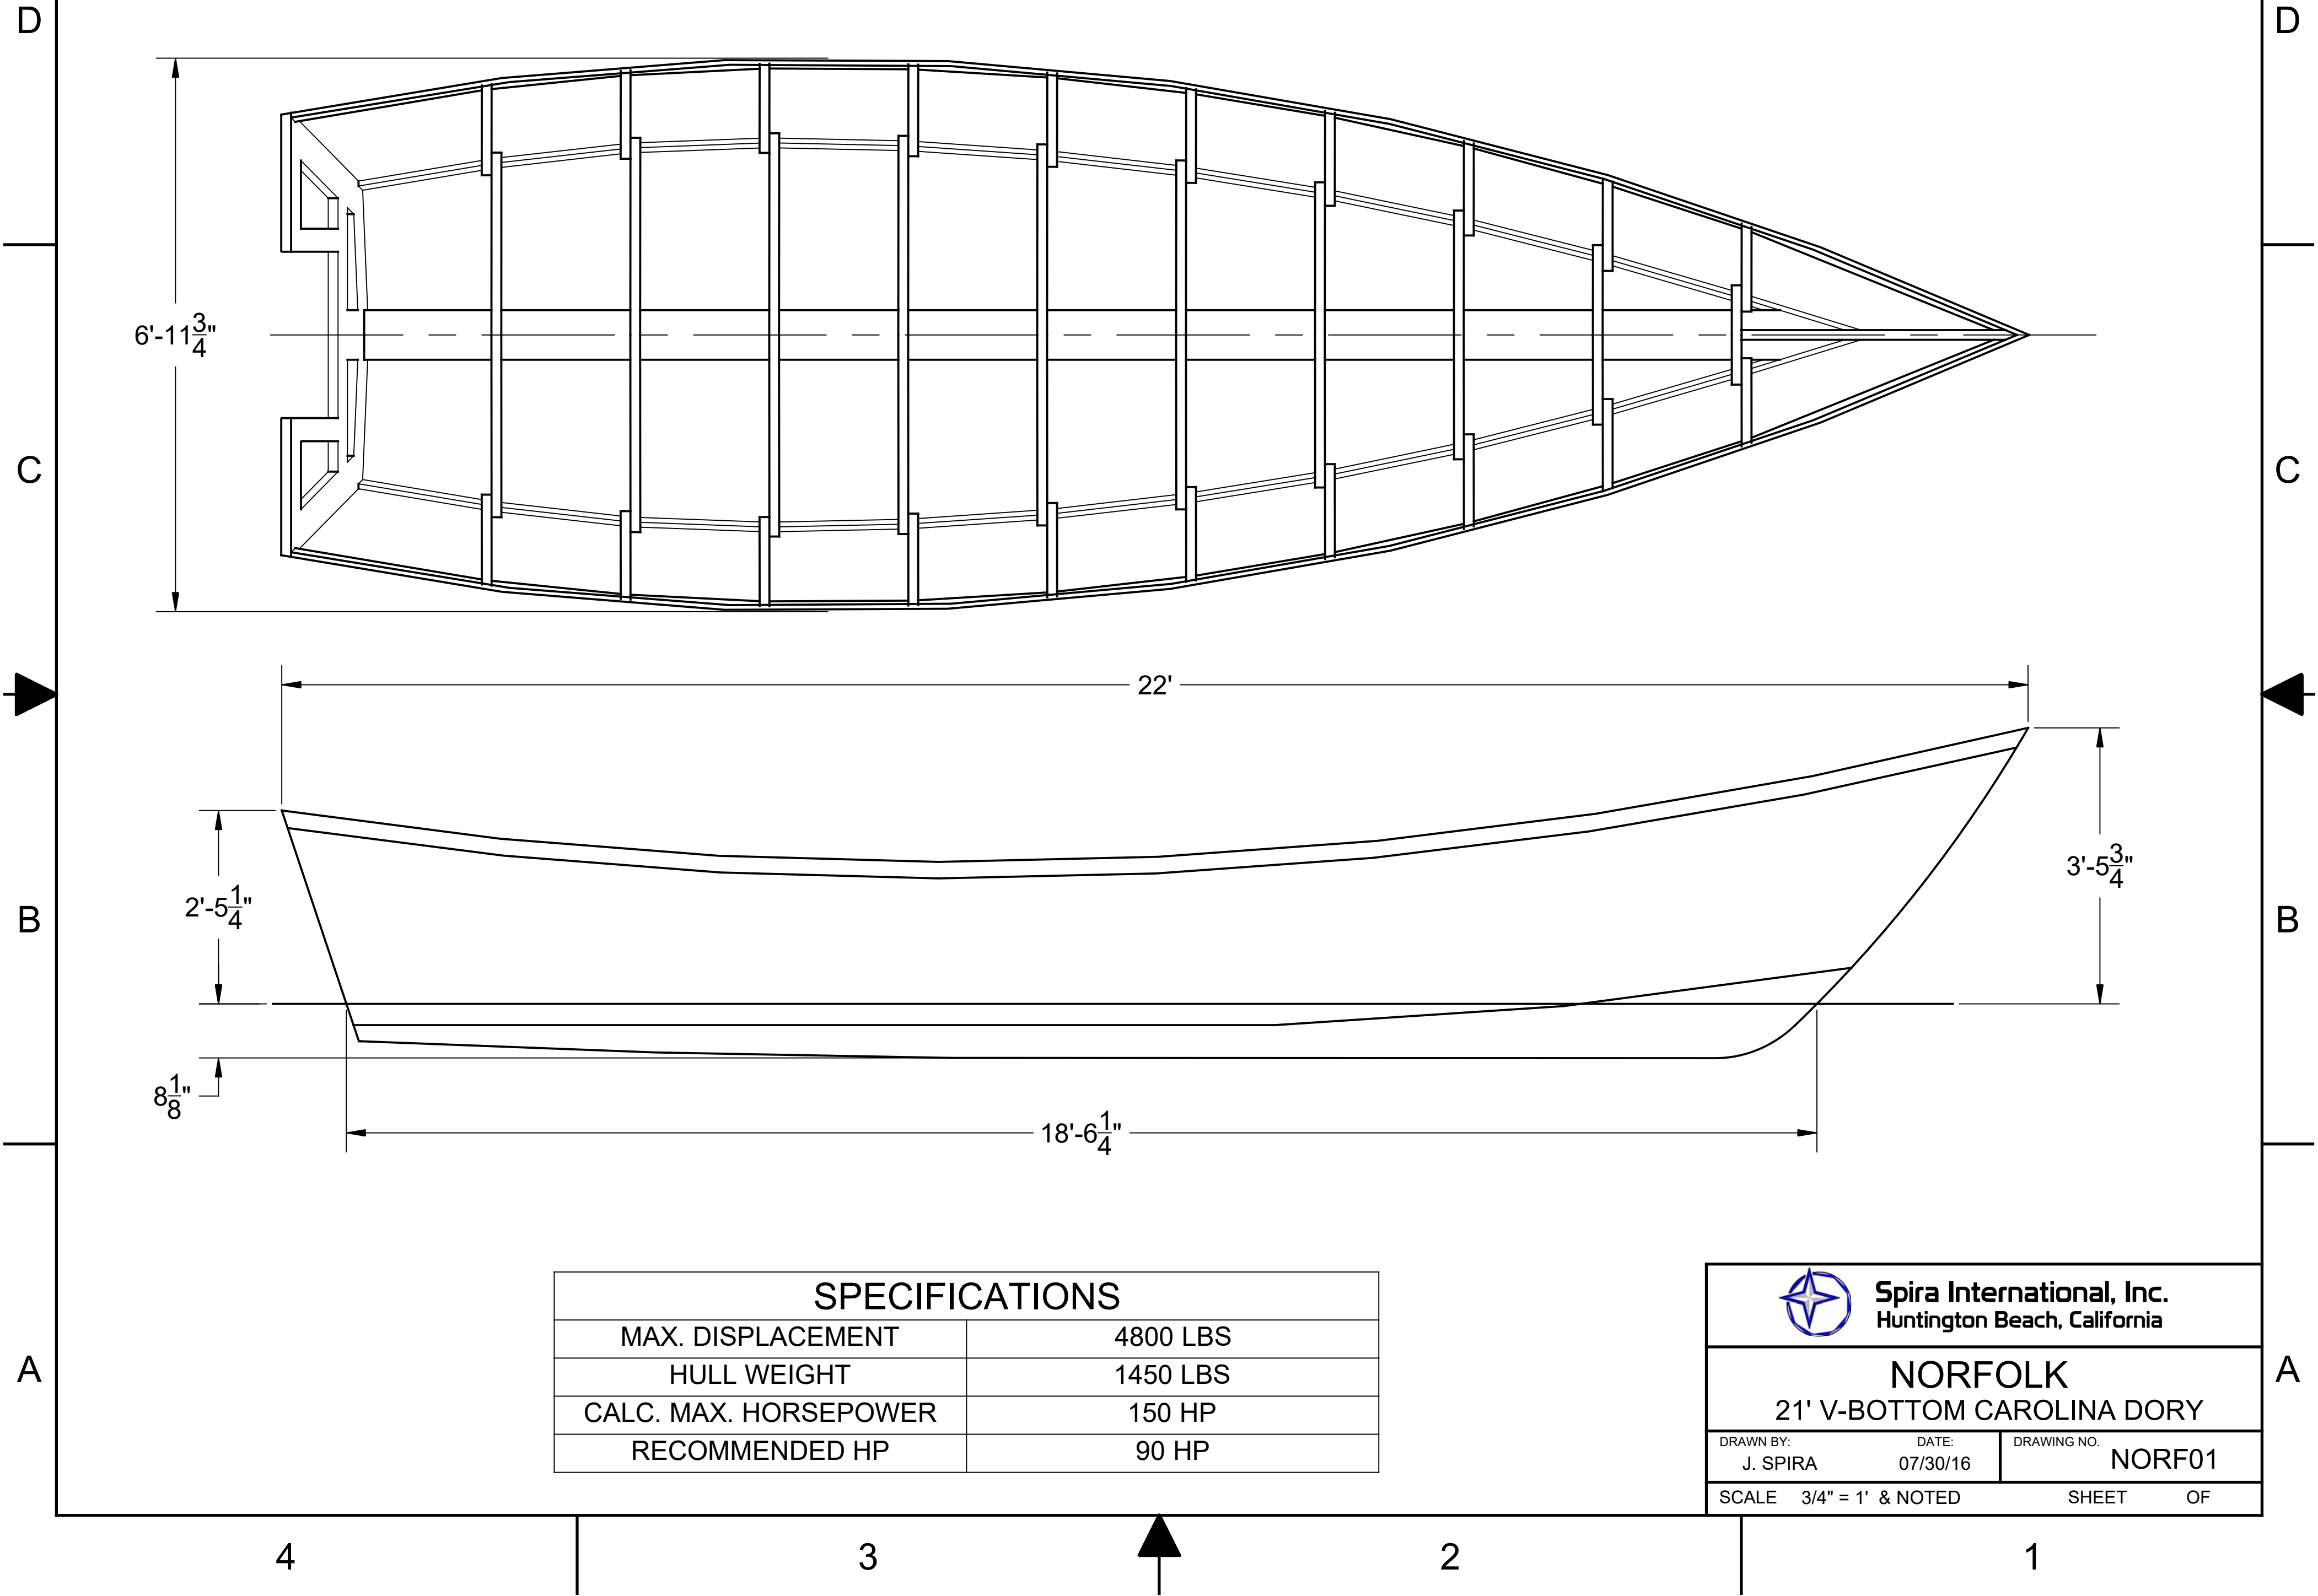

4

3


2

1

NOTICE

THIS DRAWING CONTAINS A PROPRIETARY DESIGN ASSIGNED TO SPIRA INTERNATIONAL, INC. ALL RIGHTS TO DUPLICATE, TRANSFER OR USE ARE EXPRESSLY RESERVED BY SPIRA INTERNATIONAL. THE BUYER IS LICENSED TO BUILD ONE ASSEMBLY FROM THESE PLANS.

REVISIONS				
ZONE	LTR	DESCRIPTION	DATE	APPROVED

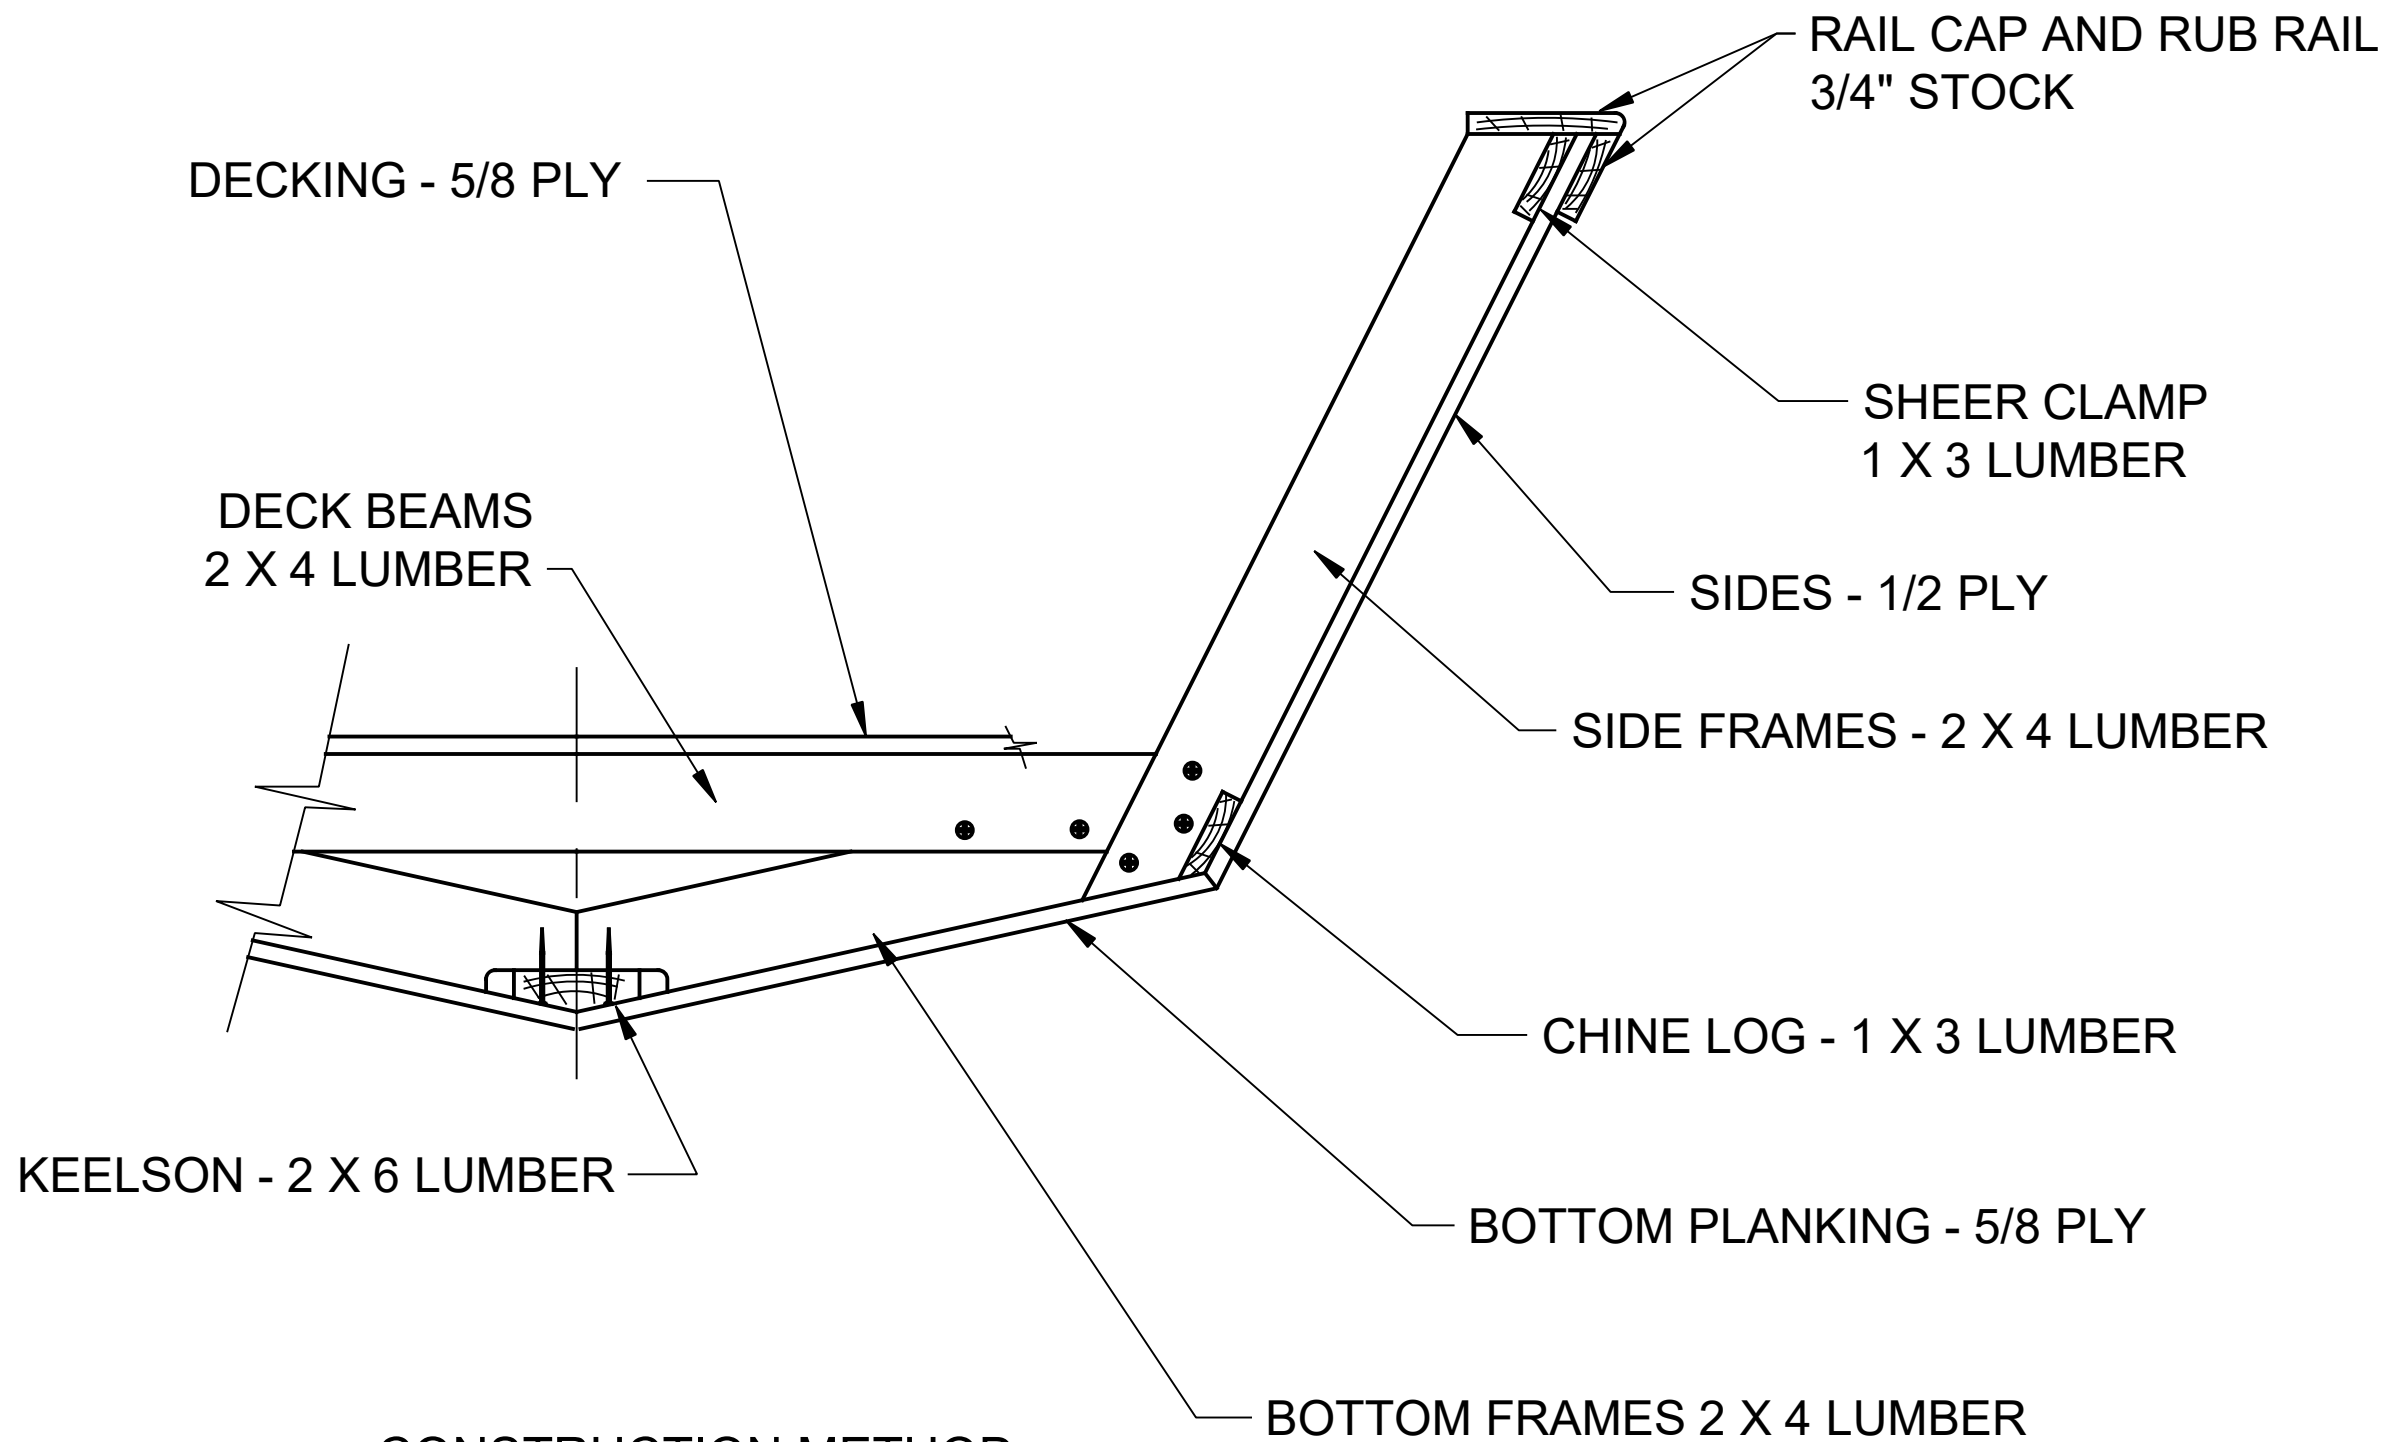

BILL OF MATERIALS (HULL ONLY)

10 SHEETS 5/8" PLY
8 SHEETS 1/2" PLY
180' 2X4 LUMBER FOR FRAMES
140' 1X3 CLEAR LUMBER FOR SHEER
CLAMP, CHINE LOG AND RUB RAILS
30' 2X6 LUMBER FOR KEELSON AND STEM
8' 2X8 LUMBER FOR TRANSOM & STEM KNEE
200 #10 X 2-1/2 SS DECK SCREWS
200 #10 X 2 SS DECK SCREWS
1500 #10 X 1-1/2 SS DECK SCREWS
3 GAL EPOXY RESIN
30 YDS - 6 OZ FIBERGLASS CLOTH (50" WIDE)

FASTENING SCHEDULE

2x FRAME TO 2x FRAME: #10 X 2 -1/2 DECK SCREWS
LONGITUDINAL TO FRAME: #10 X 2 DECK SCREWS
PLANKING TO FRAME: #10 X 1-1/2 DECK SCREWS

NOTES:

1. YOU MAY SCARF TOGETHER SHORTER PIECES TO CREATE THE LONGITUDINAL ELEMENTS.
2. NOMINAL LUMBER SIZED CALLED OUT, E.G. A 2 X 4 LUMBER IS ACTUAL SIZE 1-1/2" X 3-1/2"



Spira International, Inc.
Huntington Beach, California

NORFOLK
21' V-BOTTOM CAROLINA DORY

DRAWN BY:
J. SPIRA

DATE:
07/30/16

DRAWING NO.
NORF02

SCALE 3/4" = 1' & NOTED

SHEET OF