

4

3



2

1

NOTICE

THIS DRAWING CONTAINS A PROPRIETARY DESIGN ASSIGNED TO SPIRA INTERNATIONAL, INC. ALL RIGHTS TO DUPLICATE, TRANSFER OR USE ARE EXPRESSLY RESERVED BY SPIRA INTERNATIONAL. THE BUYER IS LICENSED TO BUILD ONE ASSEMBLY FROM THESE PLANS.

REVISIONS				
ZONE	LTR	DESCRIPTION	DATE	APPROVED

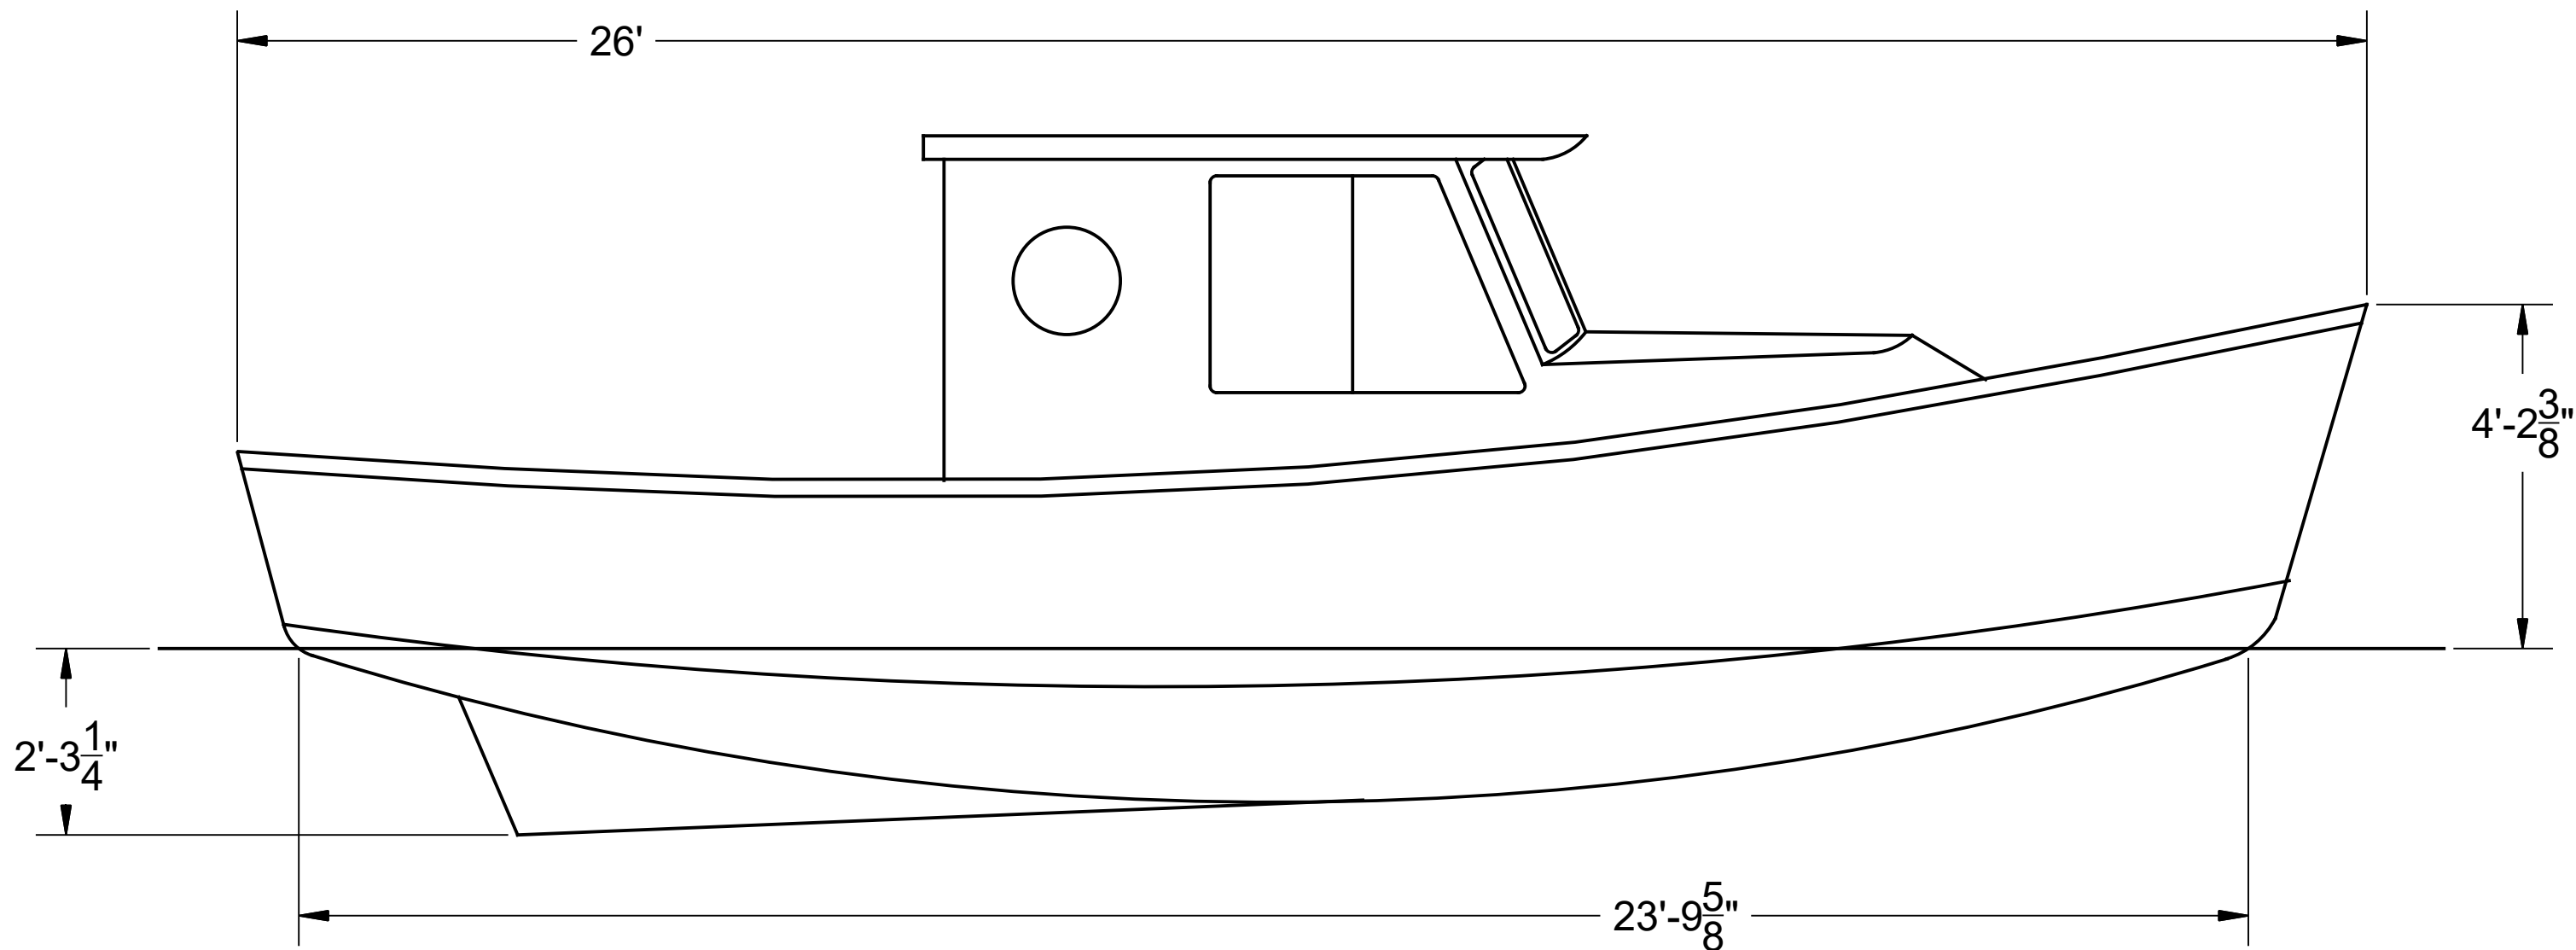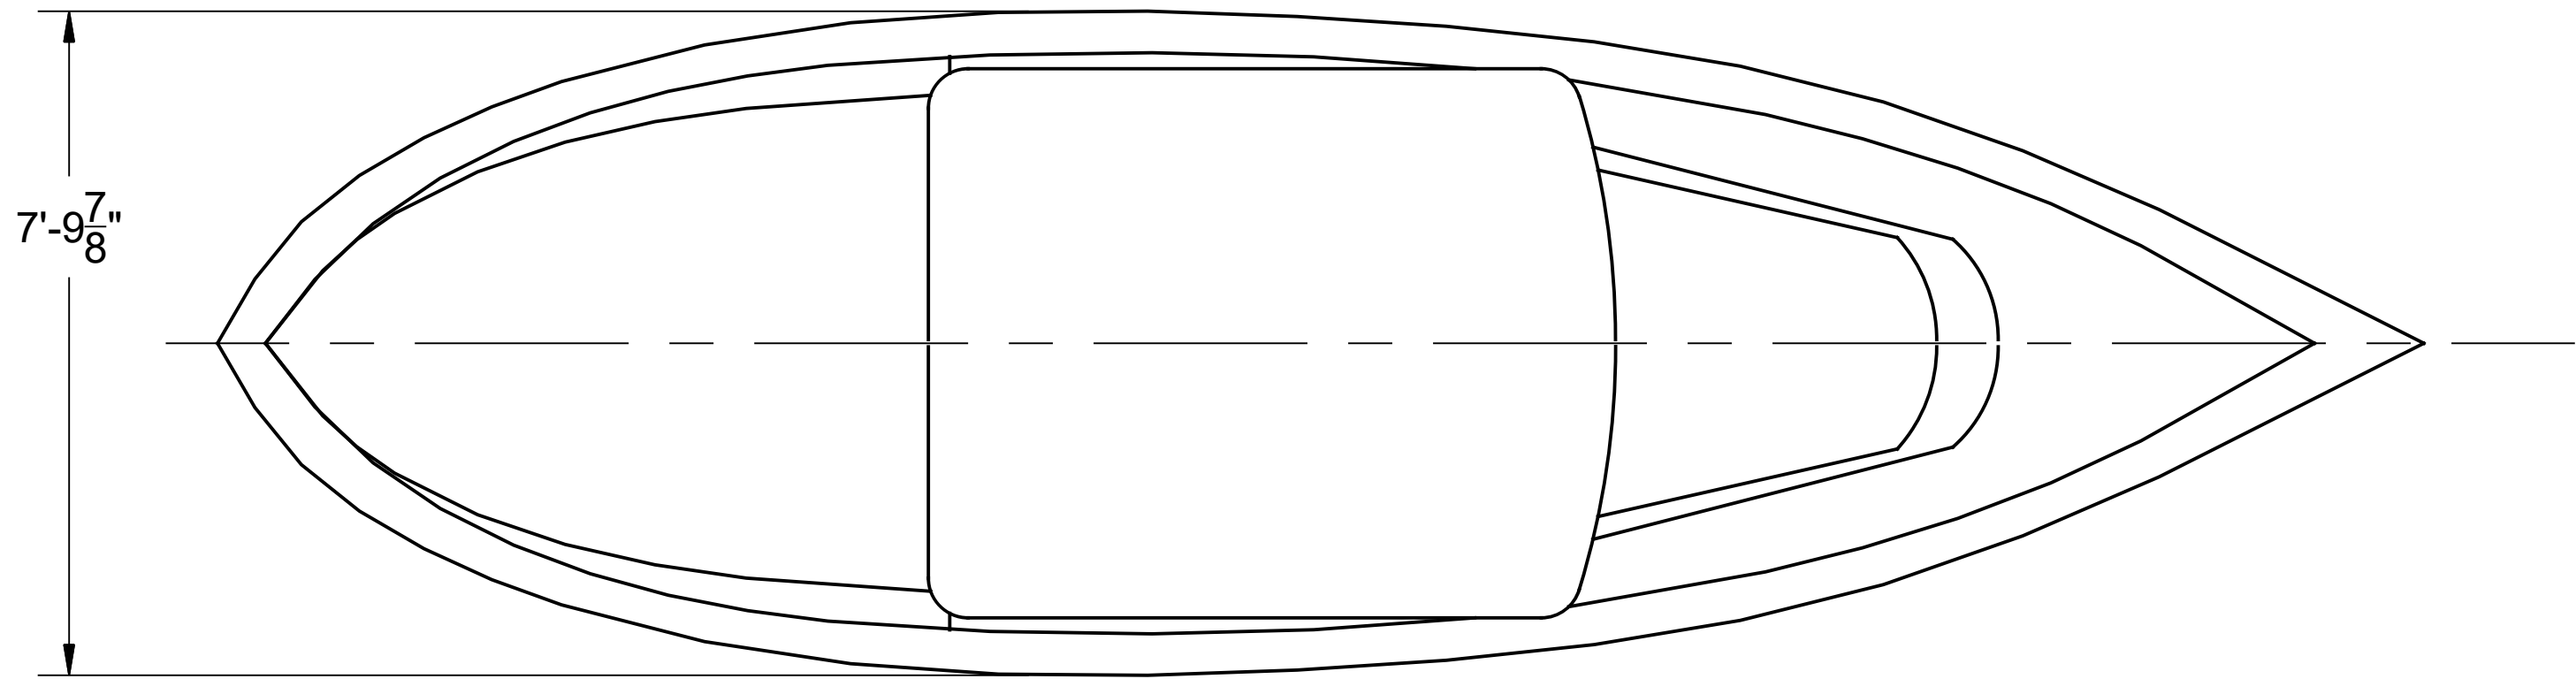

A

SPECIFICATIONS	
MAX. DISPLACEMENT	11,600 LBS.
HULL WEIGHT	2440 LBS
MAX. HORSEPOWER	55 HP
RECOMMENDED HP	18 HP

4

3

2

1

A



Spira International, Inc.
Huntington Beach, California

SAN JUAN
26' DISPLACEMENT CRUISER

DRAWN BY: J. SPIRA	DATE: 04/14/12	DRAWING NO. SANJ01
SCALE 1/2" = 1' & NOTED		SHEET OF

4

3


2

1

NOTICE

THIS DRAWING CONTAINS A PROPRIETARY DESIGN ASSIGNED TO SPIRA INTERNATIONAL, INC. ALL RIGHTS TO DUPLICATE, TRANSFER OR USE ARE EXPRESSLY RESERVED BY SPIRA INTERNATIONAL. THE BUYER IS LICENSED TO BUILD ONE ASSEMBLY FROM THESE PLANS.

REVISIONS				
ZONE	LTR	DESCRIPTION	DATE	APPROVED

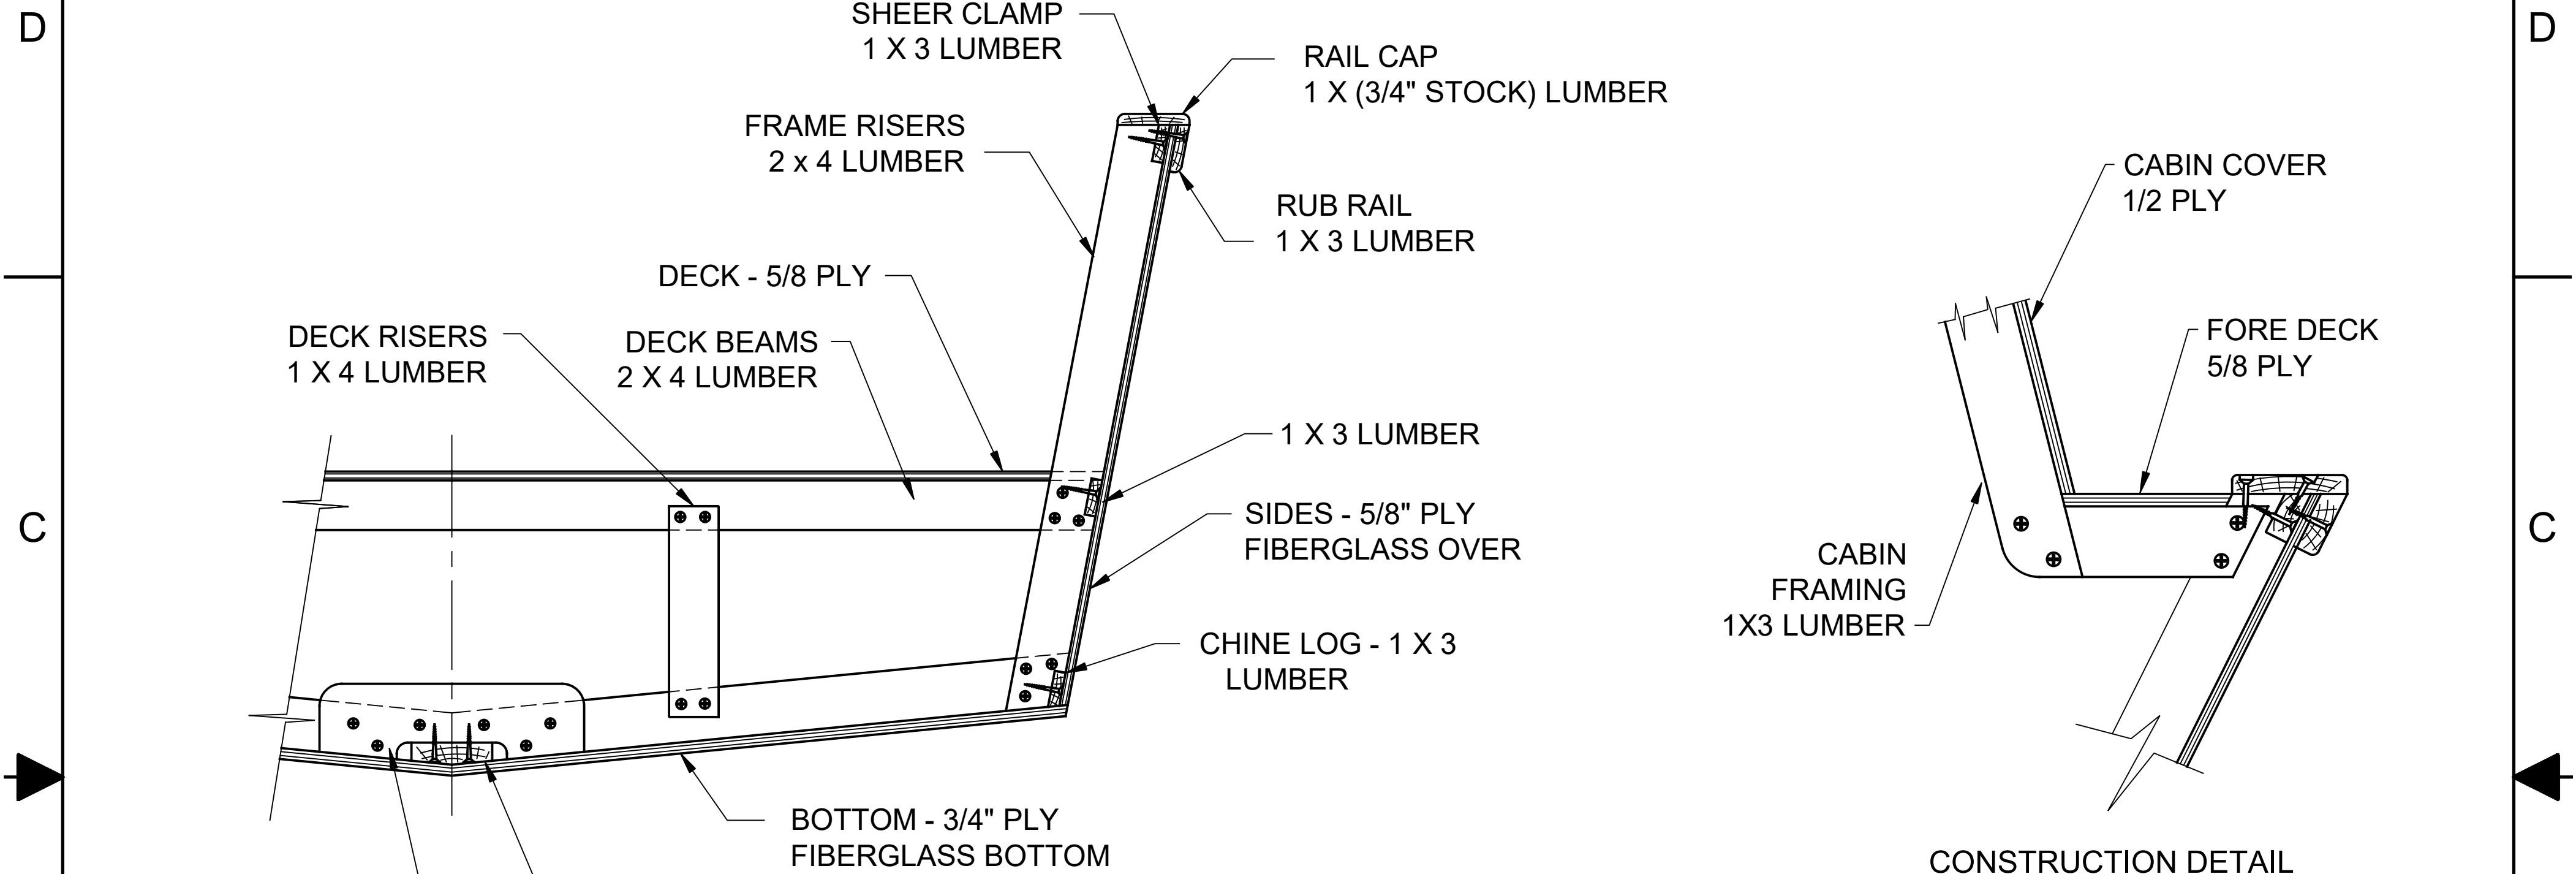

CONSTRUCTION DETAIL

TYPICAL AT AFT SECTION


NOT TO SCALE

NOTES:

1. YOU MAY SCARF TOGETHER SHORTER PIECES TO CREATE THE LONGITUDINAL ELEMENTS.
2. NOMINAL LUMBER SIZED CALLED OUT, E.G. A 2 X 4 LUMBER IS ACTUAL SIZE 1-1/2" X 3-1/2"

BILL OF MATERIALS (HULL)

FRAMES: 240 FT 2X4S
FRAMES: 60 FT 1X6S
STEMS: 16 FT 2X8S
KEELSON: 25 FT 2X6S
S/C & C/L: 160' 1X3S
SIDES: 8 SHTS 5/8" PLY
BOTTOM: 5 SHTS 3/4" PLY
GLASS: 75 YDS - 6 OZ CLOTH
EPOXY: 12 GAL
FRAMES: 500 - #10 X 2-1/2" SCREWS
PLANKING: 1500 - #8 X 2" SCREWS
DECKING: 6 SHTS 5/8 PLY
RAIL CAP: 60' 1X8

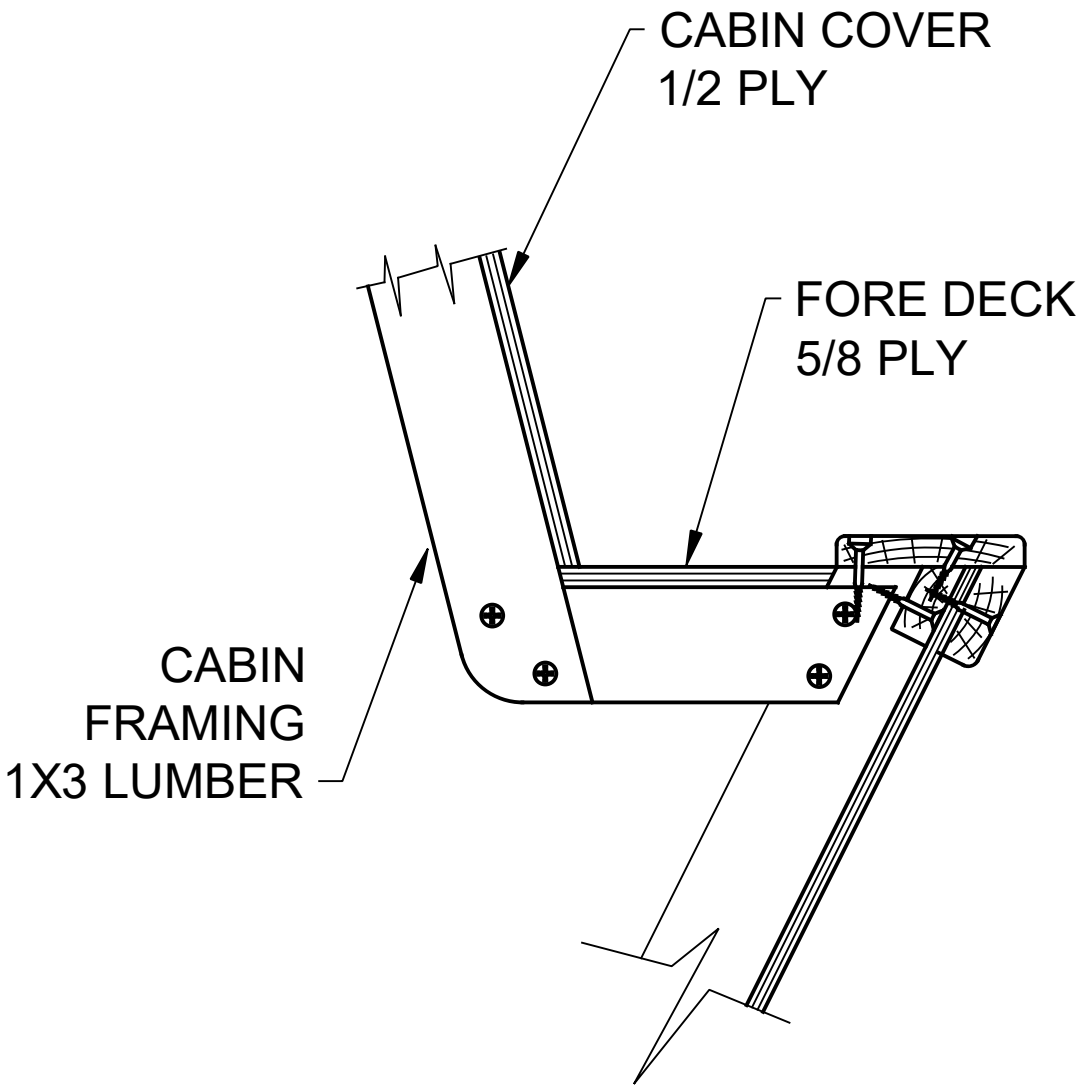

CONSTRUCTION DETAIL

CABIN SECTION

NOT TO SCALE

BILL OF MATERIALS (CABIN)

FRAMES: 64 FT 1X3S
48 FT 1X8S
SIDES: 6 SHTS 1/2" PLY
GLASS: 12 YDS - 6 OZ CLOTH
EPOXY: 2 GAL
SCREWS: 200 - #8 X 1-1/4" SCREWS



Spira International, Inc.
Huntington Beach, California

SAN JUAN
26' DOUBLE ENDER CRUISER

DRAWN BY: J. SPIRA	DATE: 05/03/12	DRAWING NO. SANJ02
SCALE 1/2" = 1'		SHEET OF