

4

3



2

1

NOTICE

THIS DRAWING CONTAINS A PROPRIETARY DESIGN ASSIGNED TO SPIRA INTERNATIONAL, INC. ALL RIGHTS TO DUPLICATE, TRANSFER OR USE ARE EXPRESSLY RESERVED BY SPIRA INTERNATIONAL. THE BUYER IS LICENSED TO BUILD ONE ASSEMBLY FROM THESE PLANS.

REVISIONS				
ZONE	LTR	DESCRIPTION	DATE	APPROVED

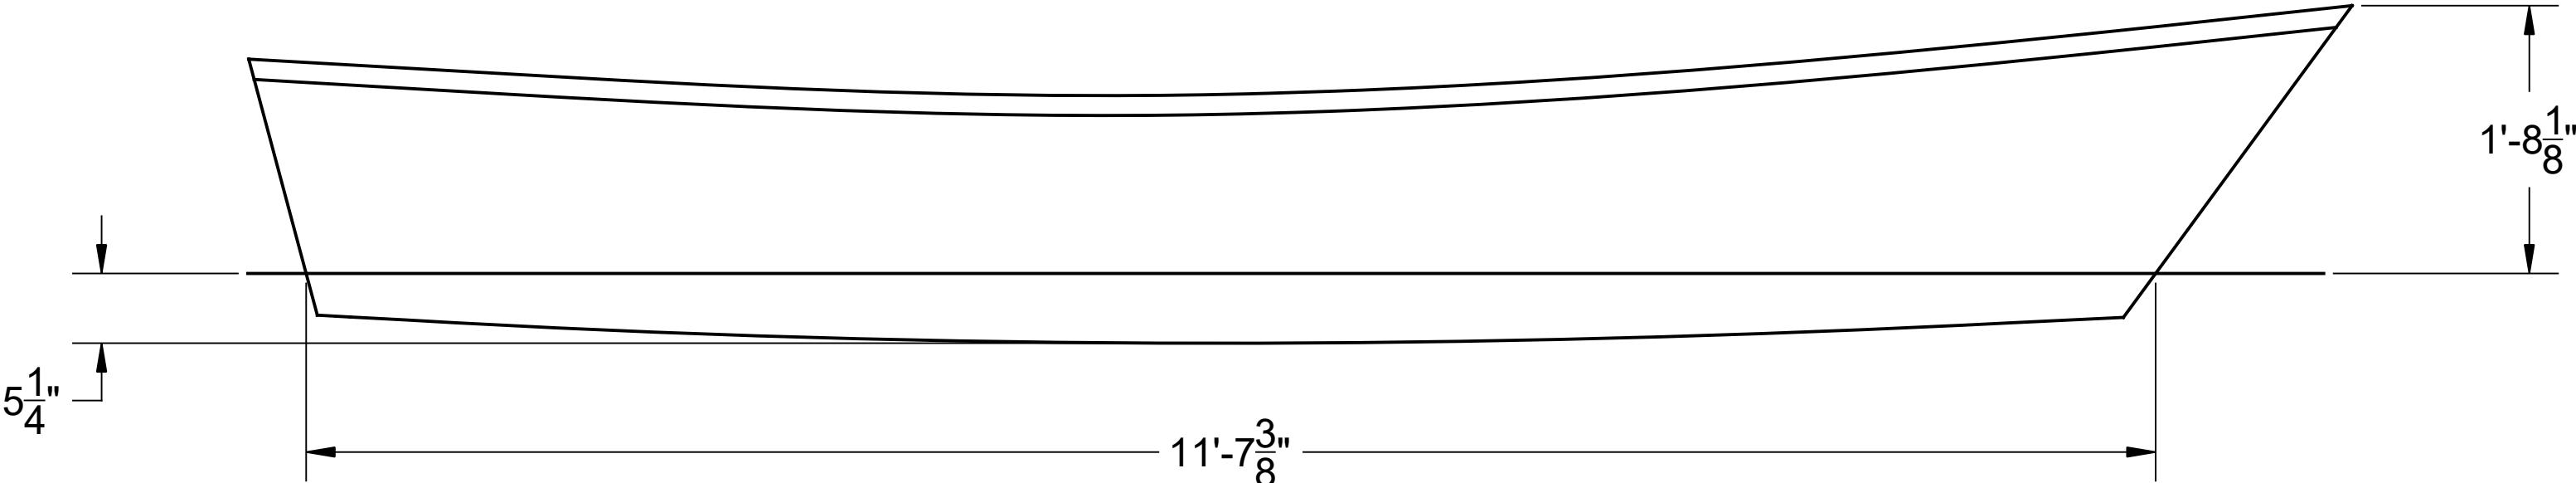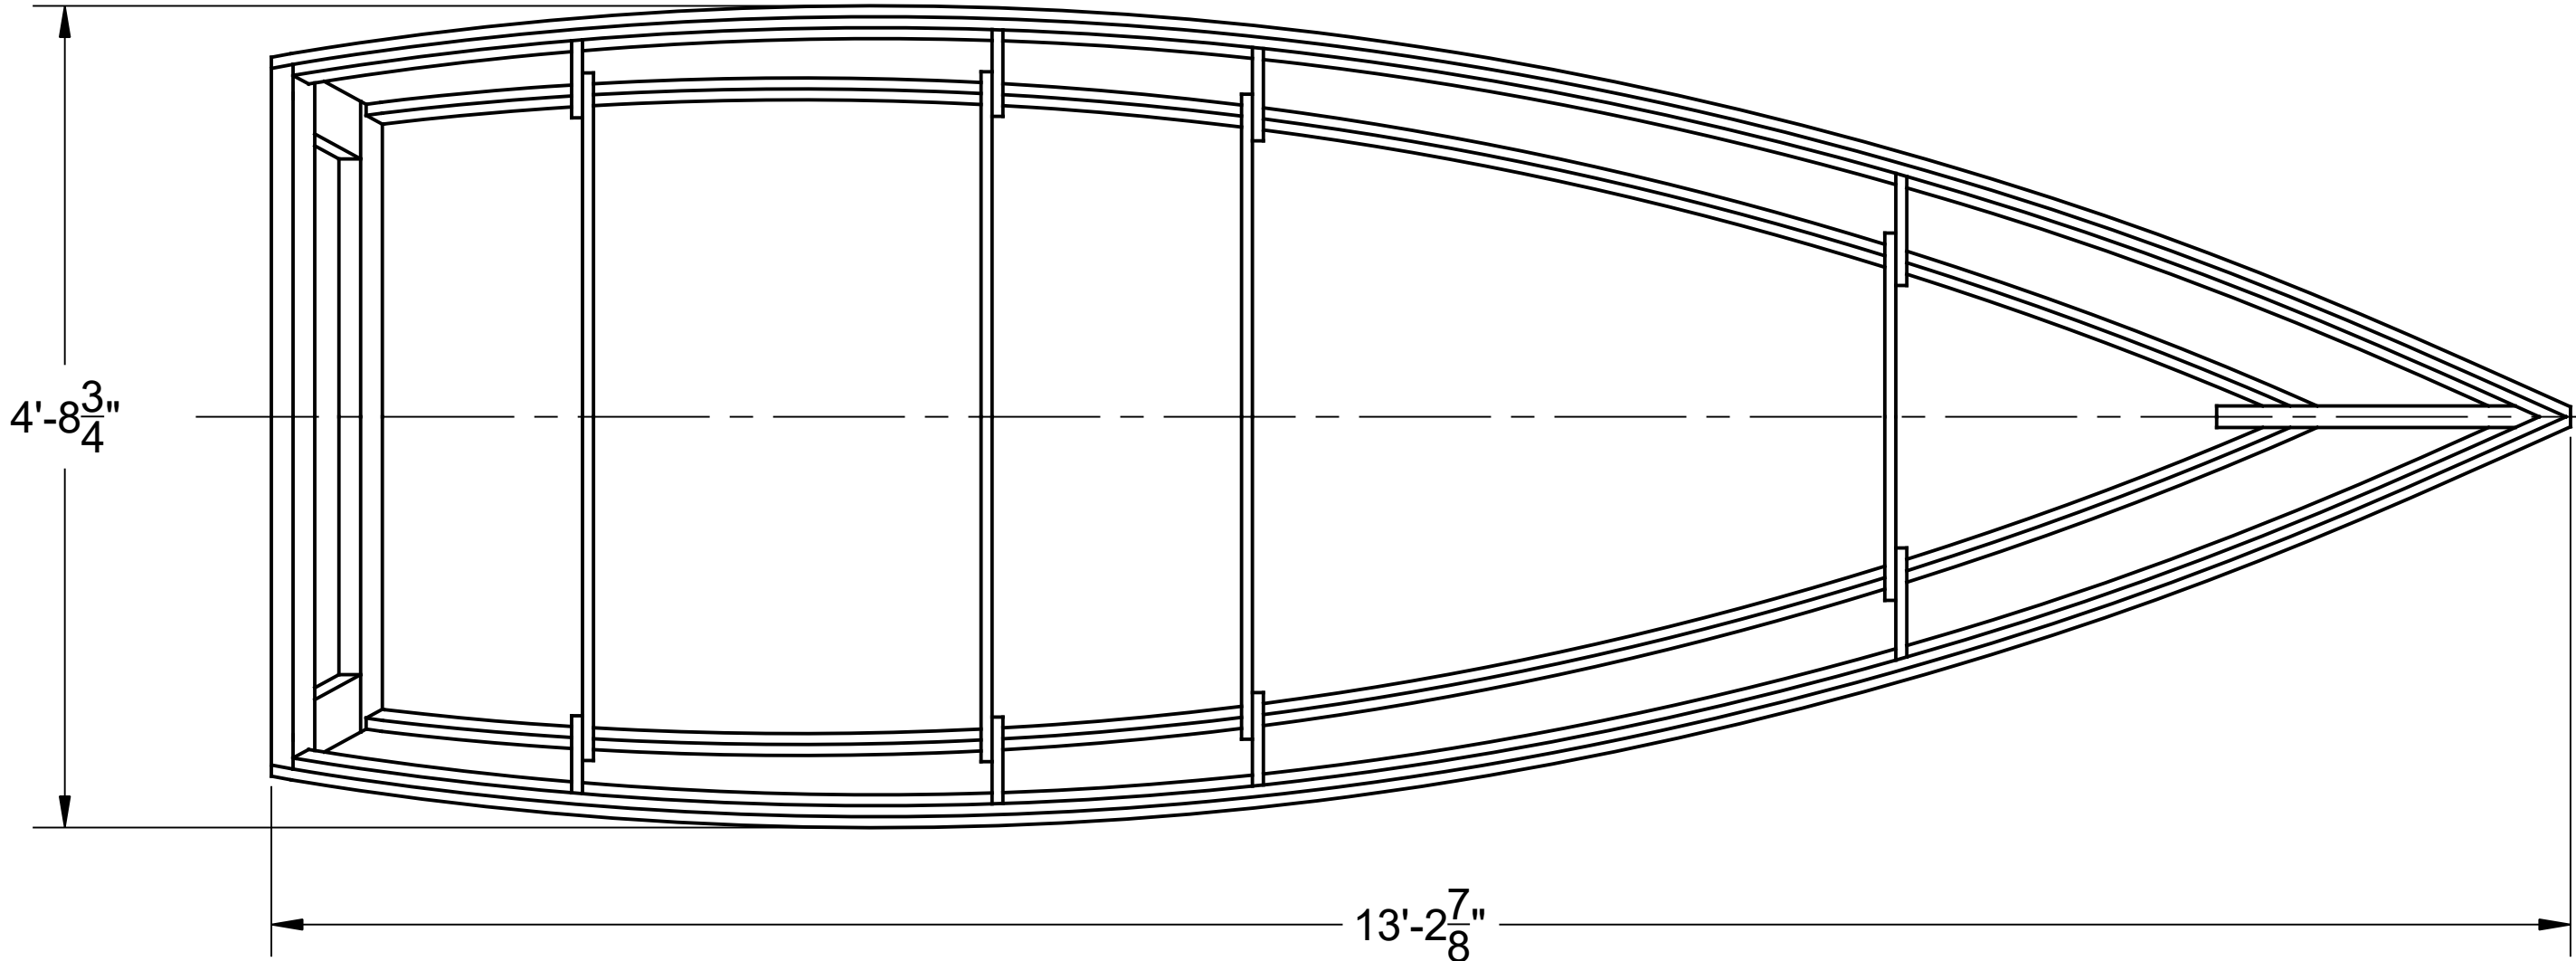

SPECIFICATIONS	
MAX. DISPLACEMENT	1110 LBS
HULL WEIGHT	125 LBS
HP - MAXIMUM	9.9 HP
HP - RECOMMENDED	5 HP

A



Spira International, Inc.
Huntington Beach, California

WALDEN
13' ROW / POWER SKIFF


DRAWN BY: J. SPIRA DATE: 03/06/16 DRAWING NO. WALD01

SCALE 1" = 1' SHEET OF

4 3 2 1

NOTICE
THIS DRAWING CONTAINS A PROPRIETARY DESIGN ASSIGNED TO SPIRA INTERNATIONAL, INC. ALL RIGHTS TO DUPLICATE, TRANSFER OR USE ARE EXPRESSLY RESERVED BY SPIRA INTERNATIONAL. THE BUYER IS LICENSED TO BUILD ONE ASSEMBLY FROM THESE PLANS.

REVISIONS				
ZONE	LTR	DESCRIPTION	DATE	APPROVED

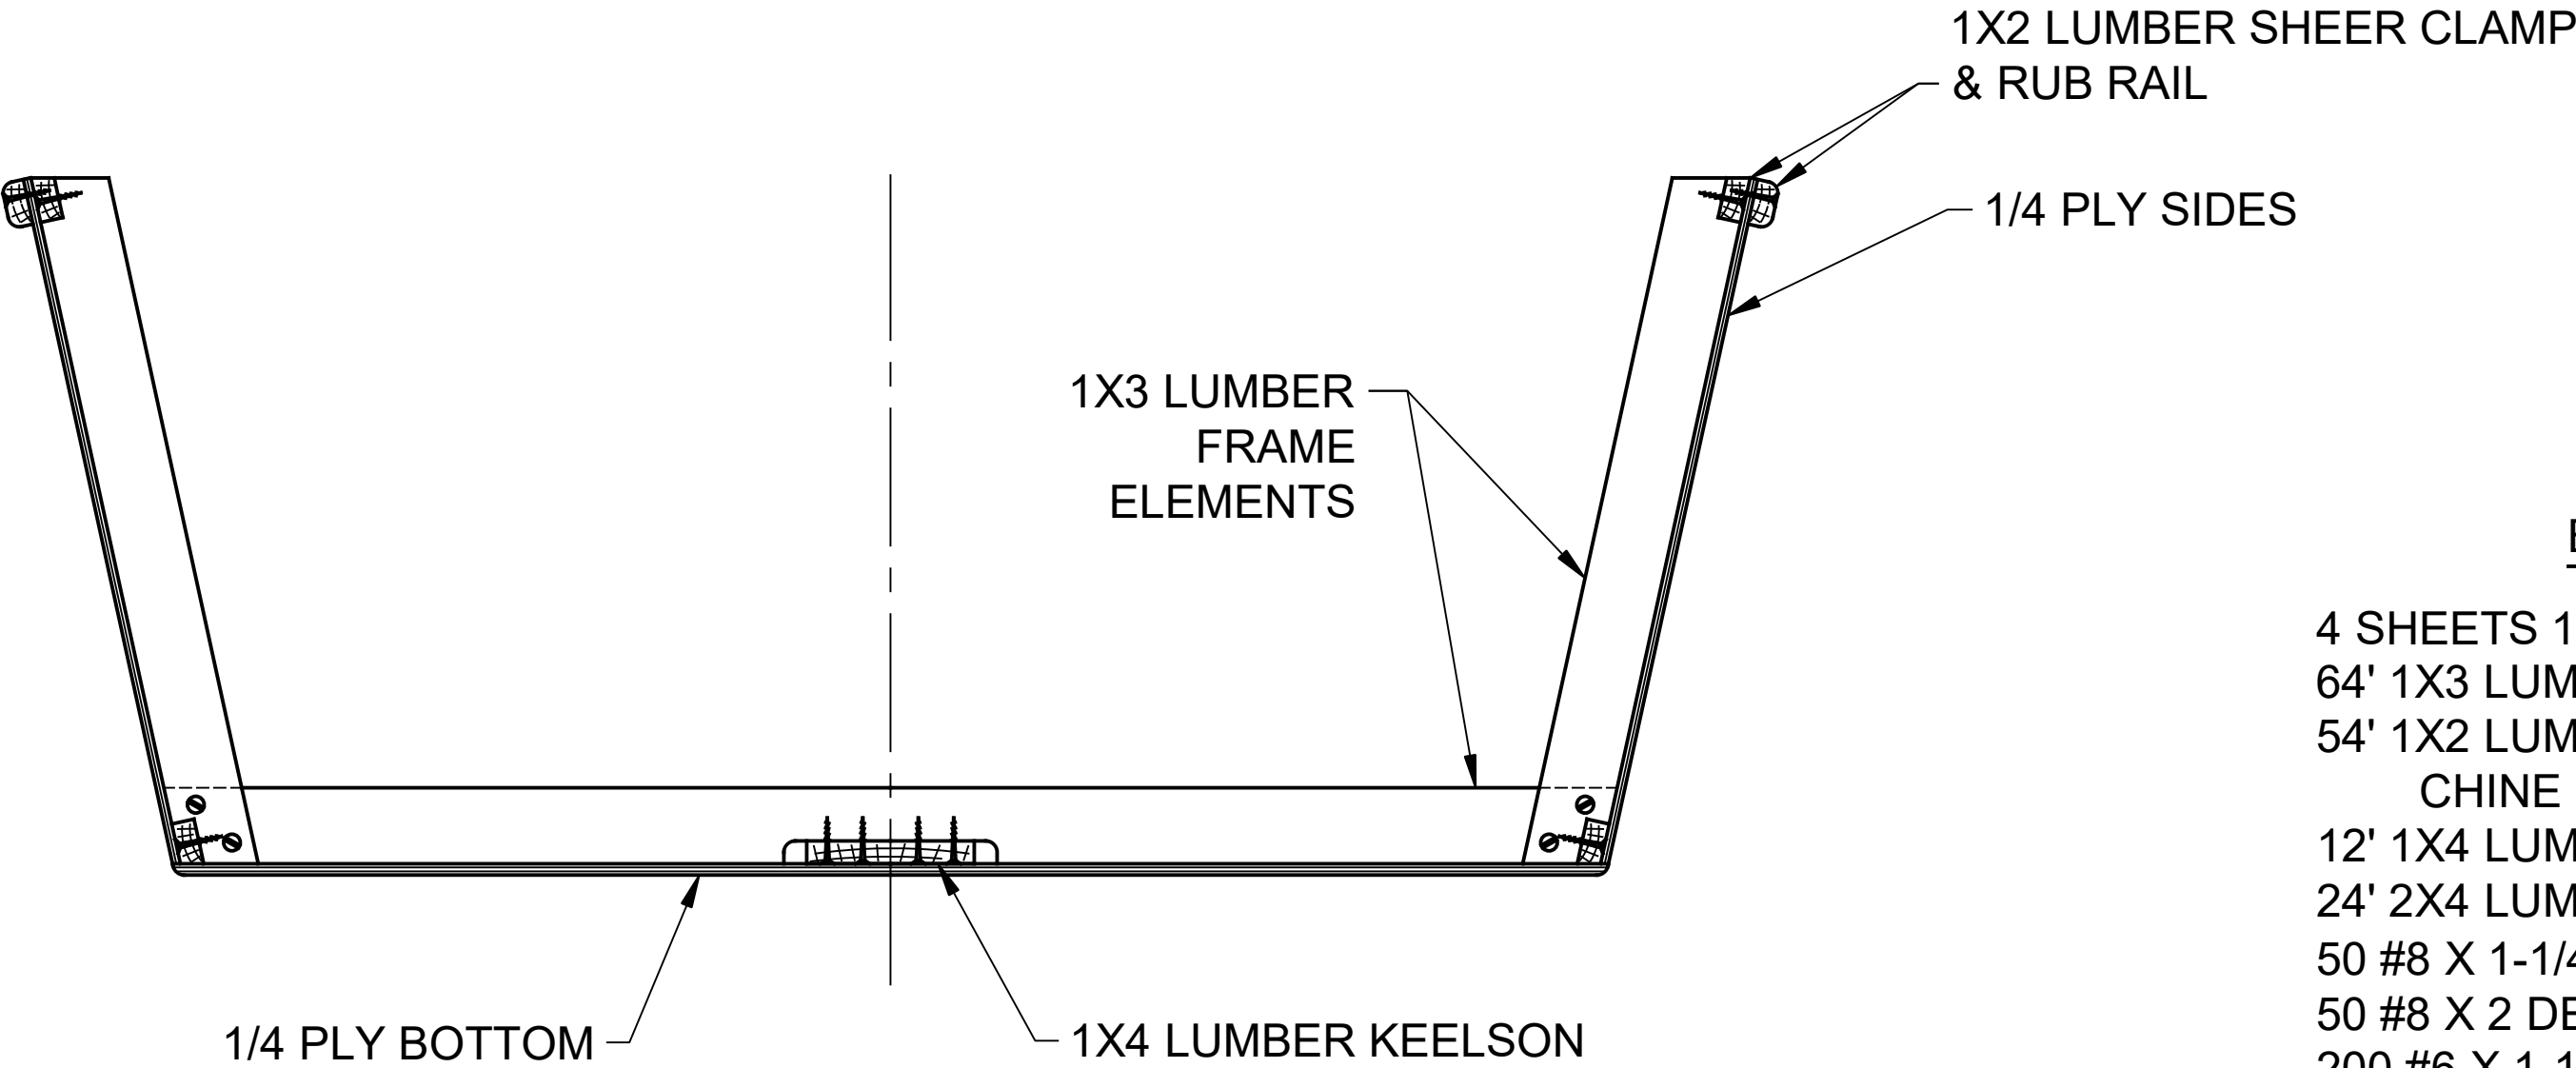

BILL OF MATERIALS

4 SHEETS 1/4" PLY FOR SIDES & BOTTOM
64' 1X3 LUMBER FOR FRAMES
54' 1X2 LUMBER FOR SHEER CLAMP
CHINE LOG AND RUB RAILS
12' 1X4 LUMBER FOR KEELSON
24' 2X4 LUMBER FOR TRANSOM & STEM
50 #8 X 1-1/4" DECK SCREWS
50 #8 X 2 DECK SCREWS
200 #6 X 1-1/4 DECK SCREWS
3 QTS EPOXY RESIN
7 YDS 6 OZ FIBERGLASS CLOTH

NOTES:

1. YOU MAY SCARF TOGETHER SHORTER PIECES TO CREATE THE LONGITUDINAL ELEMENTS.
2. NOMINAL LUMBER SIZED CALLED OUT, E.G. A 2 X 4 LUMBER IS ACTUAL SIZE 1-1/2" X 3-1/2"

FASTENING SCHEDULE

FRAME TO FRAME: #8 X 1-1/4 DECK SCREWS
LONGITUDINAL TO FRAME: #8 X 2 DECK SCREWS
PLANKING TO FRAME: #6 X 1-1/4 DECK SCREWS



Spira International, Inc.
Huntington Beach, California

WALDEN
13' ROW / POWER SKIFF

DRAWN BY: J. SPIRA	DATE: 03/06/16	DRAWING NO. WALD01
SCALE 1" = 1'	SHEET OF	