

4

3

2


1

NOTICE  
THIS DRAWING CONTAINS A PROPRIETARY DESIGN ASSIGNED TO SPIRA INTERNATIONAL, INC. ALL RIGHTS TO DUPLICATE, TRANSFER OR USE ARE EXPRESSLY RESERVED BY SPIRA INTERNATIONAL. THE BUYER IS LICENSED TO BUILD ONE ASSEMBLY FROM THESE PLANS.

| REVISIONS |     |             |      |          |
|-----------|-----|-------------|------|----------|
| ZONE      | LTR | DESCRIPTION | DATE | APPROVED |
|           |     |             |      |          |

D

D

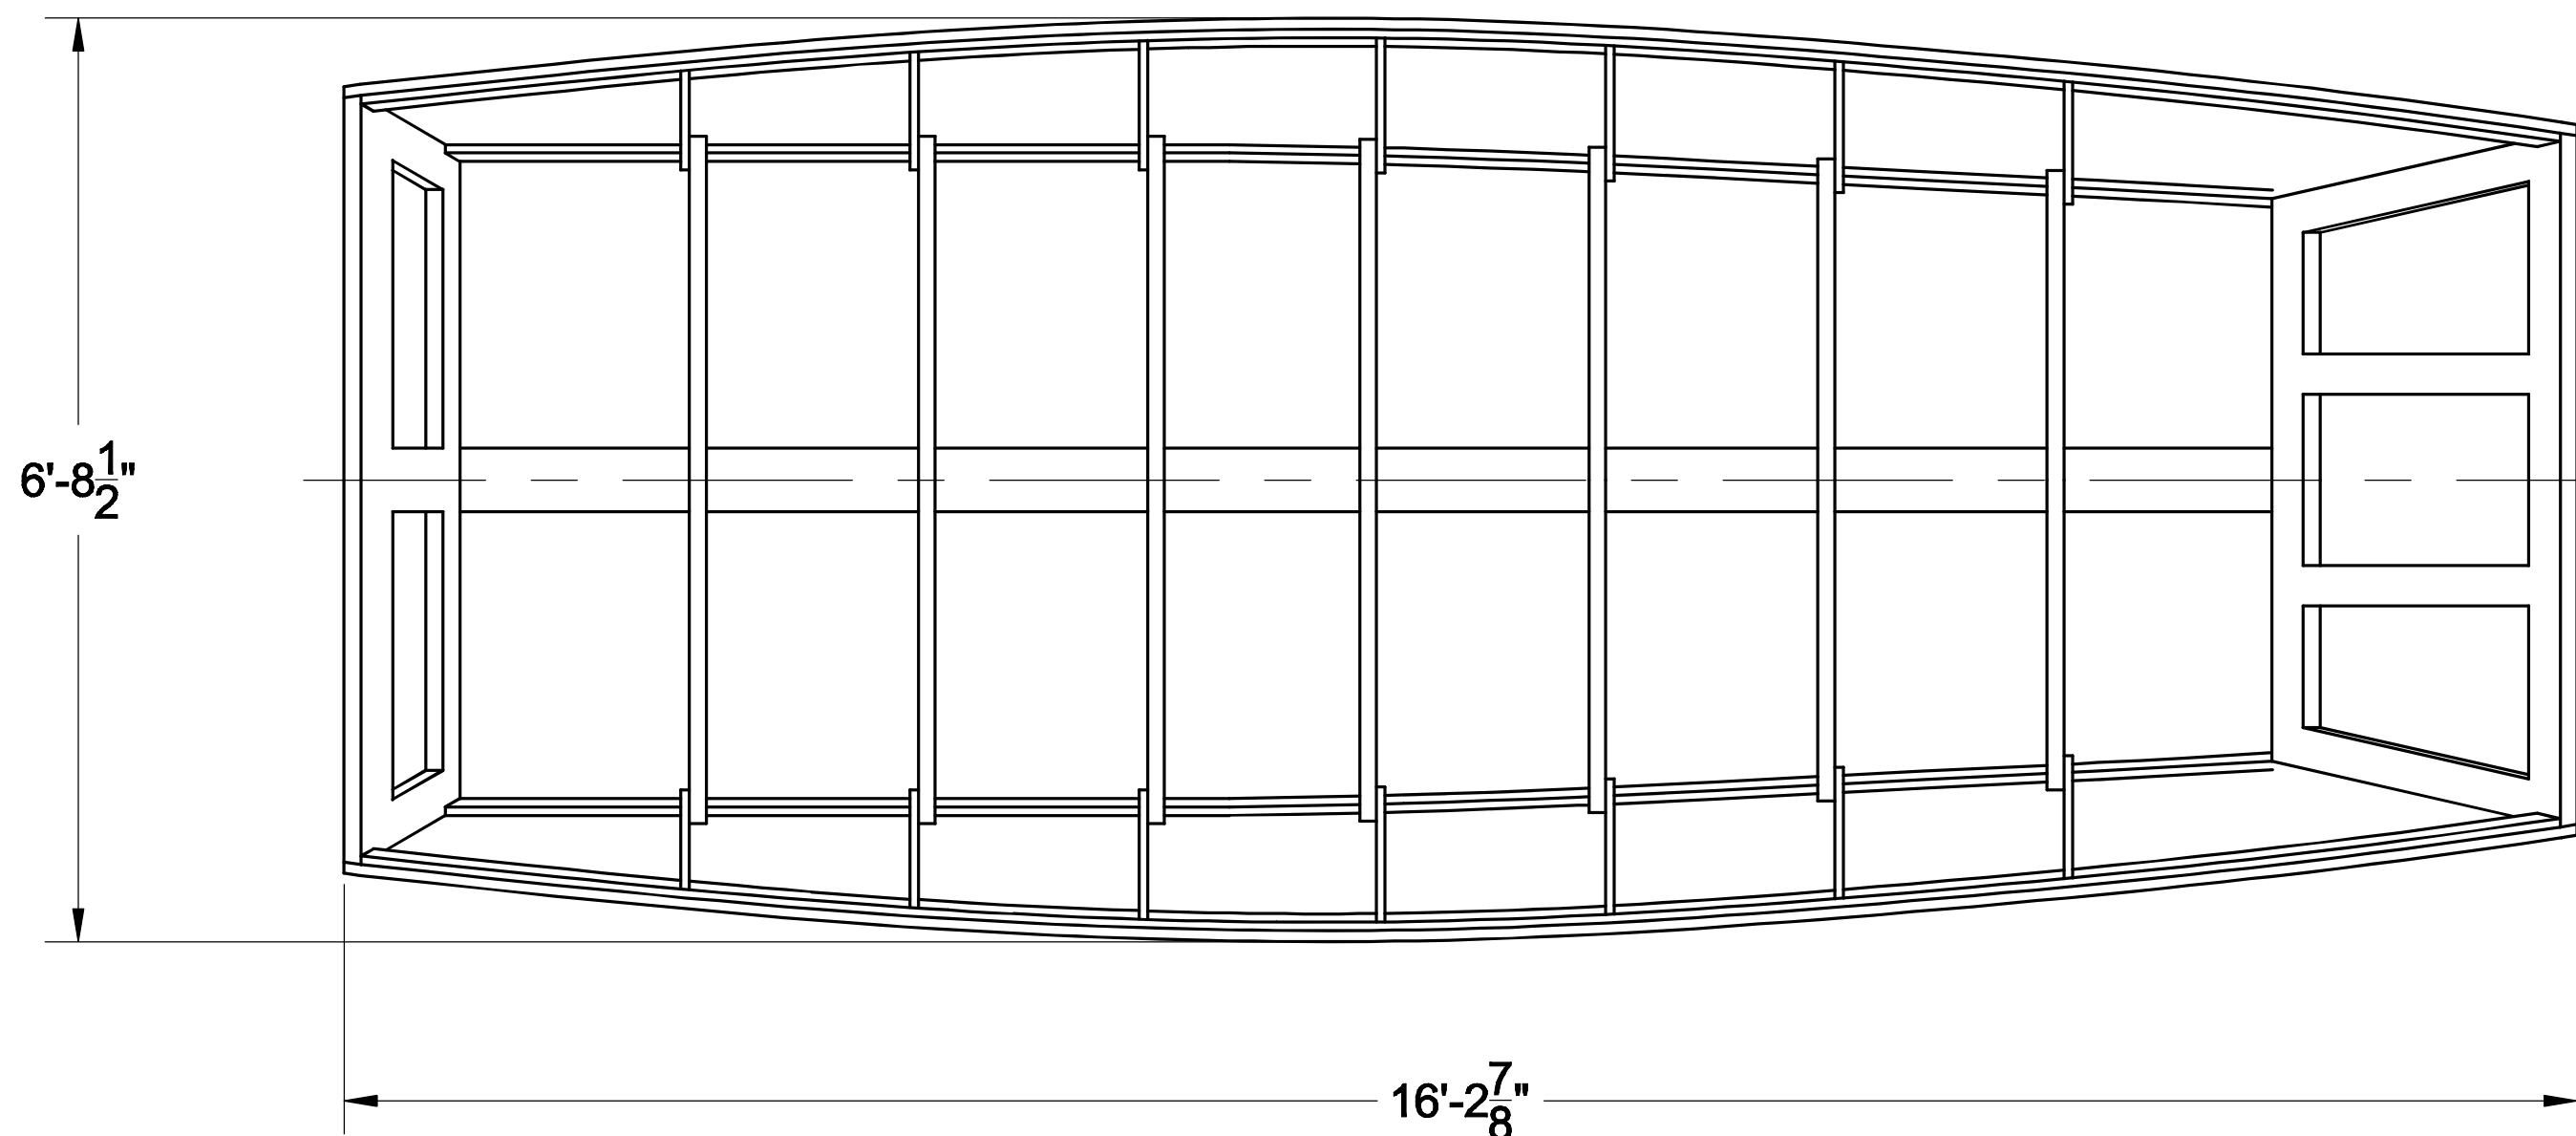


C

C

B

B

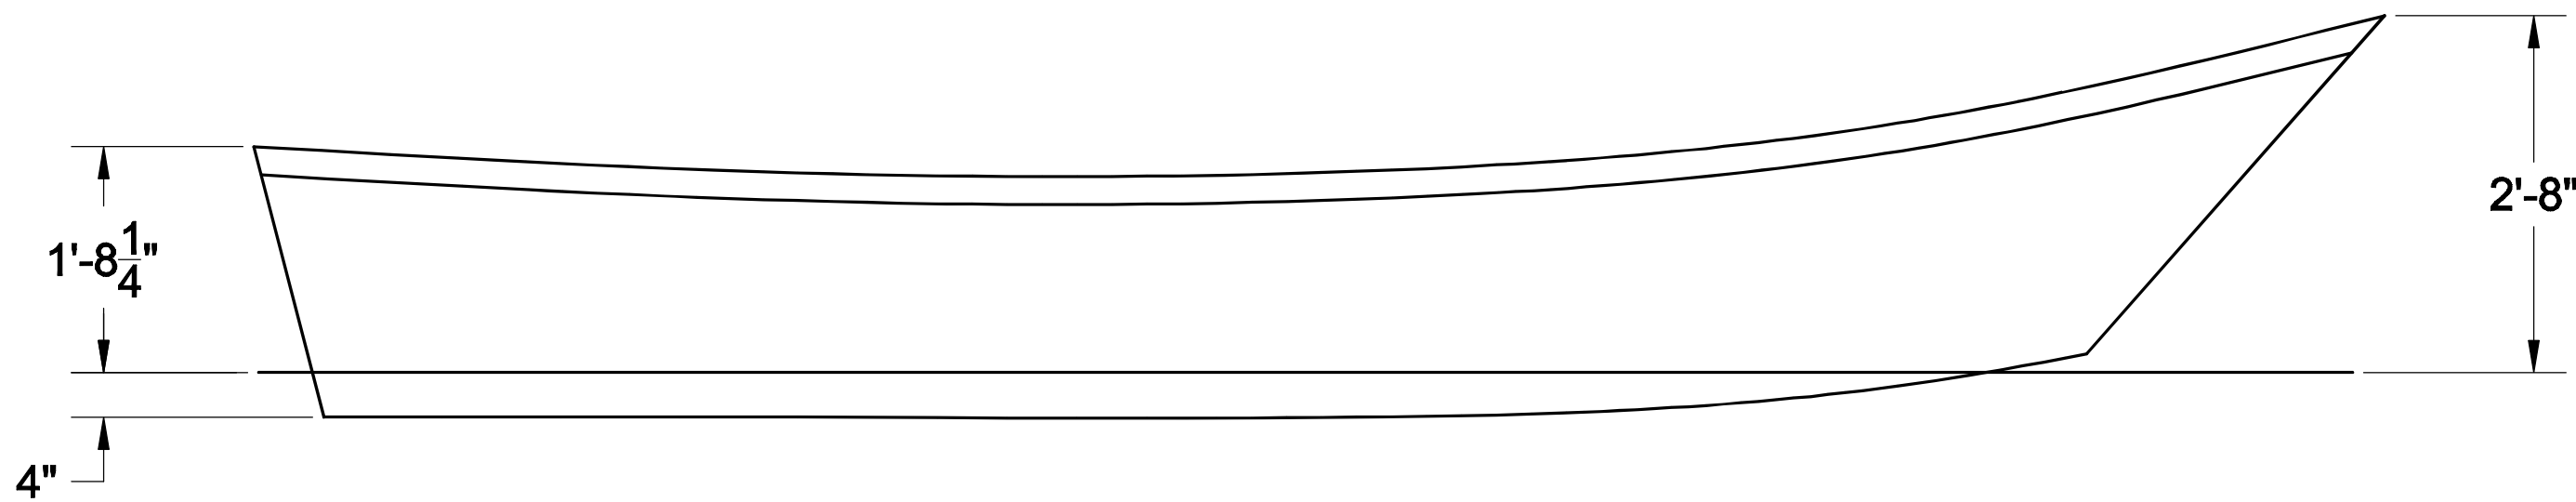

A

A

4

3

2

1

**Spira International, Inc.**  
*Huntington Beach, California*


**16' WYE RIVER  
GARVEY**

|                            |                   |                       |
|----------------------------|-------------------|-----------------------|
| DRAWN BY:<br>J. SPIRA      | DATE:<br>11/26/12 | DRAWING NO.<br>WYER01 |
| SCALE<br>3/4" = 1' & NOTED | SHEET<br>OF       |                       |

4 3 2 1

**NOTICE**  
THIS DRAWING CONTAINS A PROPRIETARY DESIGN ASSIGNED TO SPIRA INTERNATIONAL, INC. ALL RIGHTS TO DUPLICATE, TRANSFER OR USE ARE EXPRESSLY RESERVED BY SPIRA INTERNATIONAL. THE BUYER IS LICENSED TO BUILD ONE ASSEMBLY FROM THESE PLANS.

| REVISIONS |     |             |      |          |
|-----------|-----|-------------|------|----------|
| ZONE      | LTR | DESCRIPTION | DATE | APPROVED |
|           |     |             |      |          |

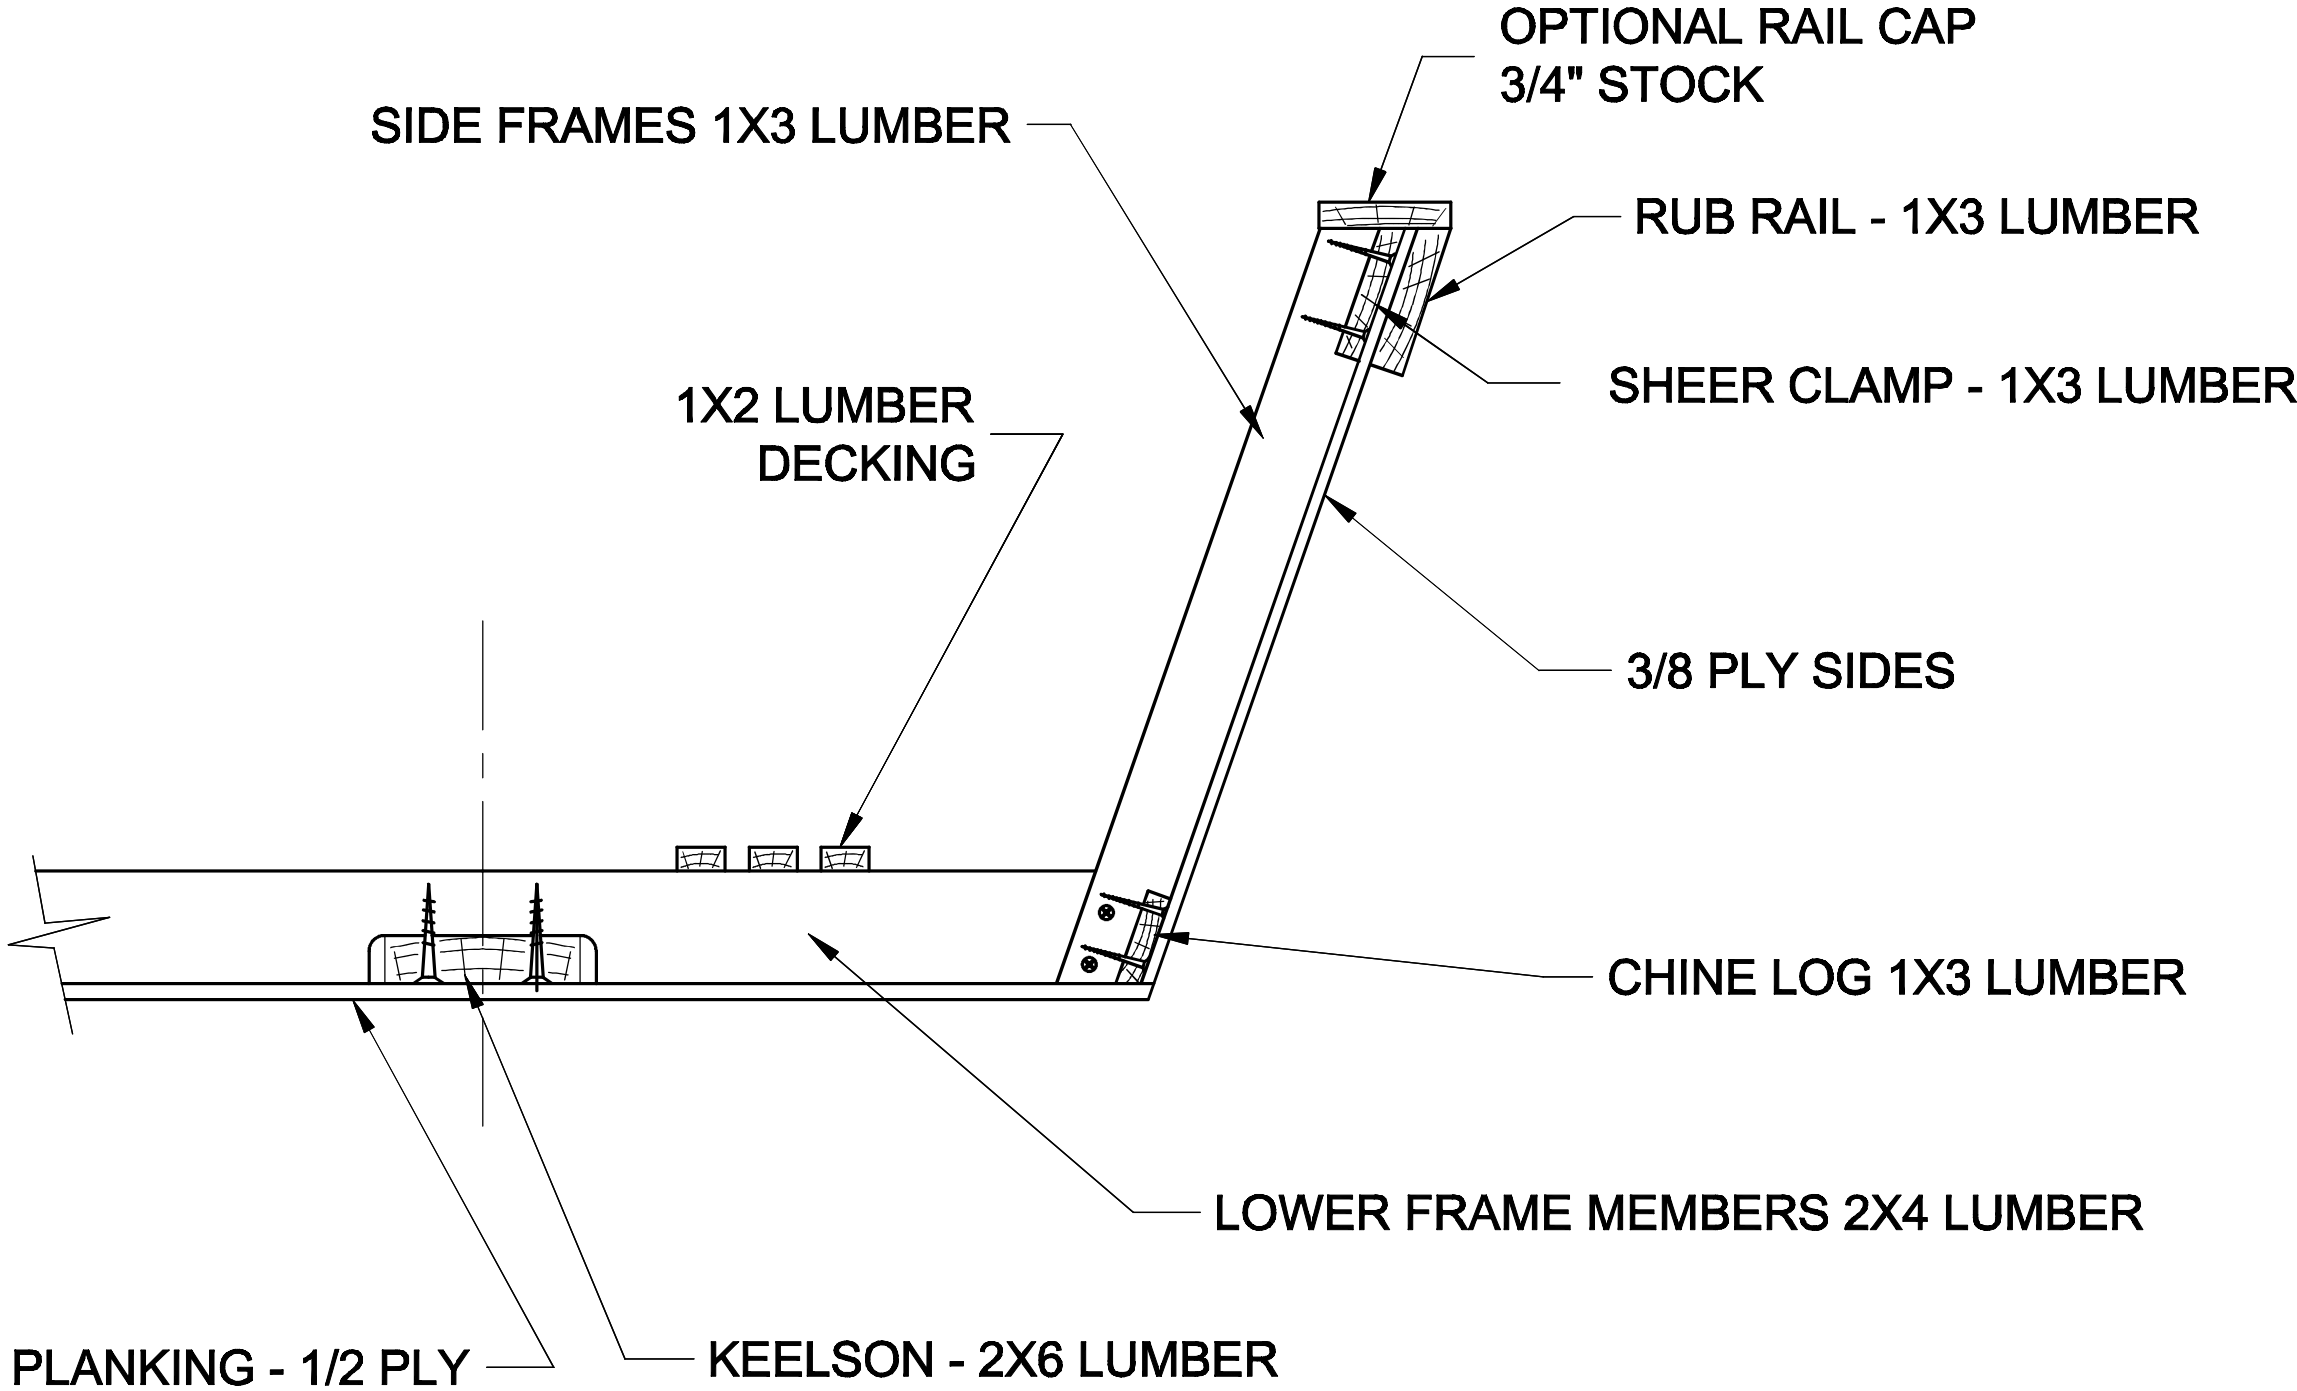

**BILL OF MATERIALS**

FRAMES: 60 FT 2X4S  
FRAMES: 20 FT 2X6S  
FRAMES, S/C & C/L: 118' 1X4S  
SIDES: 4 SHTS 3/8" PLY  
BOTTOM: 3 SHTS 1/2" PLY  
GLASS: 22 YDS - 6 OZ CLOTH  
EPOXY: 2 GAL  
100 - #10 X 2-1/2" DECK SCREWS  
100 - #10 X 2" DECK SCREWS  
400 - #8 X 1-1/2" SCREWS

**OPTIONAL**

DECKING: 250 FT 1X2S  
RAIL CAP: 32' 1X6

**FASTENING SCHEDULE**

2x FRAME TO 2x FRAME: #10 X 2 -1/2 DECK SCREWS  
1x FRAME TO 2x FRAME: #10 X 2 DECK SCREWS  
LONGITUDINAL TO FRAME: #8 X 1-1/2 DECK SCREWS  
PLANKING TO FRAME: #8 X 1-1/2 DECK SCREWS

TYPICAL CONSTRUCTION METHOD  
ALL FRAME STATIONS  
SCALE 2" = 1'

**NOTES:**

1. YOU MAY SCARF TOGETHER SHORTER PIECES TO CREATE THE LONGITUDINAL ELEMENTS.
2. NOMINAL LUMBER SIZED CALLED OUT, E.G. A 2 X 4 LUMBER IS ACTUAL SIZE 1-1/2" X 3-1/2"

|                                                                         |  |                               |                              |
|-------------------------------------------------------------------------|--|-------------------------------|------------------------------|
| <b>Spira International, Inc.</b><br><i>Huntington Beach, California</i> |  |                               |                              |
| <b>16' WYE RIVER<br/>GARVEY</b>                                         |  |                               |                              |
| DRAWN BY:<br>J. SPIRA                                                   |  | DATE:<br>11/26/12             | DRAWING NO.<br><b>WYER02</b> |
| SCALE    3/4" = 1' & NOTED                                              |  | SHEET                      OF |                              |