

4

3




2

1

NOTICE

THIS DRAWING CONTAINS A PROPRIETARY DESIGN ASSIGNED TO SPIRA INTERNATIONAL, INC. ALL RIGHTS TO DUPLICATE, TRANSFER OR USE ARE EXPRESSLY RESERVED BY SPIRA INTERNATIONAL. THE BUYER IS LICENSED TO BUILD ONE ASSEMBLY FROM THESE PLANS.

REVISIONS				
ZONE	LTR	DESCRIPTION	DATE	APPROVED

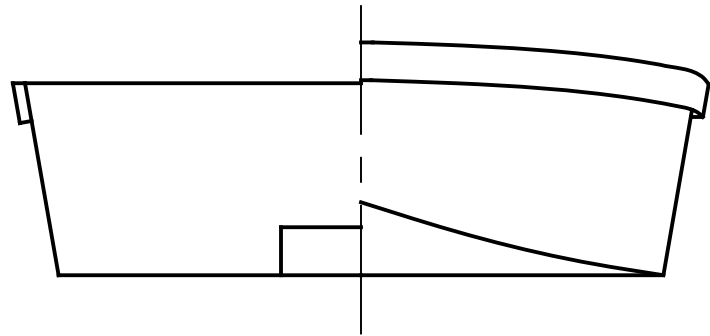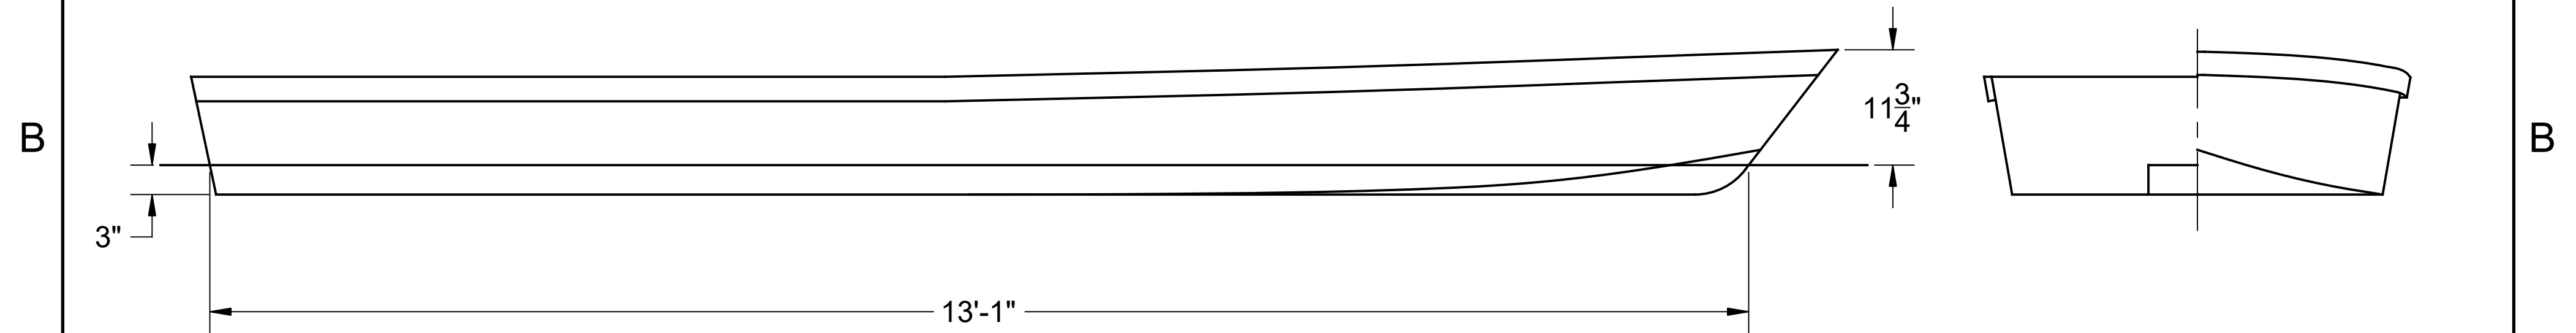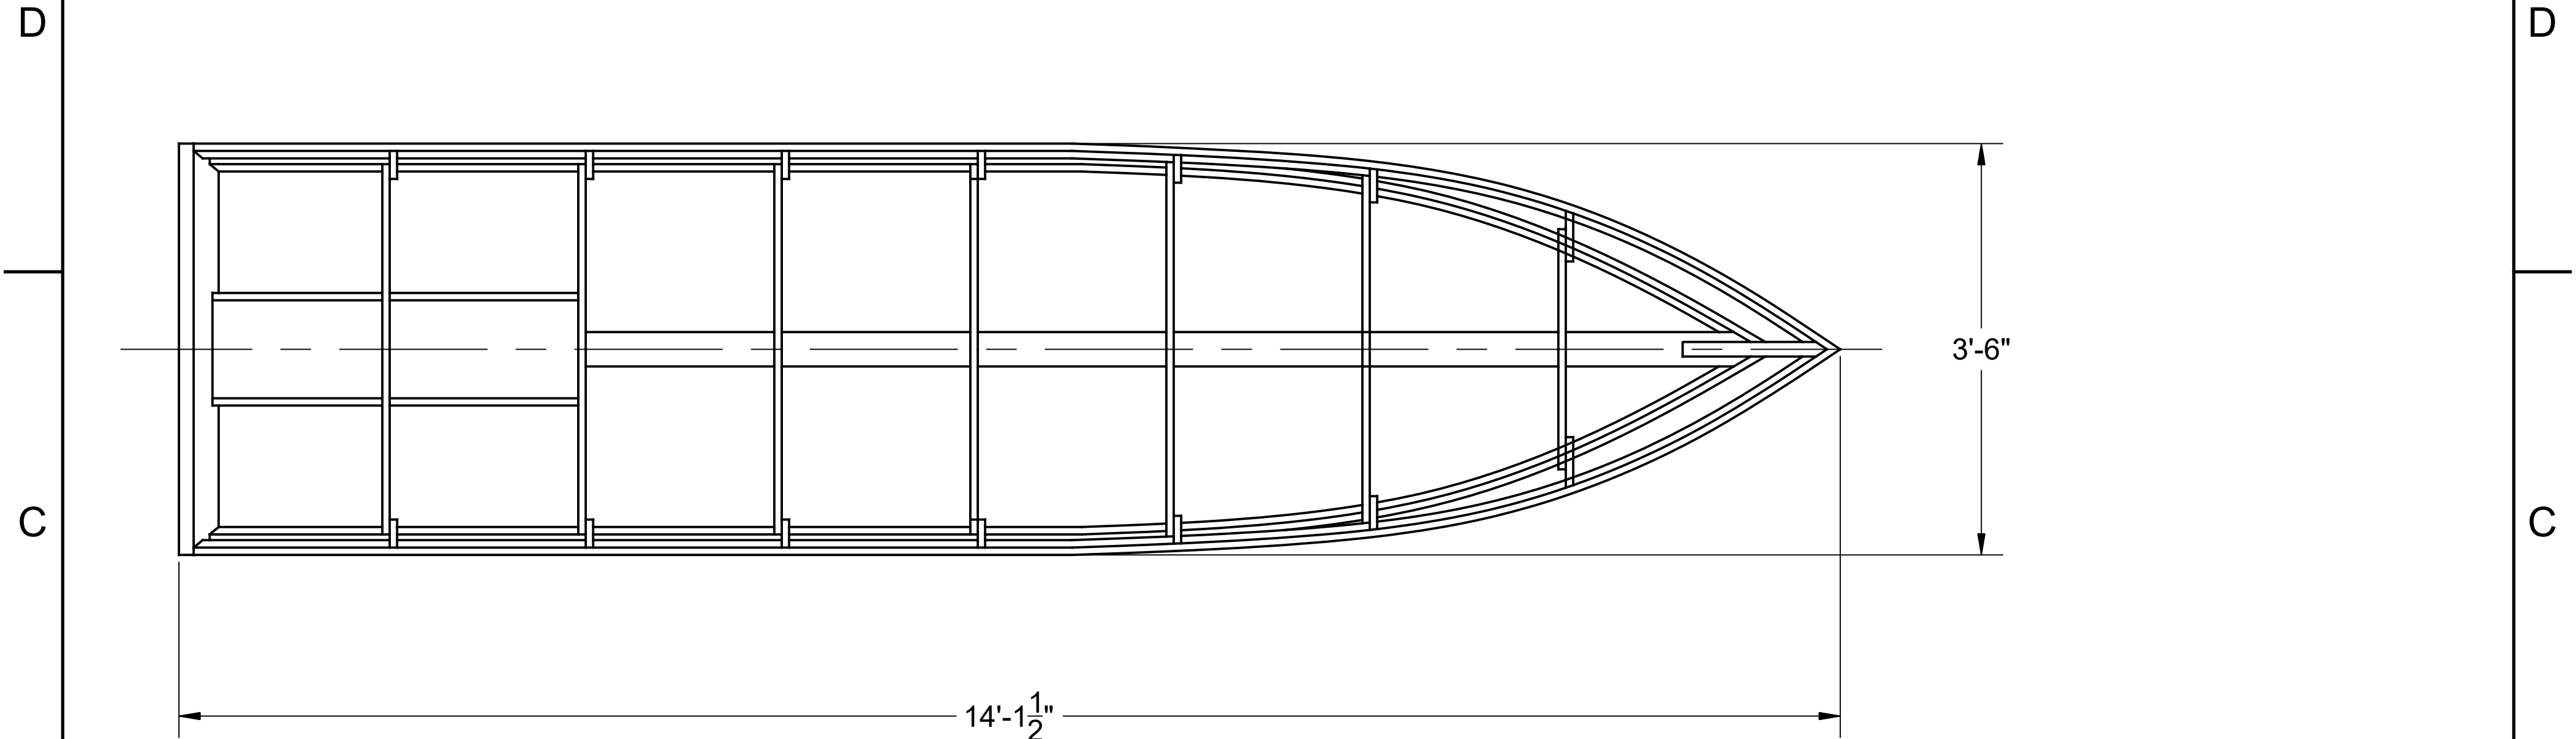

A

SPECIFICATIONS	
MAX. DISPLACEMENT	620 LBS
HULL WEIGHT	130 LBS
MAX. HP	10 HP
RECOMMENDED HP	7.5 HP

A



Spira International, Inc.
Huntington Beach, California

CHALMETTE
14' BAYOU & FLATS BOAT

DRAWN BY: J. SPIRA	DATE: 12/02/14	DRAWING NO. CHAL01
SCALE 1" = 1' & NOTED		SHEET OF

4

3

2

1

NOTICE

THIS DRAWING CONTAINS A PROPRIETARY DESIGN ASSIGNED TO SPIRA INTERNATIONAL, INC. ALL RIGHTS TO DUPLICATE, TRANSFER OR USE ARE EXPRESSLY RESERVED BY SPIRA INTERNATIONAL. THE BUYER IS LICENSED TO BUILD ONE ASSEMBLY FROM THESE PLANS.

REVISIONS				
ZONE	LTR	DESCRIPTION	DATE	APPROVED

D

C

B

A

4

3

2

1

CASTING DECKS
1/2 PLYWOOD

CENTER DECKING
1 X 2 LUMBER
1/2 PLY OPTIONAL

FRAMING
1 X 3 LUMBER

RAIL CAP
3/4 THICK LUMBER

RUB RAIL
1 X 2 LUMBER

SHEER CLAMP
1 X 2 LUMBER

SIDE PLANKING
1/4" PLYWOOD

CHINE LOG
1 X 2 LUMBER

BOTTOM PLANKING
1/4 PLYWOOD

KEELSON
2 X 4 LUMBER

FRAME BOTTOMS
1X4 LUMBER

BILL OF MATERIALS

4 SHEETS 1/4" PLY
3 SHEETS 1/2" PLY
50' 1X3 LUMBER FOR FRAMES
29' 1X4 LUMBER FOR FRAMES
80' 1X2 LUMBER FOR SHEER CLAMP &
CHINE LOG
38' 2X4 LUMBER FOR KEELSON & TRANSOM STEM
2' 1X12 LUMBER FOR TRANSOM
130' 1X2 LUMBER FOR DECKING
(OPTIONAL DECKING 1 SHT 1/2" PLYWOOD)
50 - #10 X 2-1/2 DECK SCREWS
100 - #8 X 1-1/4 DECK SCREWS
100 - #8 X 2 DECK SCREWS
400 - #6 X 1 DECK SCREWS
1 GAL EPOXY RESIN
12 YDS 6 OZ FIBERGLASS CLOTH

FASTENING SCHEDULE

KEELSON TO FRAMES: #10 X 2-1/2 DECK SCREWS
FRAMES TO FRAMES: #8 X 1-1/4 DECK SCREWS
LONGITUDINALS: #8 X 2 DECK SCREWS
PLY TO FRAMES: #6 X 1 DECK SCREWS

NOTES:

1. YOU MAY SCARF TOGETHER SHORTER PIECES TO CREATE THE LONGITUDINAL ELEMENTS.

2. NOMINAL LUMBER SIZED CALLED OUT, E.G. A 1 X 3 LUMBER IS ACTUAL SIZE 3/4" X 2-1/2"

 Spira International, Inc.
Huntington Beach, California

CHALMETTE
14' BAYOU & FLATS BOAT

DRAWN BY: J. SPIRA DATE: 12/05/14 DRAWING NO. CHAL02

SCALE 2" = 1' SHEET OF