


NOTICE
THIS DRAWING CONTAINS A PROPRIETARY DESIGN ASSIGNED TO SPIRA INTERNATIONAL, INC. ALL RIGHTS TO DUPLICATE, TRANSFER OR SELL THIS DESIGN ARE EXPRESSLY RESERVED. THE BUYER IS LICENSED TO BUILD ONE ASSEMBLY FROM THESE PLANS.

REVISIONS				
ZONE	LTR	DESCRIPTION	DATE	APPROVED

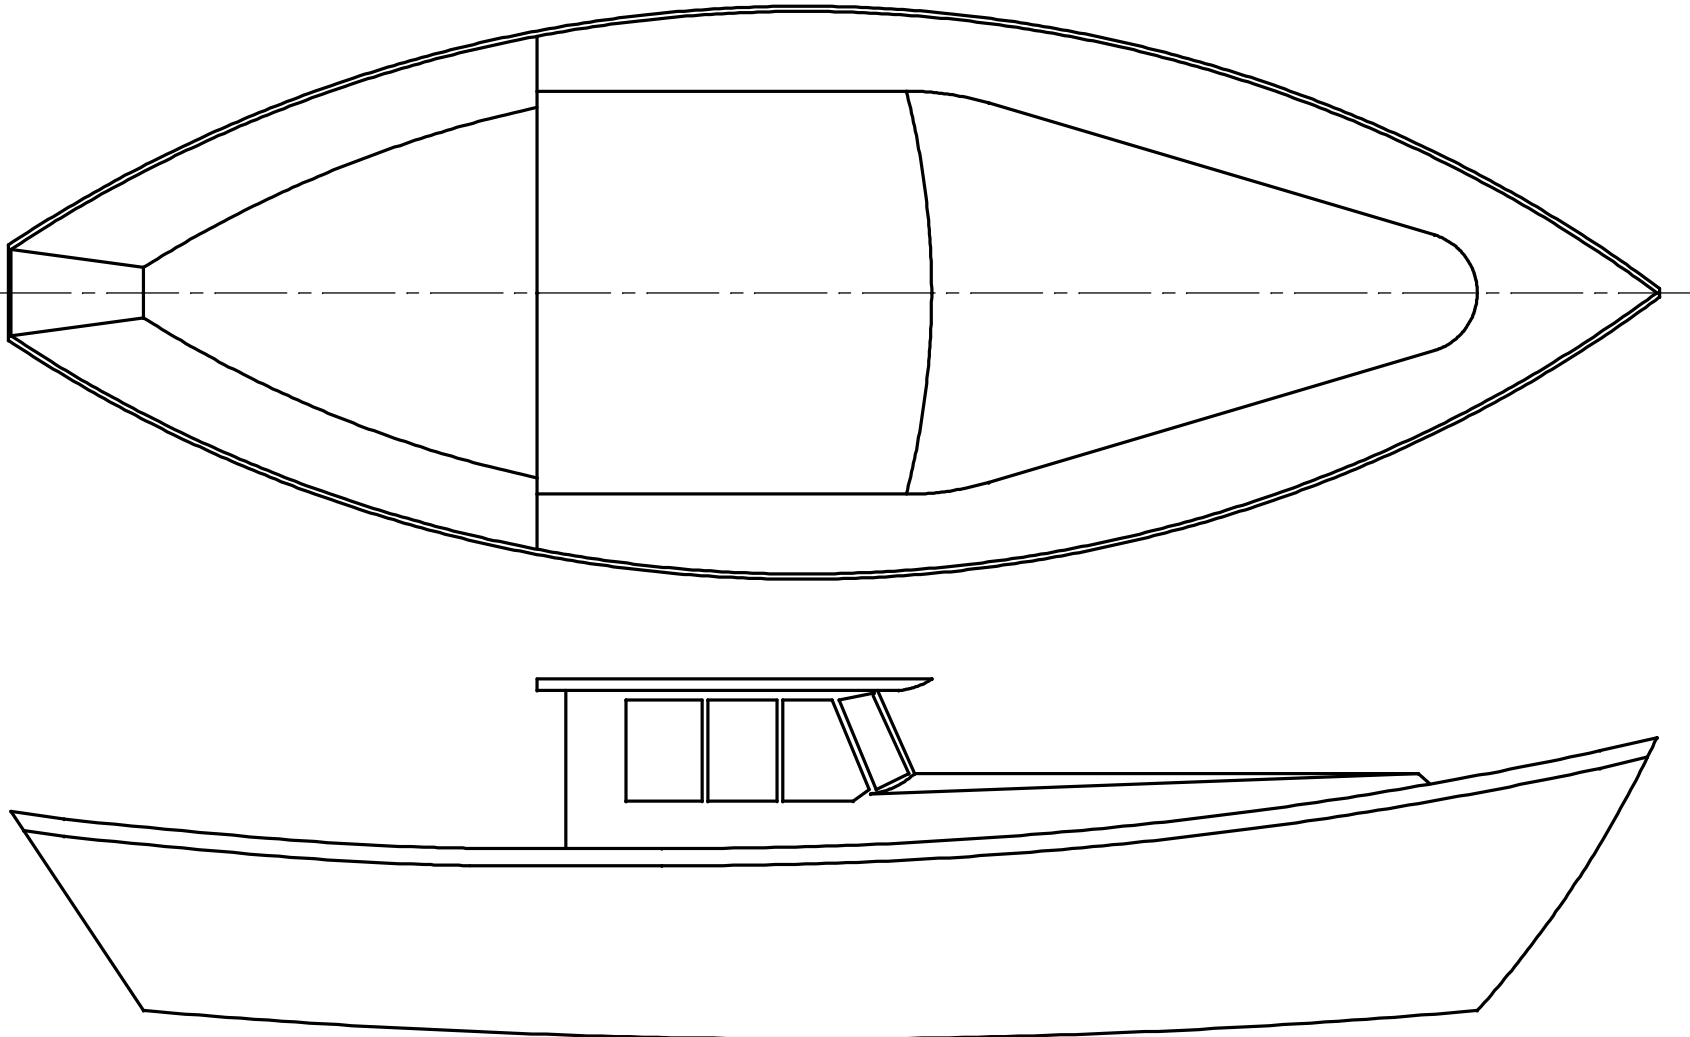

Spira International, Inc.
Huntington Beach, California

LONE STAR
34' GRAND BANKS DORY

DRAWN BY:
J. SPIRA

DATE:
09/15/09

DRAWING NO.
LONE01



SCALE 1/2" = 1' & NOTED

SHEET

OF

NOTICE
THIS DRAWING CONTAINS A PROPRIETARY DESIGN ASSIGNED TO SPIRA INTERNATIONAL, INC. ALL RIGHTS TO DUPLICATE, TRANSFER OR SELL THIS DESIGN ARE EXPRESSLY RESERVED. THE BUYER IS LICENSED TO BUILD ONE ASSEMBLY FROM THESE PLANS.

REVISIONS				
ZONE	LTR	DESCRIPTION	DATE	APPROVED

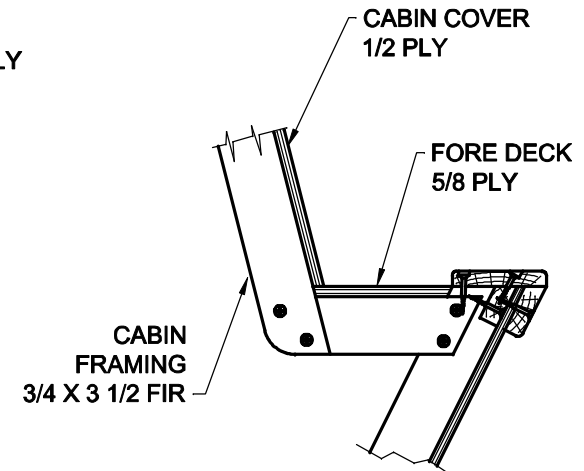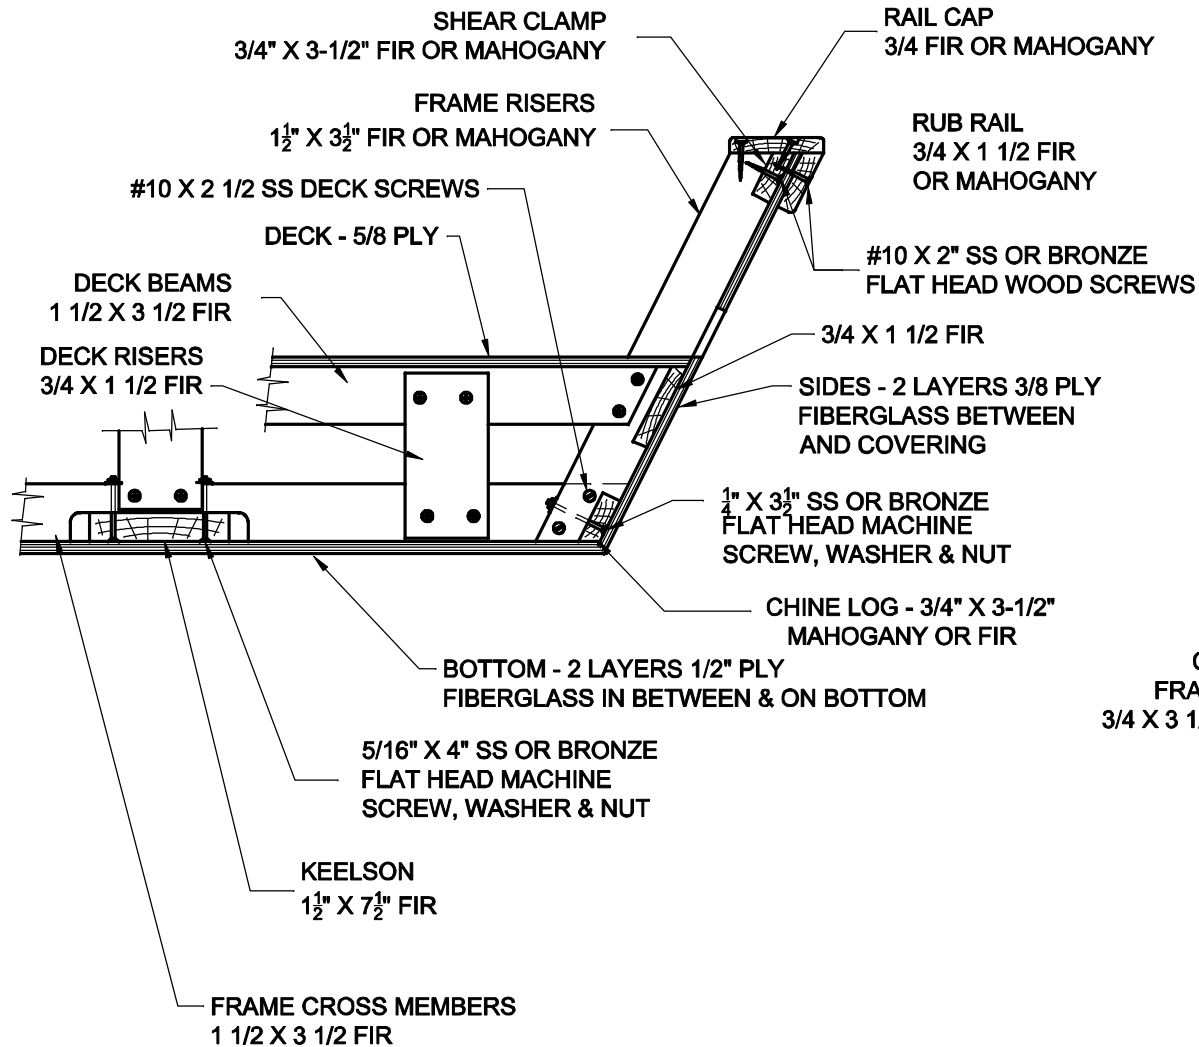

FORWARD SECTIONS
CABIN CONSTRUCTION
NO SCALE

CONSTRUCTION DETAIL
TYPICAL AT AFT SECTION
NO SCALE

Spira International, Inc.
Huntington Beach, California

LONE STAR
34' GRAND BANKS DORY

DRAWN BY: J. SPIRA	DATE: 09/15/09	DRAWING NO. LONE02
SCALE 1/2" = 1' & NOTED		SHEET OF