

4

3



2

1

NOTICE

THIS DRAWING CONTAINS A PROPRIETARY DESIGN ASSIGNED TO SPIRA INTERNATIONAL, INC. ALL RIGHTS TO DUPLICATE, TRANSFER OR USE ARE EXPRESSLY RESERVED BY SPIRA INTERNATIONAL. THE BUYER IS LICENSED TO BUILD ONE ASSEMBLY FROM THESE PLANS.

REVISIONS				
ZONE	LTR	DESCRIPTION	DATE	APPROVED

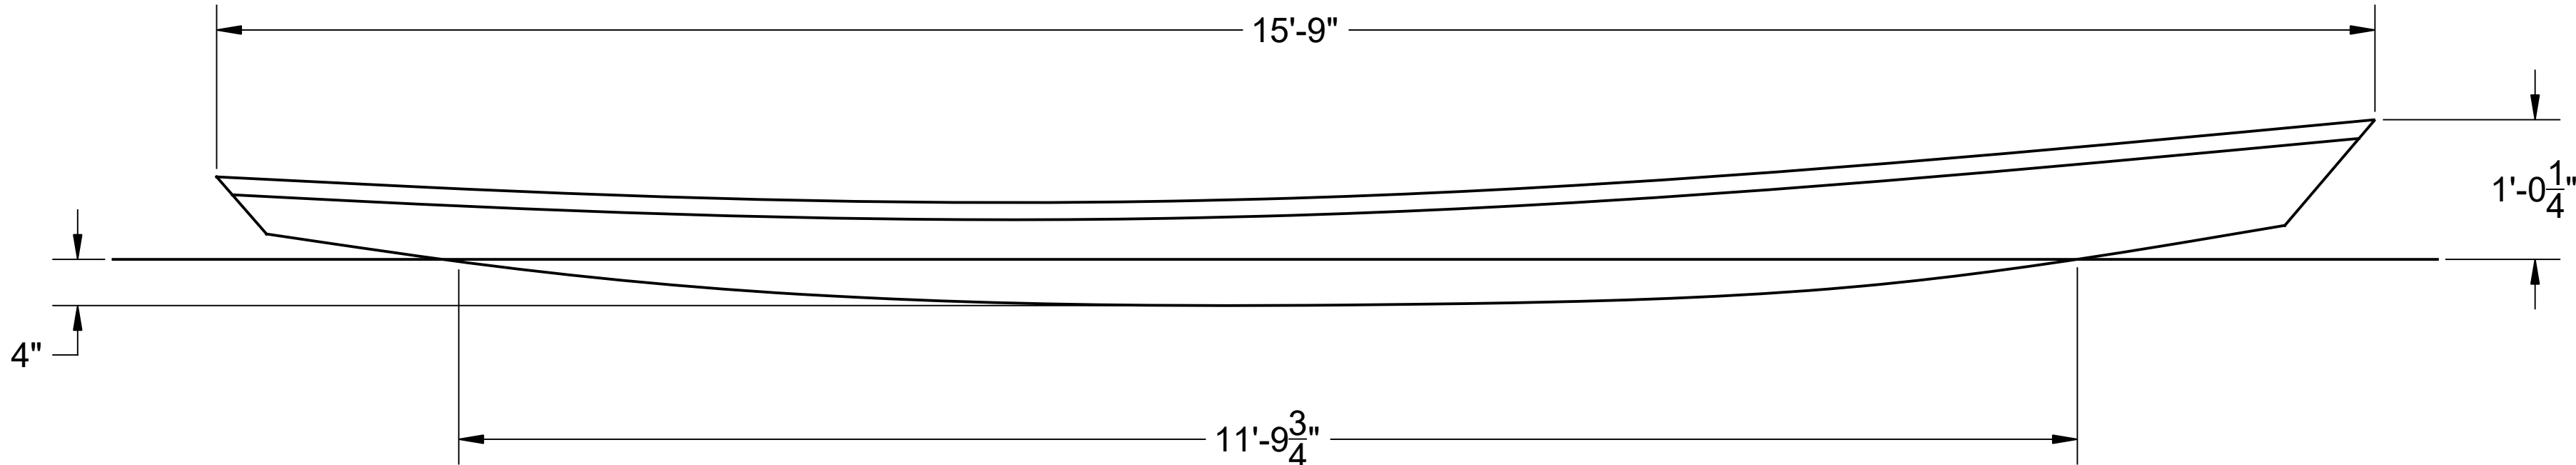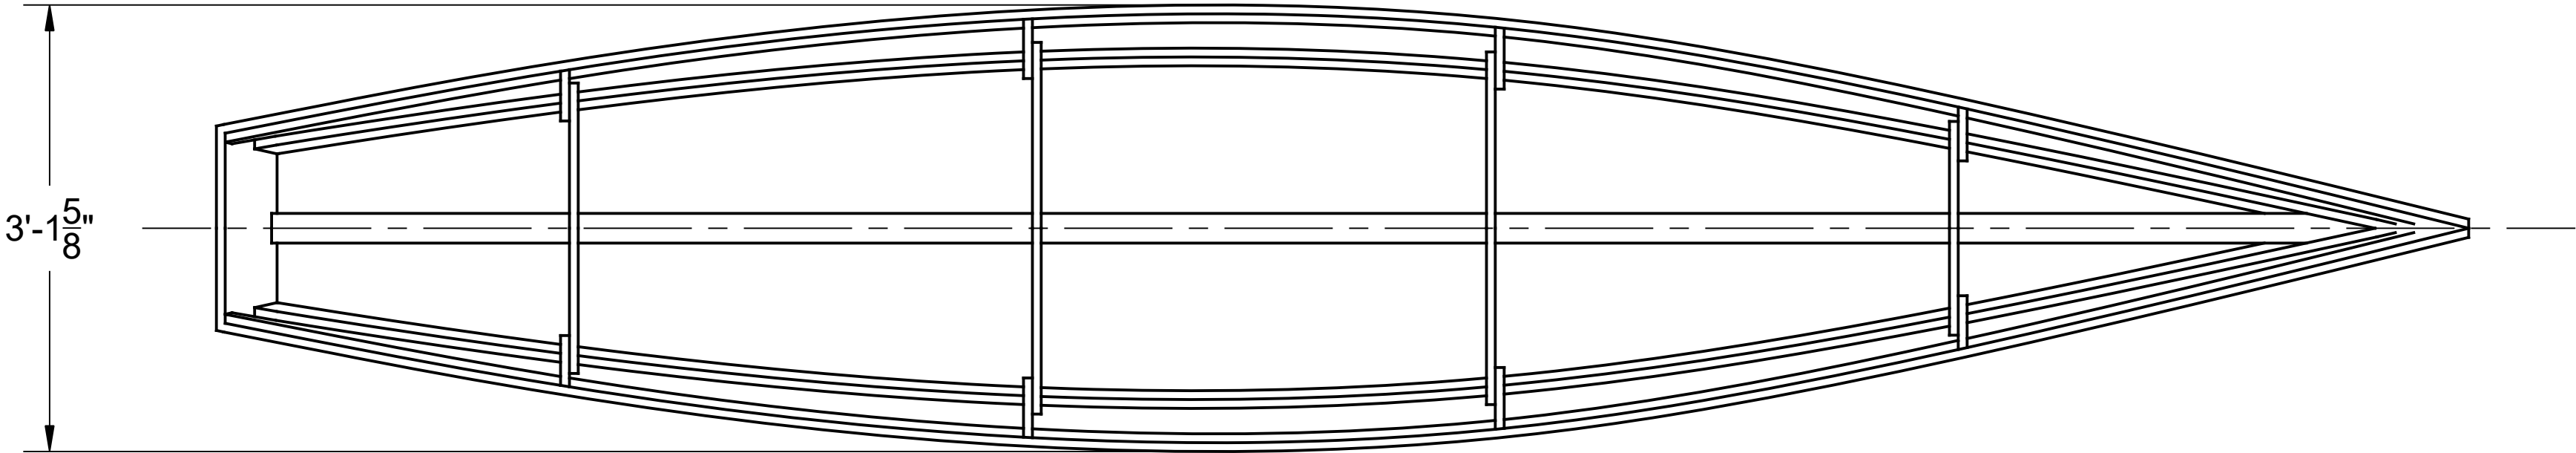

SPECIFICATIONS	
MAX. DISPLACEMENT	525 LBS
HULL WEIGHT	92 LBS
CALC. MAX. HORSEPOWER	TROLLING MOTOR
RECOMMENDED HP	PUSH POLE

A



Spira International, Inc.
Huntington Beach, California

RAILBIRD
16' CHESAPEAKE PUSHBOAT

DRAWN BY: J. SPIRA	DATE: 09/22/15	DRAWING NO. RAIL01
SCALE 1" = 1'		SHEET OF

4

3


2

1

NOTICE

THIS DRAWING CONTAINS A PROPRIETARY DESIGN ASSIGNED TO SPIRA INTERNATIONAL, INC. ALL RIGHTS TO DUPLICATE, TRANSFER OR USE ARE EXPRESSLY RESERVED BY SPIRA INTERNATIONAL. THE BUYER IS LICENSED TO BUILD ONE ASSEMBLY FROM THESE PLANS.

REVISIONS				
ZONE	LTR	DESCRIPTION	DATE	APPROVED

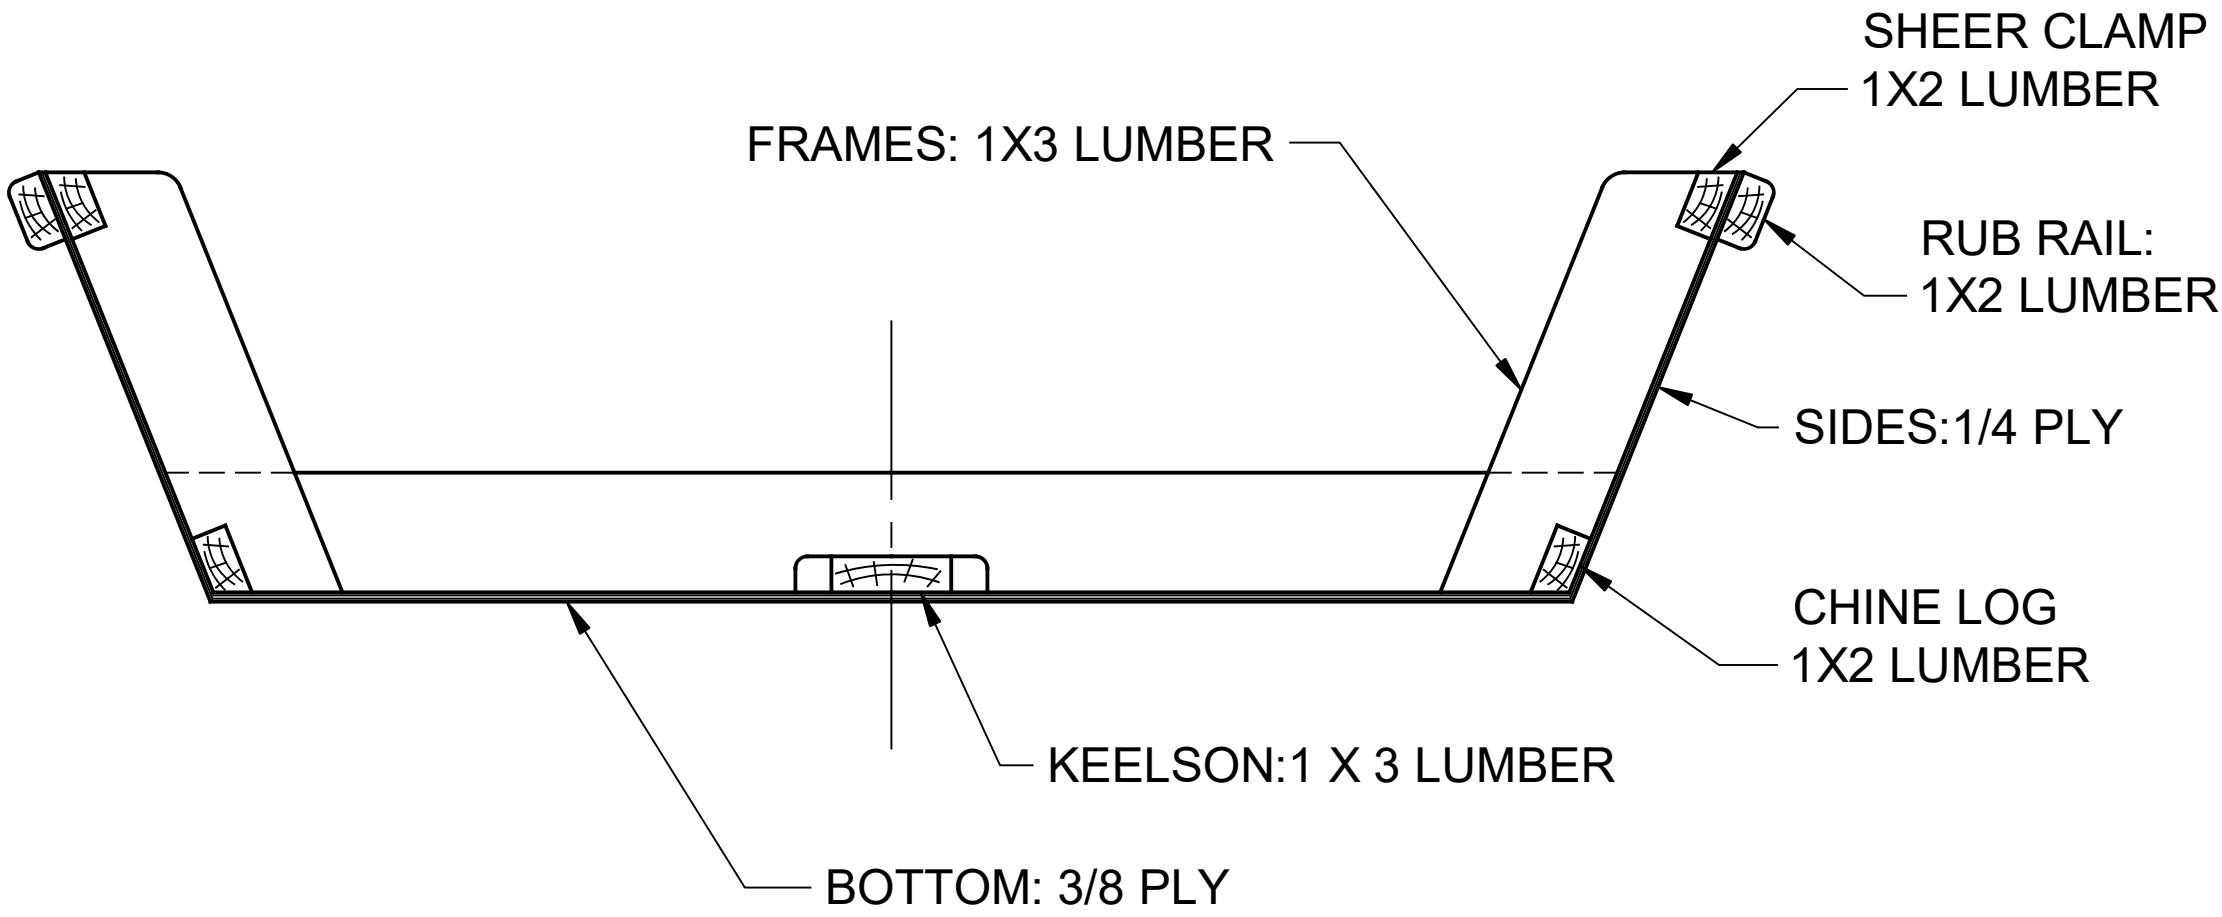

BILL OF MATERIALS

2 SHEETS - 1/4 PLY
2 SHEETS - 1/4 PLY
40' - 1 X 3 LUMBER
96' - 1 X 2 LUMBER
2' - 1 X 6 LUMBER
50 - #10 X 1- 1/2 DECK SCREWS
150 - #8 X 1 DECK SCREWS
4 QT - EPOXY RESIN
15 YDS - 50" WIDE 6 OZ F'GLASS CLOTH

TYPICAL CONSTRUCTION METHOD
SCALE: 1/4

FASTENING SCHEDULE

FRAMES TO FRAMES: #10 X 1-1/2 DECK SCREWS
PLY TO FRAMES: #8 X 1 DECK SCREWS

NOTES:

1. YOU MAY SCARF TOGETHER SHORTER PIECES TO CREATE THE LONGITUDINAL ELEMENTS.
2. NOMINAL LUMBER SIZED CALLED OUT, E.G. A 2 X 4 LUMBER IS ACTUAL SIZE 1-1/2" X 3-1/2" (MOLDINGS ACTUAL SIZES)



Spira International, Inc.
Huntington Beach, California

RAILBIRD
16' CHESAPEAKE PUSHBOAT

DRAWN BY:
J. SPIRA

DATE:
09/22/15

DRAWING NO.
RAIL02

SCALE 1" = 1' & NOTED

SHEET OF