

4

3

2

1

NOTICE
THIS DRAWING CONTAINS A PROPRIETARY DESIGN ASSIGNED TO SPIRA INTERNATIONAL, INC. ALL RIGHTS TO DUPLICATE, TRANSFER OR USE ARE EXPRESSLY RESERVED BY SPIRA INTERNATIONAL. THE BUYER IS LICENSED TO BUILD ONE ASSEMBLY FROM THESE PLANS.

REVISIONS				
ZONE	LTR	DESCRIPTION	DATE	APPROVED

D

D

C



C

B

B

A

A

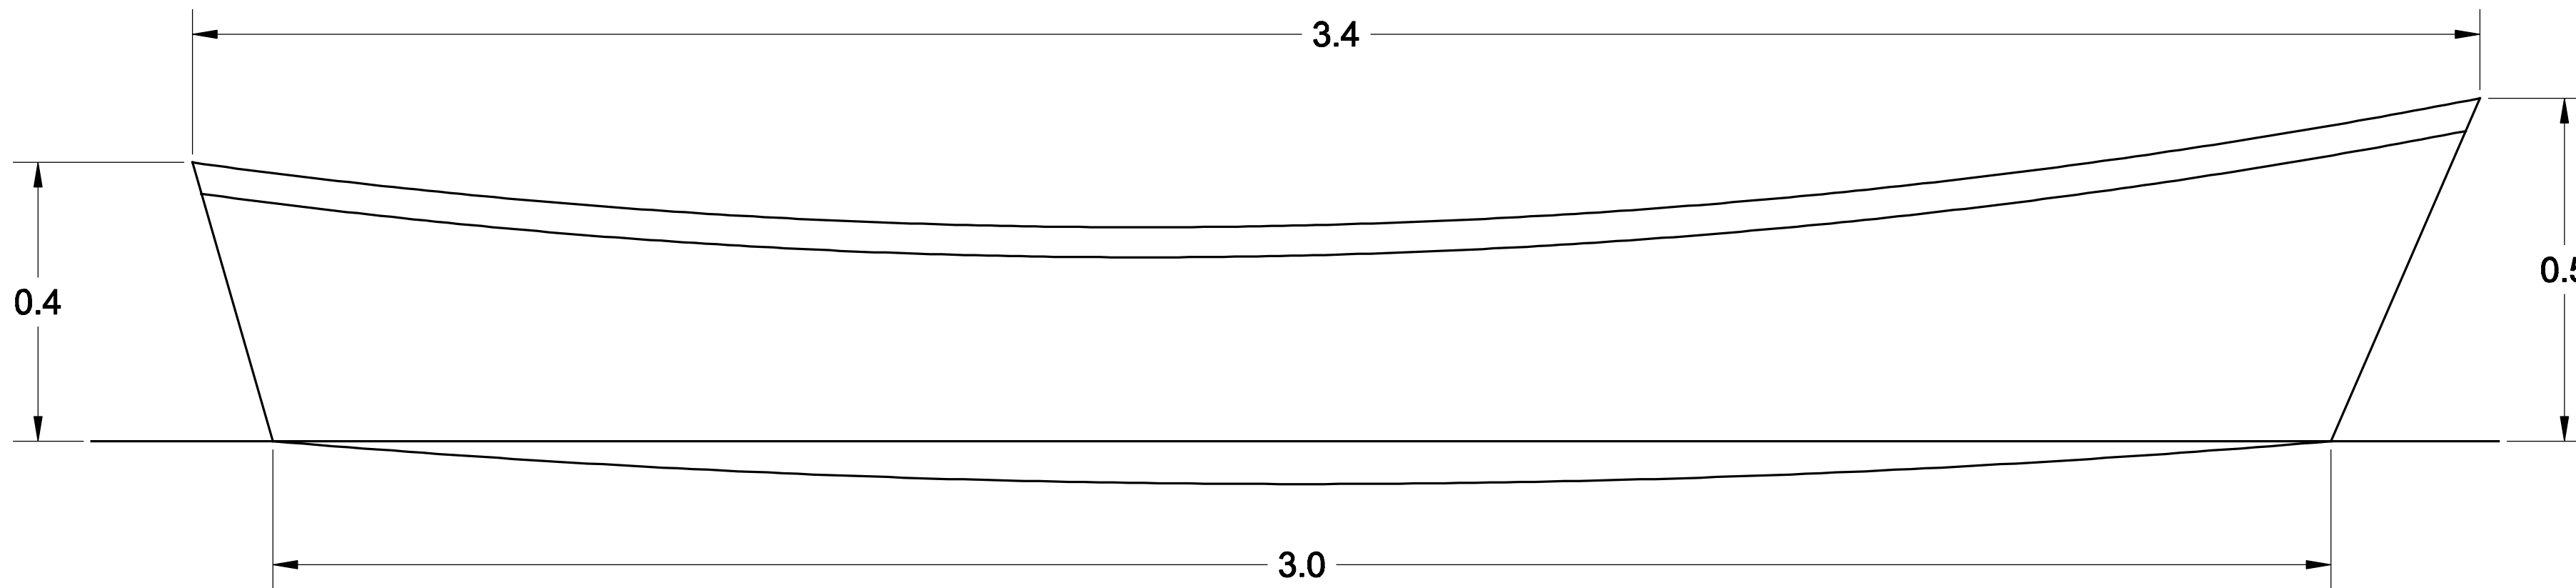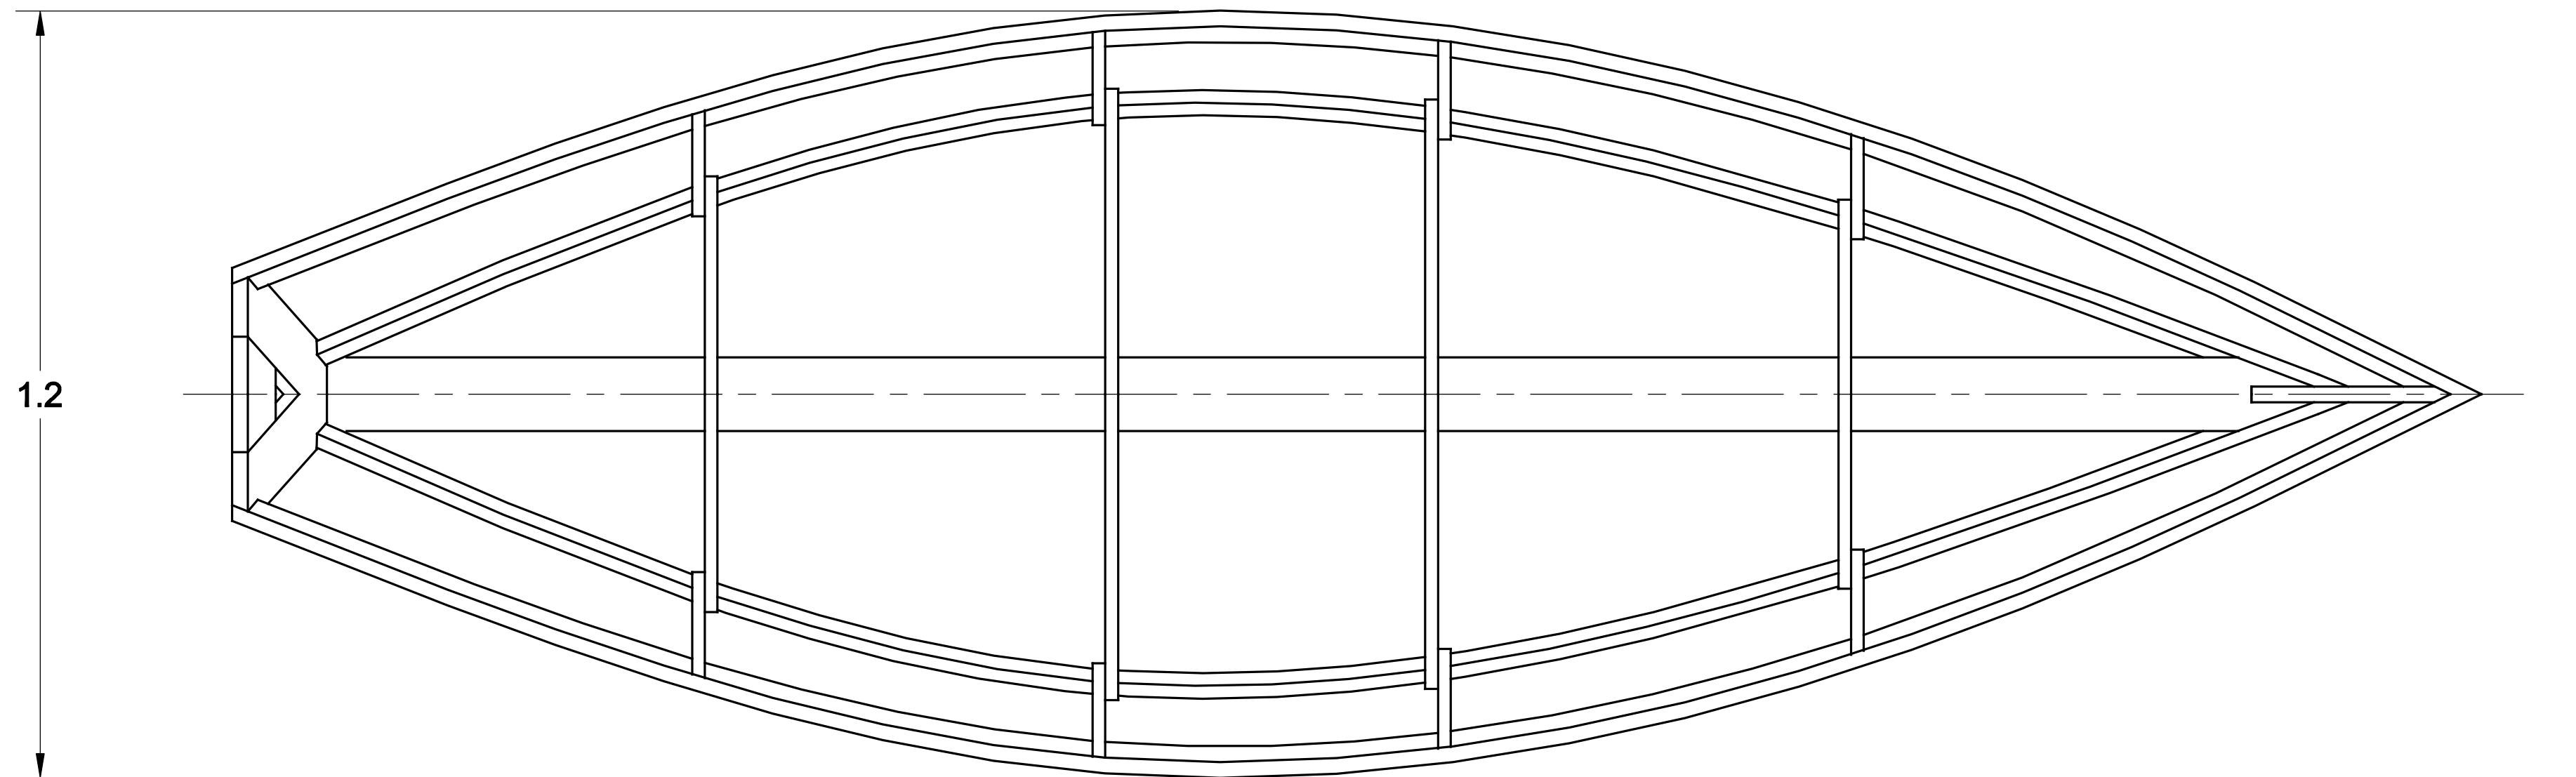

Spira International, Inc. <i>Huntington Beach, California</i>		
OTTERS POINT GRAND BANKS DORY		
DRAWN BY: J. SPIRA	DATE: 03/18/11	DRAWING NO. OTTEM01
SCALE 1/8	SHEET OF	

4

3

2

1

4

3

2

1

NOTICE
THIS DRAWING CONTAINS A PROPRIETARY DESIGN ASSIGNED TO SPIRA INTERNATIONAL, INC. ALL RIGHTS TO DUPLICATE, TRANSFER OR USE ARE EXPRESSLY RESERVED BY SPIRA INTERNATIONAL. THE BUYER IS LICENSED TO BUILD ONE ASSEMBLY FROM THESE PLANS.

REVISIONS				
ZONE	LTR	DESCRIPTION	DATE	APPROVED

D

D

C

C

B

B

A

A

SHEER CLAMP AND RUB RAIL
19 X 35 TIMBER

FRAMES 19 X 63 TIMBER

SIDES - 6MM PLY

CHINE LOG
19 X 35 TIMBER

KEELSON 19 X 140 TIMBER

BOTTOM 9MM PLY

BILL OF MATERIALS

2 SHEETS 6MM PLY (SIDES)
1 SHEET 9MM PLY (BOTTOM)
9M' 19 X 63 TIMBER FOR FRAMES
10M 19 X 35 CLEAR LUMBER FOR SHEER
CLAMP, CHINE LOG AND RUB RAILS
4M' 19 X 140 TIMBER FOR KEELSON & STEM
60 M4 X 30 DECK SCREWS
100 M4 X 50 DECK SCREWS
150 M3 X 30 DECK SCREWS
3 L EPOXY RESIN
10 M 6 OZ FIBERGLASS CLOTH

NOTES:

1. YOU MAY SCARF TOGETHER SHORTER PIECES TO CREATE THE LONGITUDINAL ELEMENTS.

CONSTRUCTION METHOD

TYPICAL AT EACH FRAME
NO SCALE

FASTENING SCHEDULE

FRAME TO FRAME: M4 X 30 DECK SCREWS
LONGITUDINAL TO FRAME: M4 X 50 DECK SCREWS
PLANKING TO FRAME: M3 X 30 DECK SCREWS

Spira International, Inc.
Huntington Beach, California

**OTTERS POINT
GRAND BANKS DORY**

DRAWN BY:
J. SPIRA

DATE:
03/18/11

DRAWING NO.
OTTEM02

SCALE 1-1/2" = 1' & NOTED

SHEET OF

4

3

2

1