

4


3

2

1

NOTICE
THIS DRAWING CONTAINS A PROPRIETARY DESIGN ASSIGNED TO SPIRA INTERNATIONAL, INC. ALL RIGHTS TO DUPLICATE, TRANSFER OR SELL THIS DESIGN ARE EXPRESSLY RESERVED. THE BUYER IS LICENSED TO BUILD ONE ASSEMBLY FROM THESE PLANS.

REVISIONS				
ZONE	LTR	DESCRIPTION	DATE	APPROVED

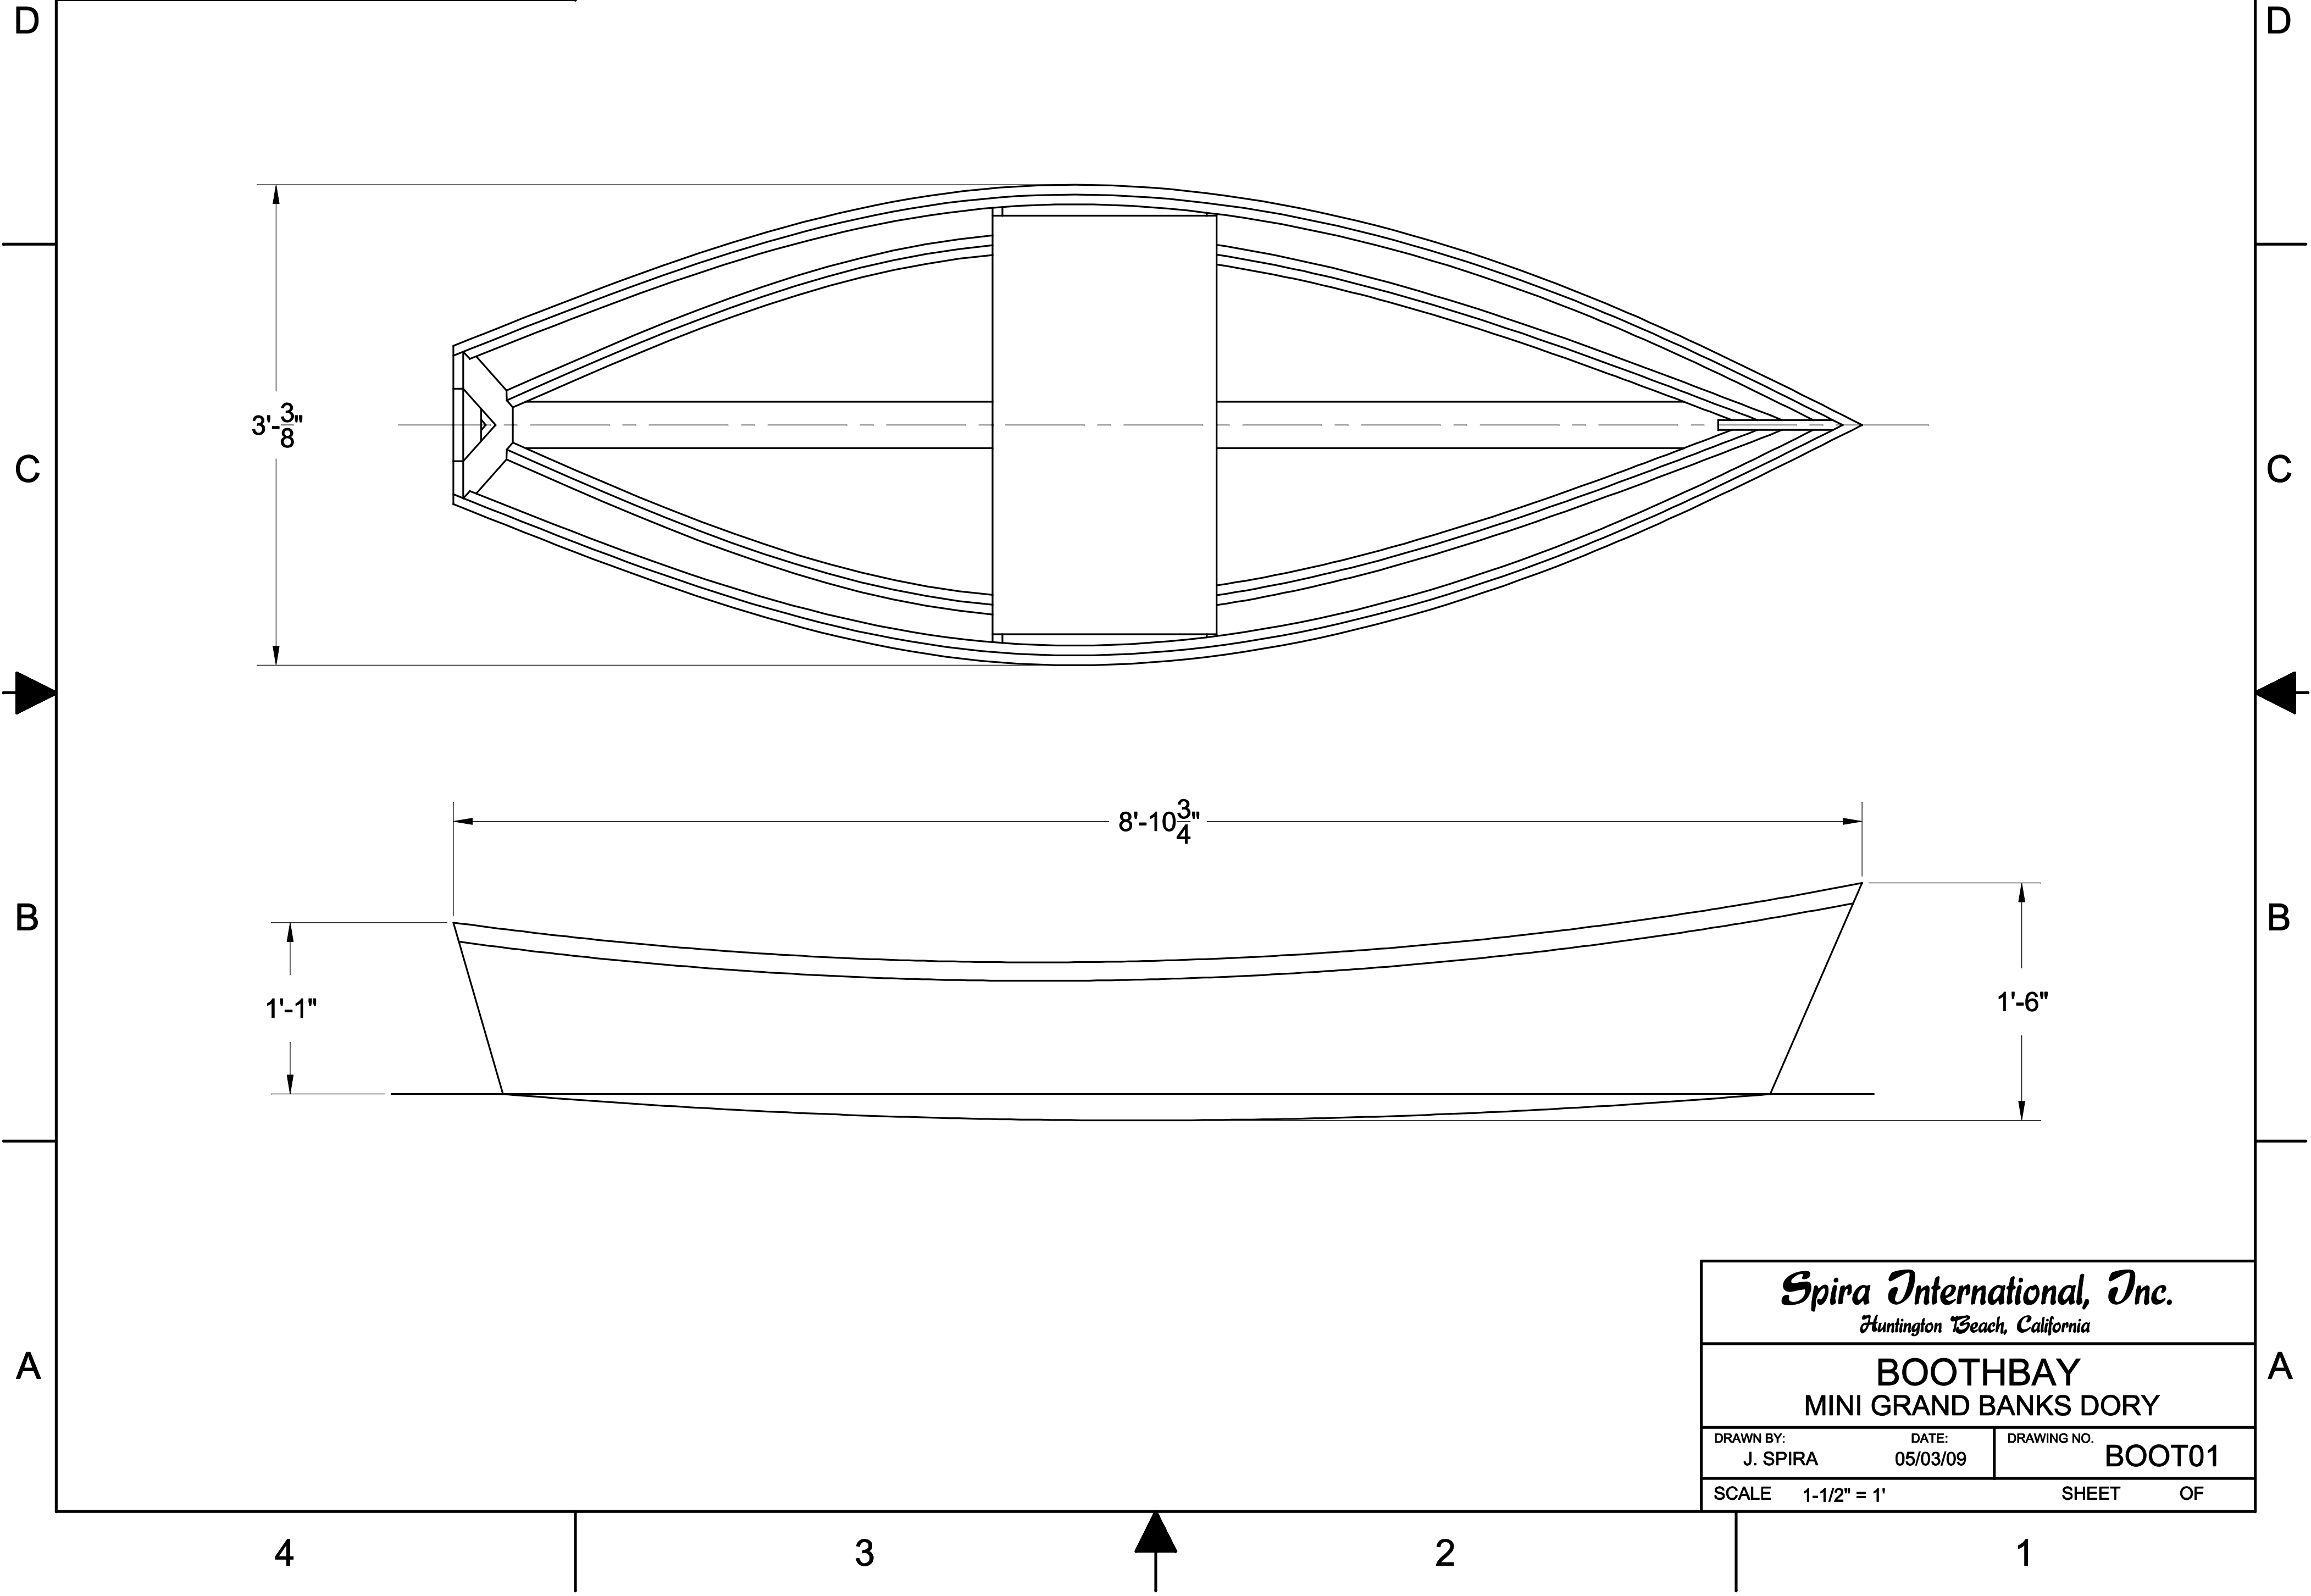

4


3

2

1

NOTICE
THIS DRAWING CONTAINS A PROPRIETARY DESIGN ASSIGNED TO SPIRA INTERNATIONAL, INC. ALL RIGHTS TO DUPLICATE, TRANSFER OR SELL THIS DESIGN ARE EXPRESSLY RESERVED. THE BUYER IS LICENSED TO BUILD ONE ASSEMBLY FROM THESE PLANS.

REVISIONS				
ZONE	LTR	DESCRIPTION	DATE	APPROVED
	A	ADDED BOM AND REARRANGED VIEWS	08/19/10	JJS

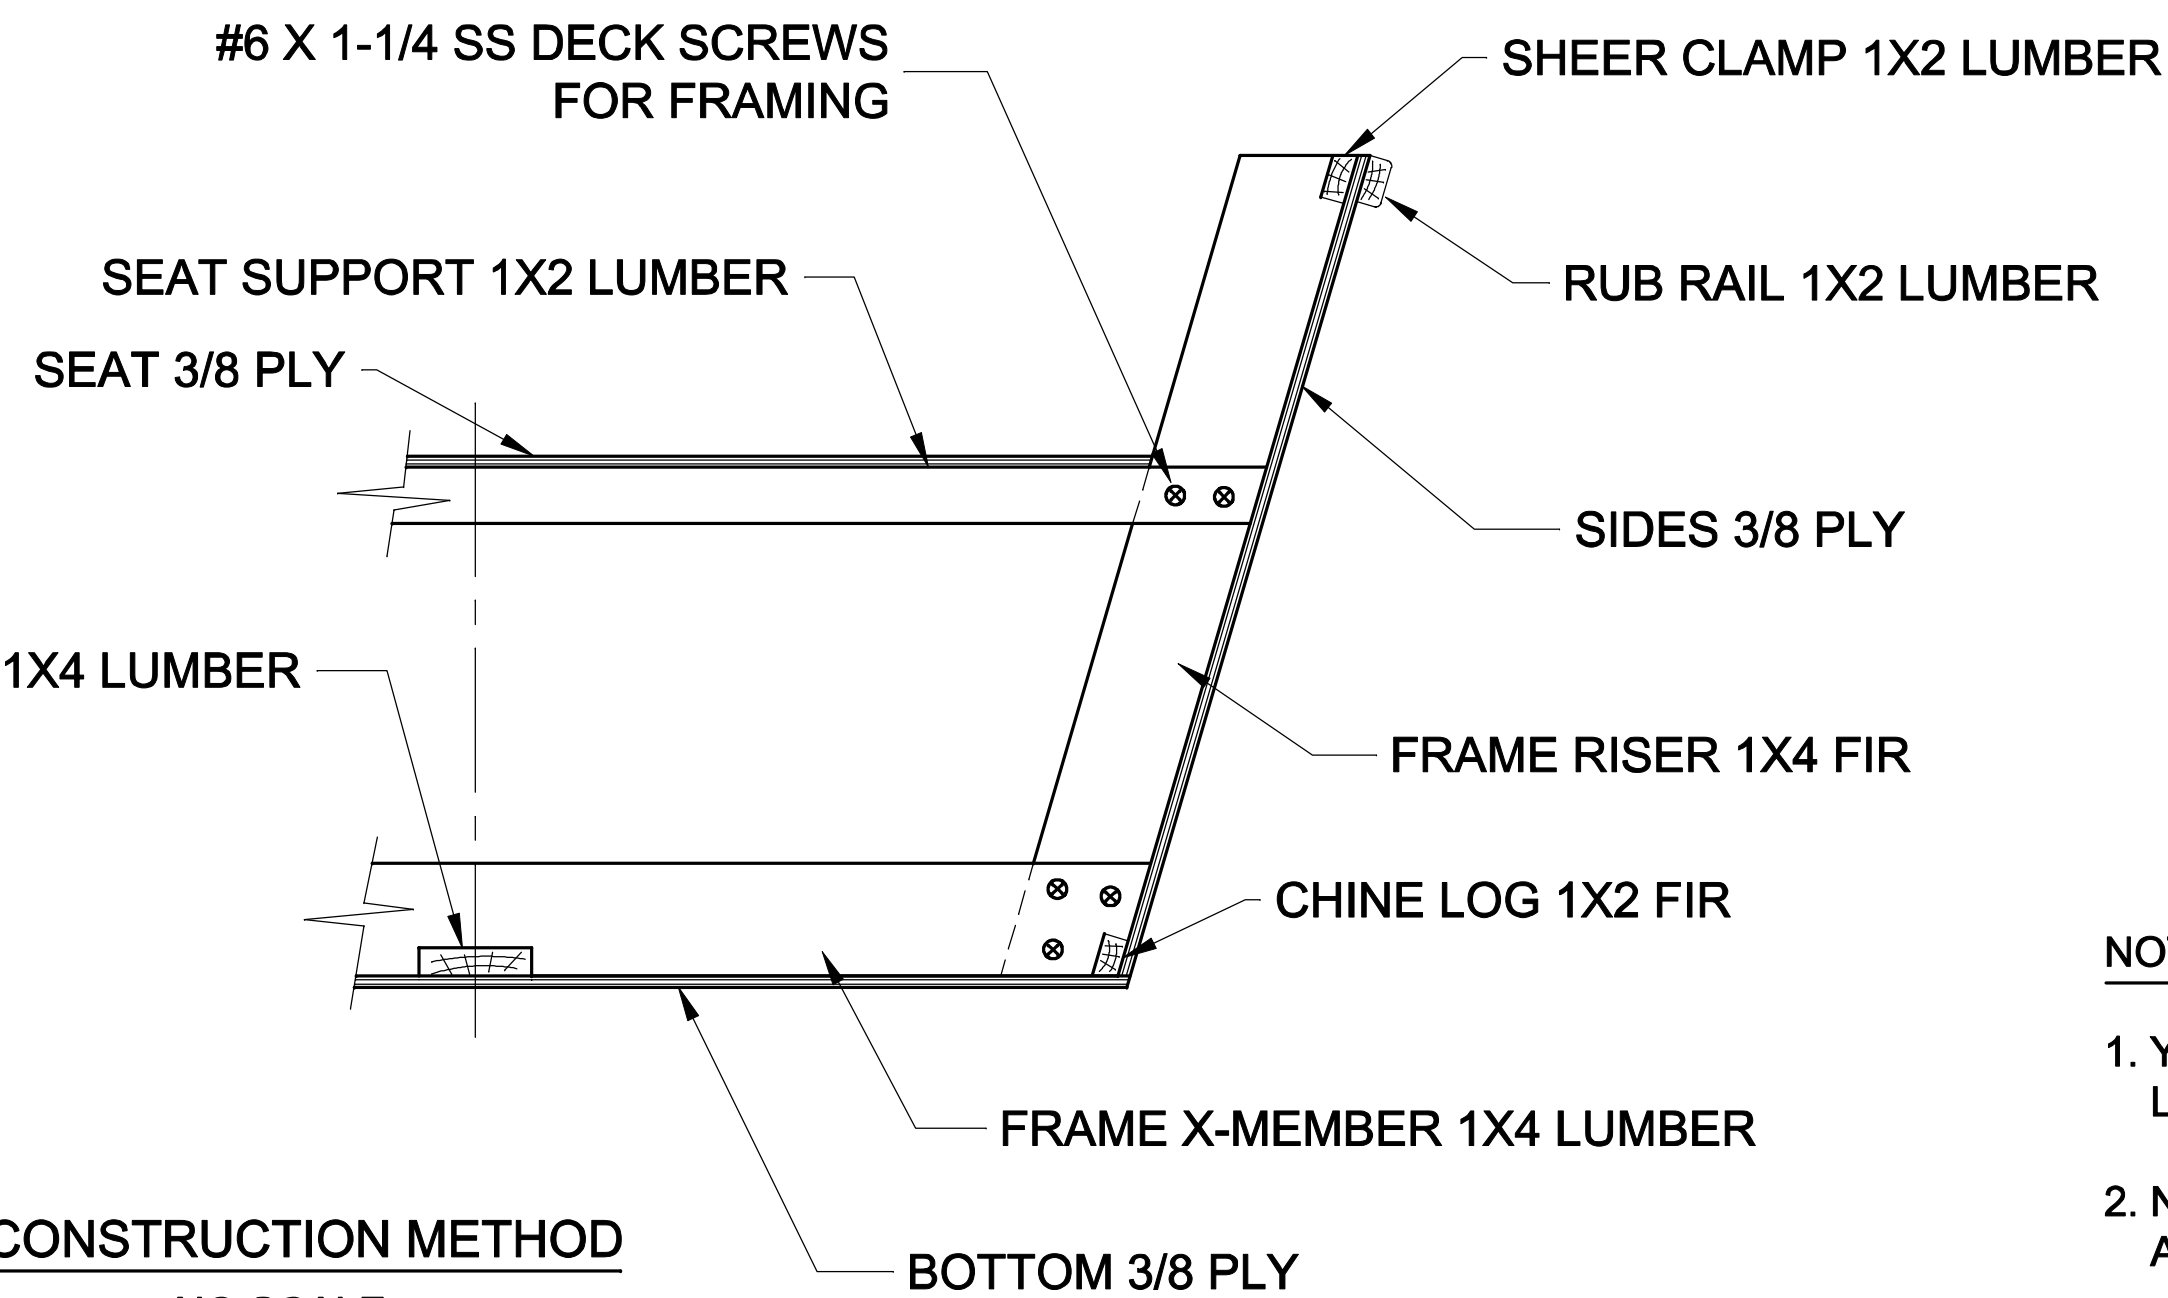



CONSTRUCTION METHOD
NO SCALE

BILL OF MATERIALS

1 4X8 SHEET 3/8" PLY
1 4X10 SHEET 3/8" PLY
80' - 1X2 LUMBER FOR SHEER CLAMP, SEAT
FRAMES, CHINE LOG, RUB RAIL
20' - 1 X 4 LUMBER FOR FRAMES AND KEELSON
100 #6 X 1-1/4 DECK SCREWS
1-1/2 QT EPOXY RESIN
OPTIONAL: 3 YDS 6OZ FIBERGLASS CLOTH
AND ADD'L 1-1/2 QT EPOXY RESIN

NOTES:

1. YOU MAY SCARF TOGETHER SHORTER PIECES TO CREATE THE LONGITUDINAL ELEMENTS.
2. NOMINAL LUMBER SIZED CALLED OUT, E.G. 1 X 4 LUMBER IS ACTUAL SIZE 3/4" X 3-1/2"

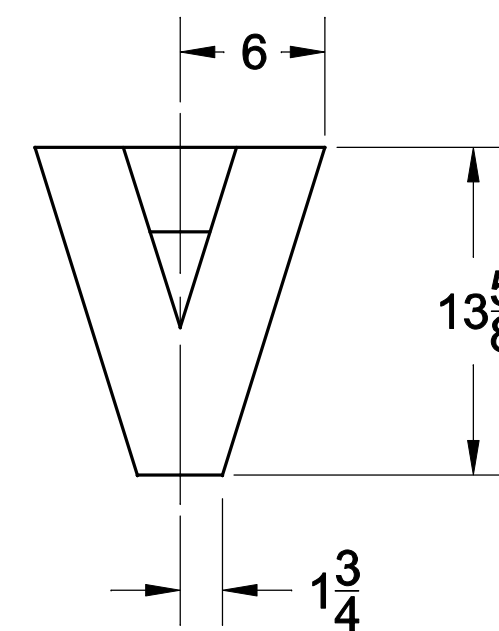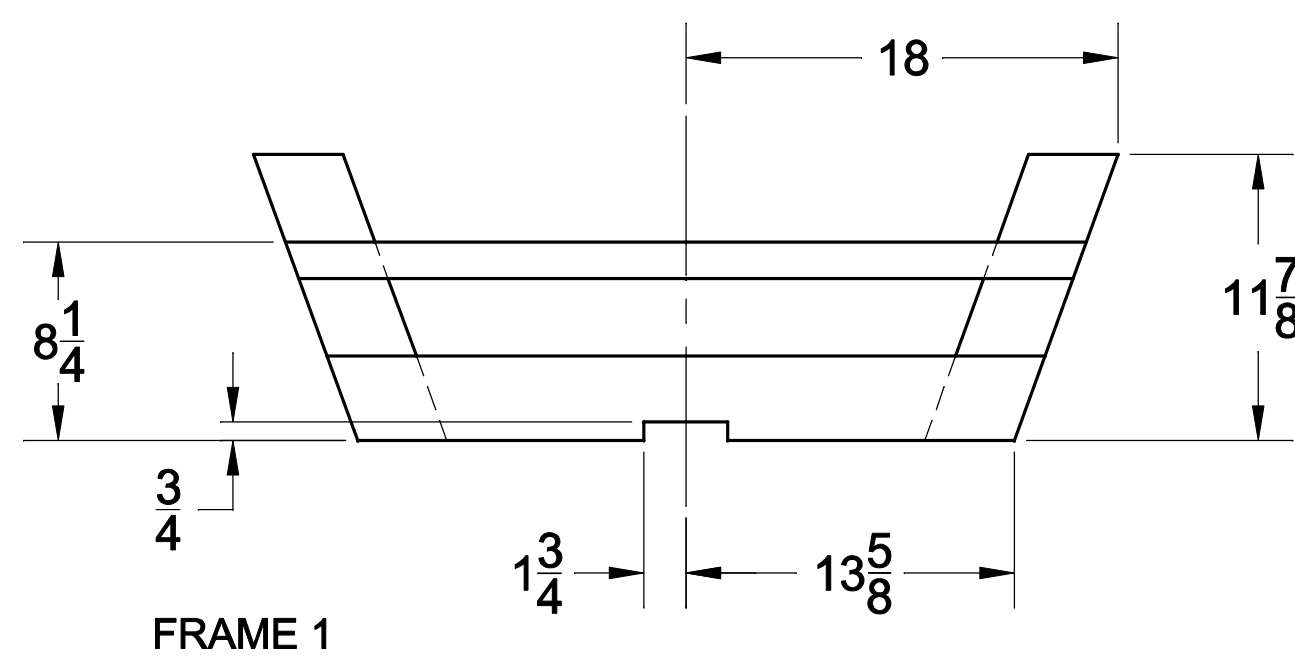

Spira International, Inc.
Huntington Beach, California

BOOTHBAY
MINI GRAND BANKS DORY

DRAWN BY:
J. SPIRA

DATE:
05/03/09



DRAWING NO.
BOOT02

SCALE 1 / 8 & NOTED



SHEET OF

NOTICE
THIS DRAWING CONTAINS A PROPRIETARY DESIGN ASSIGNED TO SPIRA INTERNATIONAL, INC. ALL RIGHTS TO DUPLICATE, TRANSFER OR SELL THIS DESIGN ARE EXPRESSLY RESERVED. THE BUYER IS LICENSED TO BUILD ONE ASSEMBLY FROM THESE PLANS.

REVISIONS				
ZONE	LTR	DESCRIPTION	DATE	APPROVED
	A	REARRANGED VIEWS	08/19/10	JJS

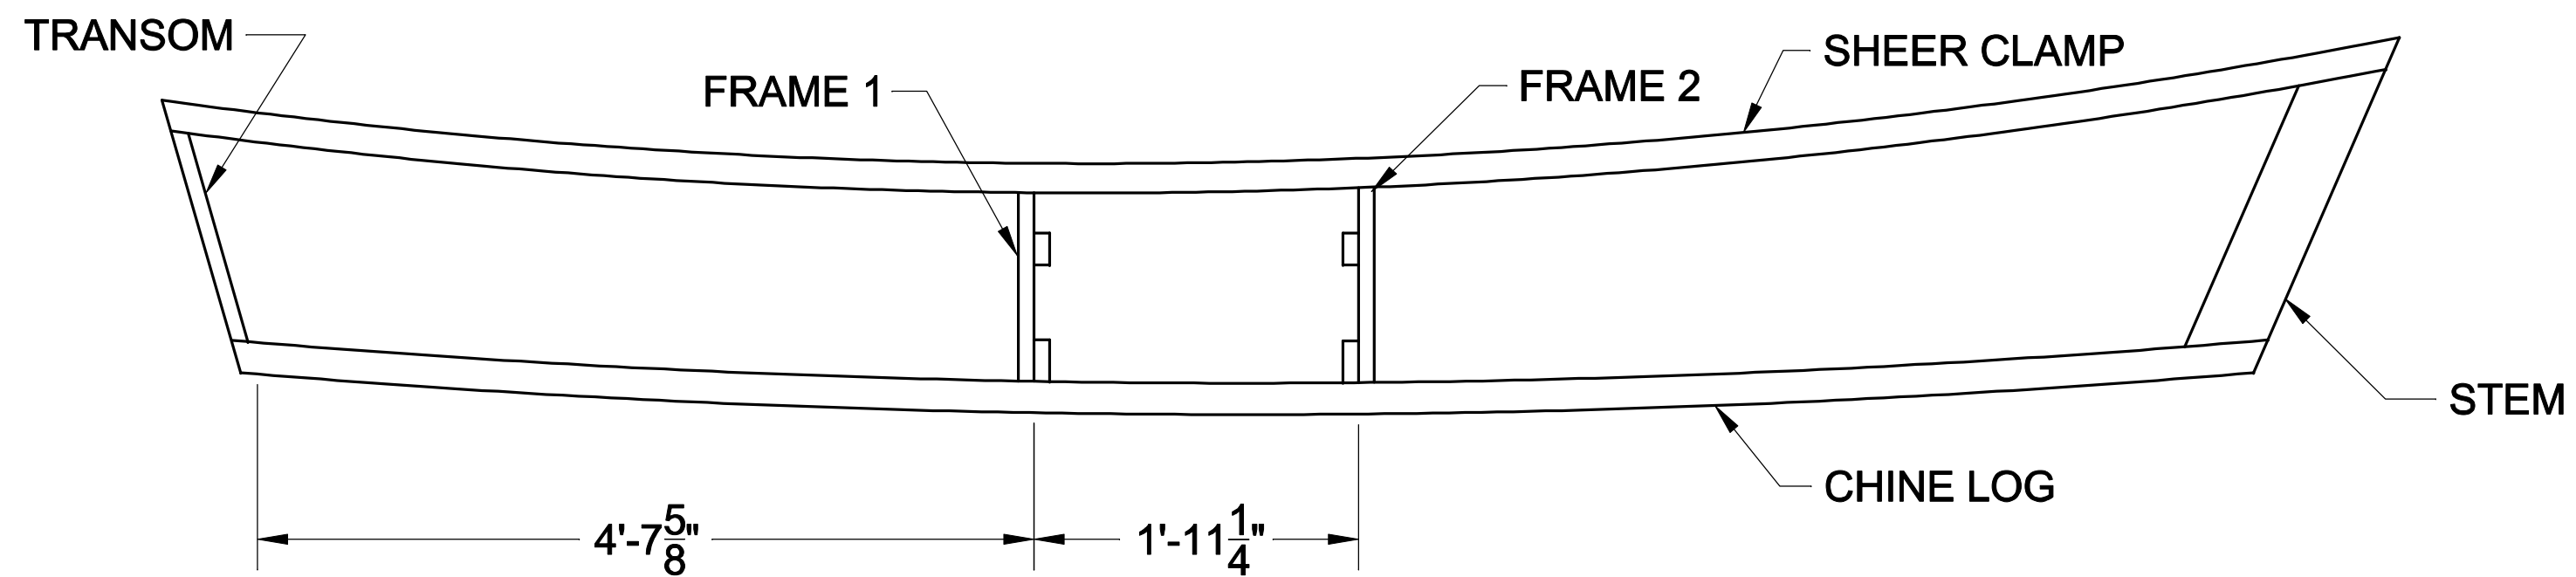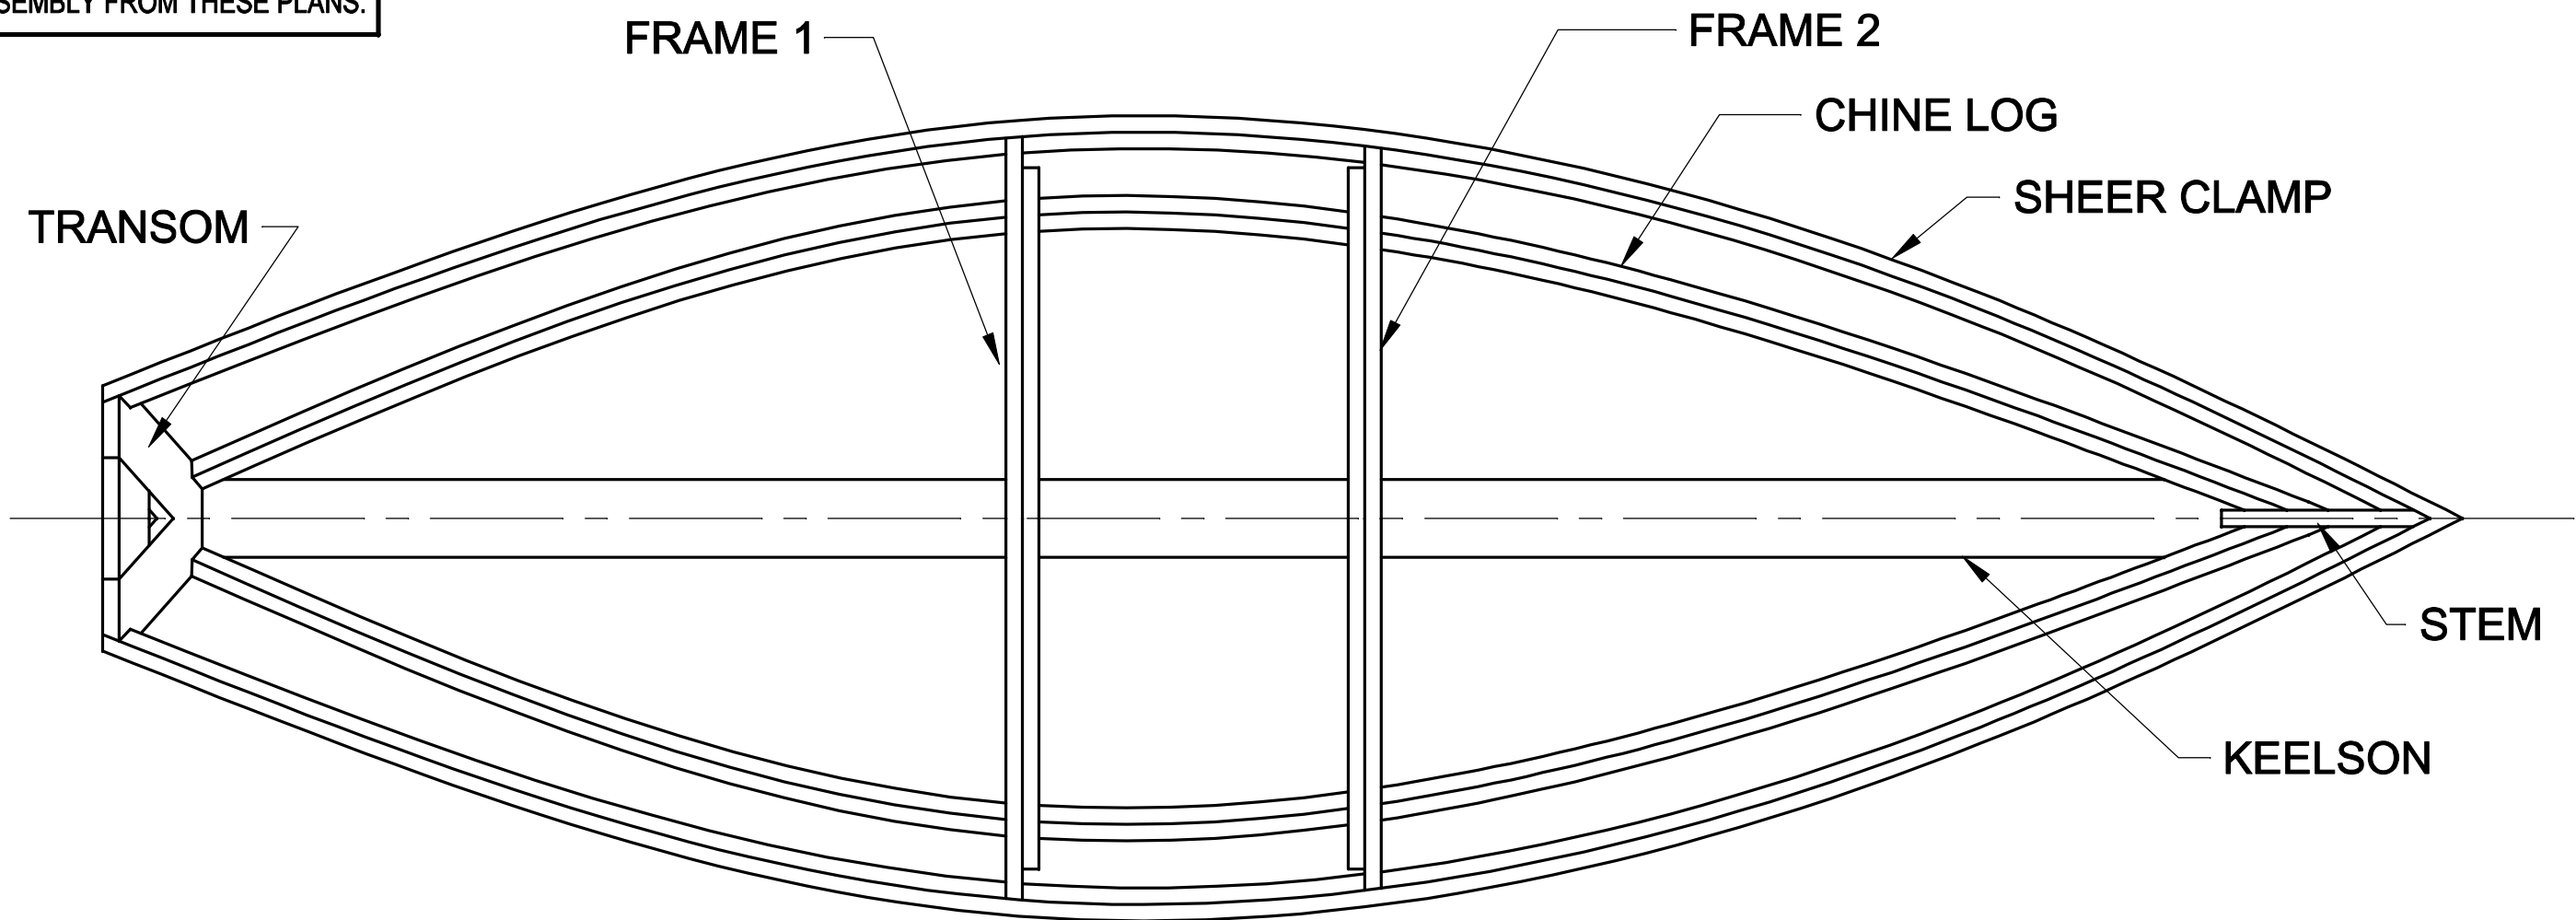

FRAMING

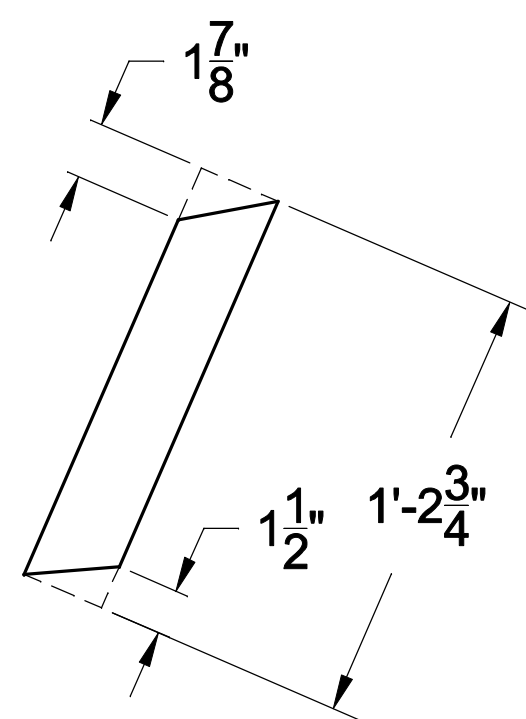
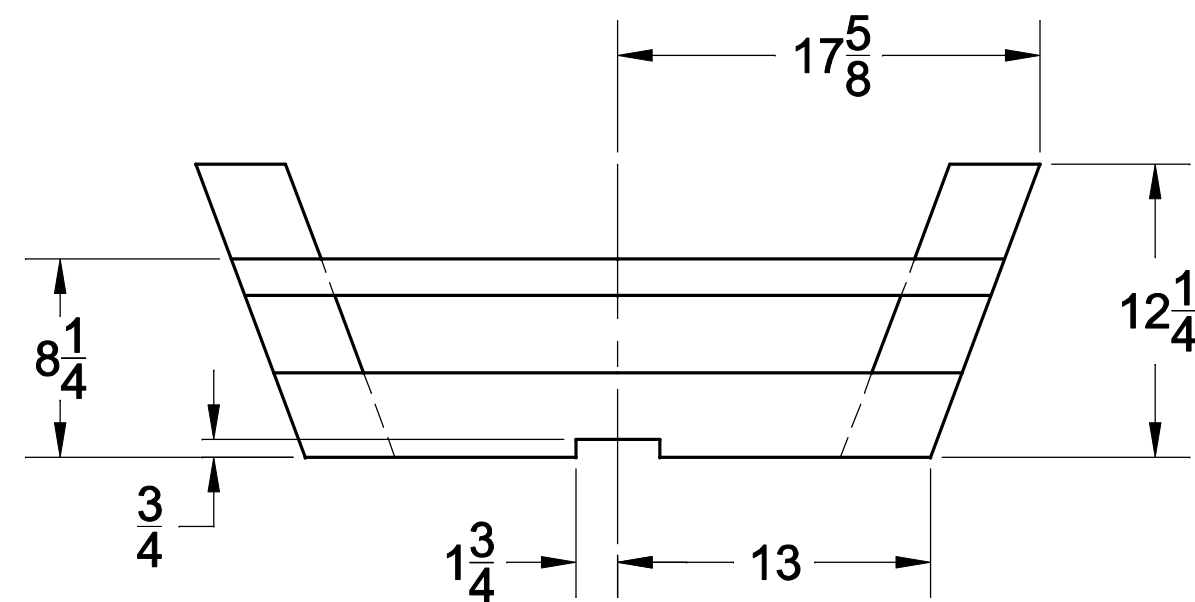


STEM



Spira International, Inc. <i>Huntington Beach, California</i>		
BOOTHBAY MINI GRAND BANKS DORY		
DRAWN BY: J. SPIRA	DATE: 05/03/09	DRAWING NO. BOOT03
SCALE 1-1/2" = 1'		SHEET OF

NOTICE
THIS DRAWING CONTAINS A PROPRIETARY DESIGN ASSIGNED TO SPIRA INTERNATIONAL, INC. ALL RIGHTS TO DUPLICATE, TRANSFER OR SELL THIS DESIGN ARE EXPRESSLY RESERVED. THE BUYER IS LICENSED TO BUILD ONE ASSEMBLY FROM THESE PLANS.

REVISIONS				
ZONE	LTR	DESCRIPTION	DATE	APPROVED

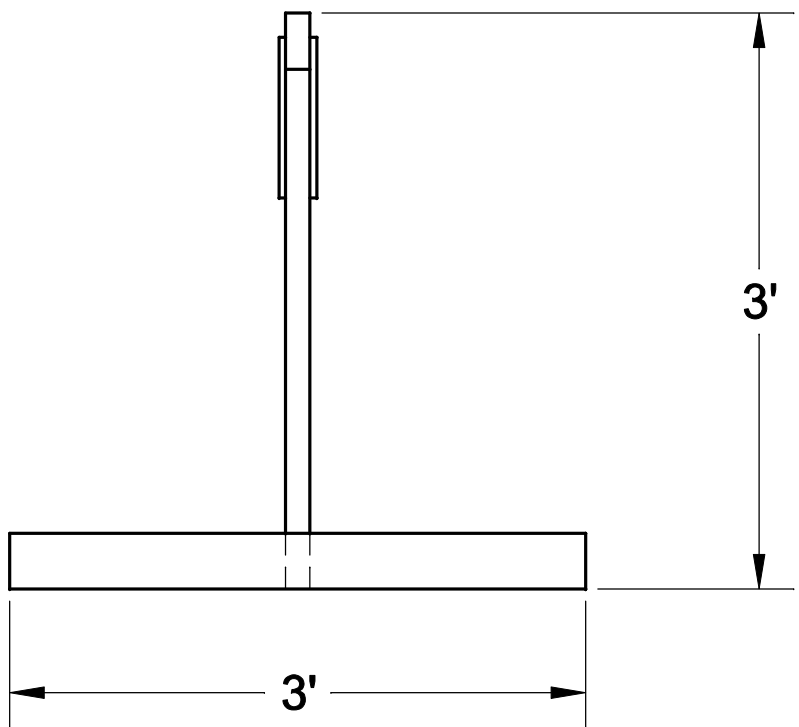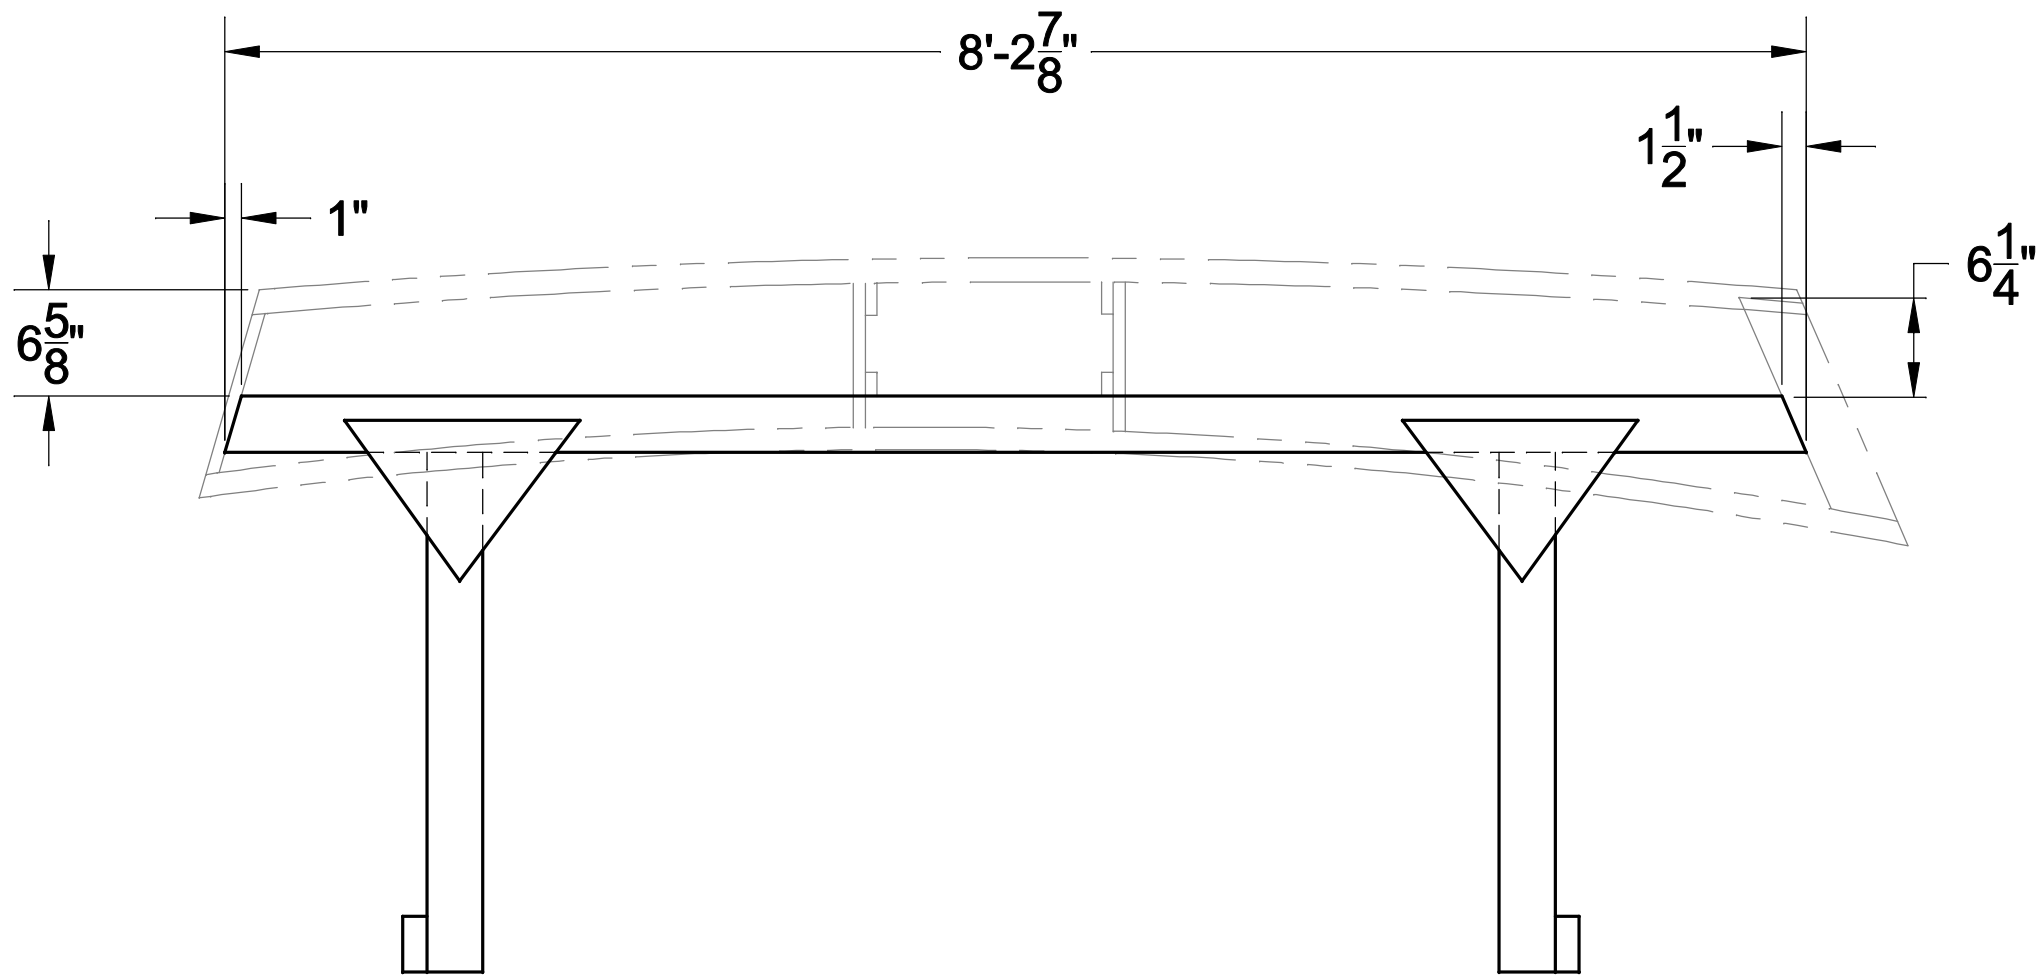

STRONGBACK JIG
MAKE FROM SCRAP 2X4S AND 3/8" PLY

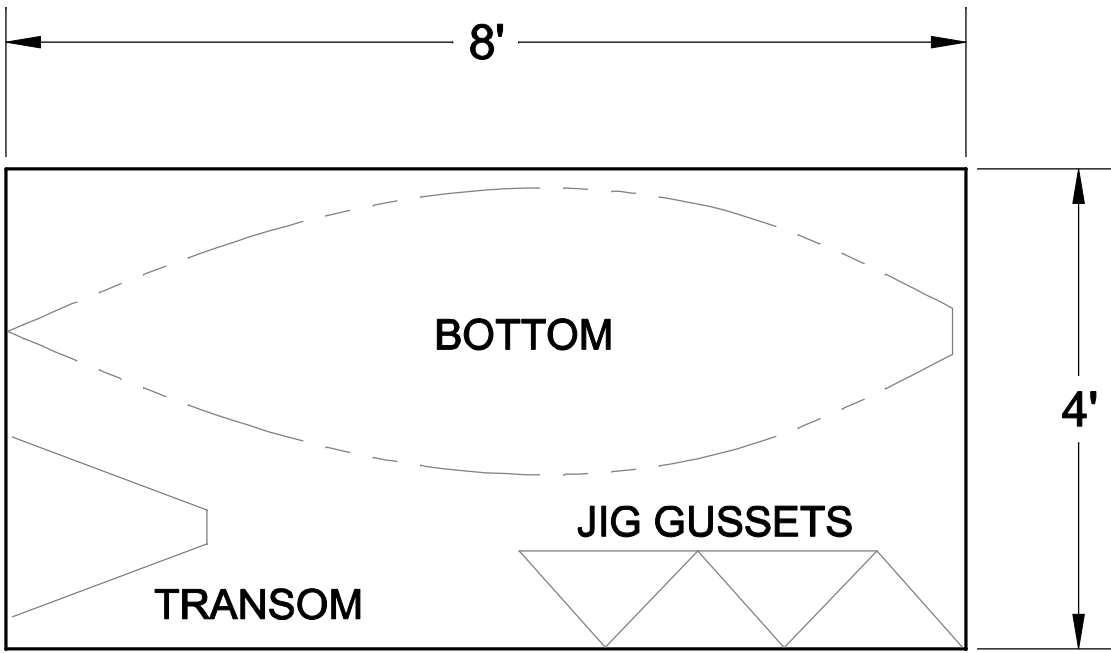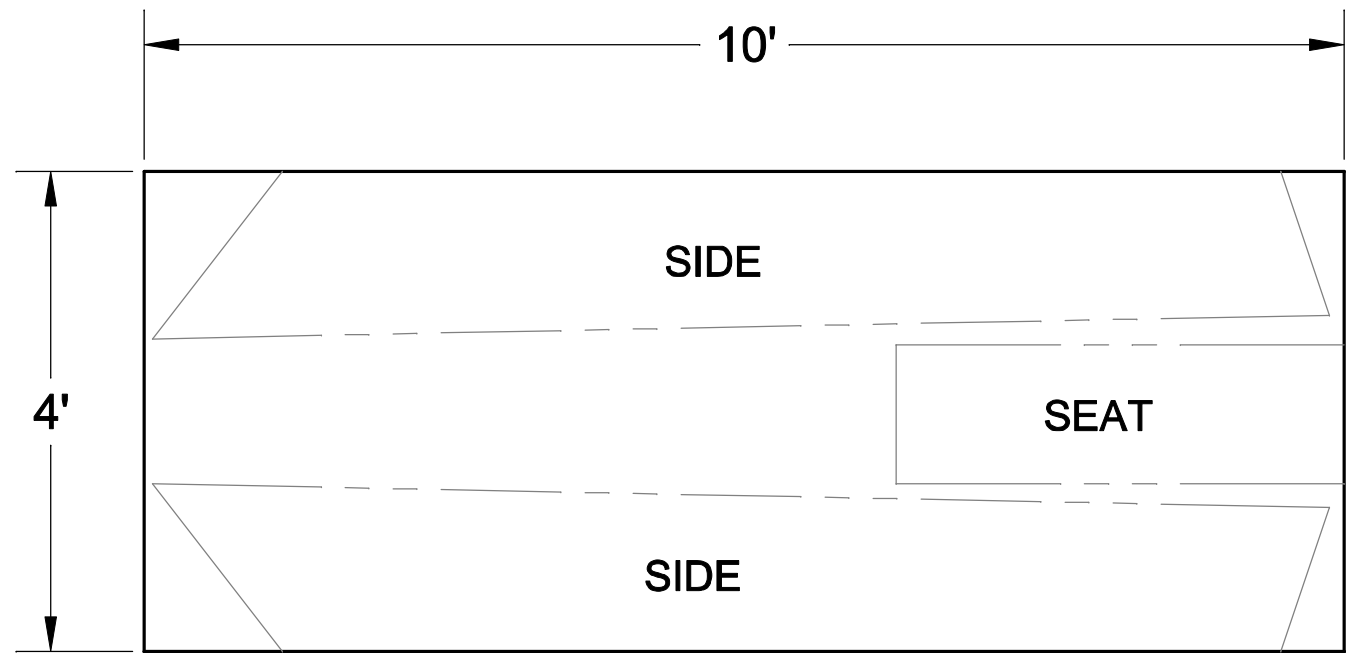

METHOD TO CUT OUT PANELS
FROM 1 SHEET OF 4' X 10' PLY & 1 SHEET OF 4' X 8' PLY
NO SCALE

Spira International, Inc.
Huntington Beach, California

BOOTHBAY
MINI GRAND BANKS DORY

DRAWN BY: J. SPIRA	DATE: 05/03/09	DRAWING NO. BOOT04
SCALE 1" = 1' & NOTED	SHEET	OF