

4

3


2

1

NOTICE

THIS DRAWING CONTAINS A PROPRIETARY DESIGN ASSIGNED TO SPIRA INTERNATIONAL, INC. ALL RIGHTS TO DUPLICATE, TRANSFER OR USE ARE EXPRESSLY RESERVED BY SPIRA INTERNATIONAL. THE BUYER IS LICENSED TO BUILD ONE ASSEMBLY FROM THESE PLANS.

REVISIONS				
ZONE	LTR	DESCRIPTION	DATE	APPROVED

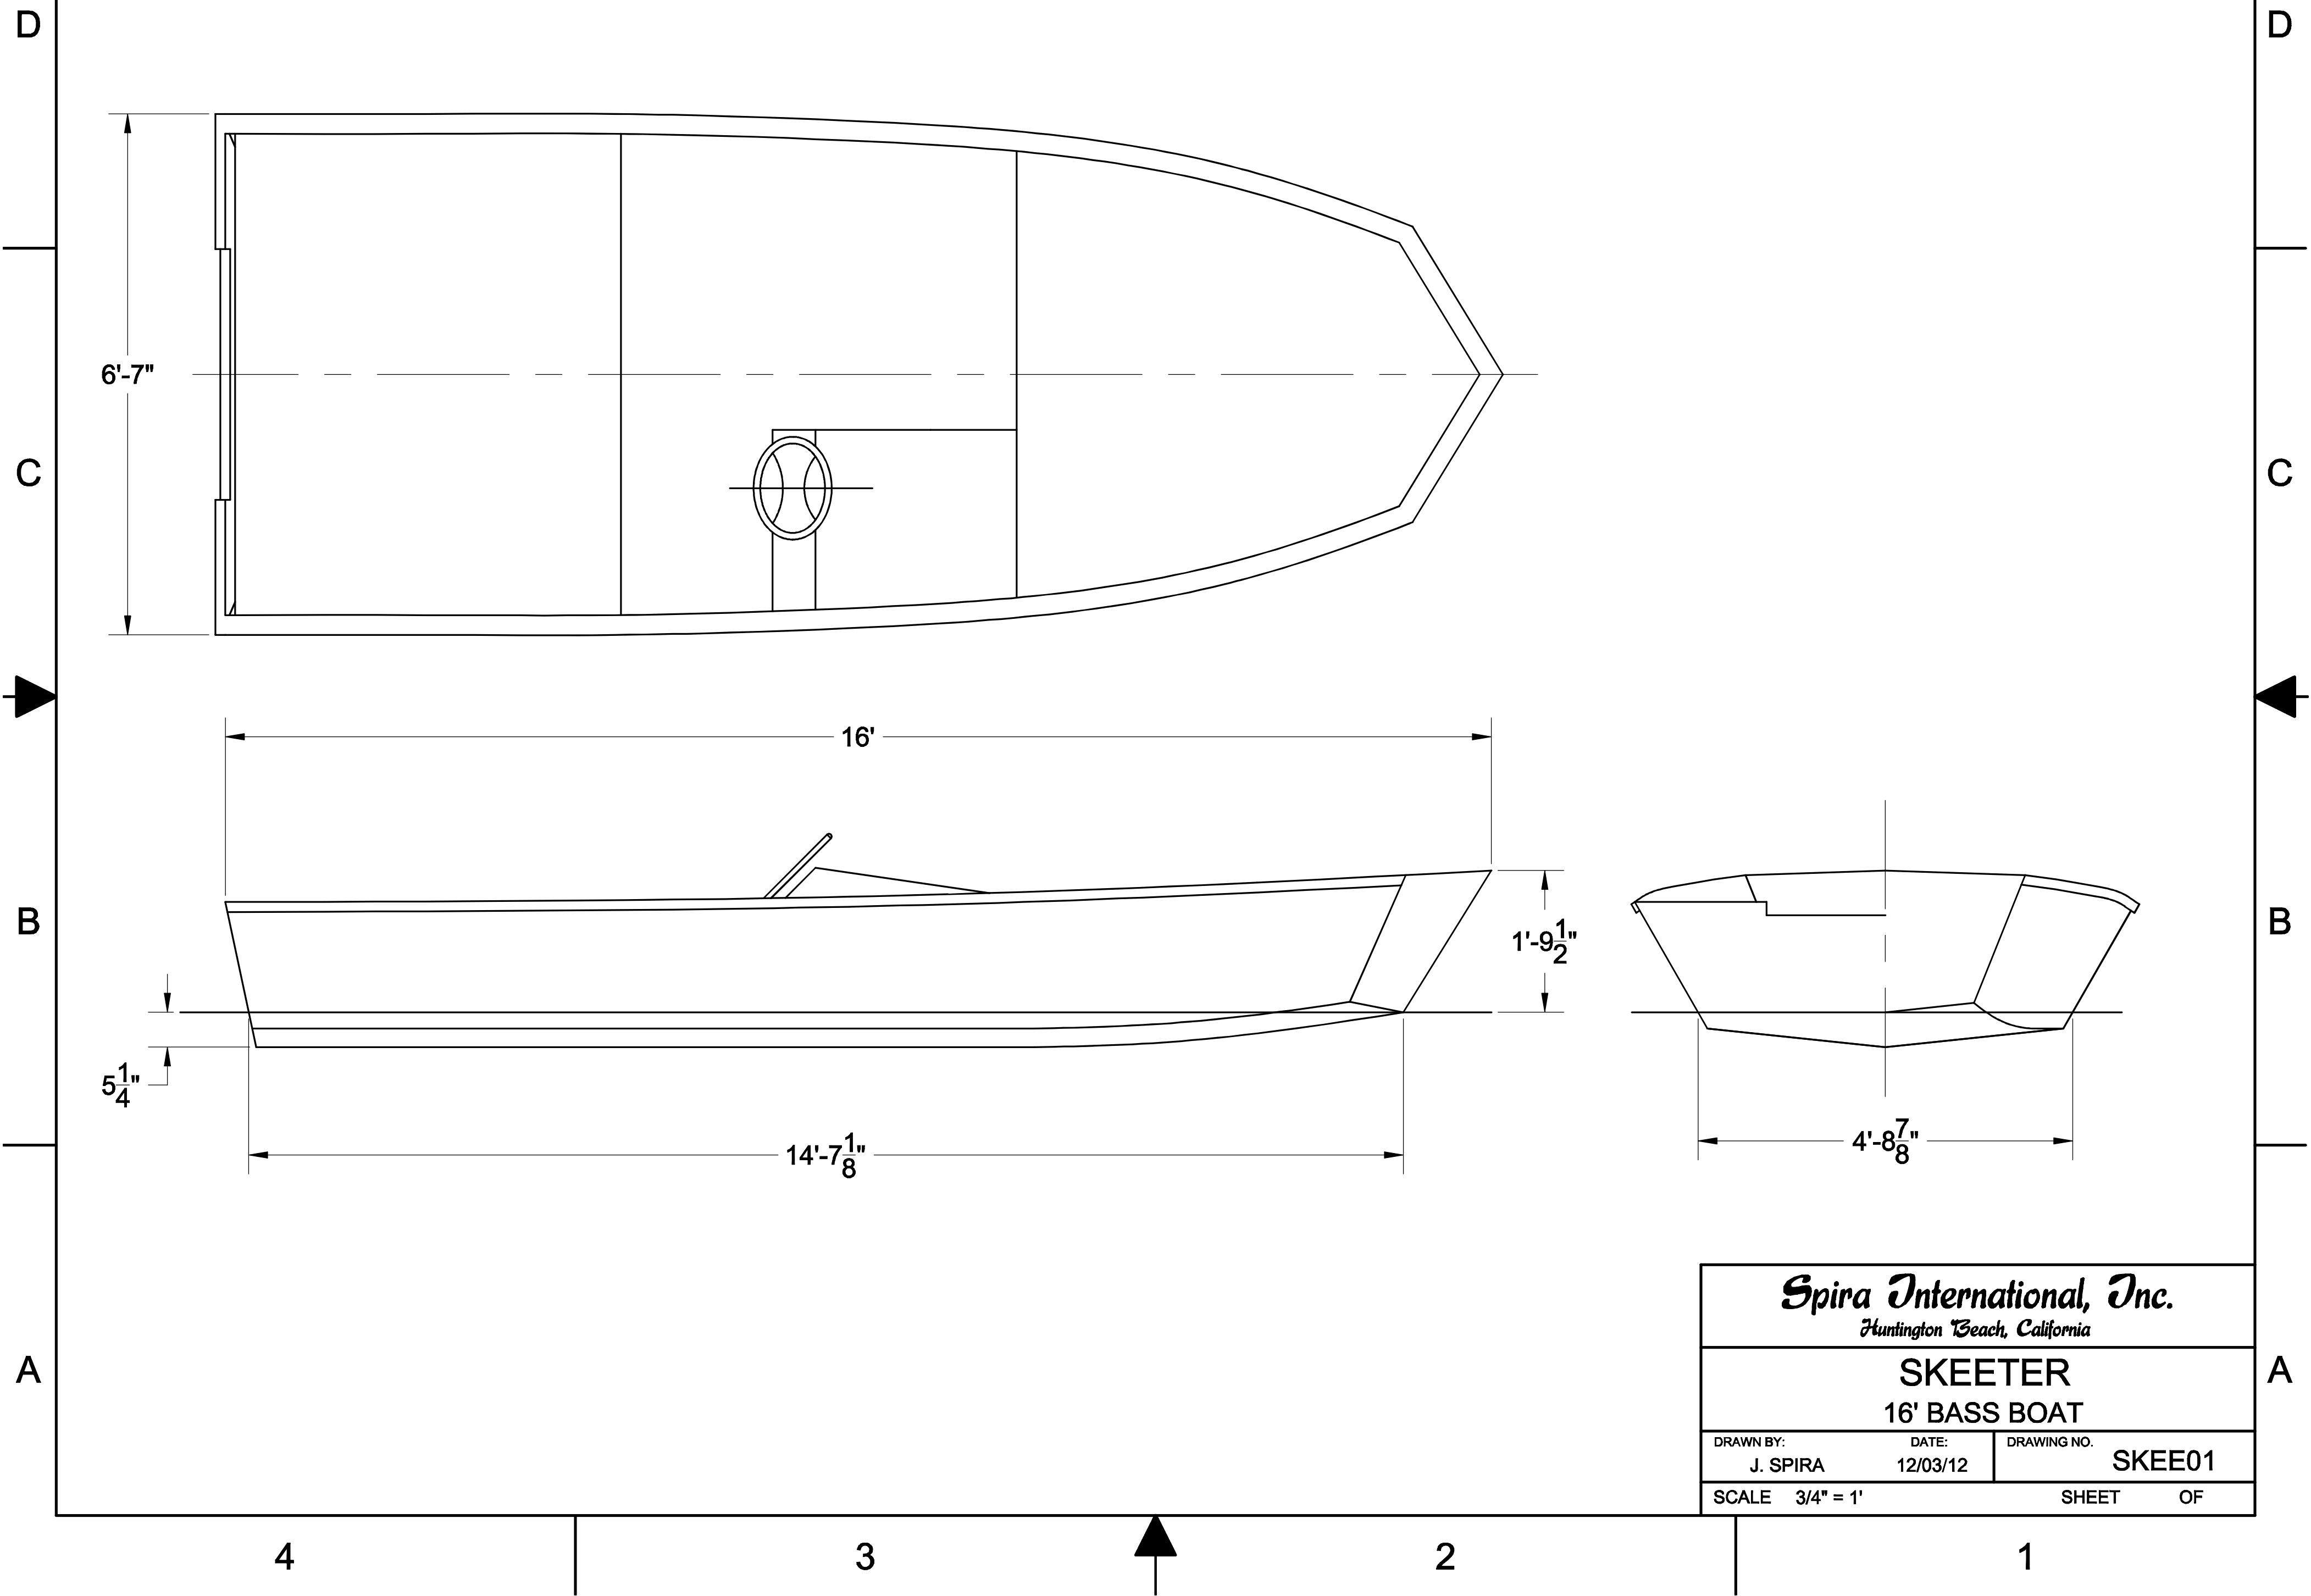

4

3


2

1

NOTICE

THIS DRAWING CONTAINS A PROPRIETARY DESIGN ASSIGNED TO SPIRA INTERNATIONAL, INC. ALL RIGHTS TO DUPLICATE, TRANSFER OR USE ARE EXPRESSLY RESERVED BY SPIRA INTERNATIONAL. THE BUYER IS LICENSED TO BUILD ONE ASSEMBLY FROM THESE PLANS.

REVISIONS				
ZONE	LTR	DESCRIPTION	DATE	APPROVED

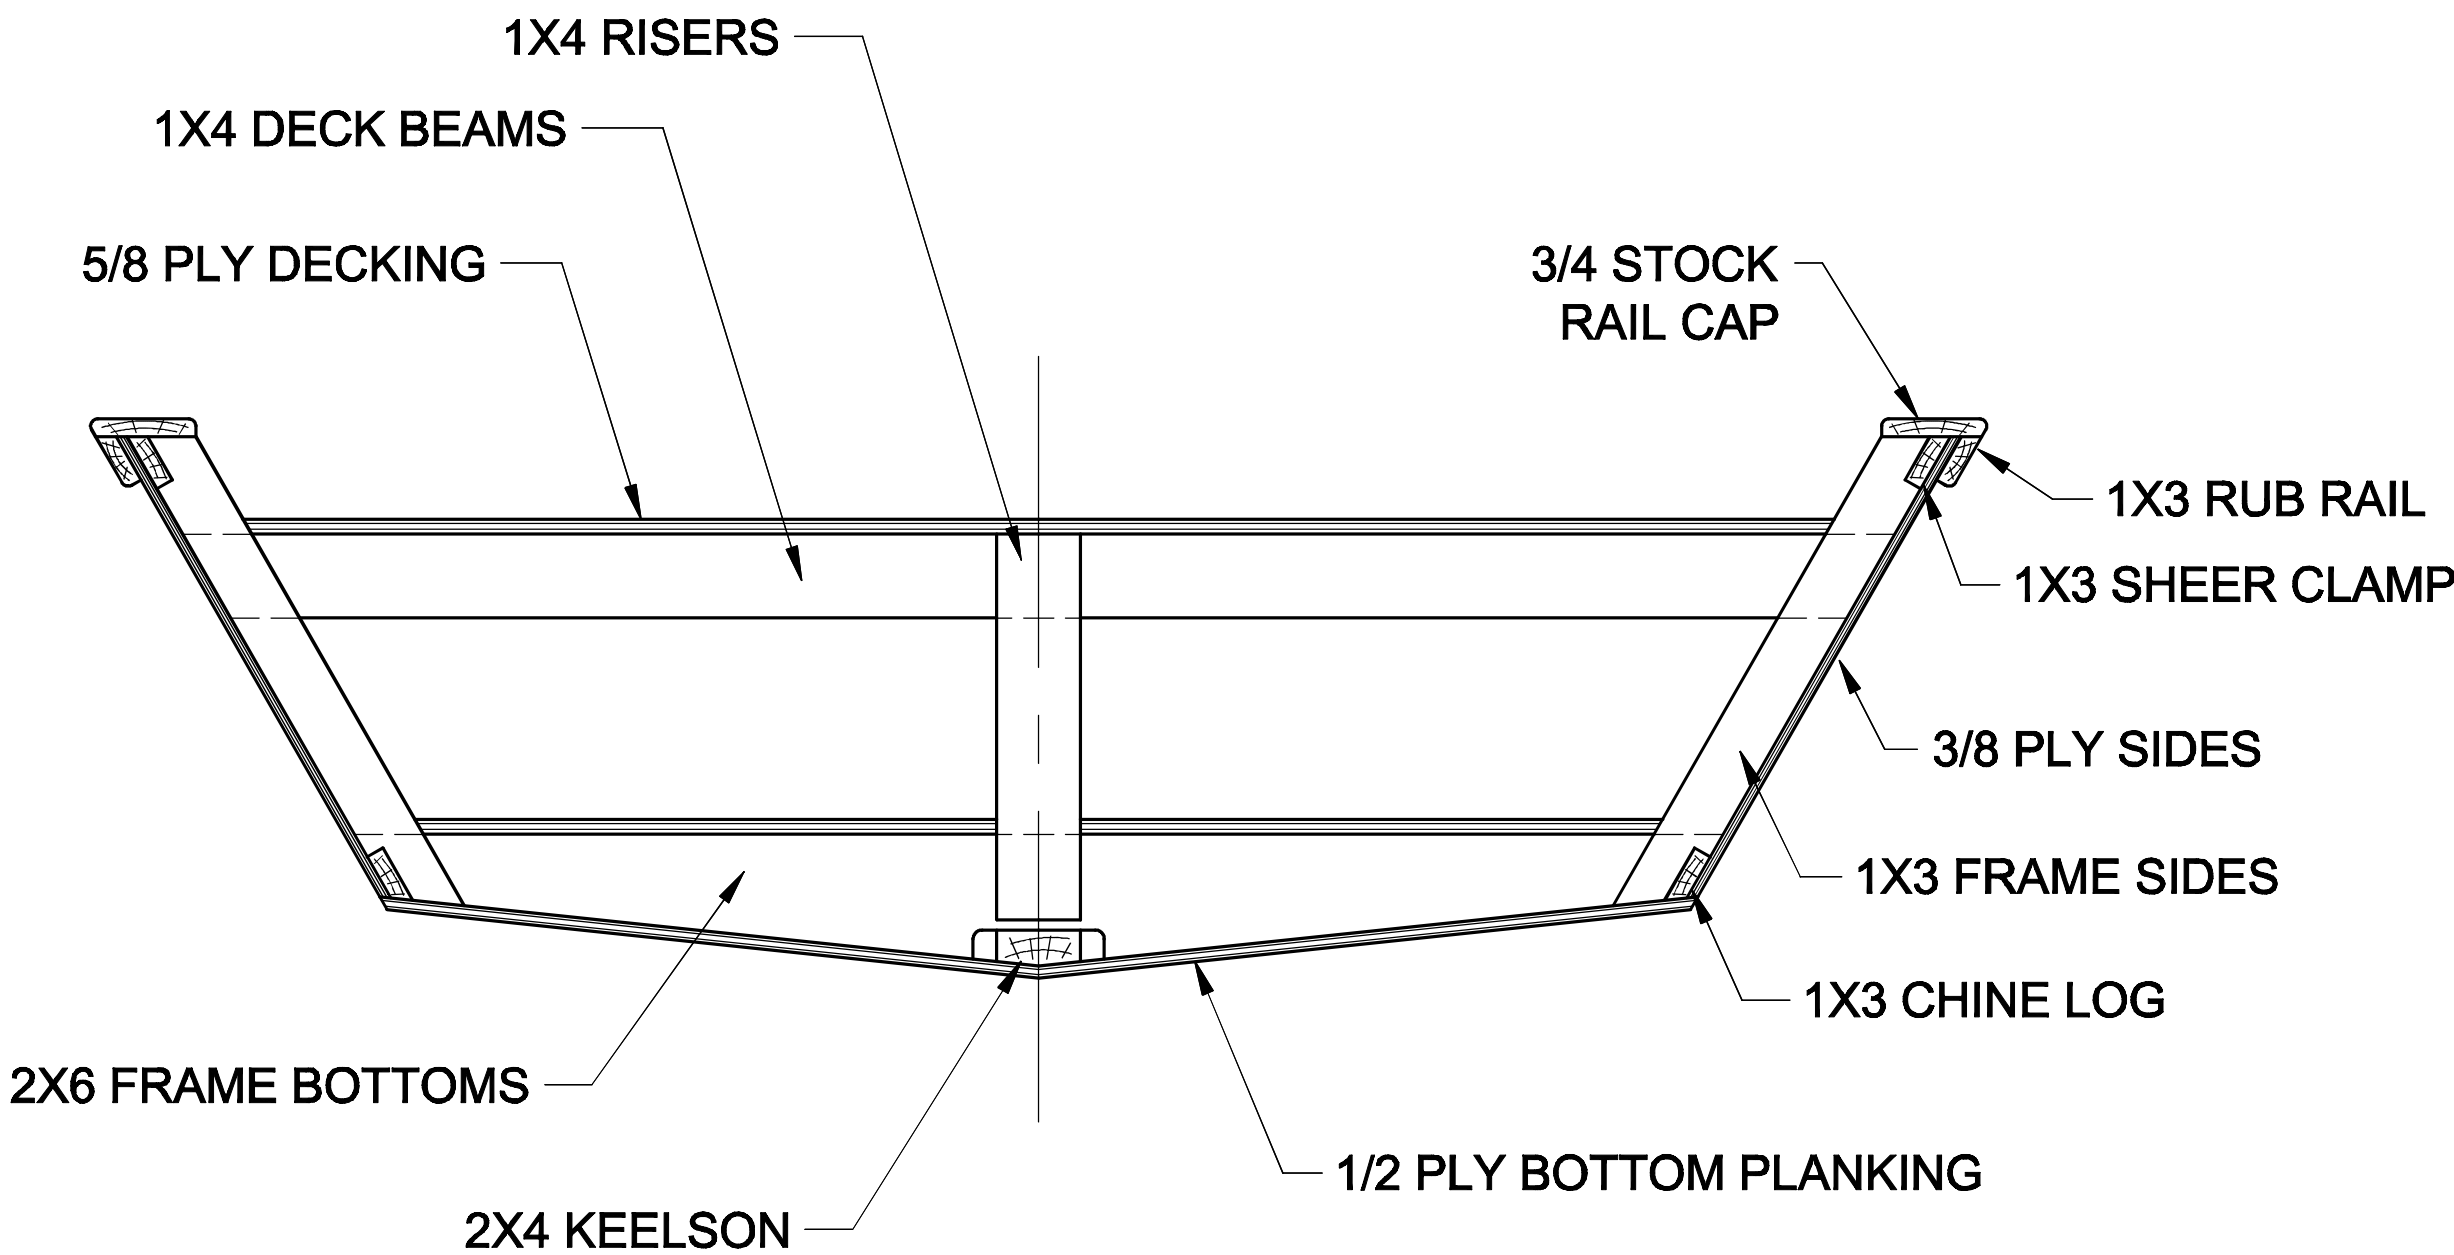

TYPICAL CONSTRUCTION
CROSS SECTION

NOTES:

1. YOU MAY SCARF TOGETHER SHORTER PIECES TO CREATE THE LONGITUDINAL ELEMENTS.
2. NOMINAL LUMBER SIZED CALLED OUT, E.G. A 2 X 4 LUMBER IS ACTUAL SIZE 1-1/2" X 3-1/2"

BILL OF MATERIALS

4 SHEETS 1/2" PLY FOR BOTTOM
4 SHEETS 3/8" PLY FOR SIDES
4 SHEETS 5/8" PLY FOR DECKING
60' 2X6 LUMBER FOR FRAMES
250' 1X3 LUMBER FOR SHEER CLAMP
CHINE LOG, RUB RAILS & DECKING
32' 1X6 LUMBER FOR RAIL CAP
36' 1X4 LUMBER FOR DECK BEAMS
19' 2X4 LUMBER FOR KEELSON & STEM
100 #10 X 2-1/2" DECK SCREWS
200 #10 X 2" DECK SCREWS
200 #10 X 1-1/4 DECK SCREWS
500 #8 X 1-1/2 DECK SCREWS
100 #8 X 2" DECK SCREWS
1-1/2 GALLON EPOXY RESIN & HARDENER
15 YDS 6 OZ FIBERGLASS CLOTH

FASTENING SCHEDULE

2x FRAME TO 2x FRAME: #10 X 2 -1/2 DECK SCREWS
1x FRAME TO 2x FRAME: #10 X 2 DECK SCREWS
1x FRAME TO 1x FRAME: #10 X 1 - 1/4 DECK SCREWS
PLANKING TO FRAME: #8 X 1-1/2 DECK SCREWS
LONGITUDINAL TO FRAME: #8 X 2 DECK SCREWS

Spira International, Inc.
Huntington Beach, California

SKEETER
16' BASS BOAT

DRAWN BY: J. SPIRA	DATE: 12/03/12	DRAWING NO. SKEE02
SCALE 3/4" = 1'	SHEET	OF