

4

3


2


1

NOTICE

THIS DRAWING CONTAINS A PROPRIETARY DESIGN ASSIGNED TO SPIRA INTERNATIONAL, INC. ALL RIGHTS TO DUPLICATE, TRANSFER OR USE ARE EXPRESSLY RESERVED BY SPIRA INTERNATIONAL. THE BUYER IS LICENSED TO BUILD ONE ASSEMBLY FROM THESE PLANS.

REVISIONS				
ZONE	LTR	DESCRIPTION	DATE	APPROVED
	A	ADDED WATERLINE AND SPECIFICATIONS	11/14/15	JJS

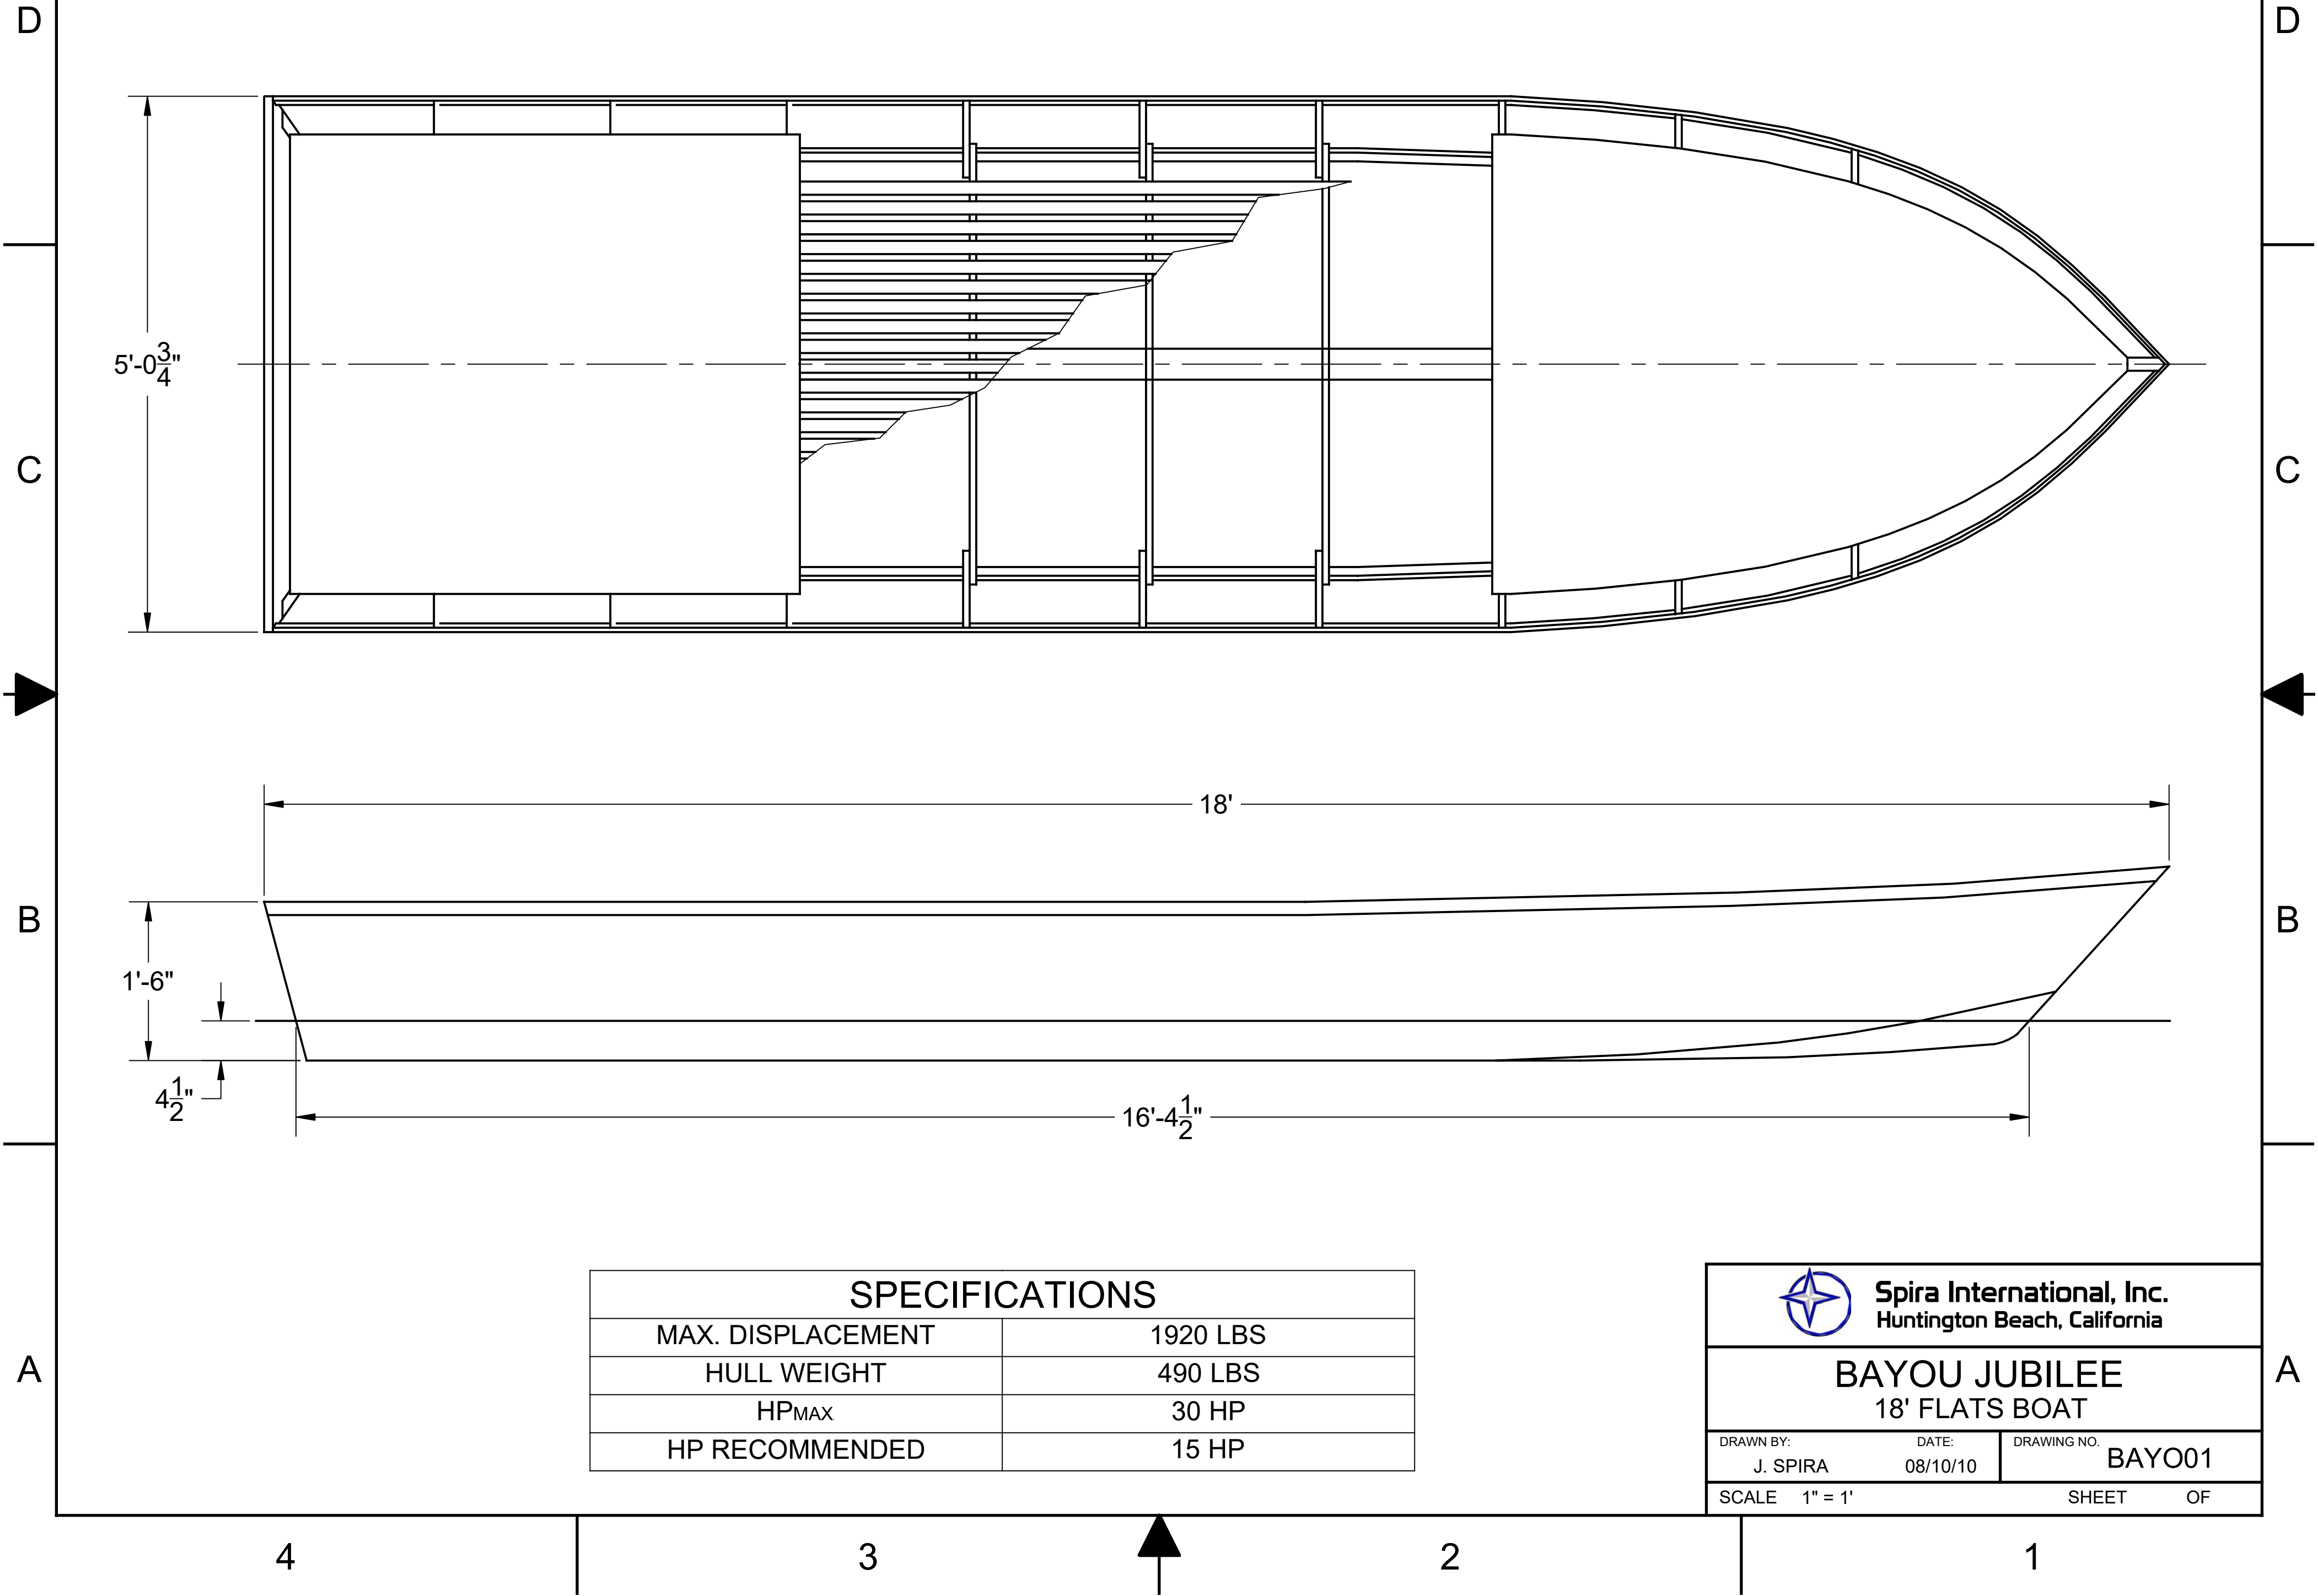

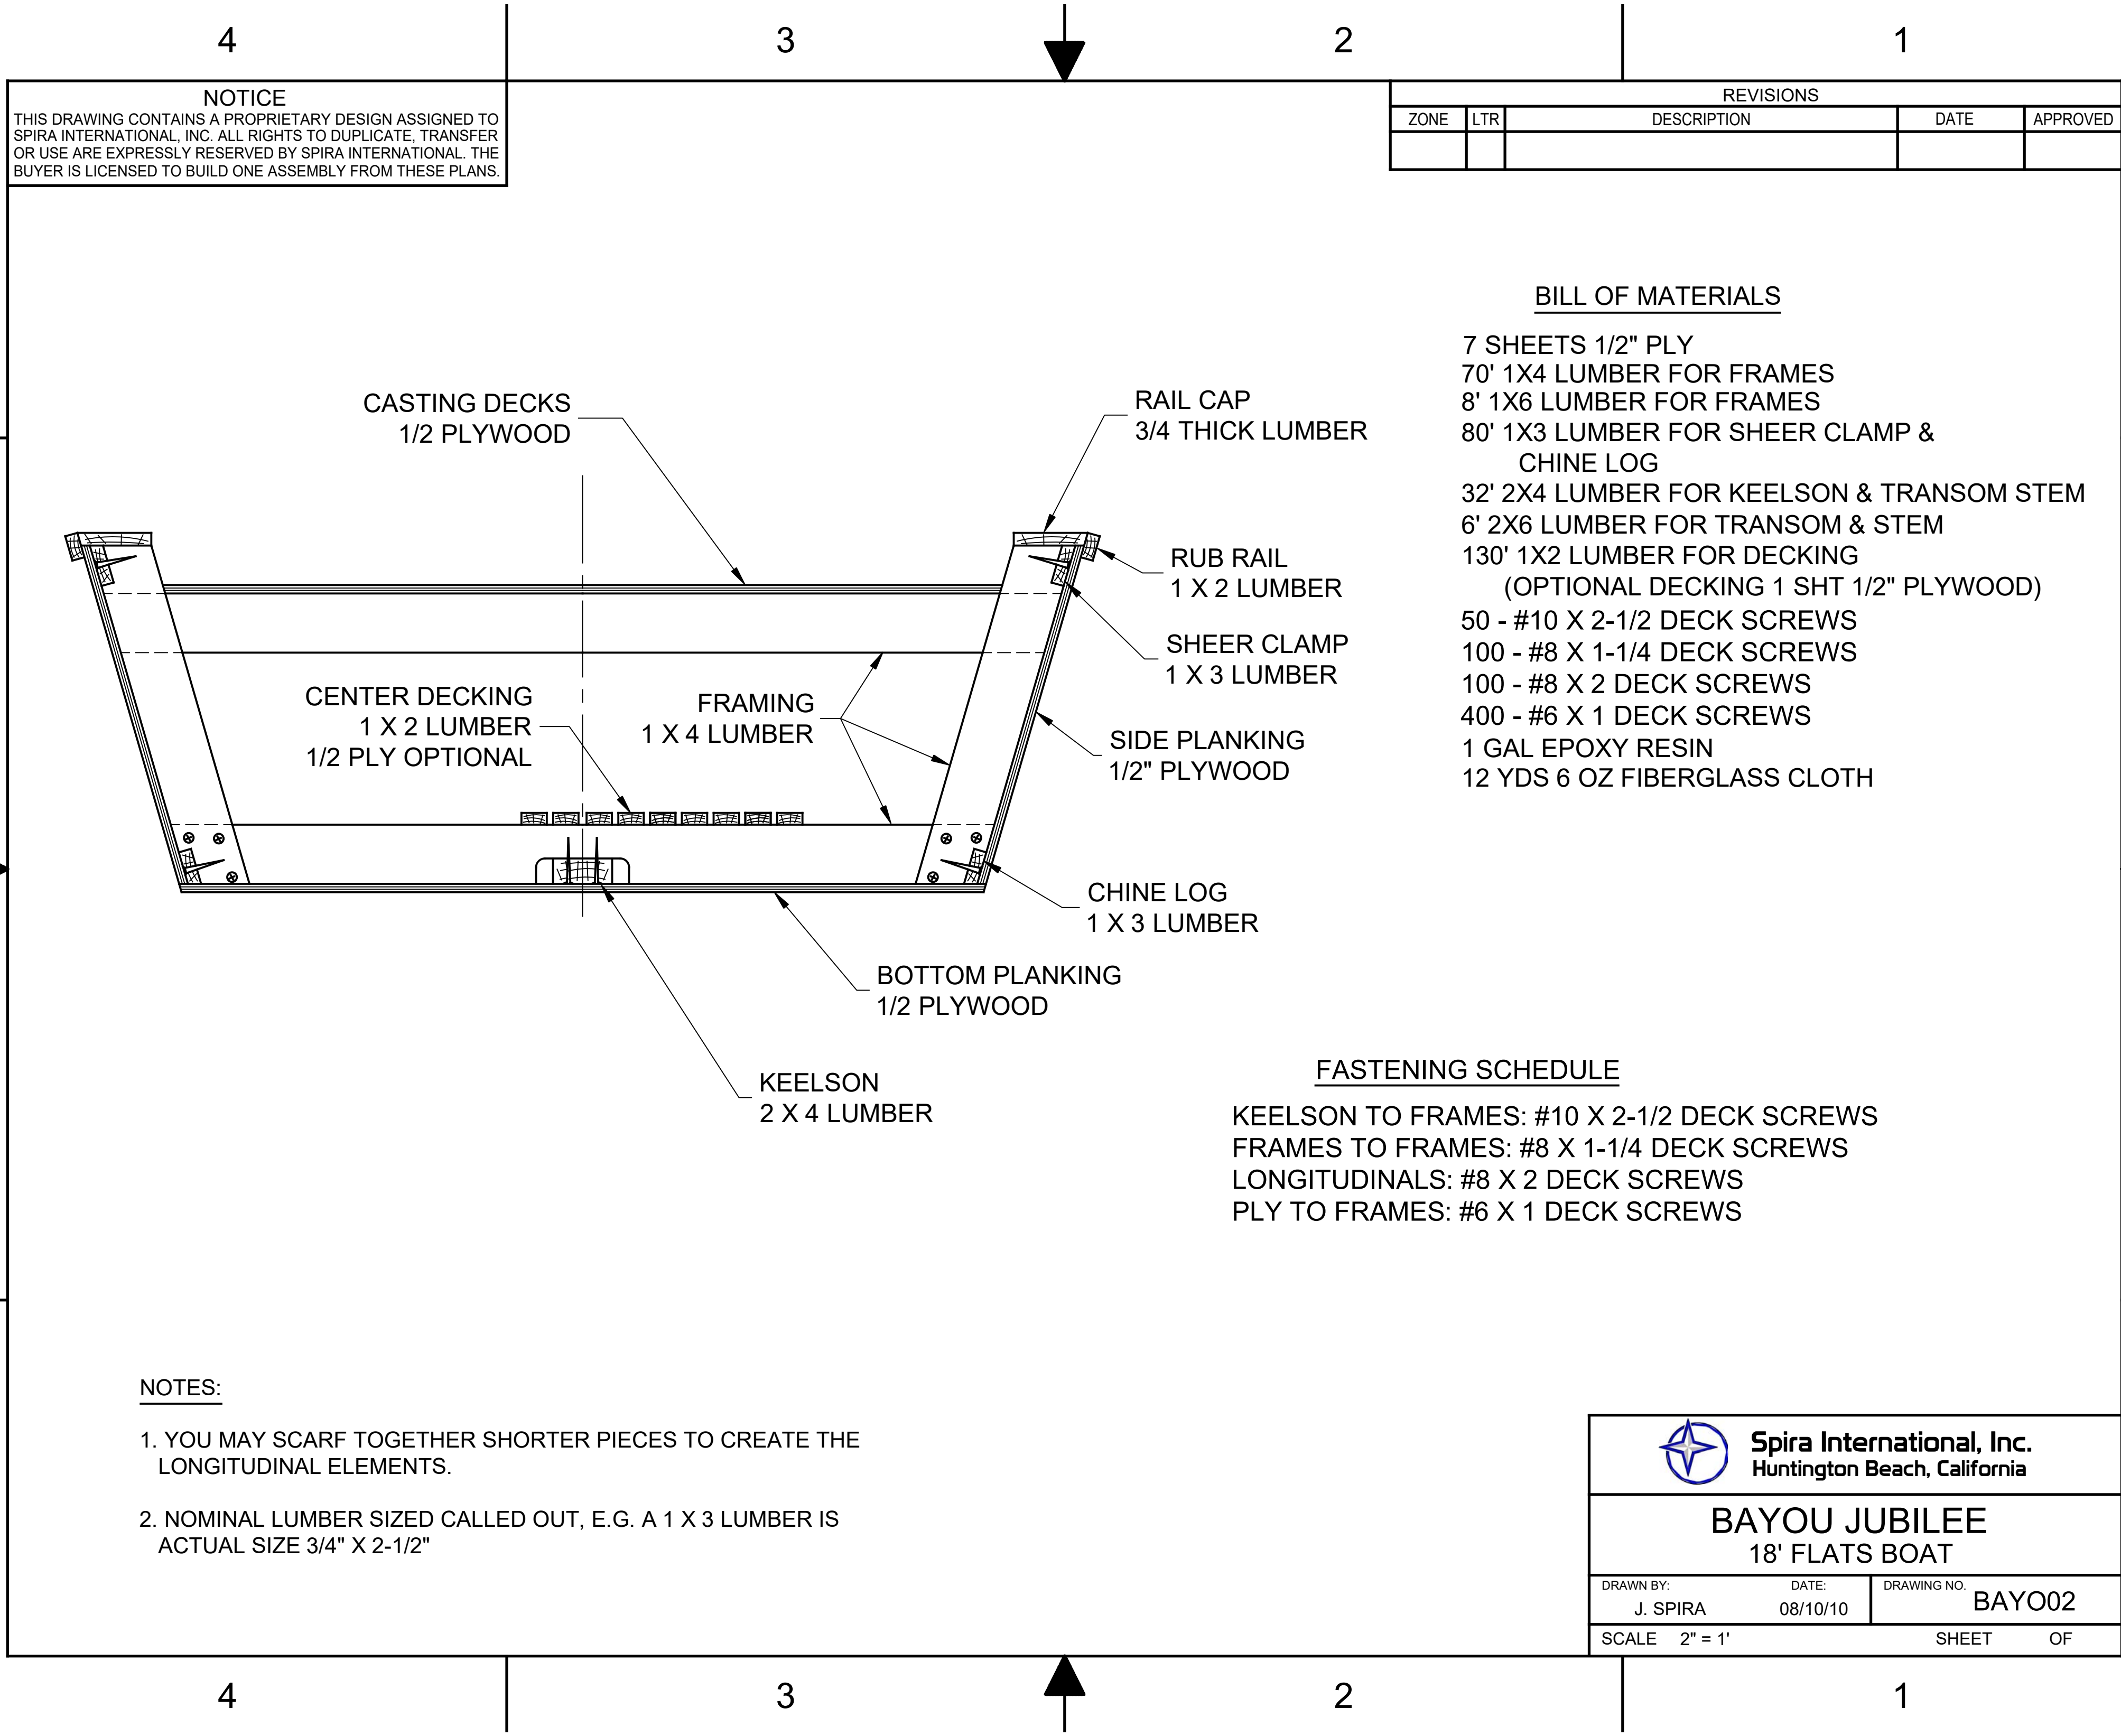

NOTICE
THIS DRAWING CONTAINS A PROPRIETARY DESIGN ASSIGNED TO SPIRA INTERNATIONAL, INC. ALL RIGHTS TO DUPLICATE, TRANSFER OR USE ARE EXPRESSLY RESERVED BY SPIRA INTERNATIONAL. THE BUYER IS LICENSED TO BUILD ONE ASSEMBLY FROM THESE PLANS.

REVISIONS				
ZONE	LTR	DESCRIPTION	DATE	APPROVED

BILL OF MATERIALS

7 SHEETS 1/2" PLY
70' 1X4 LUMBER FOR FRAMES
8' 1X6 LUMBER FOR FRAMES
80' 1X3 LUMBER FOR SHEER CLAMP & CHINE LOG
32' 2X4 LUMBER FOR KEELSON & TRANSOM STEM
6' 2X6 LUMBER FOR TRANSOM & STEM
130' 1X2 LUMBER FOR DECKING
(OPTIONAL DECKING 1 SHT 1/2" PLYWOOD)
50 - #10 X 2-1/2 DECK SCREWS
100 - #8 X 1-1/4 DECK SCREWS
100 - #8 X 2 DECK SCREWS
400 - #6 X 1 DECK SCREWS
1 GAL EPOXY RESIN
12 YDS 6 OZ FIBERGLASS CLOTH

FASTENING SCHEDULE

KEELSON TO FRAMES: #10 X 2-1/2 DECK SCREWS
FRAMES TO FRAMES: #8 X 1-1/4 DECK SCREWS
LONGITUDINALS: #8 X 2 DECK SCREWS
PLY TO FRAMES: #6 X 1 DECK SCREWS

NOTES:

1. YOU MAY SCARF TOGETHER SHORTER PIECES TO CREATE THE LONGITUDINAL ELEMENTS.
2. NOMINAL LUMBER SIZED CALLED OUT, E.G. A 1 X 3 LUMBER IS ACTUAL SIZE 3/4" X 2-1/2"



Spira International, Inc.
Huntington Beach, California

BAYOU JUBILEE
18' FLATS BOAT

DRAWN BY: J. SPIRA	DATE: 08/10/10	DRAWING NO. BAYO02
SCALE 2" = 1'	SHEET	OF