

4

3


2

1

NOTICE

THIS DRAWING CONTAINS A PROPRIETARY DESIGN ASSIGNED TO SPIRA INTERNATIONAL, INC. ALL RIGHTS TO DUPLICATE, TRANSFER OR USE ARE EXPRESSLY RESERVED BY SPIRA INTERNATIONAL. THE BUYER IS LICENSED TO BUILD ONE ASSEMBLY FROM THESE PLANS.


REVISIONS				
ZONE	LTR	DESCRIPTION	DATE	APPROVED

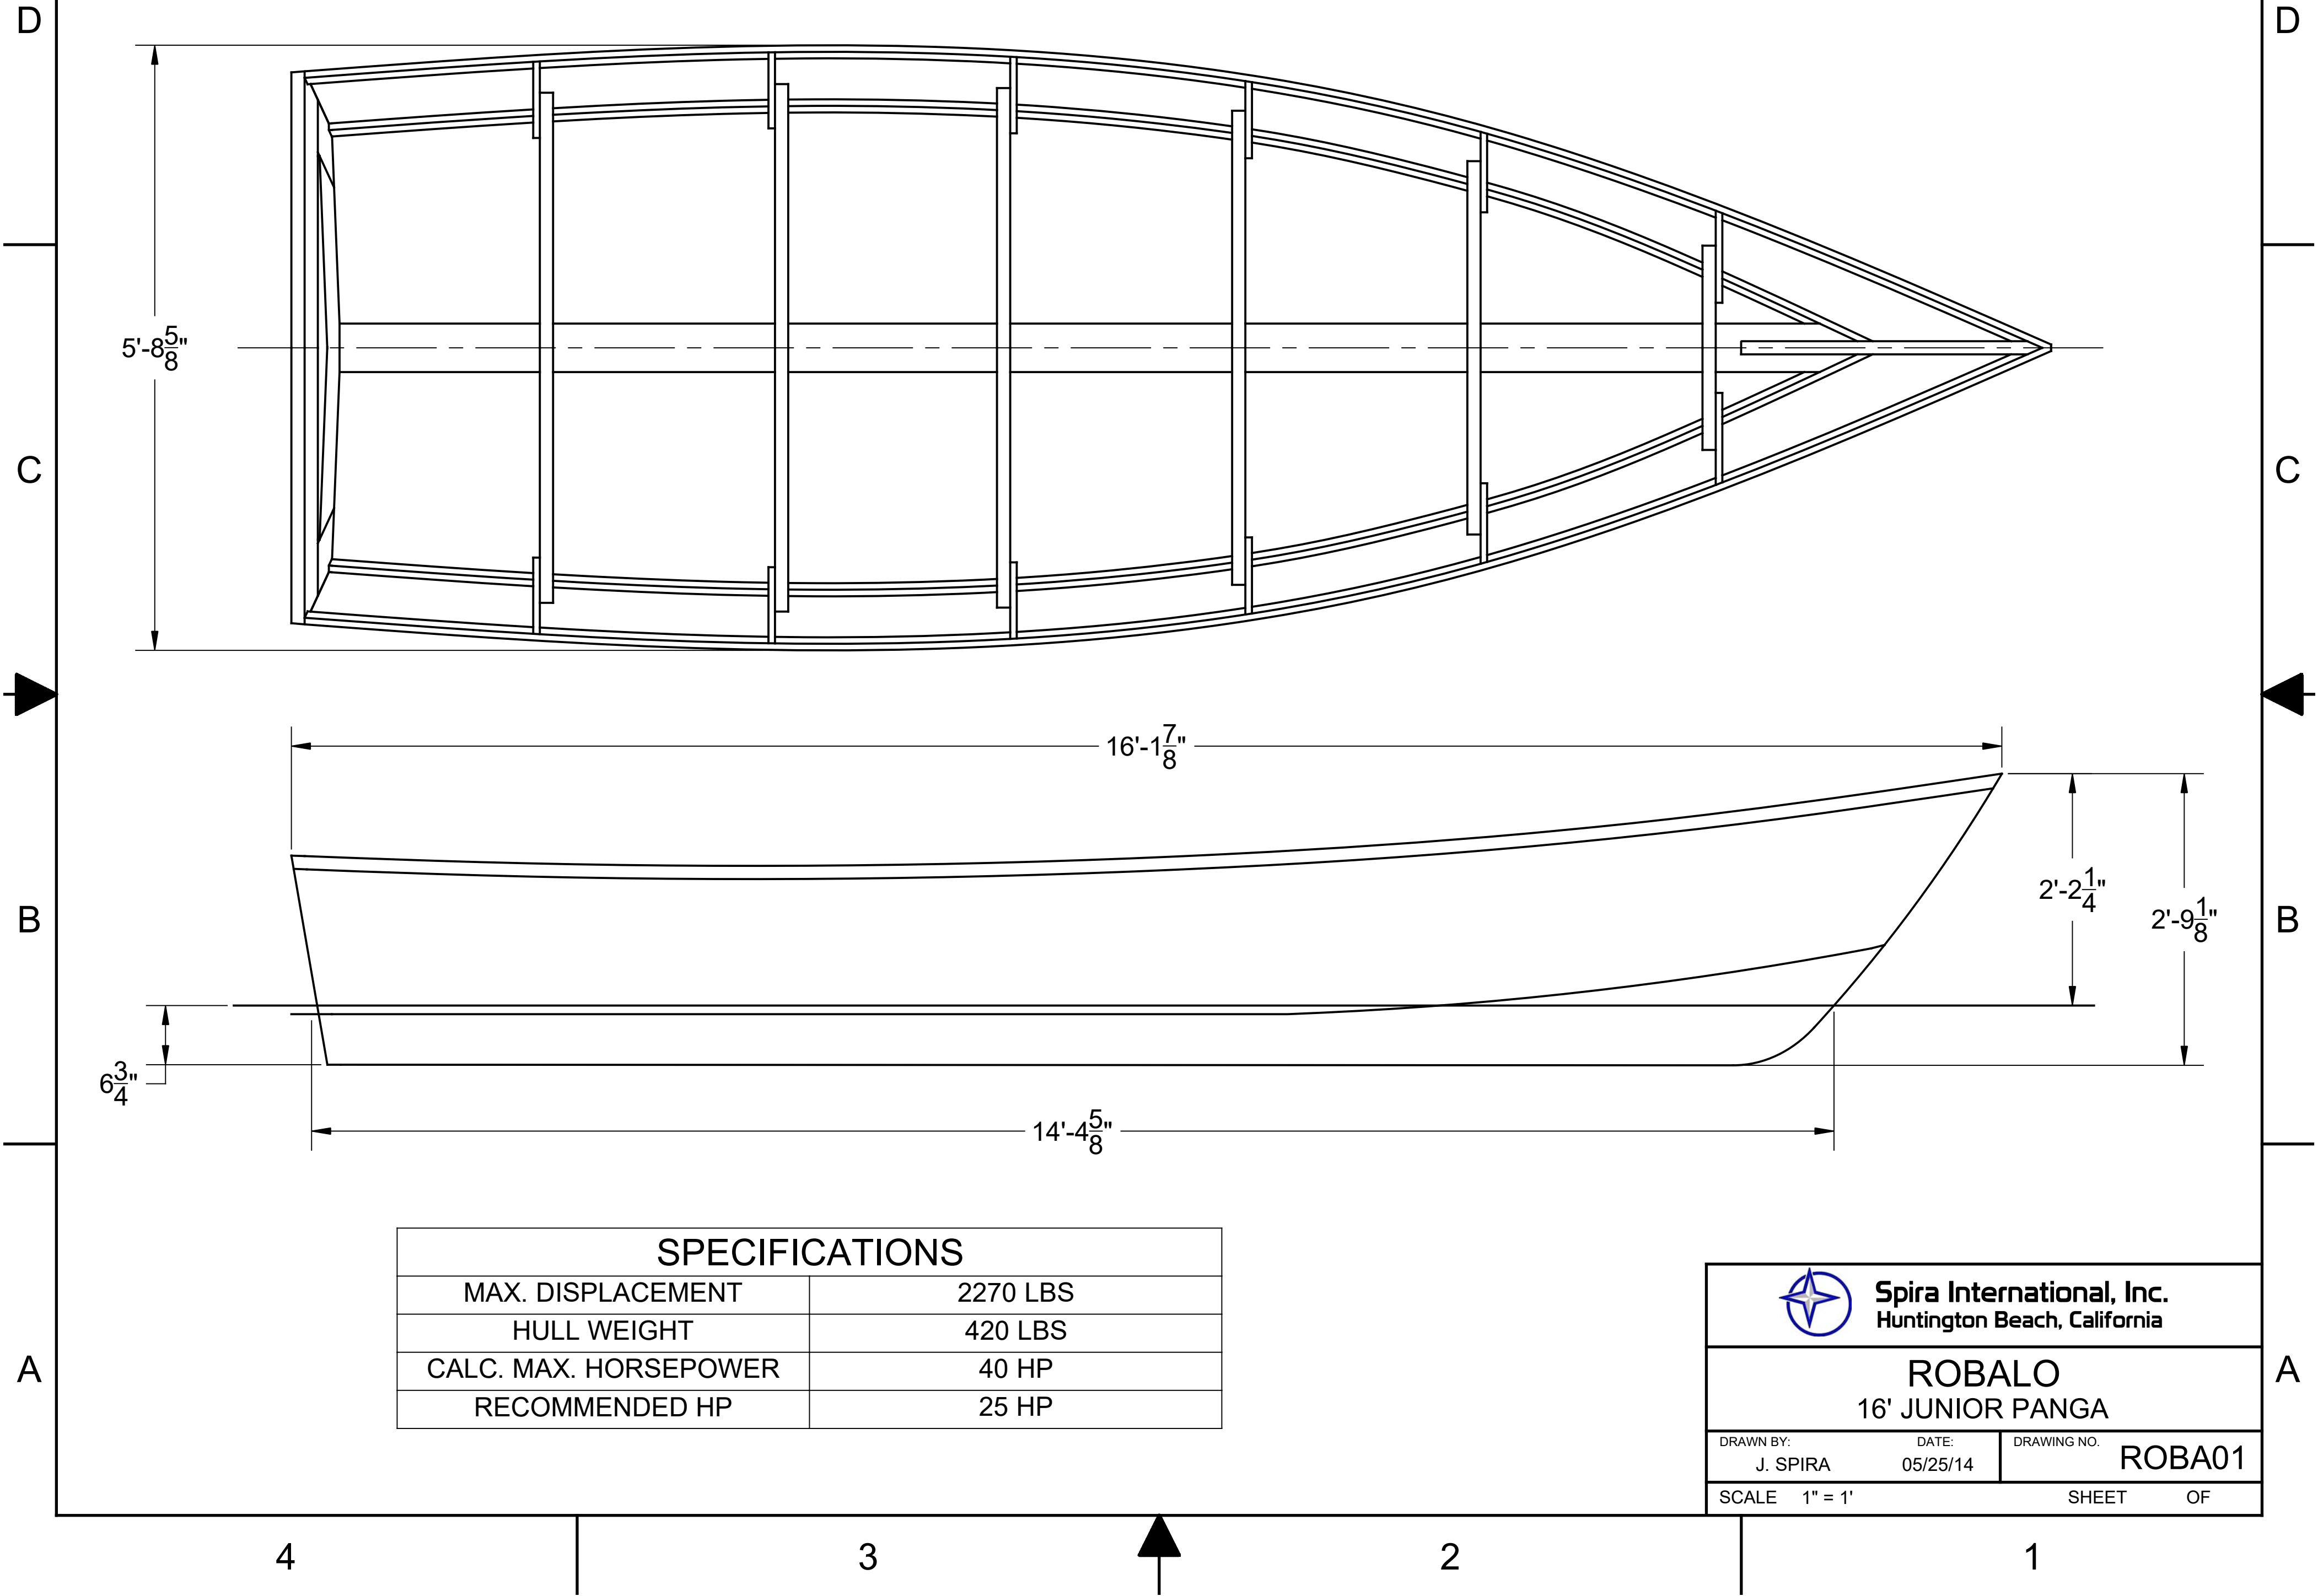

4 3 2 1

NOTICE
THIS DRAWING CONTAINS A PROPRIETARY DESIGN ASSIGNED TO SPIRA INTERNATIONAL, INC. ALL RIGHTS TO DUPLICATE, TRANSFER OR USE ARE EXPRESSLY RESERVED BY SPIRA INTERNATIONAL. THE BUYER IS LICENSED TO BUILD ONE ASSEMBLY FROM THESE PLANS.

REVISIONS				
ZONE	LTR	DESCRIPTION	DATE	APPROVED

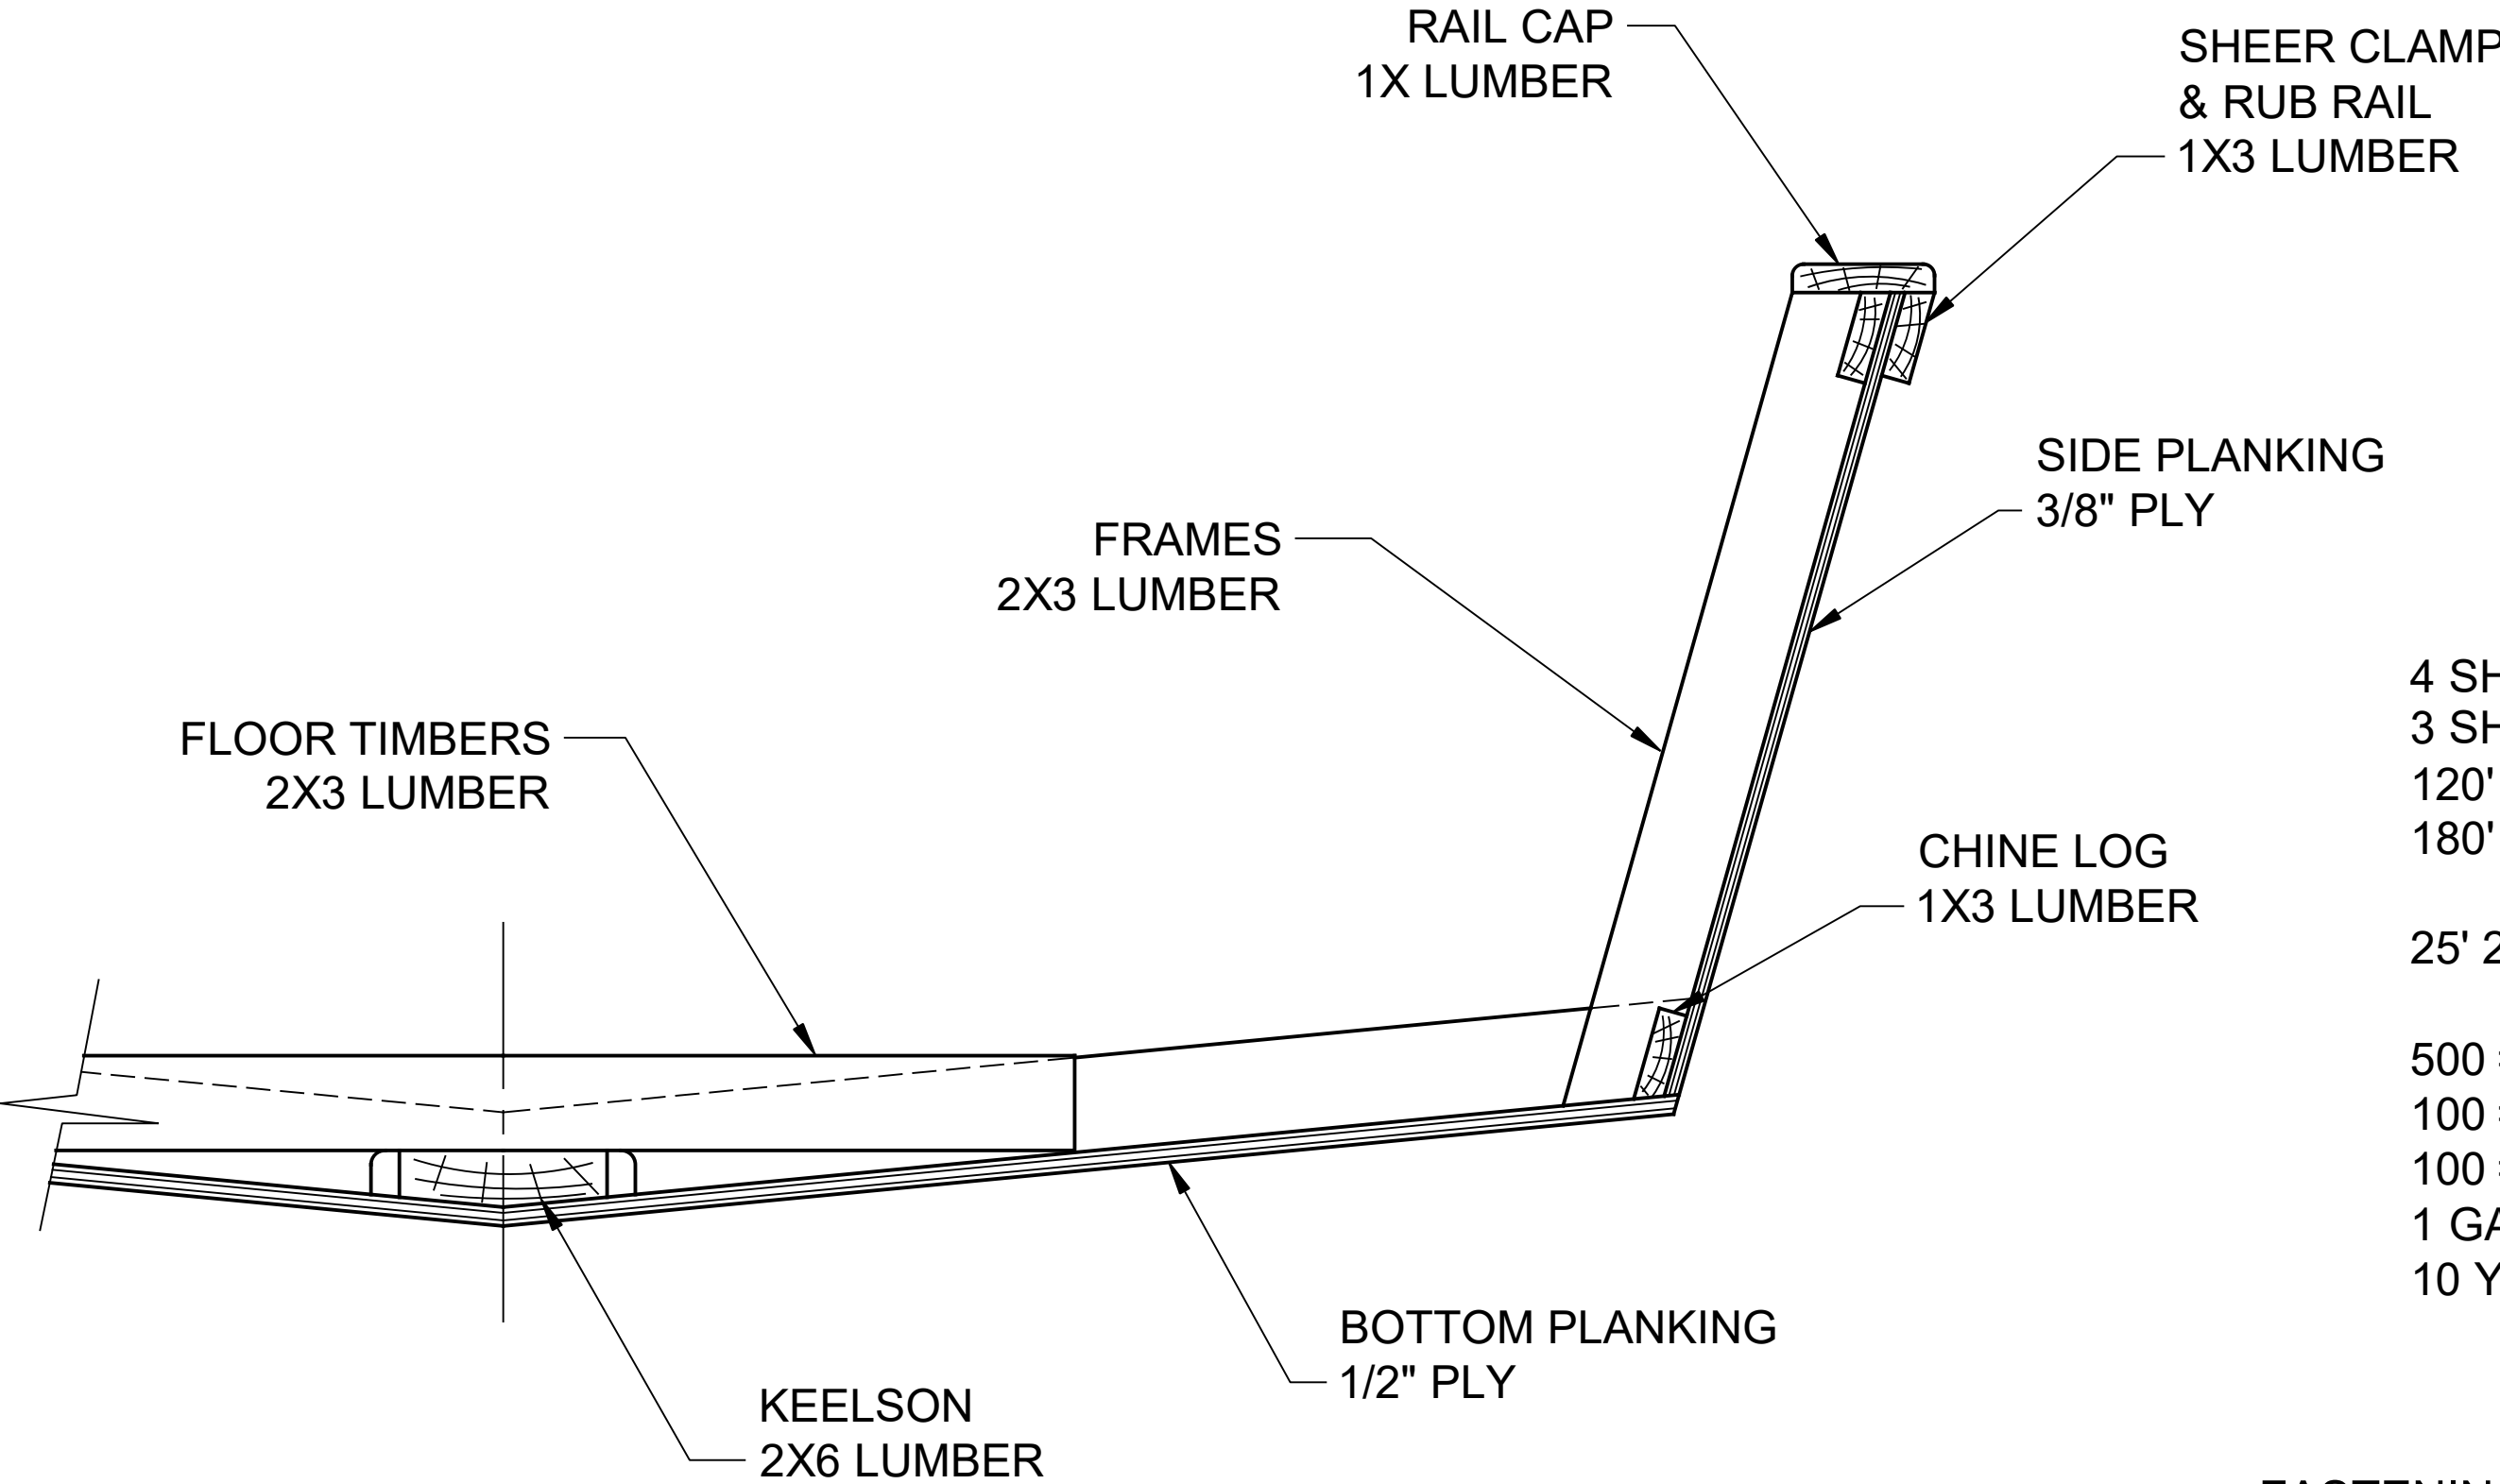

BILL OF MATERIALS

4 SHEETS 1/2" PLY FOR BOTTOM
3 SHEETS 3/8" PLY FOR SIDES
120' 2X3 LUMBER FOR FRAMES (5/4 X 3 OPTIONAL)
180' 1X3 LUMBER FOR SHEER CLAMP
CHINE LOG AND RUB RAILS
25' 2X6 LUMBER FOR KEELSON
TRANSOM & STEM
500 #8 X 1-1/2" DECK SCREWS
100 #8 X 2 DECK SCREWS
100 #10 X 2-1/2 DECK SCREWS
1 GAL EPOXY RESIN
10 YDS 6 OZ FIBERGLASS CLOTH

FASTENING SCHEDULE

FRAME TO FRAME: #10 X 2 -1/2 DECK SCREWS
PLANKING TO FRAME: #8 X 1-1/2 DECK SCREWS
LONGITUDINAL TO FRAME: #8 X 2 DECK SCREWS

NOTES:

1. YOU MAY SCARF TOGETHER SHORTER PIECES TO CREATE THE LONGITUDINAL ELEMENTS.
2. NOMINAL LUMBER SIZED CALLED OUT, E.G. A 2 X 4 LUMBER IS ACTUAL SIZE 1-1/2" X 3-1/2" - IMPERIAL SIZES ONLY

A

 **Spira International, Inc.**
Huntington Beach, California

ROBALO
16' JUNIOR PANGA

DRAWN BY: J. SPIRA	DATE: 05/25/14	DRAWING NO. ROBA02
SCALE 1" = 1'		SHEET OF