


4 3 2 1

NOTICE
THIS DRAWING CONTAINS A PROPRIETARY DESIGN ASSIGNED TO SPIRA INTERNATIONAL, INC. ALL RIGHTS TO DUPLICATE, TRANSFER OR USE ARE EXPRESSLY RESERVED BY SPIRA INTERNATIONAL. THE BUYER IS LICENSED TO BUILD ONE ASSEMBLY FROM THESE PLANS.


REVISIONS				
ZONE	LTR	DESCRIPTION	DATE	APPROVED

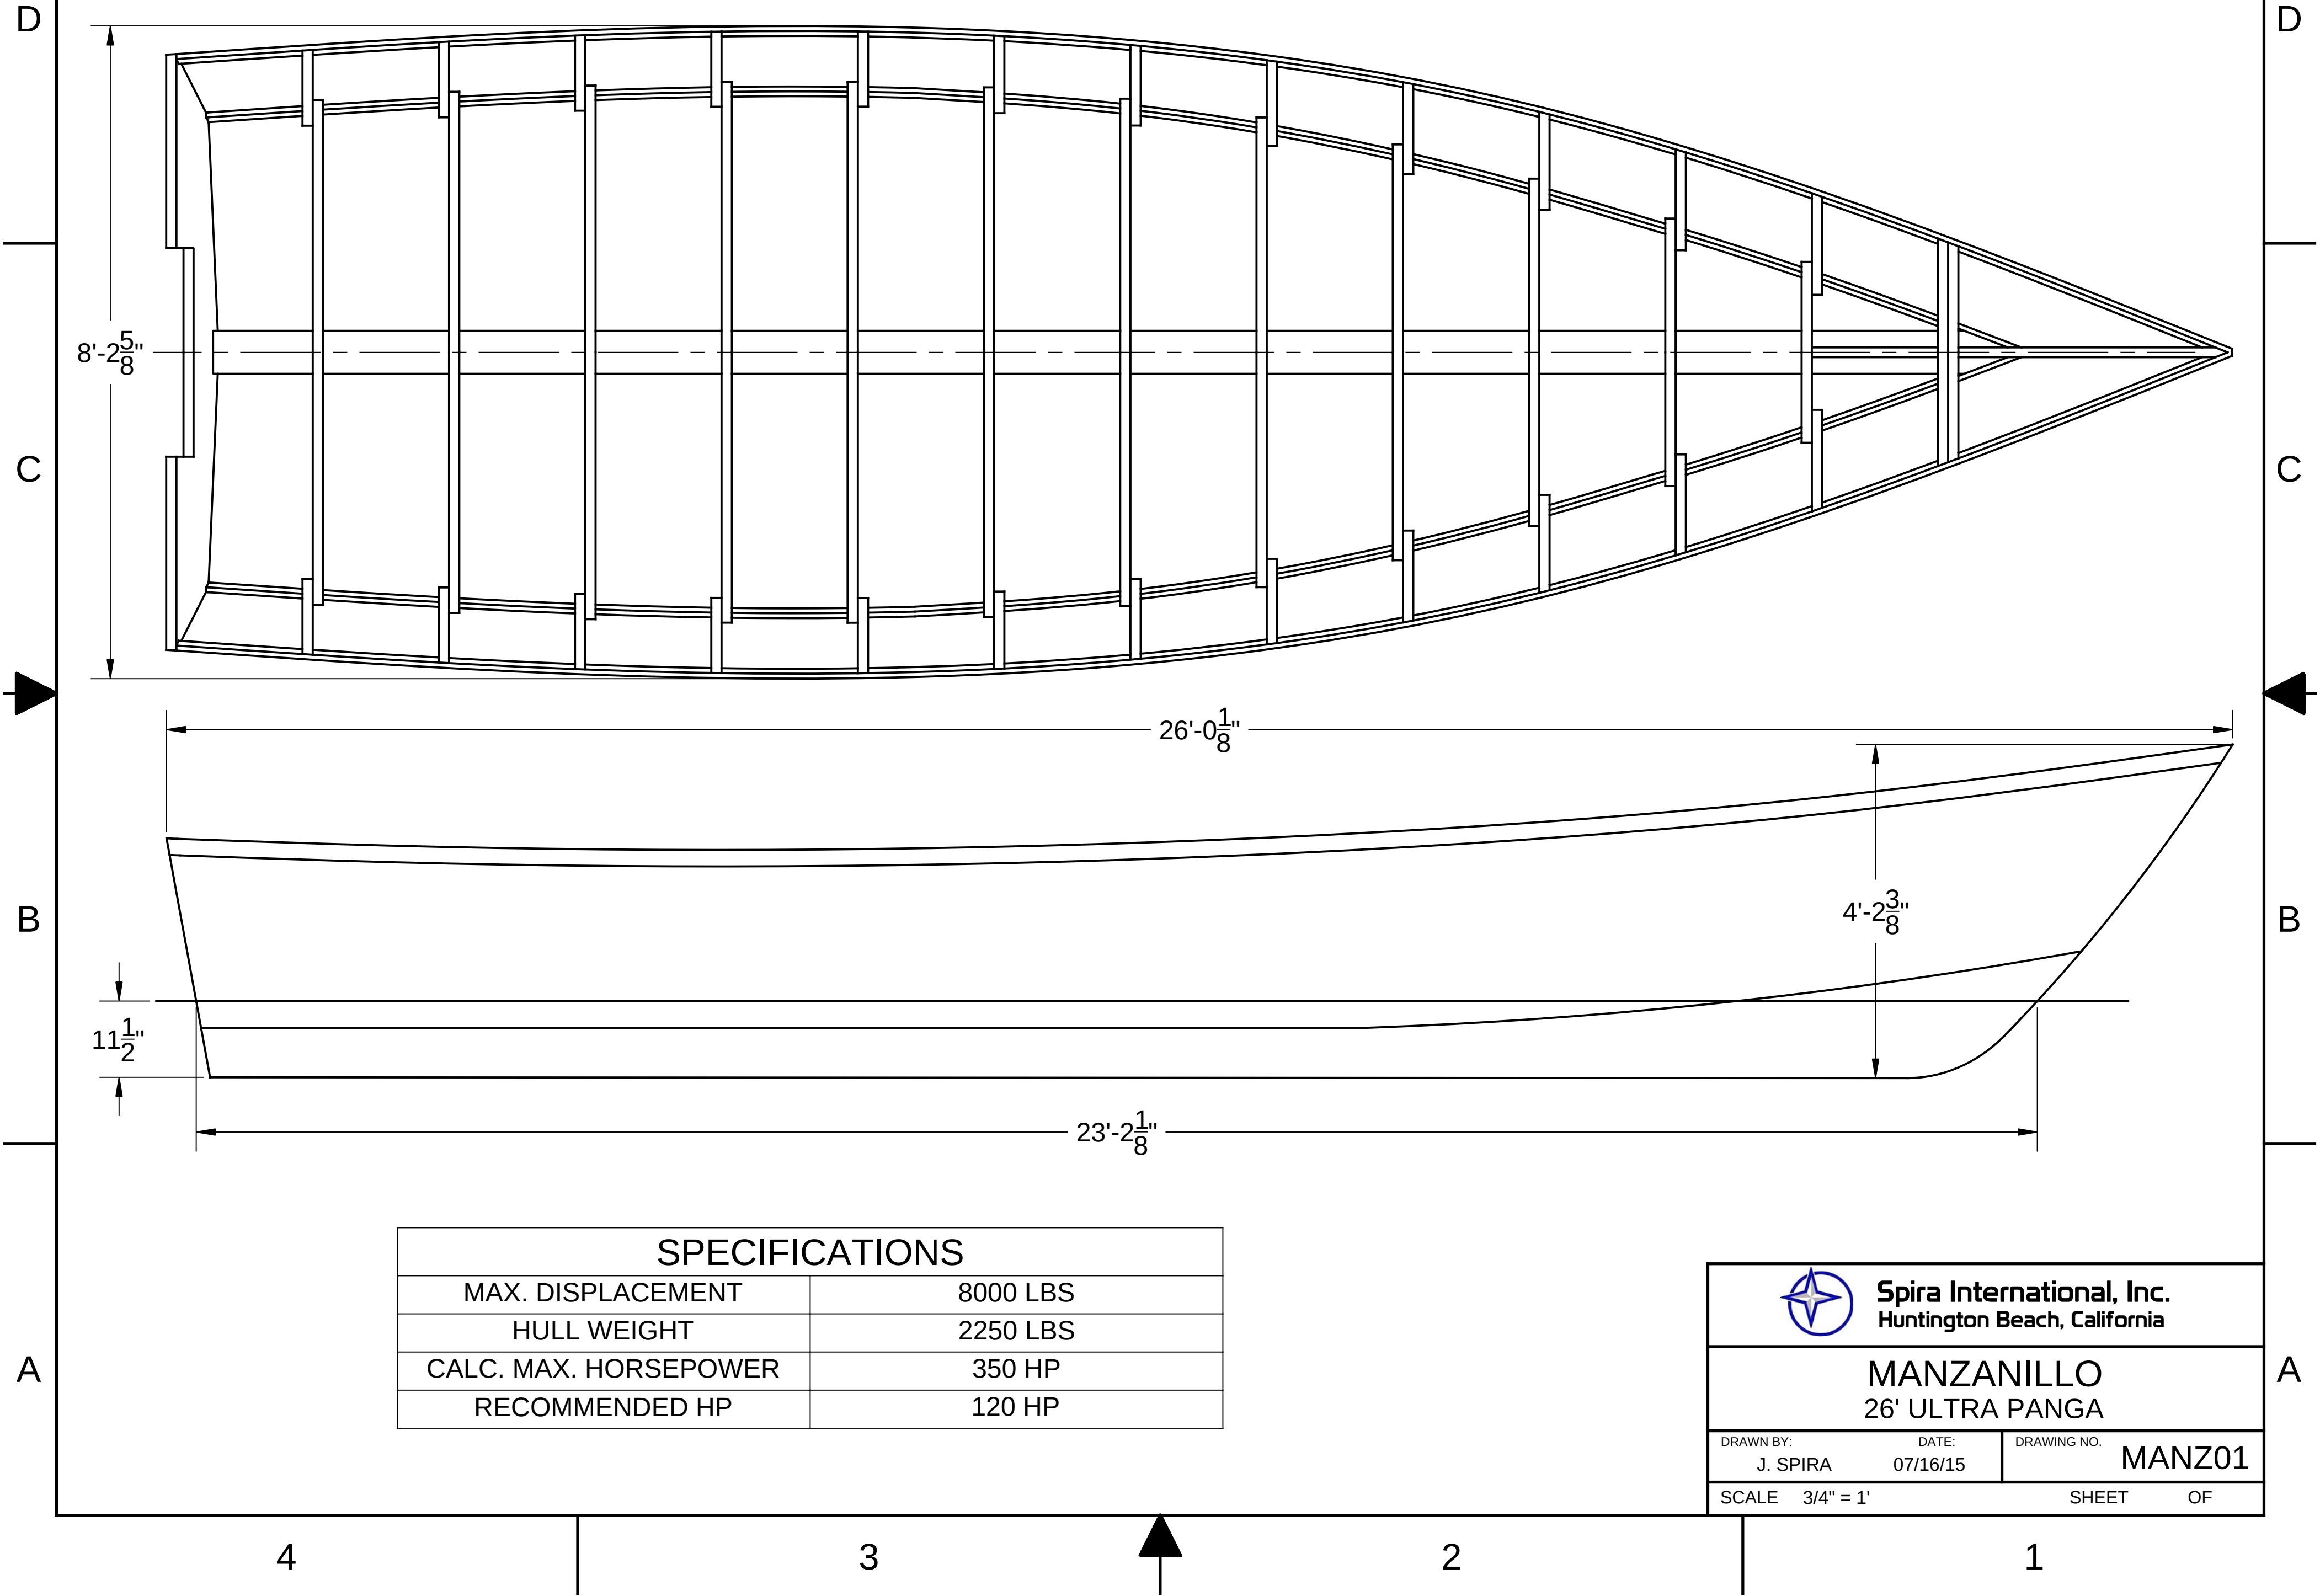

4 3 2 1

NOTICE
THIS DRAWING CONTAINS A PROPRIETARY DESIGN ASSIGNED TO SPIRA INTERNATIONAL, INC. ALL RIGHTS TO DUPLICATE, TRANSFER OR USE ARE EXPRESSLY RESERVED BY SPIRA INTERNATIONAL. THE BUYER IS LICENSED TO BUILD ONE ASSEMBLY FROM THESE PLANS.

REVISIONS				
ZONE	LTR	DESCRIPTION	DATE	APPROVED

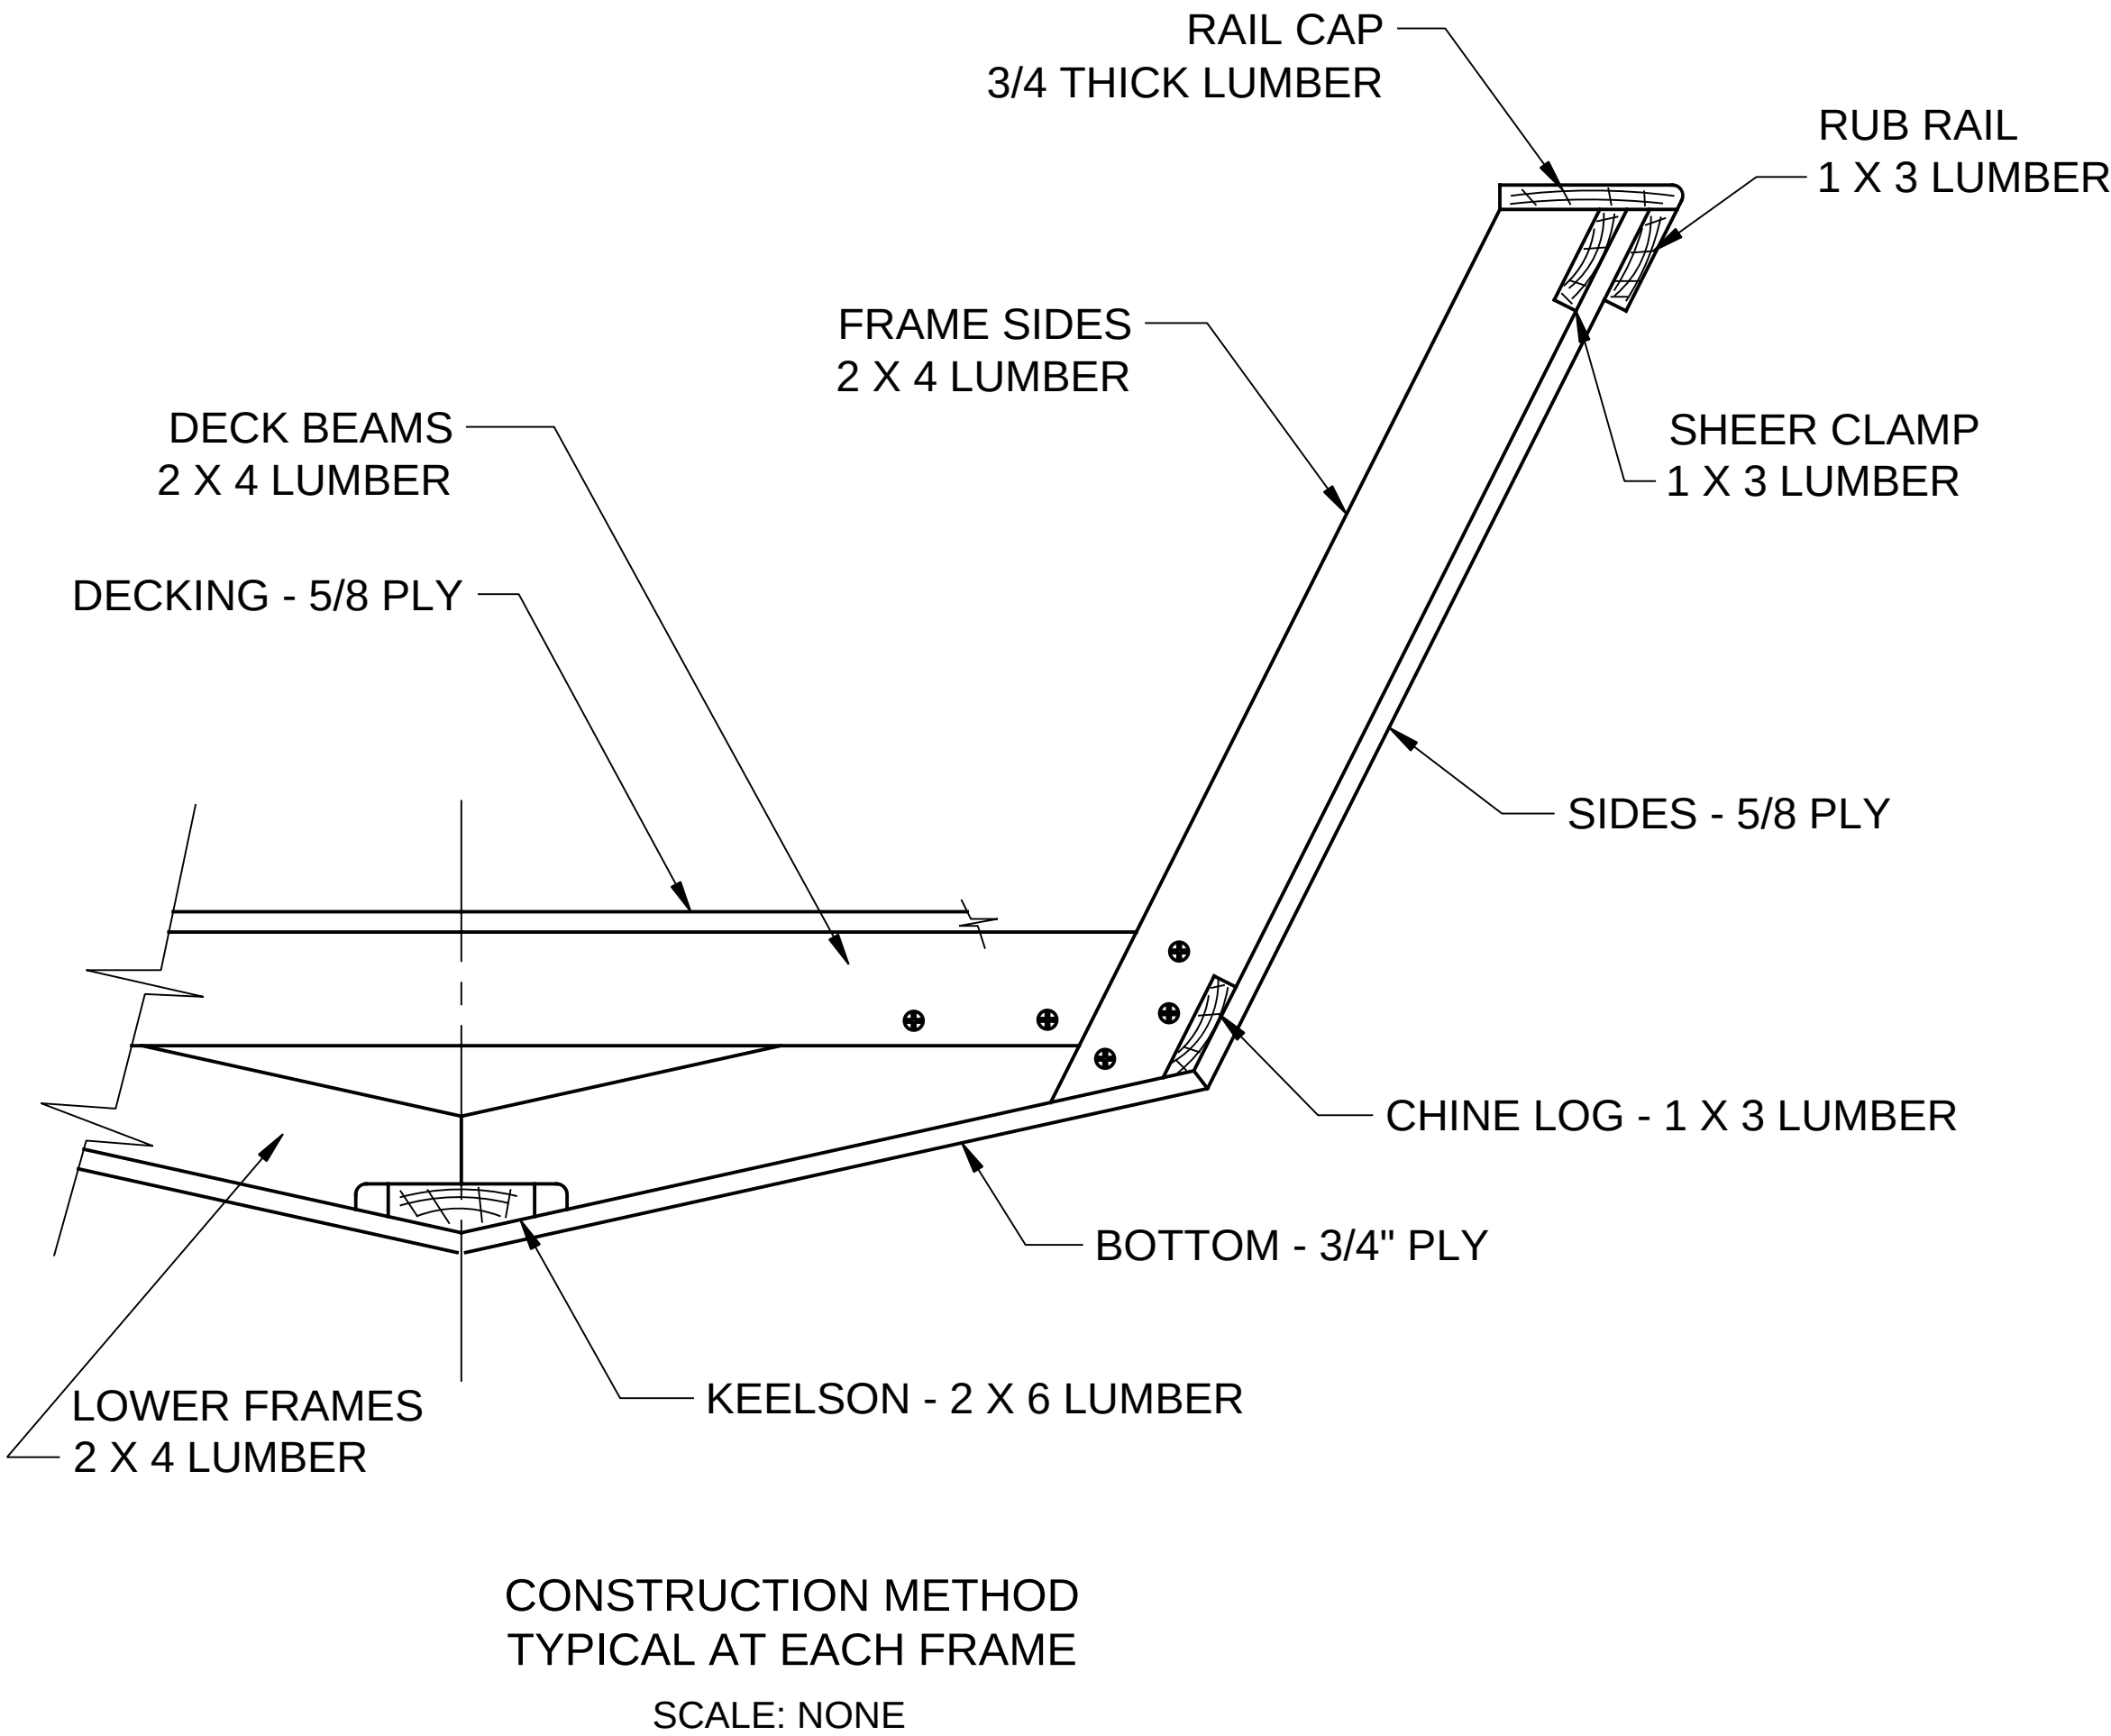

BILL OF MATERIALS (HULL ONLY)

14 SHEETS 5/8" PLY
7 SHEETS 3/4 PLY
280' 2X4 LUMBER FOR FRAMES
220' 1X3 CLEAR LUMBER FOR SHEER
CLAMP, CHINE LOG AND RUB RAILS
26' 2X6 LUMBER FOR KEELSON
16' 2X8 LUMBER FOR TRANSOM & STEM
52' 1X8 LUMBER FOR RAIL CAP
300 #10 X 2-1/2 SS DECK SCREWS
300 #8 X 2 SS DECK SCREWS
3000 #8 X 1-1/2 SS DECK SCREWS
9 GAL EPOXY RESIN
60 YDS 50" WIDE, 10 OZ FIBERGLASS CLOTH

FASTENING SCHEDULE

2x FRAME TO 2x FRAME: #10 X 2 -1/2 DECK SCREWS
LONGITUDINAL TO FRAME: #10 X 2 DECK SCREWS
PLANKING TO FRAME: #10 X 1-1/2 DECK SCREWS

NOTES:

1. YOU MAY SCARF TOGETHER SHORTER PIECES TO CREATE THE LONGITUDINAL ELEMENTS.
2. NOMINAL LUMBER SIZED CALLED OUT, E.G. A 2 X 4 LUMBER IS ACTUAL SIZE 1-1/2" X 3-1/2"



Spira International, Inc.
Huntington Beach, California

MANZANILLO
26' ULTRA PANGA

DRAWN BY:
J. SPIRA

DATE:
07/16/15

DRAWING NO.
MANZ02

SCALE 3/4" = 1'

SHEET OF