


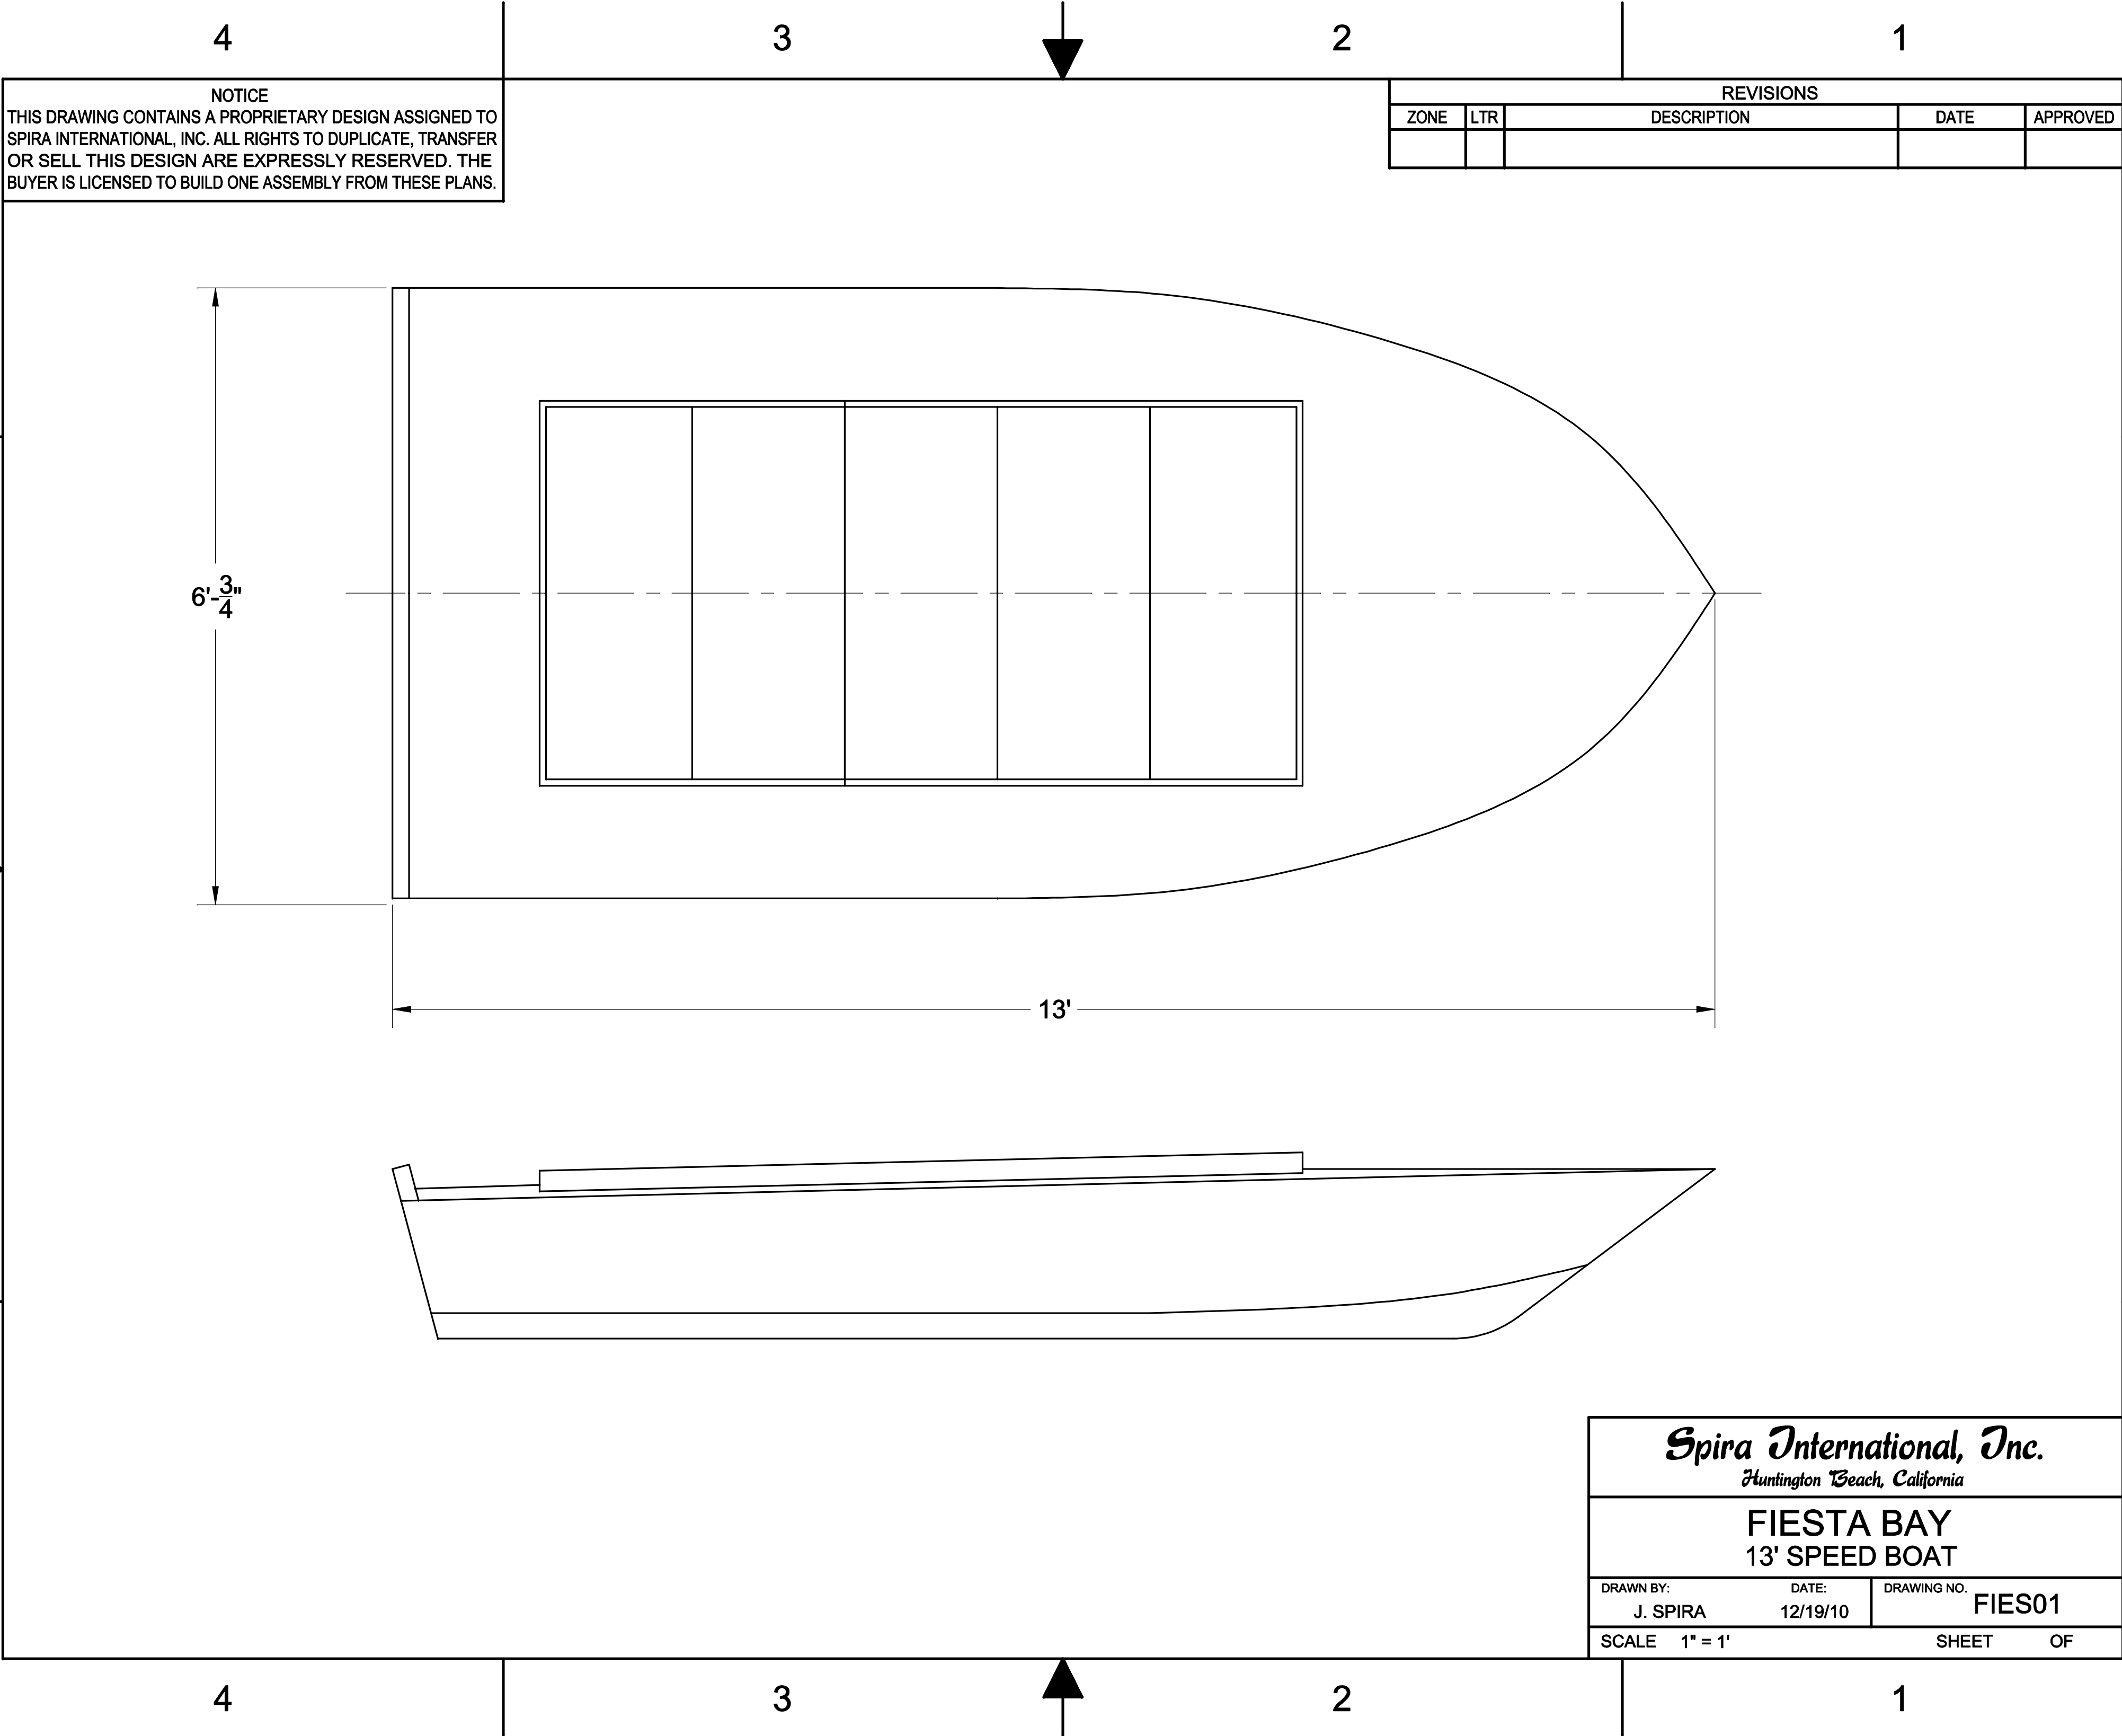

NOTICE
THIS DRAWING CONTAINS A PROPRIETARY DESIGN ASSIGNED TO SPIRA INTERNATIONAL, INC. ALL RIGHTS TO DUPLICATE, TRANSFER OR SELL THIS DESIGN ARE EXPRESSLY RESERVED. THE BUYER IS LICENSED TO BUILD ONE ASSEMBLY FROM THESE PLANS.

REVISIONS				
ZONE	LTR	DESCRIPTION	DATE	APPROVED

Spira International, Inc.
Huntington Beach, California

FIESTA BAY
13' SPEED BOAT

DRAWN BY:
J. SPIRA

DATE:
12/19/10

DRAWING NO.
FIES01

SCALE 1" = 1'

SHEET
OF

4


3

2

1

NOTICE
THIS DRAWING CONTAINS A PROPRIETARY DESIGN ASSIGNED TO SPIRA INTERNATIONAL, INC. ALL RIGHTS TO DUPLICATE, TRANSFER OR SELL THIS DESIGN ARE EXPRESSLY RESERVED. THE BUYER IS LICENSED TO BUILD ONE ASSEMBLY FROM THESE PLANS.

REVISIONS				
ZONE	LTR	DESCRIPTION	DATE	APPROVED

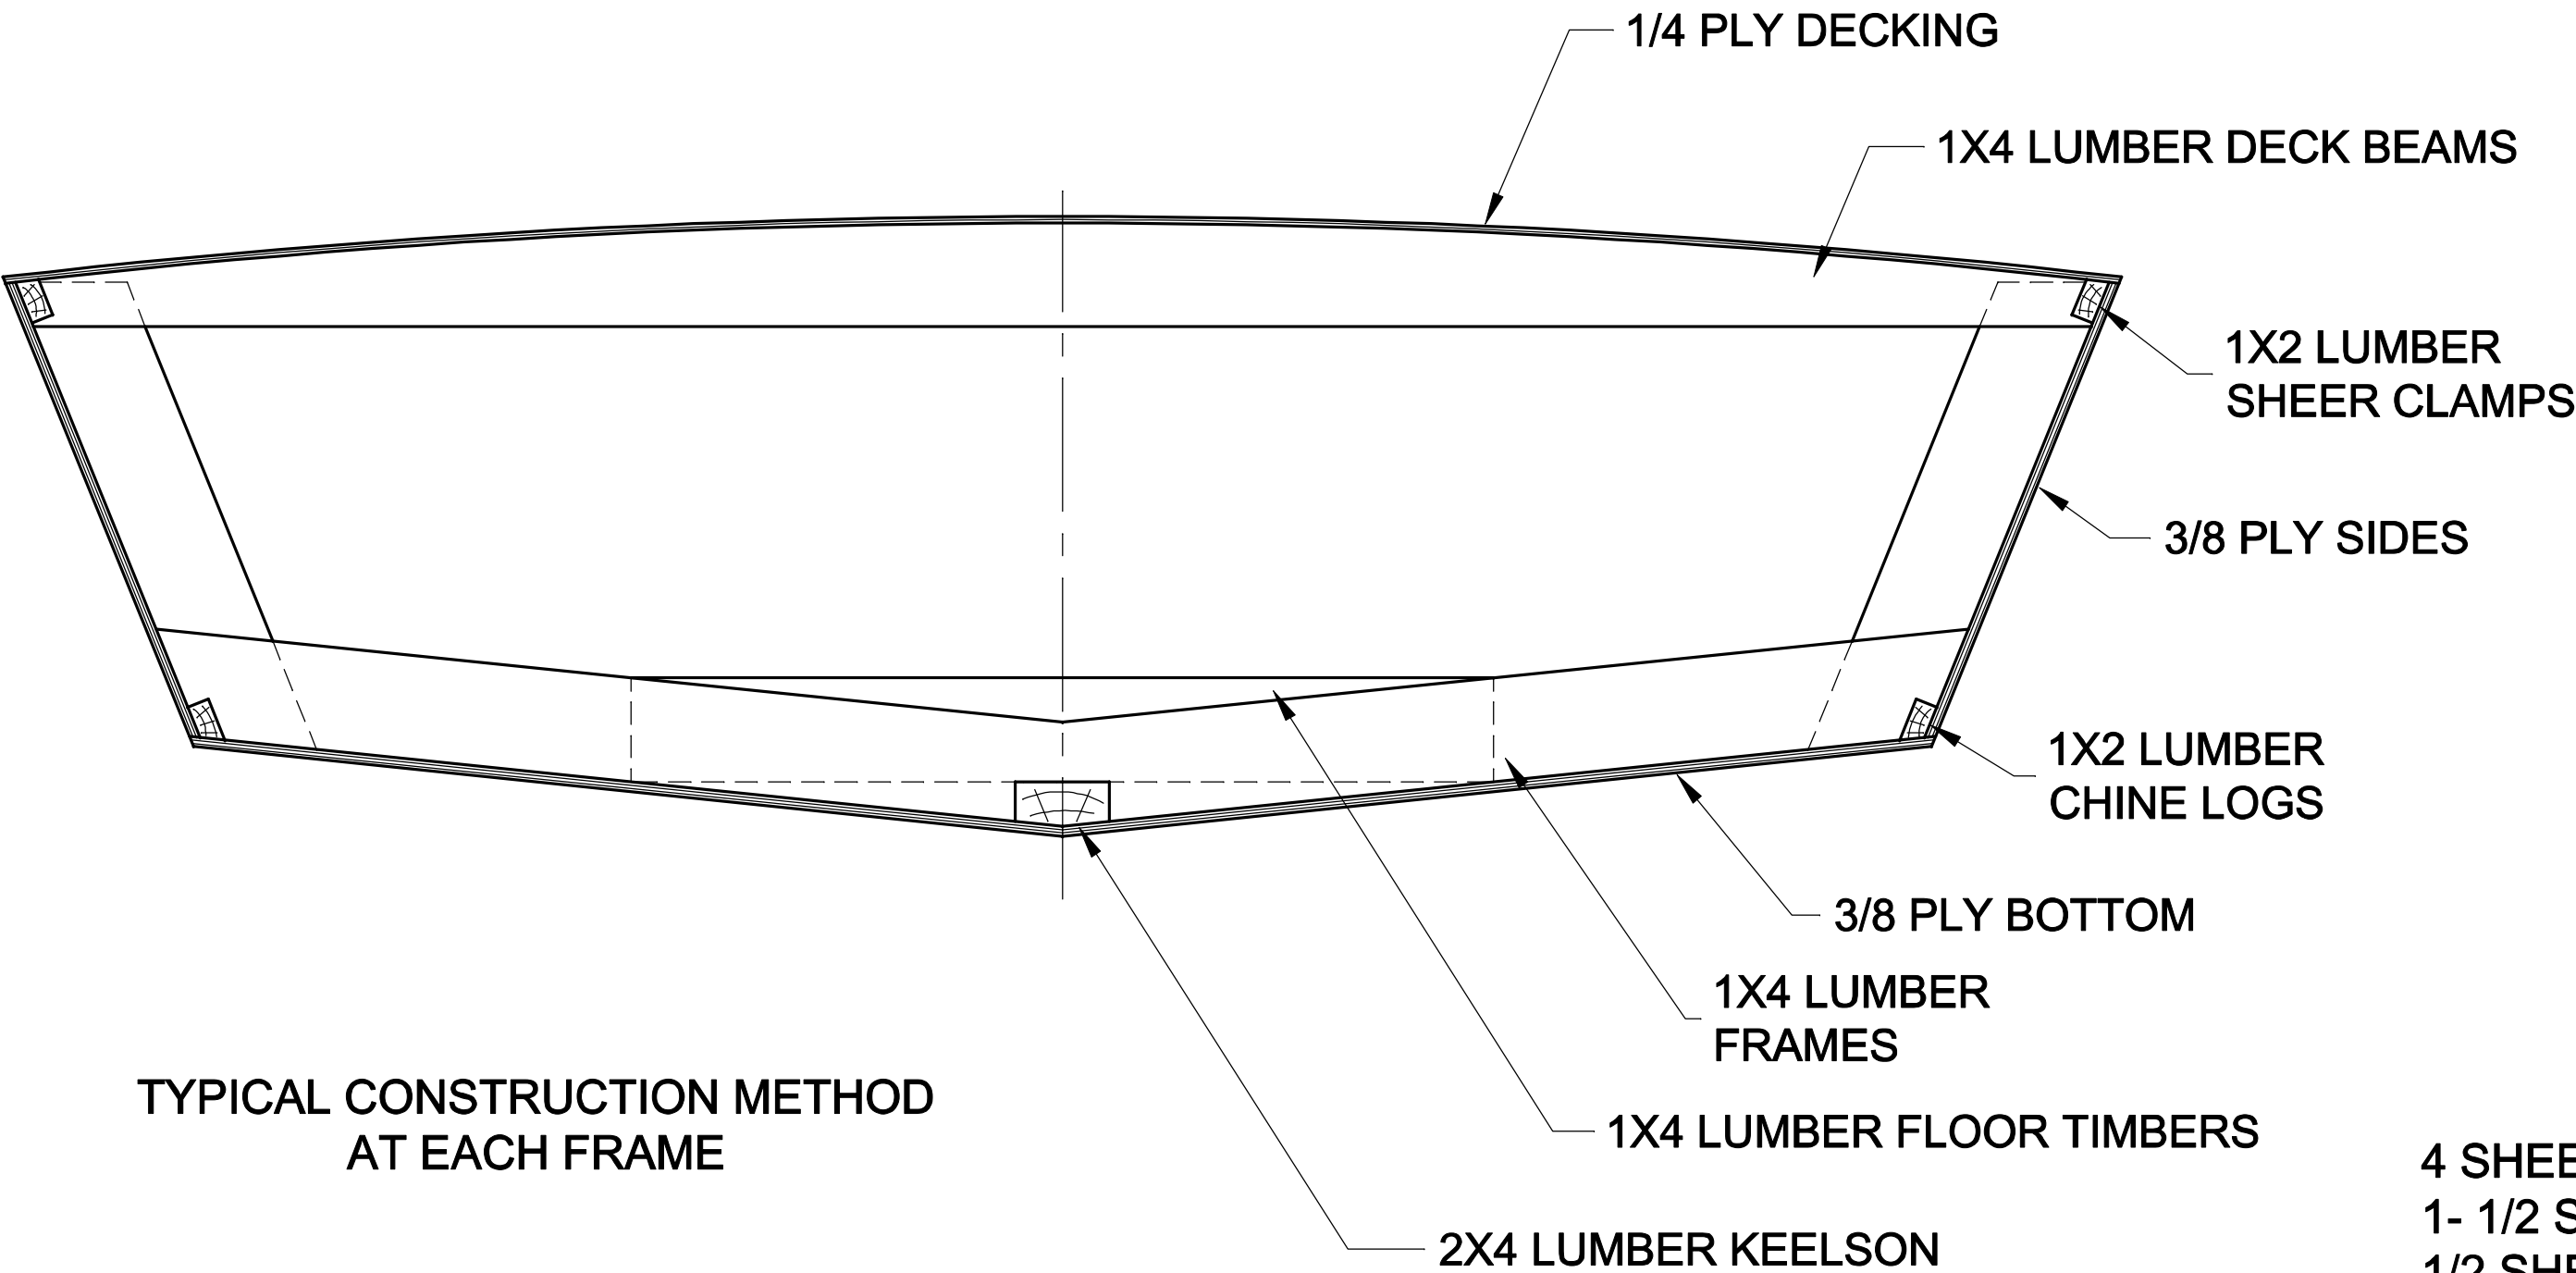

FASTENING SCHEDULE

KEELSON TO FRAMES: #8 X 3 DECK SCREWS
FRAMES TO FRAMES: DRYWALL SCREWS
LONGITUDINALS: #8 X 2 DECK SCREWS
PLY TO FRAMES: DRYWALL SCREWS

NOTES:

1. YOU MAY SCARF TOGETHER SHORTER PIECES TO CREATE THE LONGITUDINAL ELEMENTS.
2. NOMINAL LUMBER SIZED CALLED OUT, E.G. A 1 X 3 LUMBER IS ACTUAL SIZE 3/4" X 2-1/2"

BILL OF MATERIALS

4 SHEETS 3/8 PLY
1- 1/2 SHEET 1/4 PLY
1/2 SHEET 5/8 PLY
75 FT 1X4 CONSTRUCTION LUMBER
50 FT 1X2 CONSTRUCTION LUMBER
32 FT 2X4 CONSTRUCTION LUMBER
6 FT 2X8 CONSTRUCTION LUMBER
250 DRYWALL SCREWS
100 #8 X 2 DECK SCREWS
25 #8 X 3" DECK SCREWS
6 QT EPOXY
12 YDS 6 OZ FIBERGLASS CLOTH

Spira International, Inc.
Huntington Beach, California

FIESTA BAY
13' SPEED BOAT

DRAWN BY: J. SPIRA	DATE: 12/19/10	DRAWING NO. FIES02
SCALE 2" = 1'		SHEET OF