

4

3

2


1

NOTICE
THIS DRAWING CONTAINS A PROPRIETARY DESIGN ASSIGNED TO SPIRA INTERNATIONAL, INC. ALL RIGHTS TO DUPLICATE, TRANSFER OR USE ARE EXPRESSLY RESERVED BY SPIRA INTERNATIONAL. THE BUYER IS LICENSED TO BUILD ONE ASSEMBLY FROM THESE PLANS.

REVISIONS				
ZONE	LTR	DESCRIPTION	DATE	APPROVED

D

D

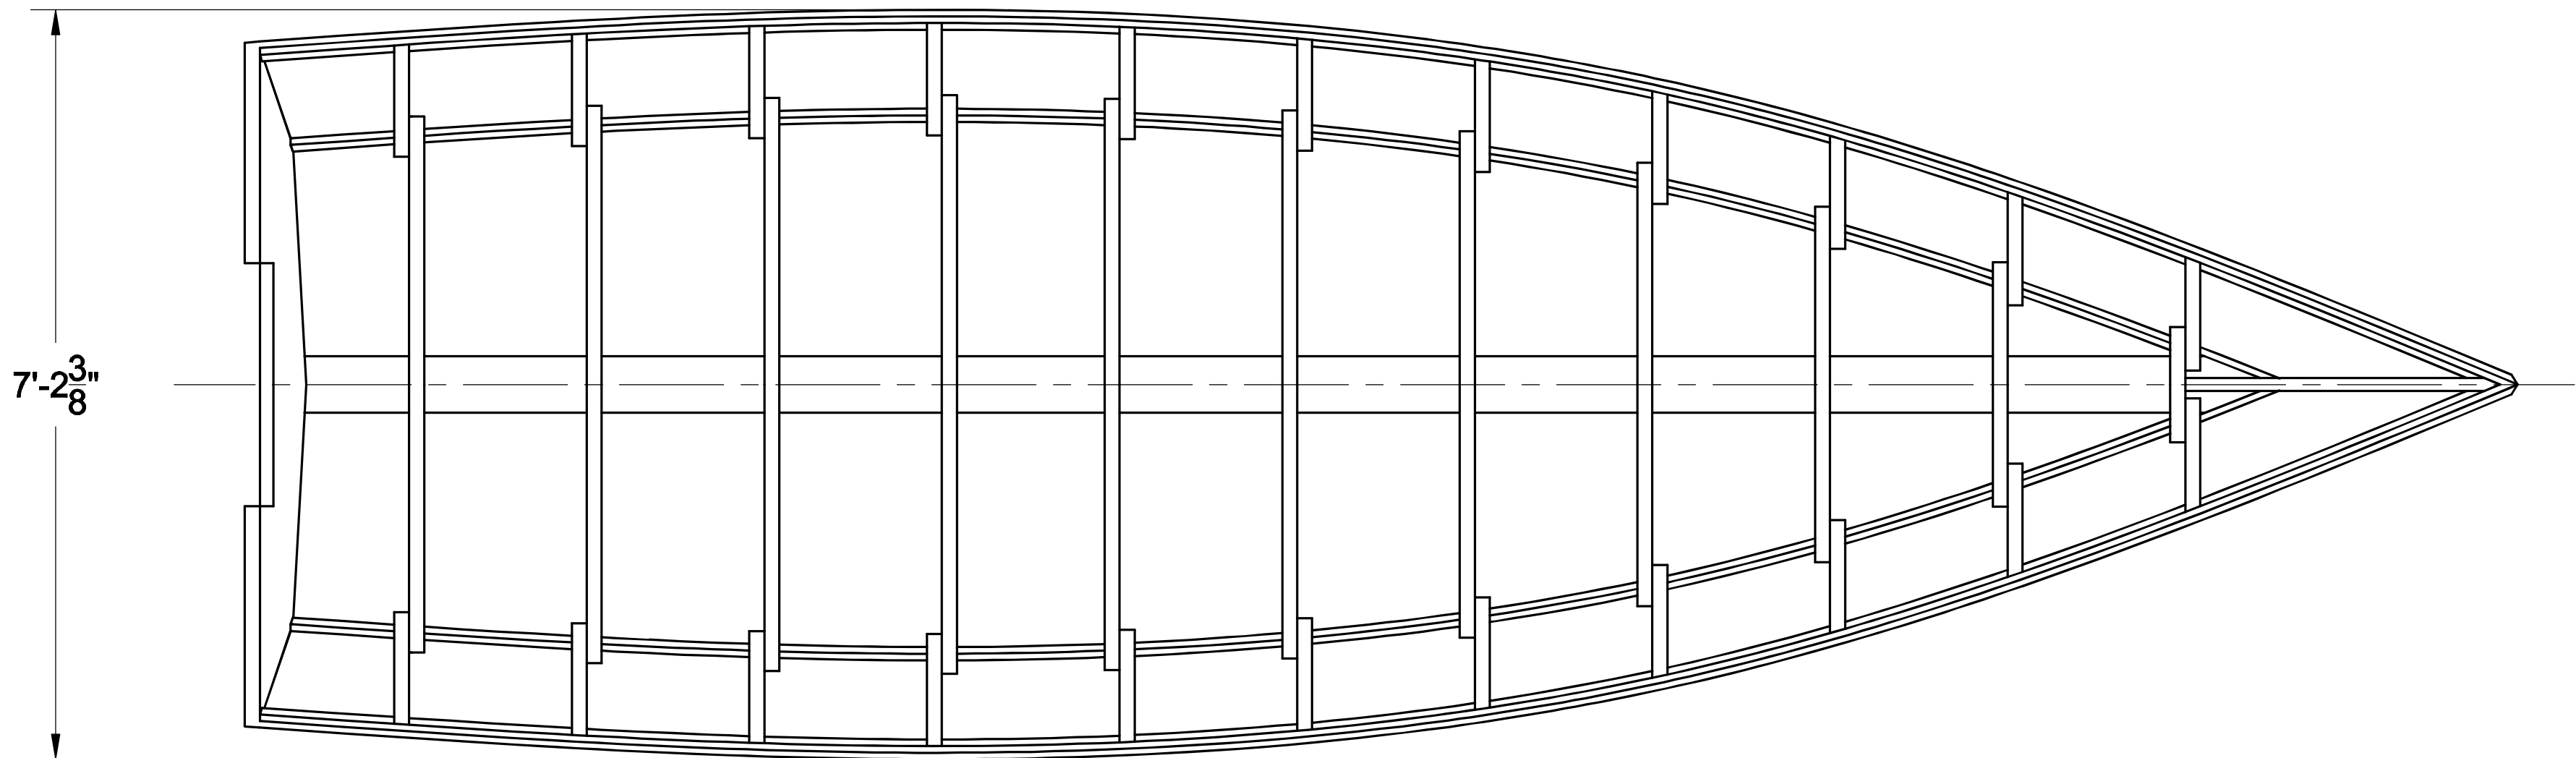


C

C

B

B

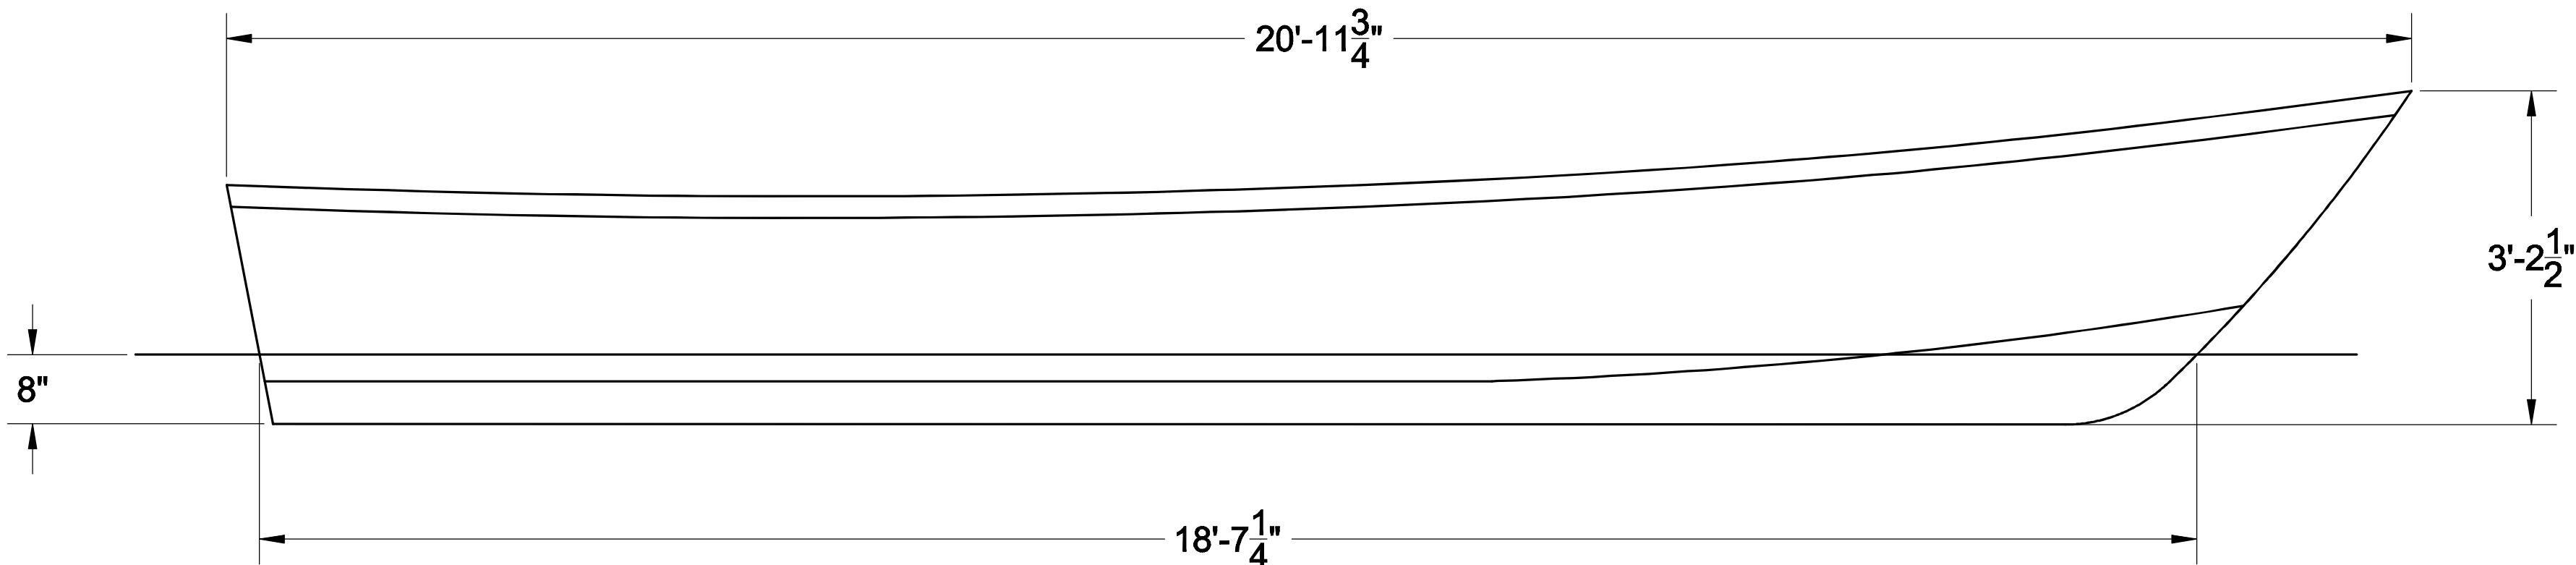

A

A

Spira International, Inc.
Huntington Beach, California

TIBURON
21' PANGA

DRAWN BY:
J. SPIRA

DATE:
01/06/13

DRAWING NO.
TIBU01

SCALE 3/4" = 1'

SHEET OF

4

3

2

1

4

3

2

1

NOTICE

THIS DRAWING CONTAINS A PROPRIETARY DESIGN ASSIGNED TO SPIRA INTERNATIONAL, INC. ALL RIGHTS TO DUPLICATE, TRANSFER OR USE ARE EXPRESSLY RESERVED BY SPIRA INTERNATIONAL. THE BUYER IS LICENSED TO BUILD ONE ASSEMBLY FROM THESE PLANS.

REVISIONS

ZONE	LTR	DESCRIPTION	DATE	APPROVED

D

D

DECKING - 5/8 PLY

DECK BEAMS
2 X 4 LUMBER

RAIL CAP AND RUB RAIL
3/4" STOCK

CHINE LOG
1 X 3 LUMBER

SIDES - 1/2 PLY

SIDE FRAMES - 2 X 4 LUMBER

CHINE LOG - 1 X 3 LUMBER

BOTTOM PLANKING - 5/8 PLY

BOTTOM FRAMES 2 X 4 LUMBER

KEELSON - 2 X 6 LUMBER

CONSTRUCTION METHOD
TYPICAL AT EACH FRAME

SCALE: 3" = 1'

BILL OF MATERIALS (HULL ONLY)

8 SHEETS 5/8" PLY
6 SHEETS 1/2" PLY
170' 2X4 LUMBER FOR FRAMES
140' 1X3 CLEAR LUMBER FOR SHEER
CLAMP, CHINE LOG AND RUB RAILS
20' 2X6 LUMBER FOR KEELSON
20' 2X8 LUMBER FOR TRANSOM & STEM
200 #10 X 2-1/2 SS DECK SCREWS
200 #8 X 2 SS DECK SCREWS
2000 #8 X 1-1/2 SS DECK SCREWS
5 GAL EPOXY RESIN
40 YDS 6 OZ FIBERGLASS CLOTH

FASTENING SCHEDULE


2x FRAME TO 2x FRAME: #10 X 2 -1/2 DECK SCREWS
LONGITUDINAL TO FRAME: #8 X 2 DECK SCREWS
PLANKING TO FRAME: #8 X 1-1/2 DECK SCREWS

NOTES:


1. YOU MAY SCARF TOGETHER SHORTER PIECES TO CREATE THE LONGITUDINAL ELEMENTS.
2. NOMINAL LUMBER SIZED CALLED OUT, E.G. A 2 X 4 LUMBER IS ACTUAL SIZE 1-1/2" X 3-1/2"

SEQUENCE FOR MAKING FRAMES


NO SCALE

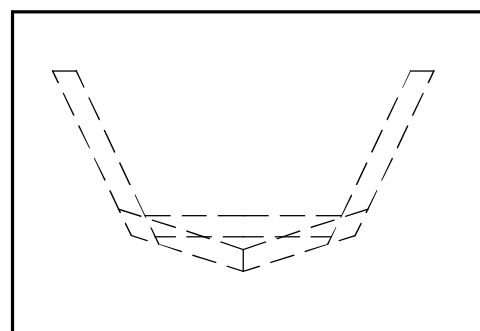


DRAW FRAME ON
SCRAP PLYWOOD

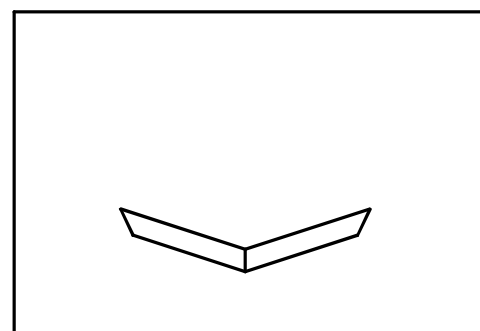


CUT OUT LOWER FRAME
ELEMENTS AND LOCATE
IN POSITION - EPOXY
CENTER JOINT

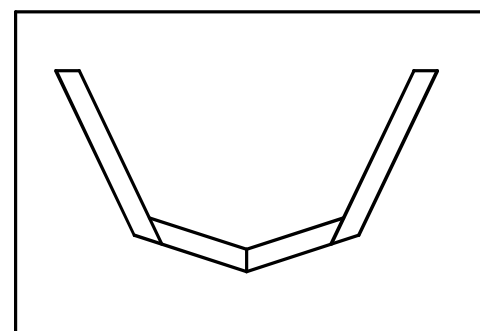

REPEAT FOR SIDE
FRAMES - EPOXY &
SCREW IN POSITION
ATOP BOTTOM FRAMES

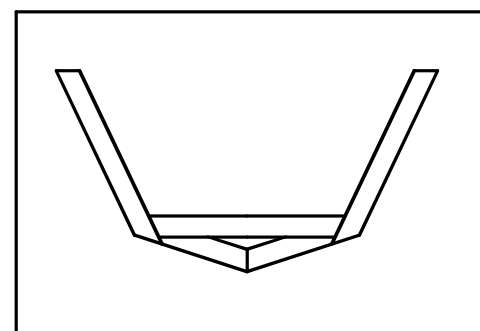

CUT OUT DECK
BEAM, LOCATE IN
POSITION, EPOXY &
SCREW IN PLACE

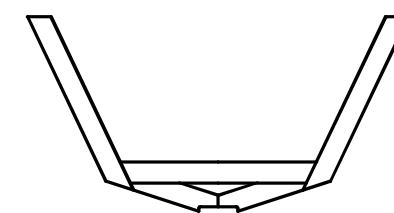

CUT OUT KEELSON
NOTCH AFTER EPOXY
HAS SET FULLY

Spira International, Inc.
Huntington Beach, California

TIBURON
21' PANGA

DRAWN BY:
J. SPIRA

DATE:
01/06/13

DRAWING NO.
TIBU02

SCALE 3/4" = 1'

SHEET OF

B

B

A

A

4

3

2

1